Демо-версия проекта

Заказать полную версию

Проект индивидуального жилого дома
по каркасной технологии

Проект "Палома"

Архитектурные решения (АР)

dokadom.com

Ведомостьчертежей раздела АР

Лист	**Наименование**	**Примечание**
	Титульный лист АР.	
1	Ведомость чертежей.	
2	Технико-экономические показатели.	
3	Общий вид 1,2.	
4	Общий вид 3,4.	
5	План на отметке 0,000. М 1:50.	
6	Экспликация помещений.	
7	Фасад 1-5.	
8	Фасад 5-1.	
9	Фасад А-Д.	
10	Фасад Д-А.	
11	Разрез 1-1.	
12	Разрез 2-2.	
13	Спецификация оконных проемов. Спецификация дверных проемов.	
14	План кровли. М 1:50.	
15	Общие данные к плану кровли. Спецификация элементов водостока.	

Взам. инв.. №

Подп. и дата

Инв.. № подл.

ООО "Каркасники"	*Каркасный дом "Палома"*	*Ведомость чертежей.*	АР	Лист 1

Копировал

Технико-экономические показатели

№ п./п.	Наименование	Единица измерения	Кол-во
1.	Площадь застройки	м.2	67,00
2.	Общая площадь	м.2	61,49
3.	Жилая площадь	м.2	0,00
4.	Строительный объем	м.3	195,23

Взам. инв.. №

Подп. и дата

Инв.. № подл.

ООО "Каркасники"	Каркасный дом "Палома"	Технико-экономические показатели.	АР	Лист 2

Общий вид 1.

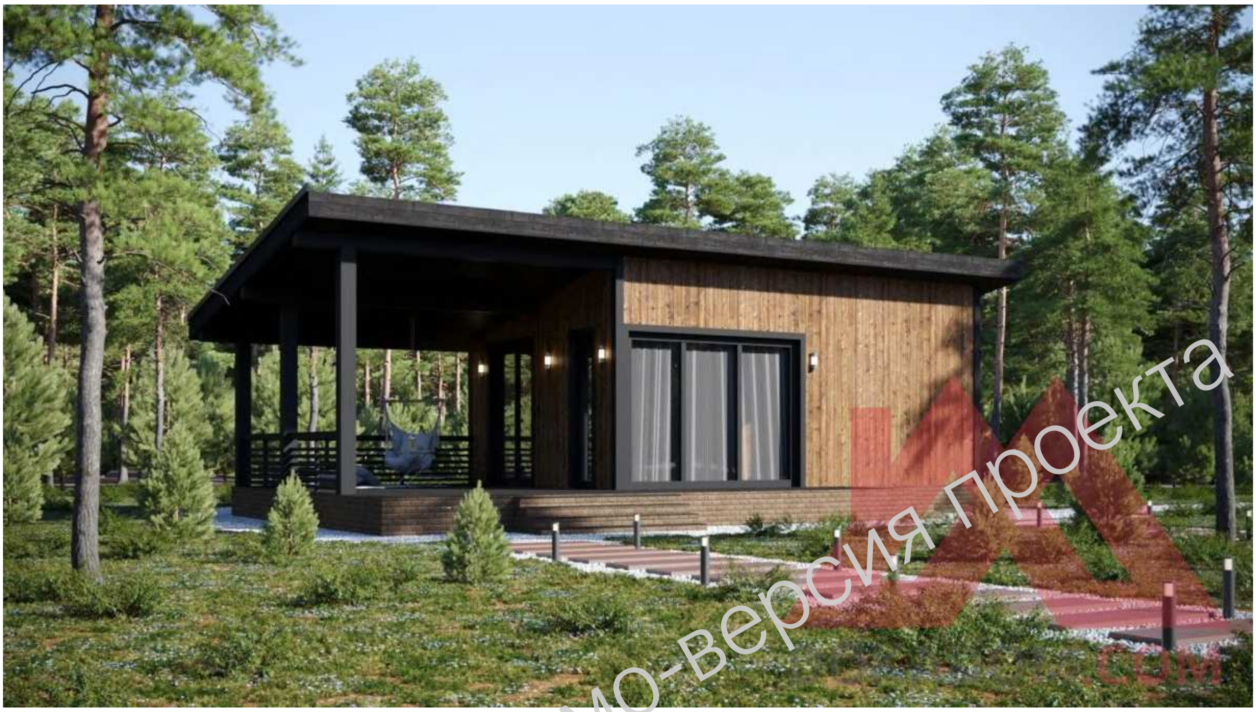

Общий вид 2.

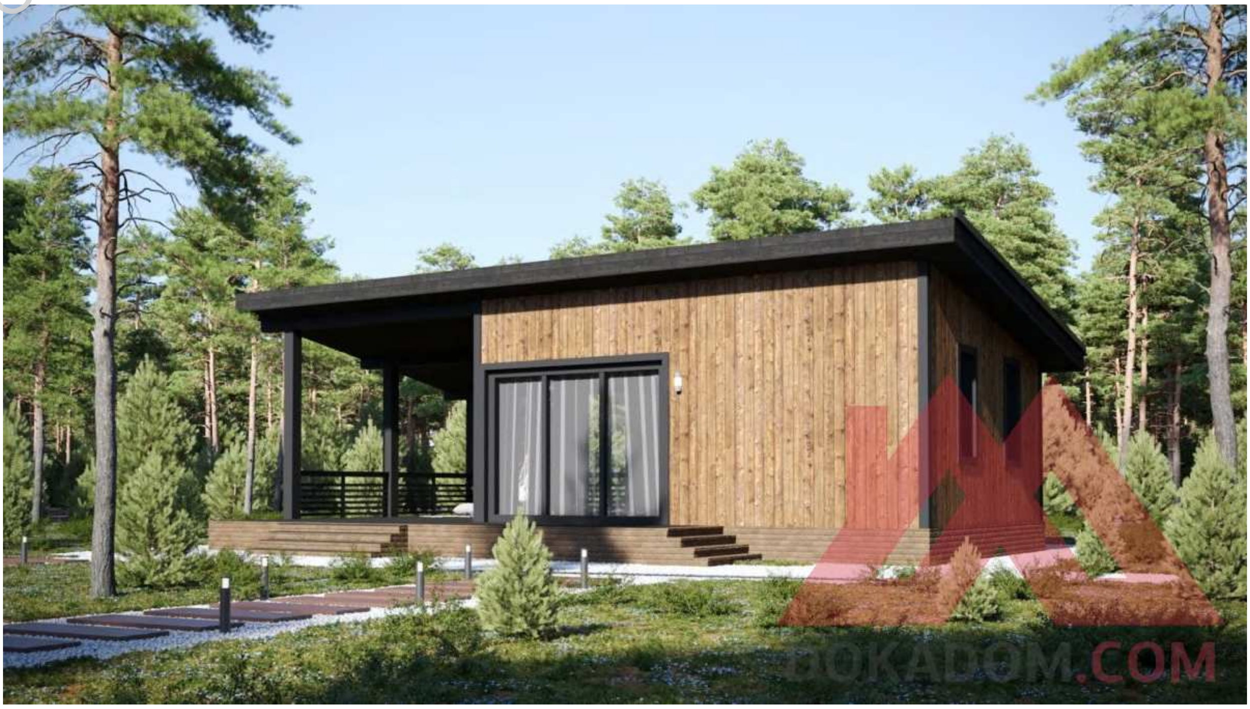

Взам. инв.. №	
Подп. и дата	
Инв.. № подл.	

ООО "Каркасники"	Каркасный дом "Палома"	Общий вид 1,2.	АР	Лист 3

Общий вид 3.

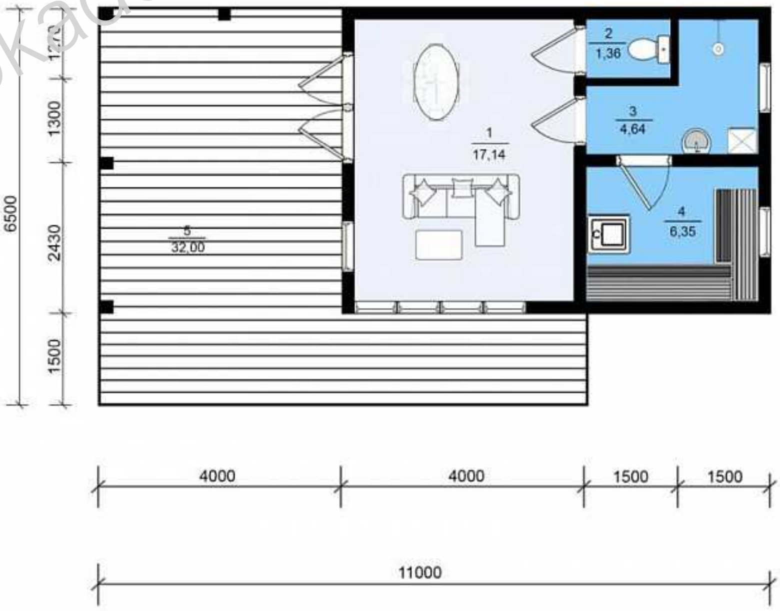

Экспликация помещений на отм. 0,000.			
№ п.п	Наименование	Площадь м2	Примечание
1	Комната отдыха	17,14	
2	С/у	1,36	
3	Душевая	4,64	
4	Парная	6,35	
5	Терраса	32,00	
		61,49 м²	

Взам. инв.. №

Подп. и дата

Инв.. № подл.

ООО "Каркасники"	Каркасный дом "Палома"	Общий вид 3,4.	АР	Лист 4

Копировал

ПЛАН НА ОТМЕТКЕ 0,000. М 1:50.

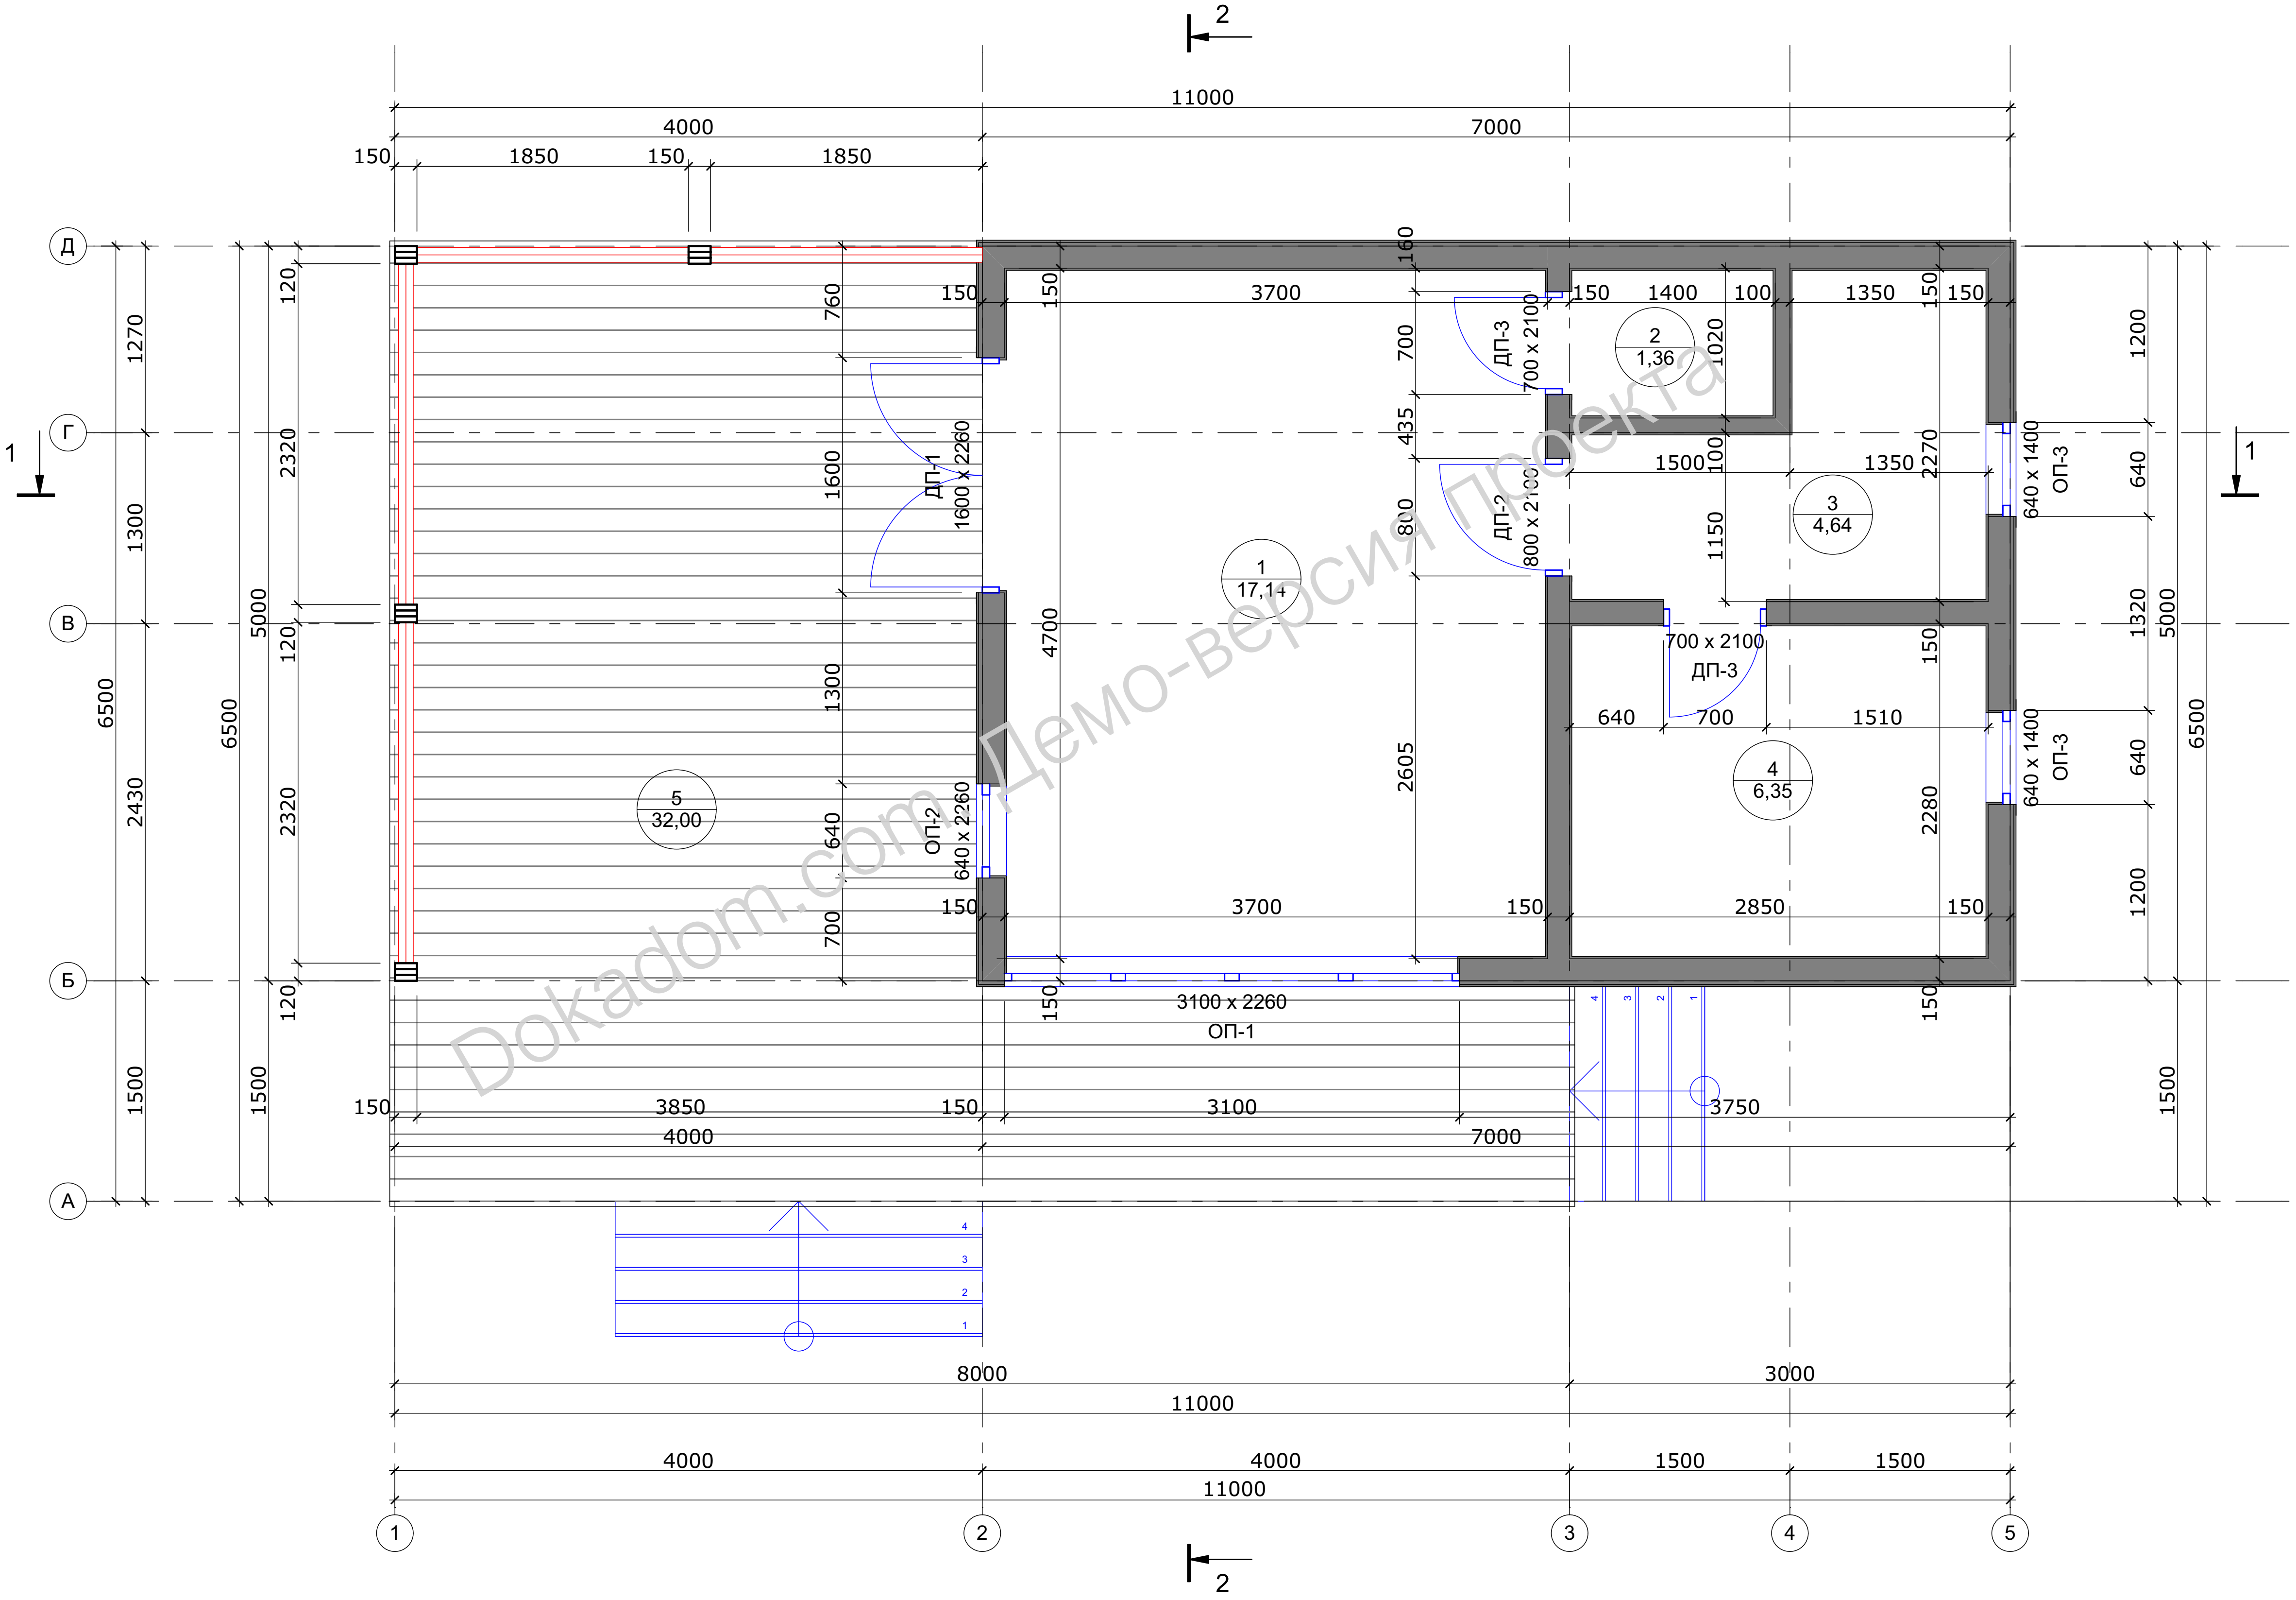

Согласовано

Взам. инв. №

Подп. и дата

Инв. № подп.

Изм..	Кол.уч.	Лист	№док.	Подп.	Дата
Разработал		Саяпин П.			
Утвердил		Маркович П.В.			

АР

ООО "Каркасники"

Проект "Палома"

Стадия	Лист	Листов
РП	5	15

План на отметке 0,000. М 1:50.

dokadom.com

Копировал

Экспликация помещений на отм. 0,000.

№ п.п	Наименование	Площадь м2	Примечание
1	Комната отдыха	17,14	
2	С/у	1,36	
3	Душевая	4,64	
4	Парная	6,35	
5	Терраса	32,00	
		61,49 $м^2$	

Согласовано

Взам. инв. №

Подп. и дата

Инв.. № подп.

Изм..	Кол.уч.	Лист	№док.	Подп.	Дата
Разработал		*Саяпин П.*			
Утвердил		*Маркович П.В.*			

АР

ООО "Каркасники"

Проект "Палома"

Стадия	Лист	Листов
РП	6	15

Экспликация помещений.

dokadom.com

Копировал

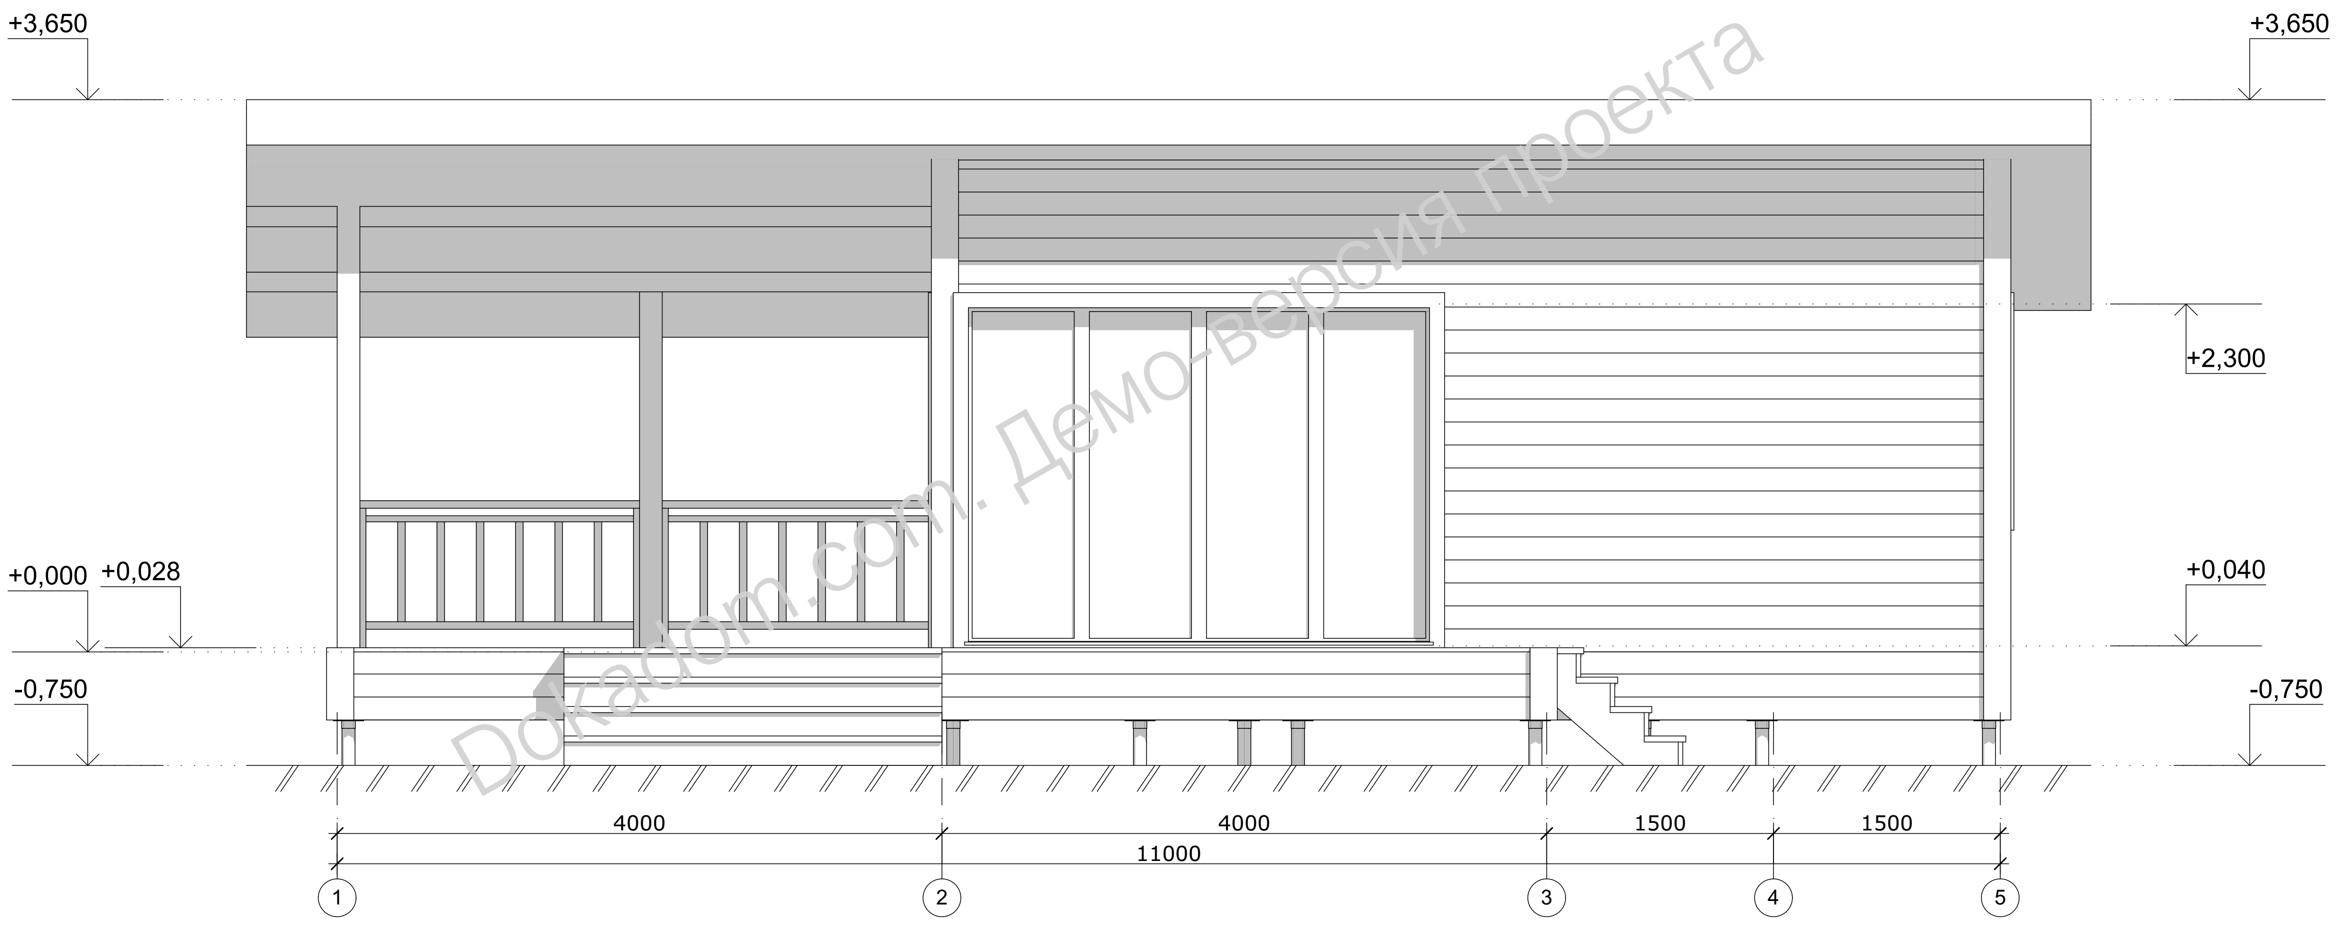

Согласовано

Взам. инв. №

Подп. и дата

Инв.. № подп.

Изм..	Кол.уч.	Лист	№док.	Подп.	Дата	
Разработал		Саяпин П.				
Утвердил		Маркович П.В.				

АР

ООО "Каркасники"

Проект "Палома"

Стадия	Лист	Листов
РП	7	15

Фасад 1-5.

dokadom.com

Копировал

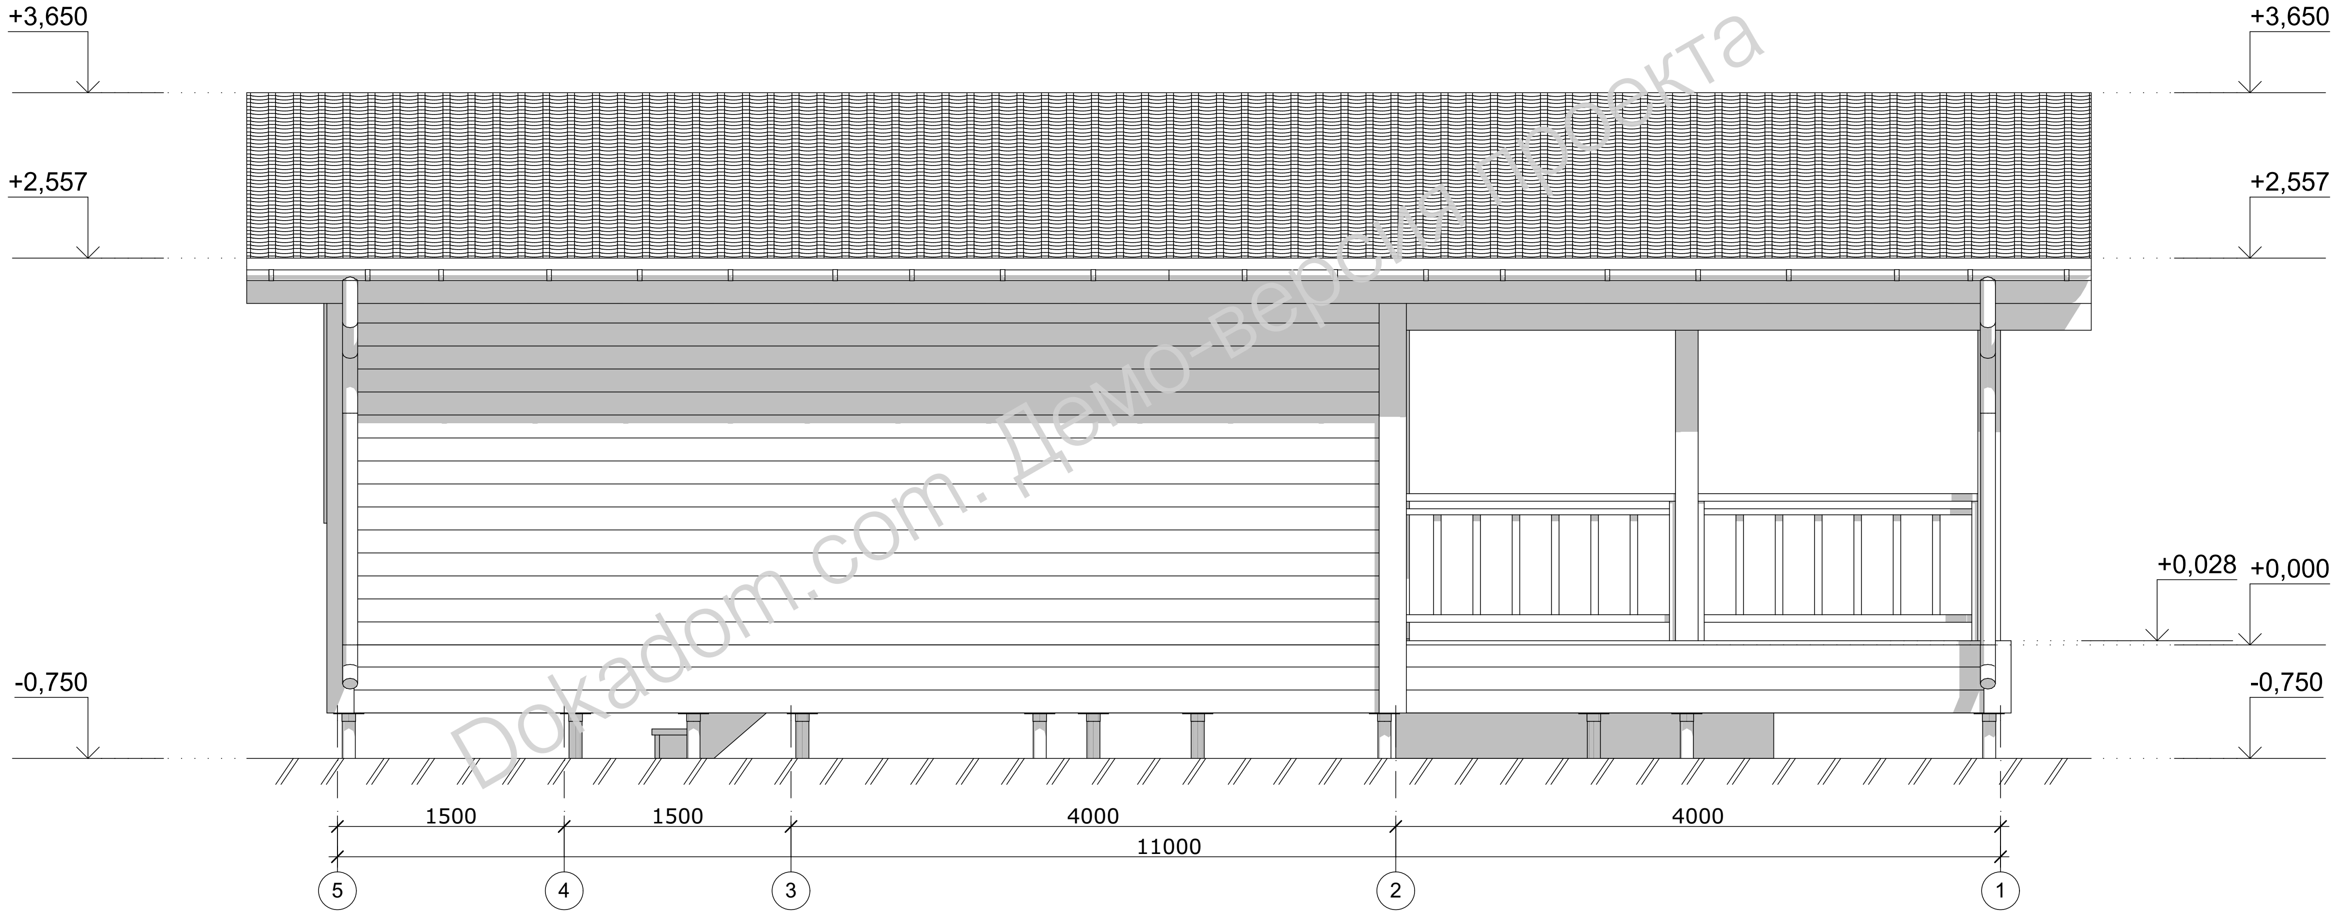

Согласовано

Взам. инв. №

Подп. и дата

Инв. № подл.

Изм..	Кол.уч.	Лист	№док.	Подп.	Дата
Разработал		Саяпин П.			
Утвердил		Маркович П.В.			

АР

ООО "Каркасники"

Проект "Палома"

Стадия	Лист	Листов
РП	8	15

Фасад 5-1.

dokadom.com

Копировал

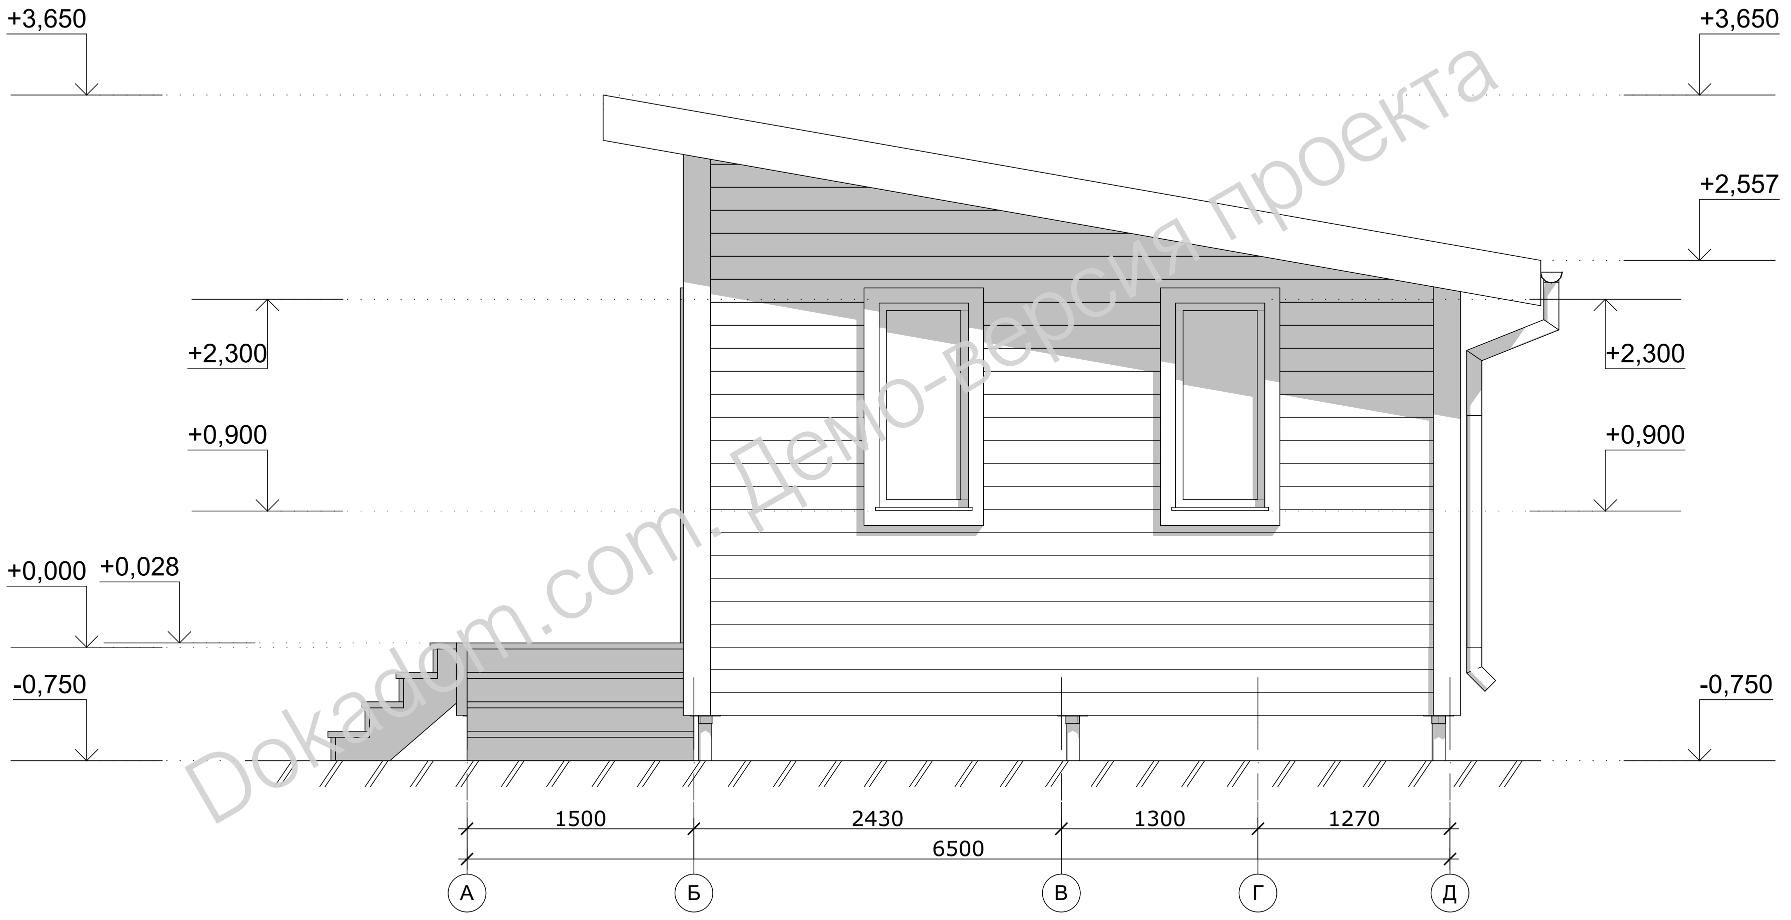

Согласовано

Взам. инв. №

Подп. и дата

Инв.. № подп.

Изм..	Кол.уч.	Лист	№док.	Подп.	Дата
Разработал		Саяпин П.			
Утвердил		Маркович П.В.			

АР

ООО "Каркасники"

Проект "Палома"

Стадия	Лист	Листов
РП	9	15

Фасад А-Д.

dokadom.com

Копировал

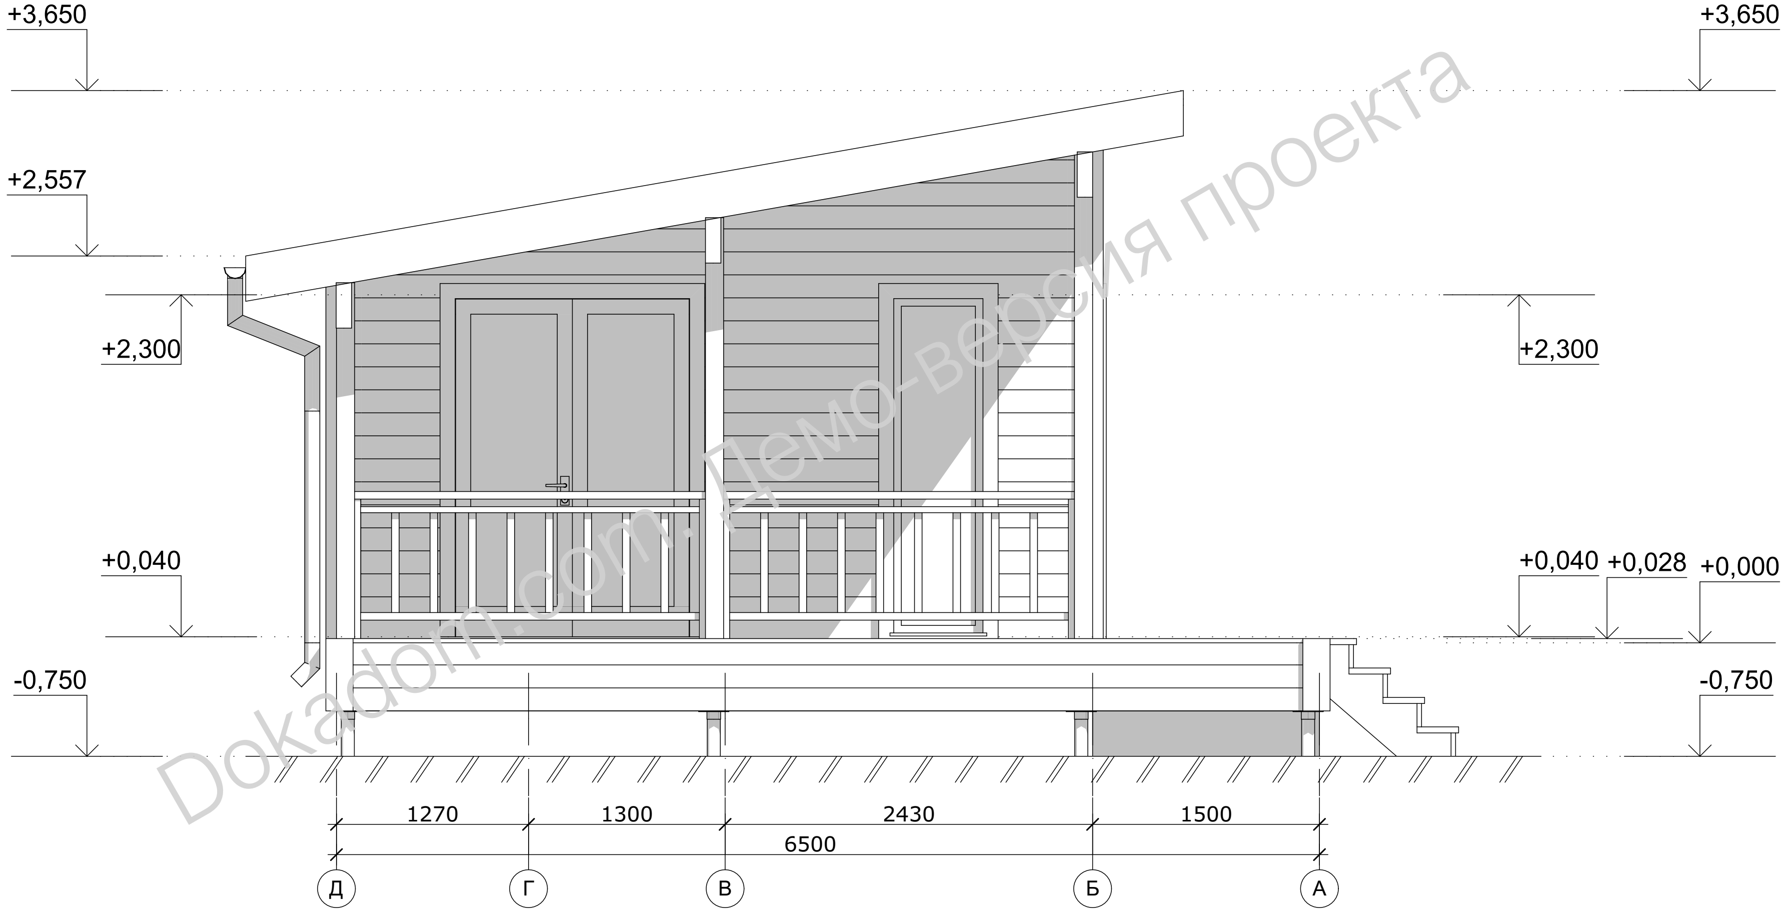

Согласовано

Взам. инв. №

Подп. и дата

Инв.. № подп.

Изм..	Кол.уч.	Лист	№док.	Подп.	Дата	
Разработал		Саяпин П.				
Утвердил		Маркович П.В.				

АР

ООО "Каркасники"

Проект "Палома"

Стадия	Лист	Листов
РП	10	15

Фасад Д-А.

dokadom.com

Копировал

1. Металлочерепица, цвет:
2. Обрешетка сеч. 25х100 - 25
3. Контрбрус 40х40 - 40
4. Ветро-влагозащитная мембрана, морозостойкая
5. Стропила сеч. 50х200, с утеплителем су=35кг/м3 толщиной 200мм -200
6. Пароизоляционная пленка
7. Имитация бруса, толщ. 16мм. -16

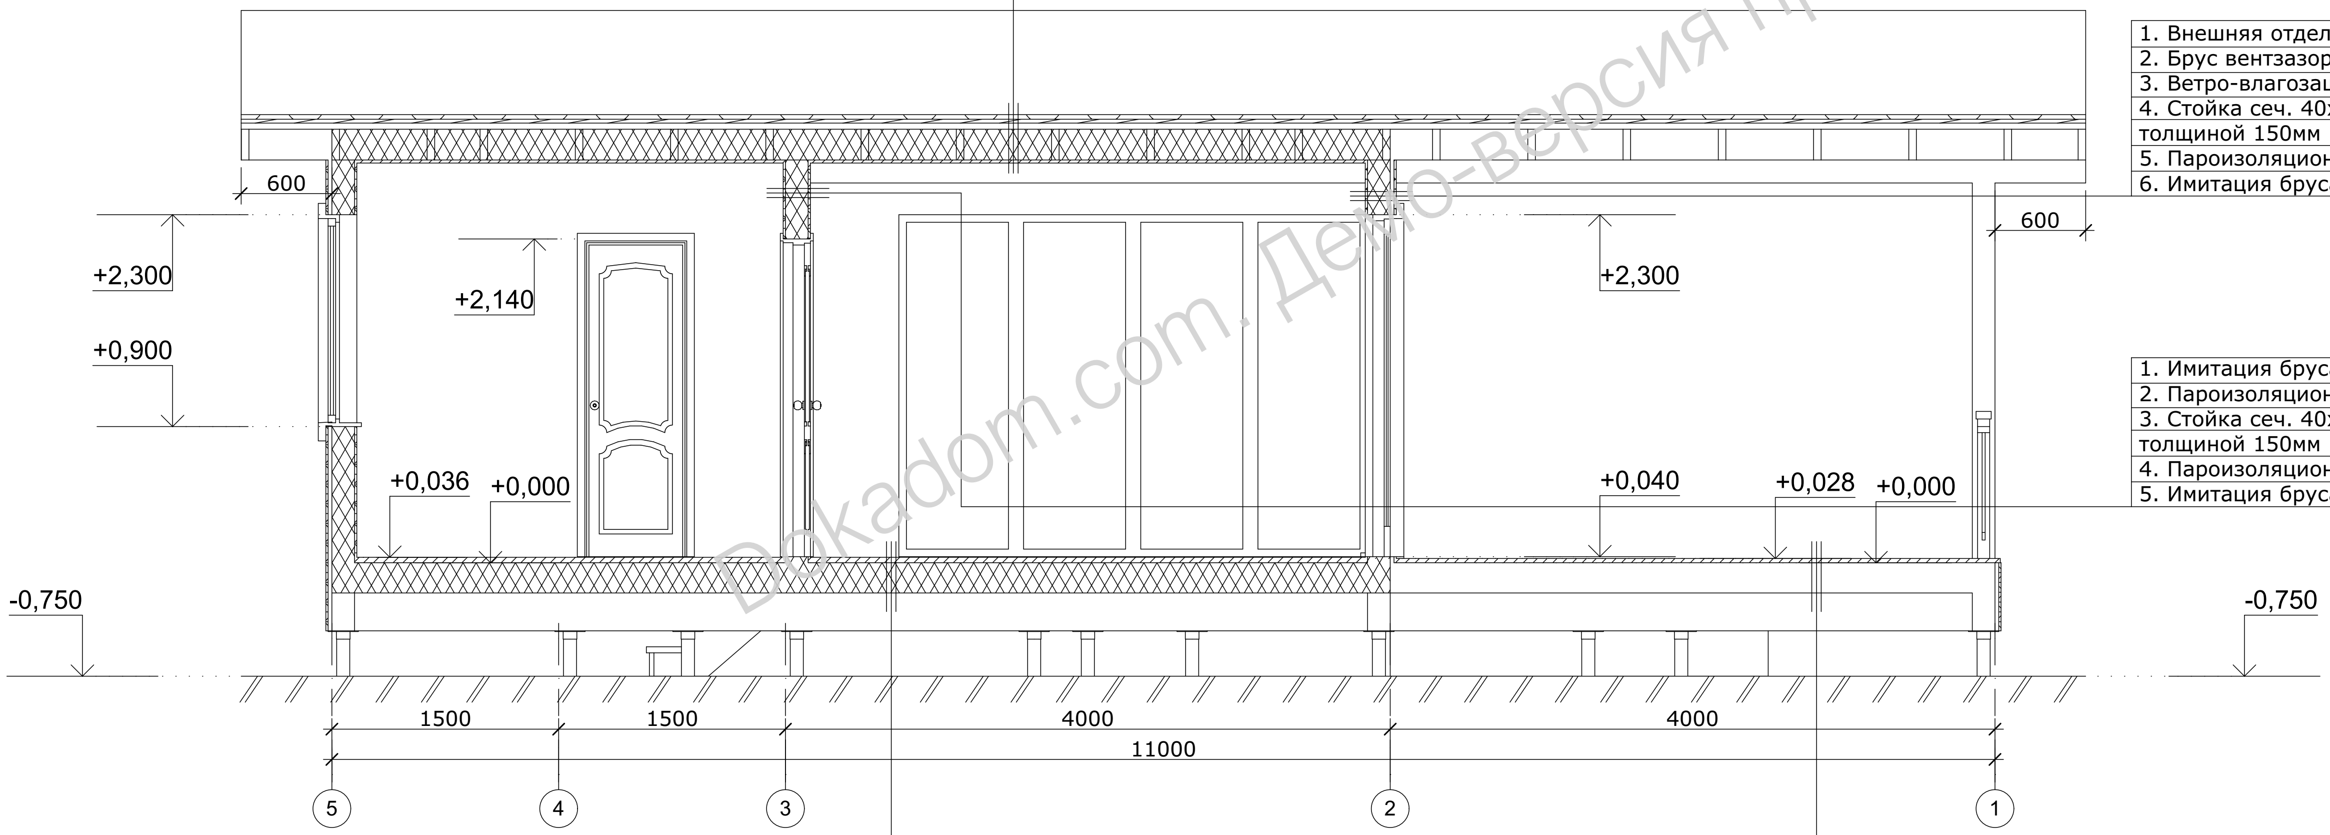

1. Внешняя отделка - Имитация бруса, толщ. 16мм. -16
2. Брус вентзазора h=25мм. -25
3. Ветро-влагозащитная мембрана
4. Стойка сеч. 40х150, с утеплителем су=35кг/м3 толщиной 150мм -150
5. Пароизоляционная пленка
6. Имитация бруса, толщ. 16мм. -16

1. Имитация бруса, толщ. 16мм. -16
2. Пароизоляционная пленка
3. Стойка сеч. 40х150, с утеплителем су=35кг/м3 толщиной 150мм -150
4. Пароизоляционная пленка
5. Имитация бруса, толщ. 16мм. -16

1. Доска шпунтованная, толщ. 36мм. -36
2. Гидроизоляционная пленка
3. Балки пола сеч. 50х200, с утеплителем су=35кг/м3, толщиной 200мм. -200
4. Ветро-влагозащитная мембрана
5. Сетка оцинкованная, ячейка 2х2мм.

1. Доска террасная, толщ. 28мм. -28
2. Балки пола сеч. 50х200, -200

Согласовано

Взам. инв. №

Подп. и дата

Инв.. № подл.

Изм..	Кол.уч.	Лист	№док.	Подп.	Дата
Разработал		Саяпин П.			
Утвердил		Маркович П.В.			

АР

ООО "Каркасники"

Проект "Палома"

Стадия	Лист	Листов
РП	11	15

Разрез 1-1.

dokadom.com

Копировал

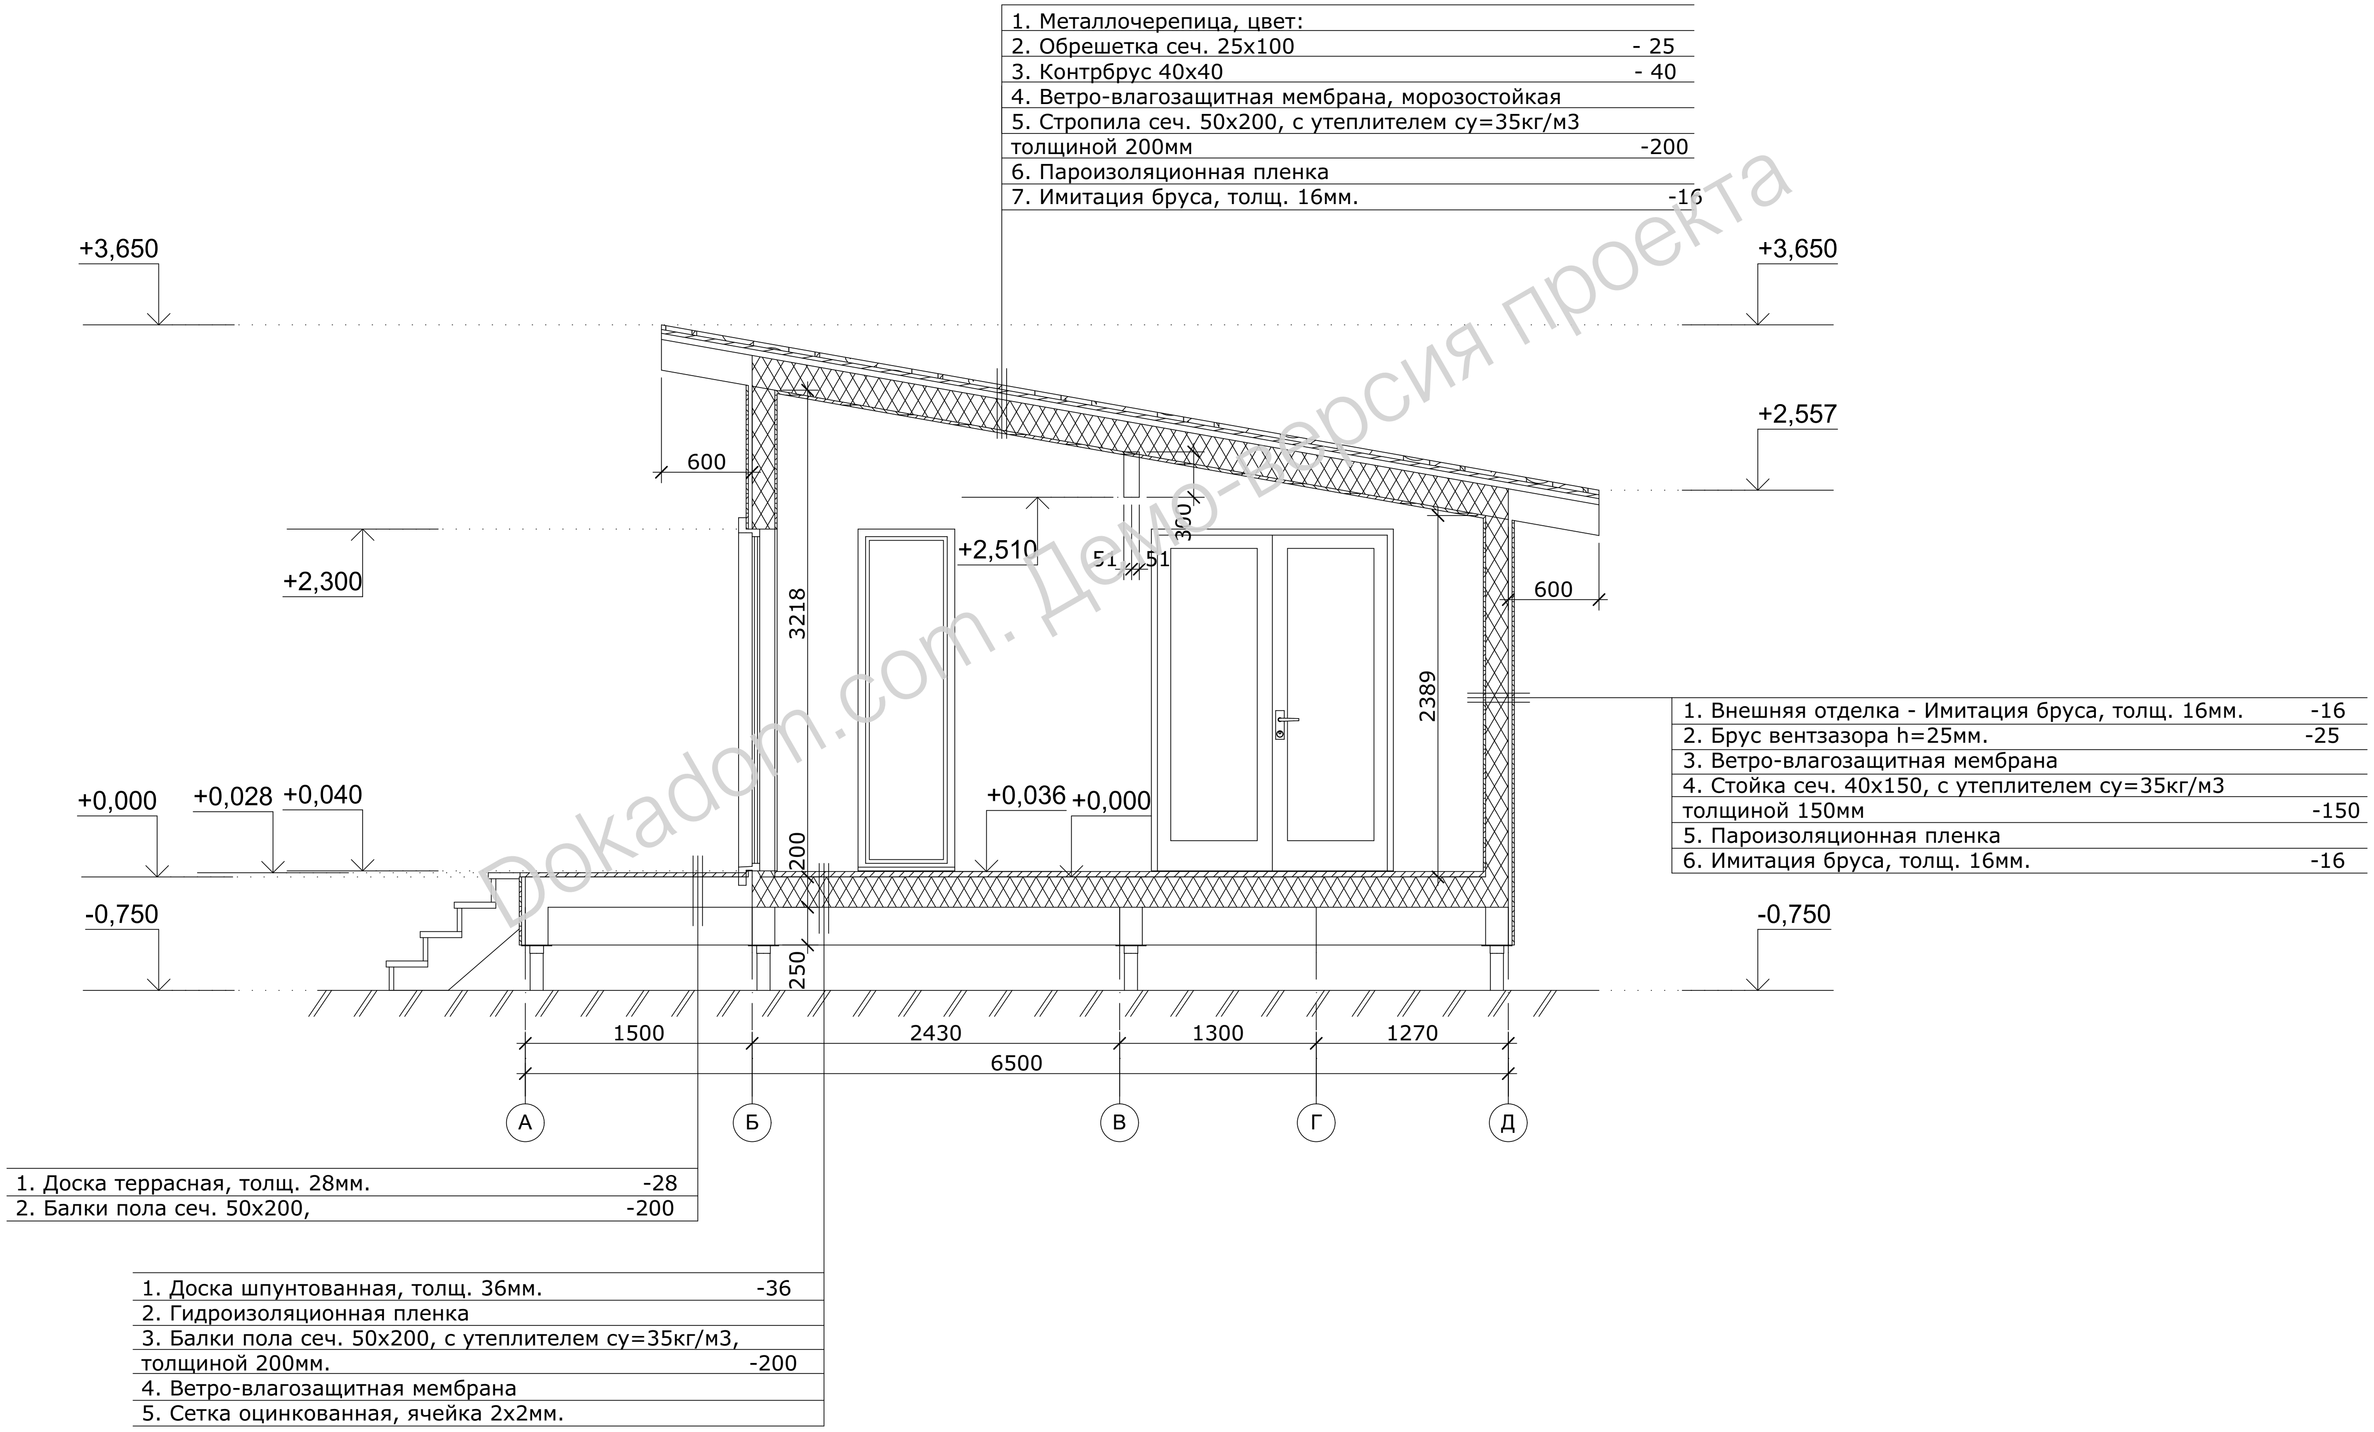

1. Металлочерепица, цвет:	
2. Обрешетка сеч. 25х100	- 25
3. Контрбрус 40х40	- 40
4. Ветро-влагозащитная мембрана, морозостойкая	
5. Стропила сеч. 50х200, с утеплителем су=35кг/м3 толщиной 200мм	-200
6. Пароизоляционная пленка	
7. Имитация бруса, толщ. 16мм.	-16

1. Внешняя отделка - Имитация бруса, толщ. 16мм.	-16
2. Брус вентзазора h=25мм.	-25
3. Ветро-влагозащитная мембрана	
4. Стойка сеч. 40х150, с утеплителем су=35кг/м3 толщиной 150мм	-150
5. Пароизоляционная пленка	
6. Имитация бруса, толщ. 16мм.	-16

1. Доска террасная, толщ. 28мм.	-28
2. Балки пола сеч. 50х200,	-200

1. Доска шпунтованная, толщ. 36мм.	-36
2. Гидроизоляционная пленка	
3. Балки пола сеч. 50х200, с утеплителем су=35кг/м3, толщиной 200мм.	-200
4. Ветро-влагозащитная мембрана	
5. Сетка оцинкованная, ячейка 2х2мм.	

Согласовано

Взам. инв. №

Подп. и дата

Инв. № подл.

Изм..	Кол.уч.	Лист	№док.	Подп.	Дата
Разработал		Саяпин П.			
Утвердил		Маркович П.В.			

АР

ООО "Каркасники"

Проект "Палома"	Стадия	Лист	Листов
	РП	12	15

Разрез 2-2.

dokadom.com

Копировал

Спецификация оконных проемов.

Позиция	Фронтальный вид	Размер Ш х В	Площадь проема	Кол-во	Примечание
ОП-1	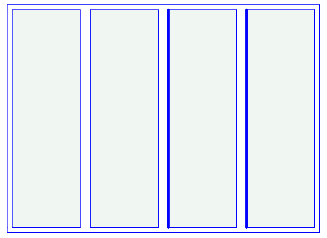	3100x2260	7,01	1	
ОП-2	 	640x2260	1,45	1	
ОП-3	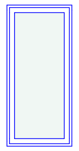	640x1400	0,90	2	
			10,26 м²		

Спецификация дверных проемов

Позиция	Символ	Размер Ш х В	Ориентация	Количество	Площадь Проема	Примечание
ДП-1	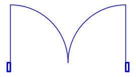	1600x2260	Л	1	3,62	террасная
ДП-2	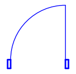	800x2100	Л	1	1,68	
ДП-3	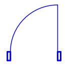	700x2100	Л	2	1,47	
					8,24 м²	

Примечание:
1. Перед изготовлением изделий для оконных и дверных проемов фирме-изготовителю дополнительно выполнить обмеры проемов.
2. Дизайн оконных изделий показан условно. Рисунок, форма и длина ограждений может быть изменена согласно технологии производства, технических особенностей конструкции и креплений.

Согласовано

Взам. инв. №

Подп. и дата

Инв.. № подп.

Изм..	Кол.уч.	Лист	№док.	Подп.	Дата	
						АР
						ООО "Каркасники"
Разработал	*Саяпин П.*					*Проект "Палома"*
Утвердил	*Маркович П.В.*					

Стадия	Лист	Листов
РП	13	15

Спецификация оконных проемов.
Спецификация дверных проемов.

dokadom.com

Копировал

ПЛАН КРОВЛИ. М 1:50.

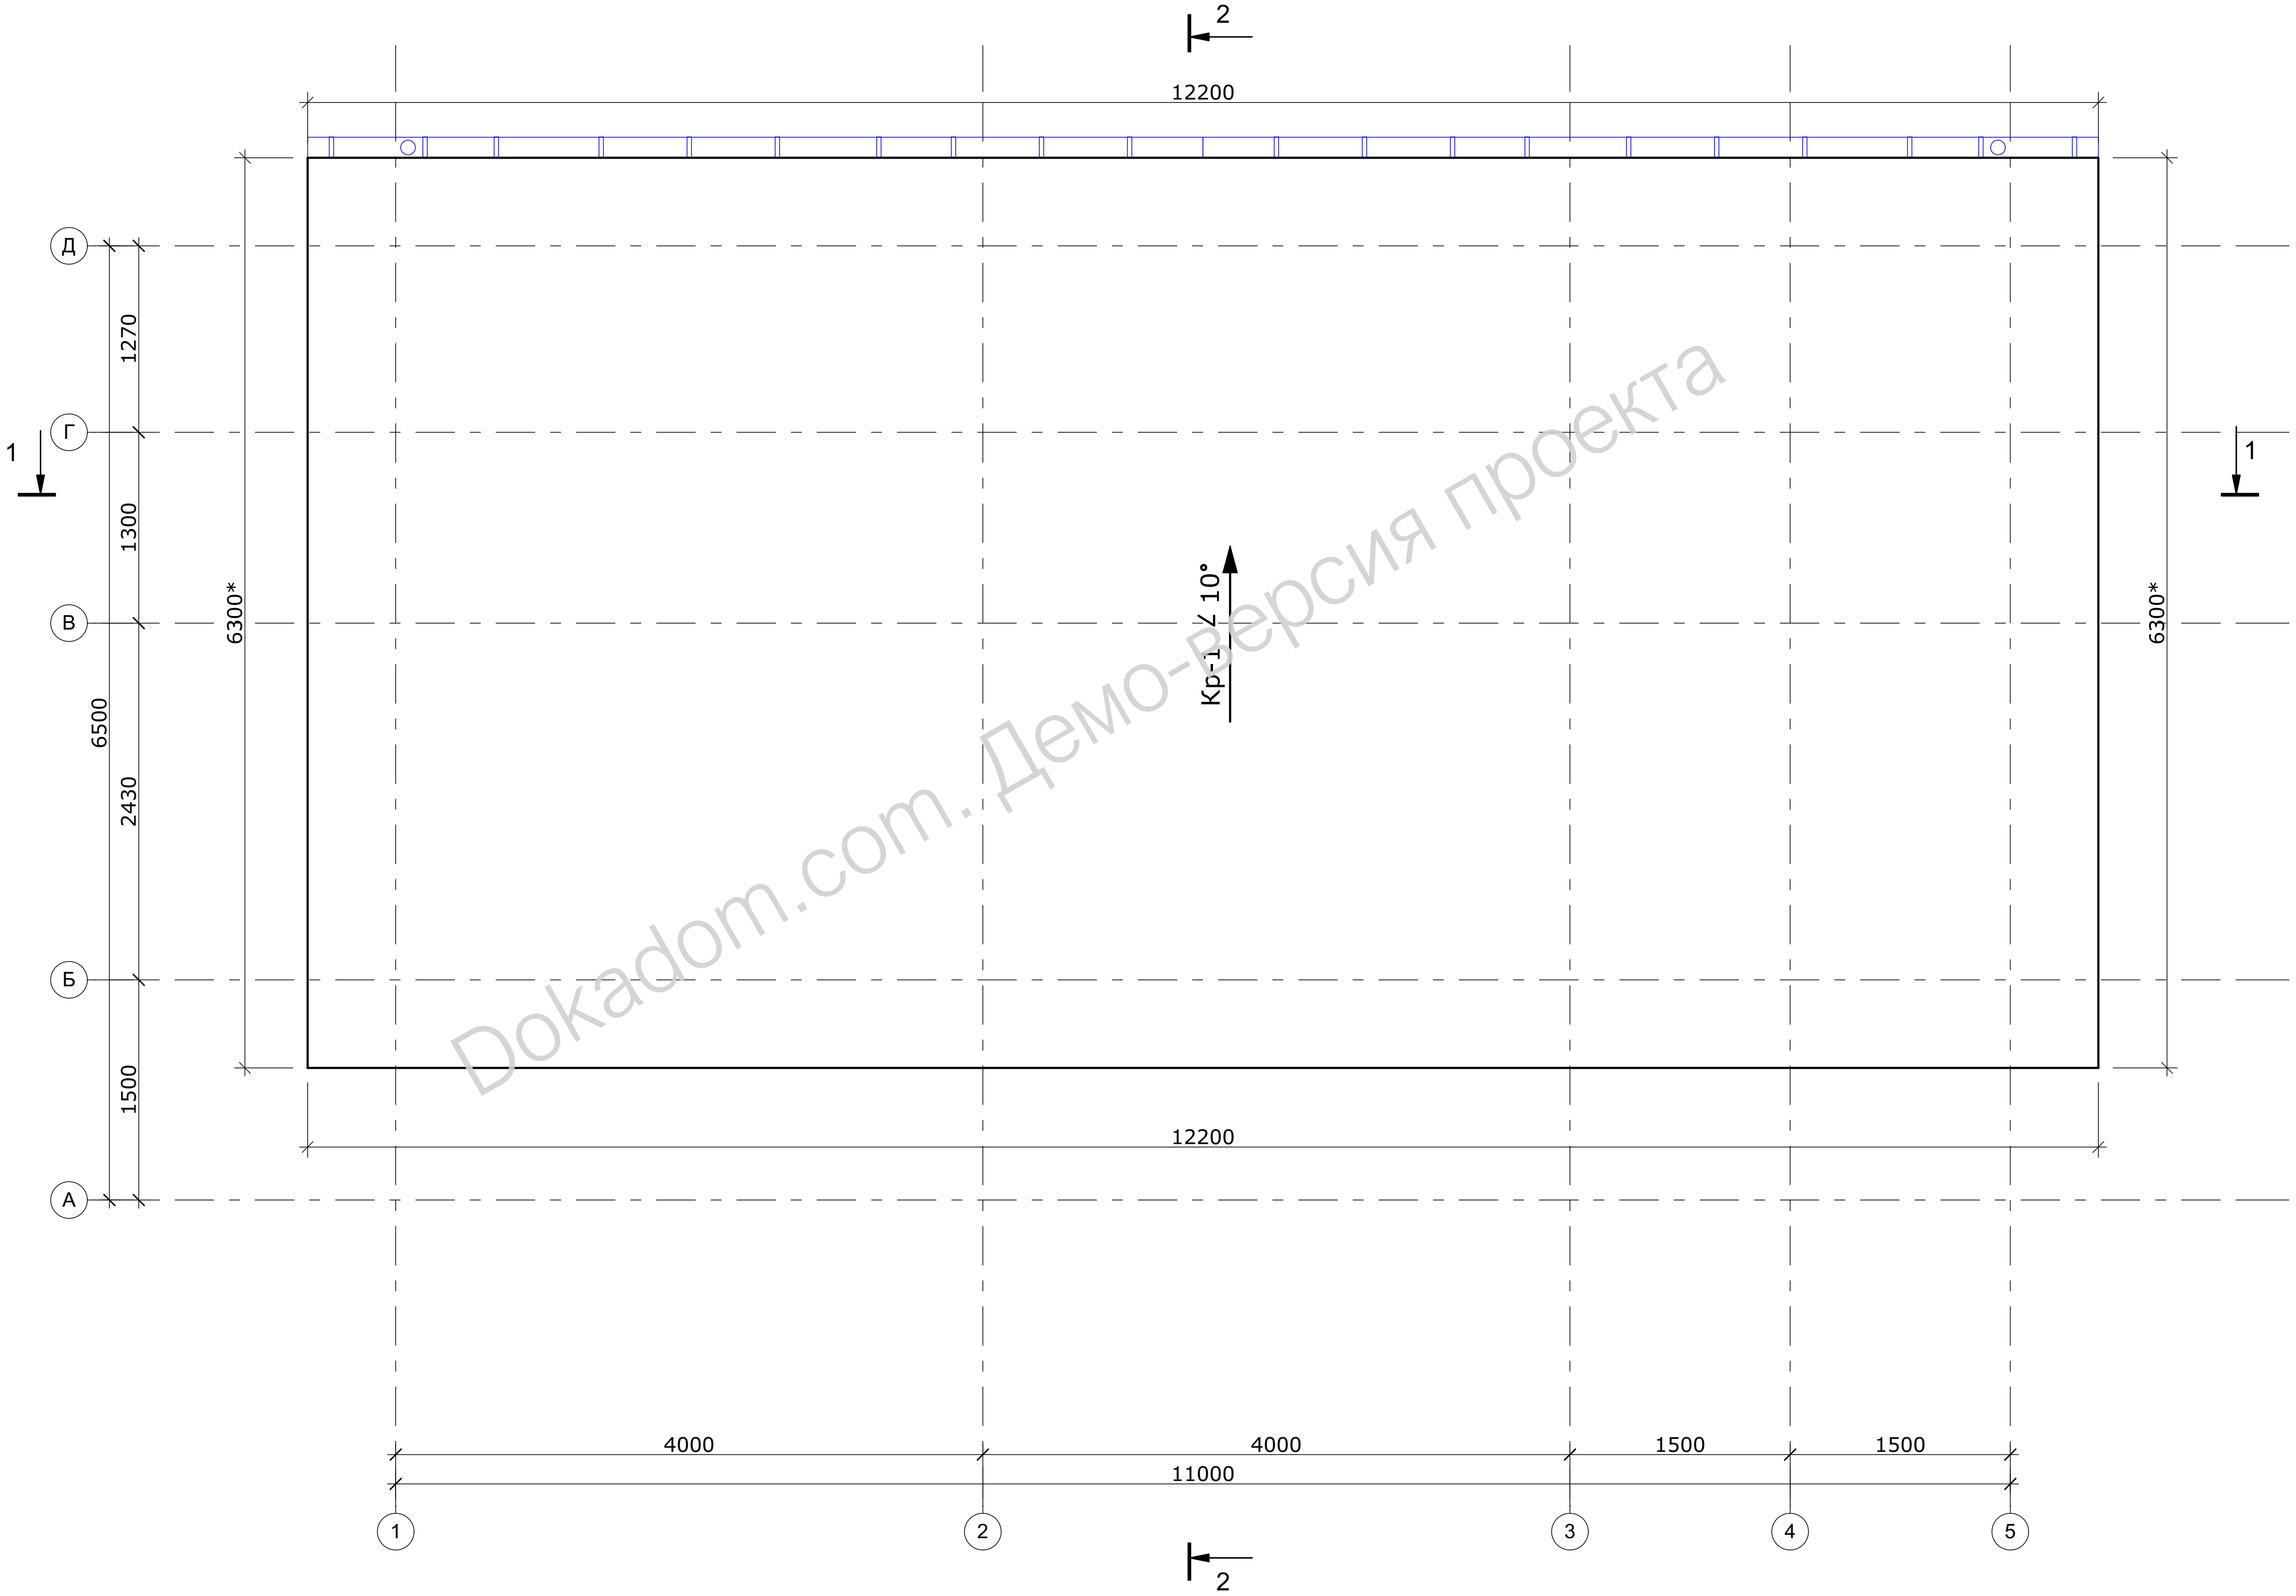

* - размер указан в натуральную величину.

Изм..	Кол.уч.	Лист	№док.	Подп.	Дата
Разработал		Саяпин П.			
Утвердил		Маркович П.В.			

АР

ООО "Каркасники"

Проект "Палома"

Стадия	Лист	Листов
РП	14	15

План кровли. М 1:50.

dokadom.com

Согласовано

Взам. инв. №

Подп. и дата

Инв.. № подп.

Копировал

1. Площадь кровли - 76,81 м2 (отход на раскрой не учтен).
длина коньков - 0,00 м;
длина торцов - 12,60 м;
длина карнизов - 24,40 м;
длина планки примыкания - 0,00 м.
длина ендовы - 0,00 м.

Кровельный материал - Металлочерепица, цвет:

2. Для вентиляции подкровельного пространства предусмотреть щелевую подшивку карнизов .

3. Поверх стропил утепленной кровли крепить гидроизоляцию мембрана диффузионная. Обрешётка выполняется из обрезной доски 25х100 мм с шагом 300 мм.

4. Кровельный материал укладывается согласно инструкции производителя.

Спецификация элементов водостока.

№ п/п	Наименование	Кол-во	Длина мм,
1	Желоб Водосточный 18	2	6100
2	Труба Водоотведения 18	2	1532
3	Отвод Трубы Водоотведения 18	2	877
4	Колено Трубы Водоотведения 18	2	291

Согласовано

Взам. инв. №

Подп. и дата

Инв. № подл.

Изм..	Кол.уч.	Лист	№док.	Подп.	Дата
Разработал	Саяпин П.				
Утвердил	Маркович П.В.				

АР

ООО "Каркасники"

Проект "Палома"

Стадия	Лист	Листов
РП	15	15

Общие данные к плану кровли.
Спецификация элементов водостока.

dokadom.com

Копировал

ВЕДОМОСТЬ ЧЕРТЕЖЕЙ КОМПЛЕКТА КМ

Лист	Наименование	Примечание
1	Общие данные. Ведомость чертежей.	
2	Конструктивная деталь устройства наружной стены.	
3	План свайного поля. М 1:50.	
4	Спецификация к плану свайного поля.	

ВЕДОМОСТЬ ОСНОВНЫХ КОМПЛЕКТОВ РАБОЧИХ ЧЕРТЕЖЕЙ

Обозначение	Наименование	Примечание
АР	Архитектурные решения	
КМ	Конструкции металлические	
КД	Конструкции деревянные	

Согласовано

Взам. инв. №

Подп. и дата

Инв.. № подп.

Изм..	Кол.уч.	Лист	№док.	Подп.	Дата
Разработал		Саяпин П.			
Утвердил		Маркович П.В.			

КМ

ООО "Каркасники"

Проект "Палома"

Стадия	Лист	Листов
РП	1	4

Общие данные. Ведомость чертежей.

dokadom.com

Копировал

КОНСТРУКТИВНАЯ ДЕТАЛЬ УСТРОЙСТВА КАРКАСА НАРУЖНОЙ СТЕНЫ

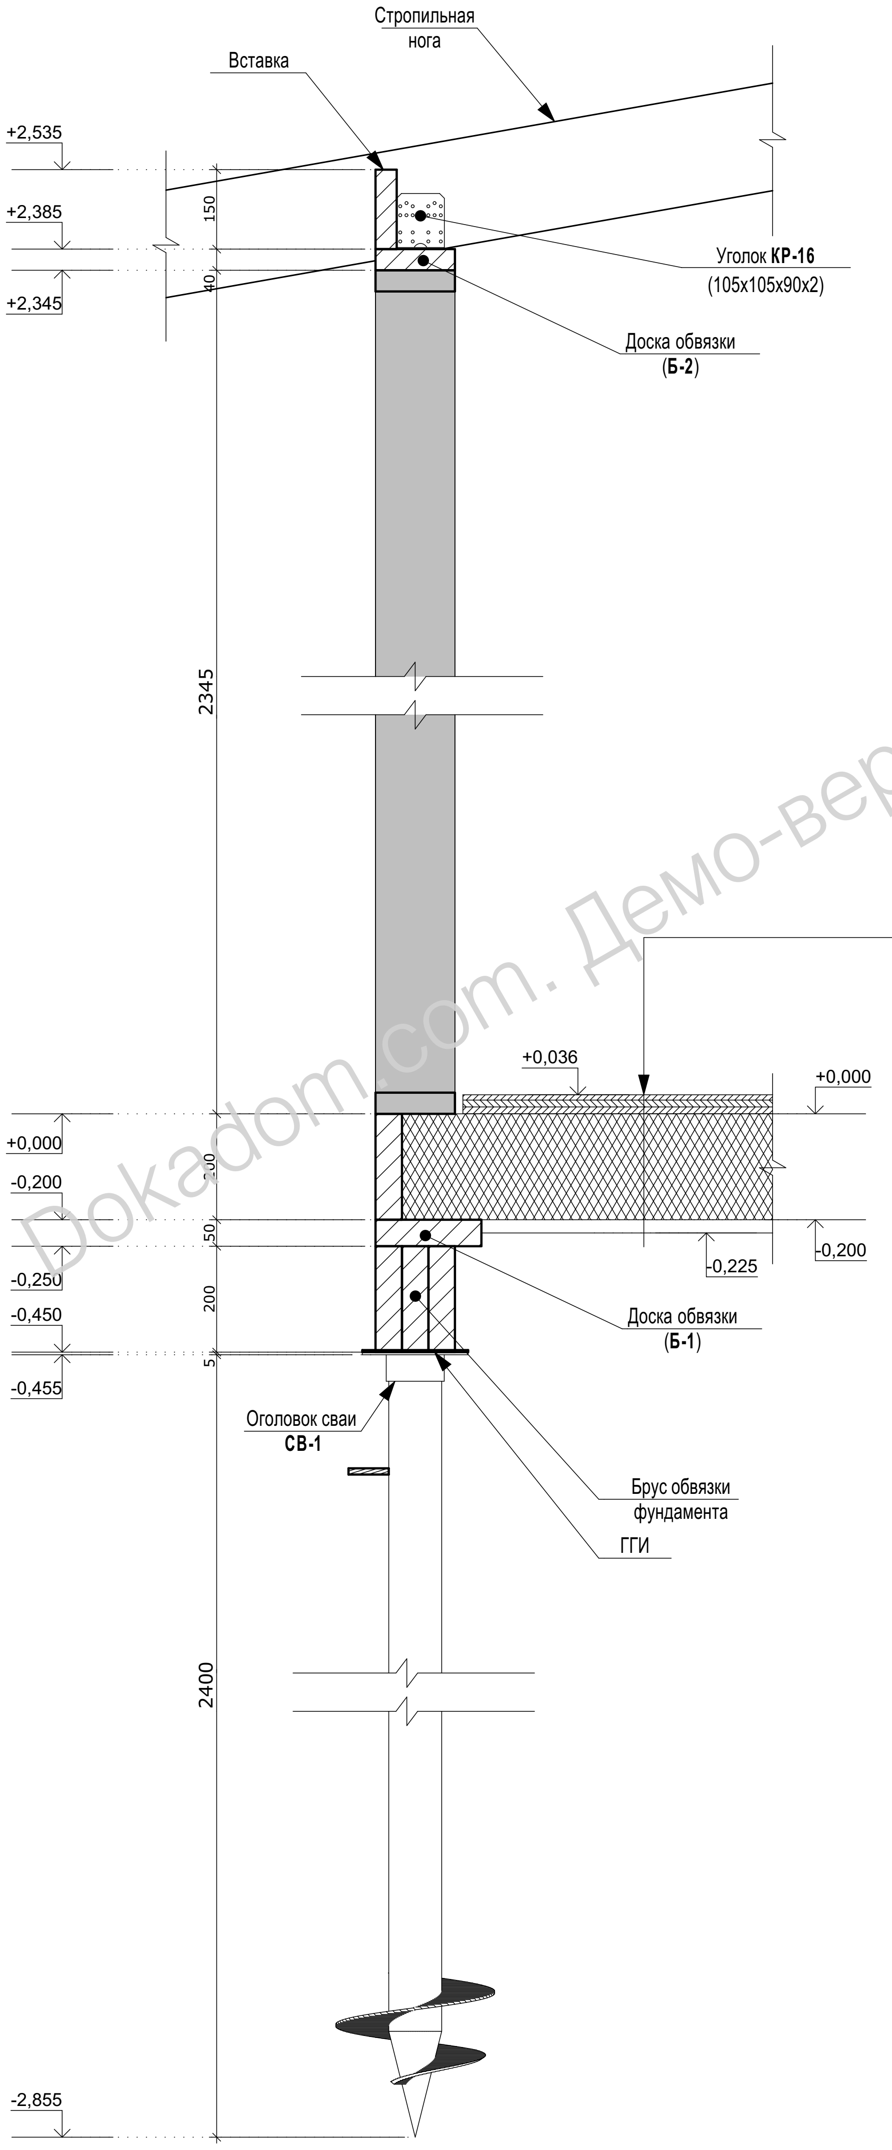

1. Доска шпунтованная, толщ. 36мм.	-36
2. Гидроизоляционная плёнка	
3. Балки пола сеч. 50х200, между которыми	
уложен утеплитель сγ=35 кг/м толщиной 200 мм	-200
4. Ветрозащитная мембрана	
5. Сетка оцинкованная, ячейка 2х2мм.	
6. Доска сеч. 25х100 для удержания сетки.	

Обшивки наружной стены условно не показаны.

Согласовано

Взам. инв. №

Подп. и дата

Инв. № подл.

Изм..	Кол.уч.	Лист	№док.	Подп.	Дата
Разработал		Саяпин П.			
Утвердил		Маркович П.В.			

КМ

ООО "Каркасники"

Проект "Палома"

Стадия	Лист	Листов
РП	2	4

Конструктивная деталь устройства наружной стены.

dokadom.com

Копировал

ПЛАН СВАЙНОГО ПОЛЯ. М 1:50.

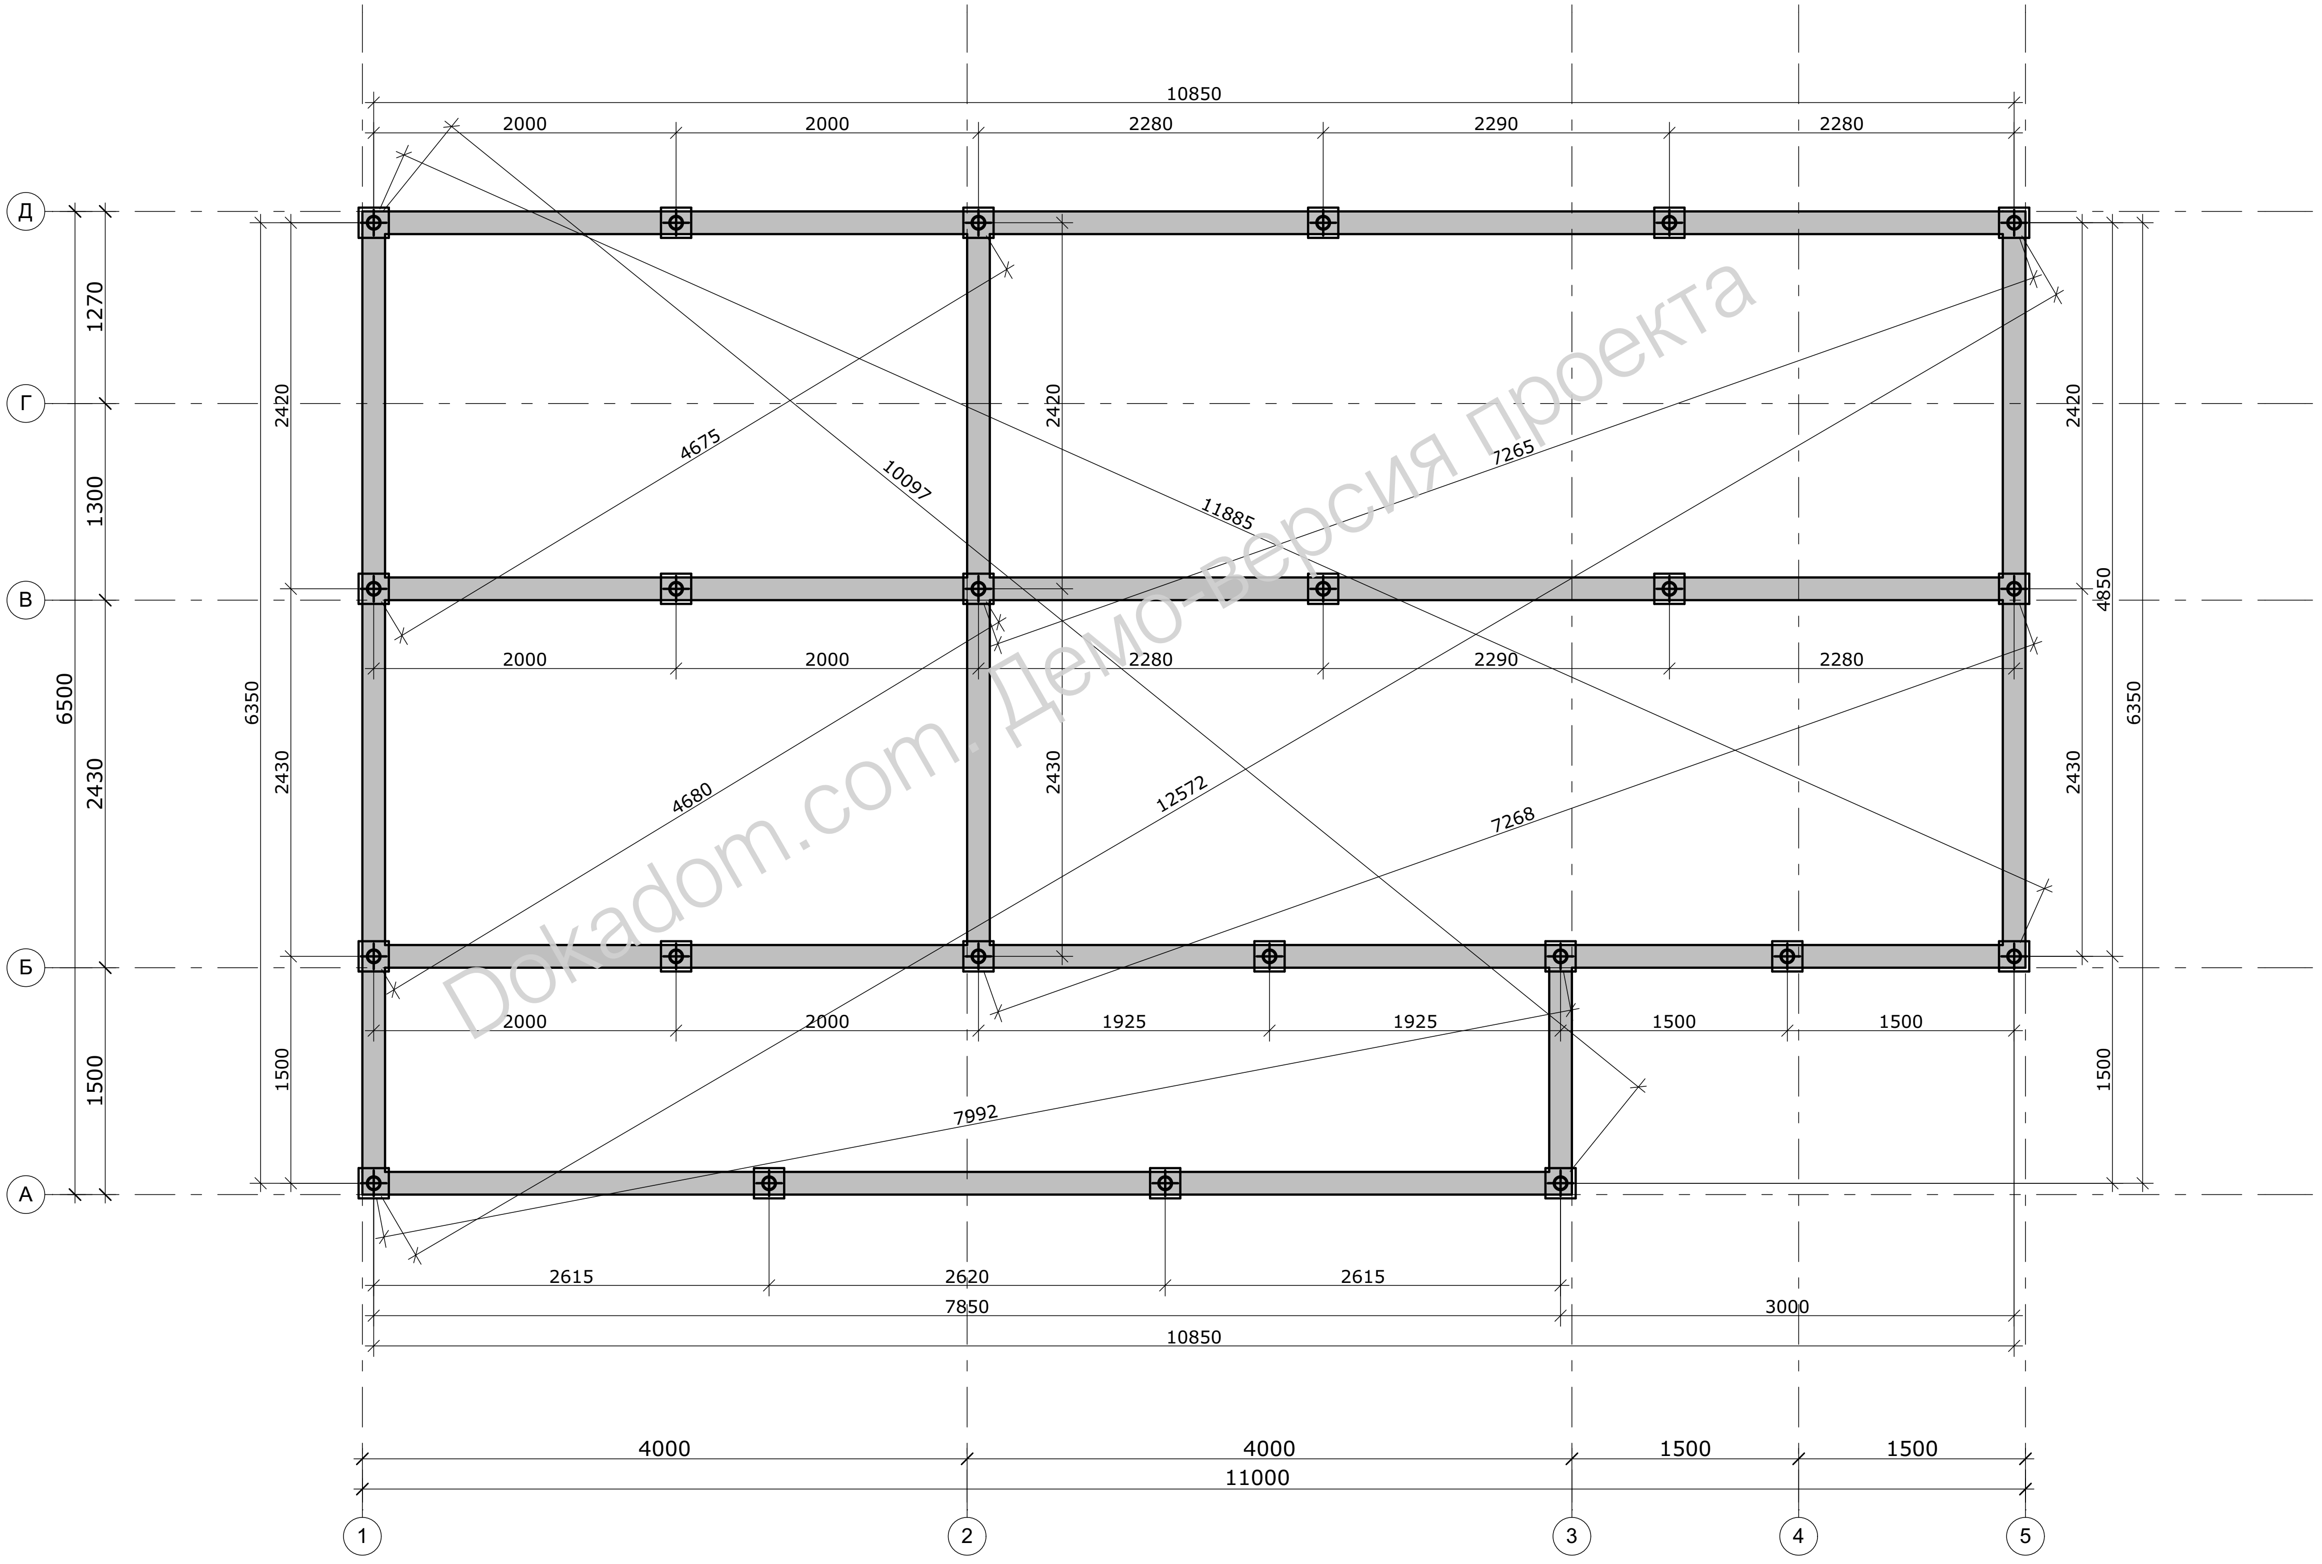

Согласовано

Взам. инв. №

Подп. и дата

Инв.. № подп.

Изм..	Кол.уч.	Лист	№док.	Подп.	Дата
Разработал		*Саяпин П.*			
Утвердил		*Маркович П.В.*			

КМ

ООО "Каркасники"

Проект "Палома"

Стадия	Лист	Листов
РП	3	4

План свайного поля. М 1:50.

dokadom.com

Копировал

ВЕДОМОСТЬ СВАЙ

Марка сваи	Номера свай	Отметки сваи		К-во, шт..	Условные обозначения
		Низа сваи	Верха сваи		
СВ-1		-2,855	-0,455	23	⌖

СПЕЦИФИКАЦИЯ МЕТАЛЛИЧЕСКИХ СВАЙ

Марка	Обозначение	Название	Длина 1 поз., мм	К-во, шт..	Вес 1 поз., кг	Общ. вес, кг	Примеч..
1	2	3	4	5	6	7	8
		Свая металлическая	2500	**23**	—	—	
		винтовая СВ-1					
СВ-1		Винтовая свая Ø108 мм с толщиной стенки ствола 4 мм. Толщина лопасти 5 мм; диаметр	2500	**23**	—	—	

СПЕЦИФИКАЦИЯ МЕТАЛЛИЧЕСКИХ КРЕПЁЖНЫХ ИЗДЕЛИЙ ДЛЯ СВАЙ

Марка	Обозначение	Название	Длина 1 поз., мм	К-во, шт..	Вес 1 поз., кг	Общ. вес, кг	Примеч..
1	2	3	4	5	6	7	8
		Оголовок сваи СВ-1	-	-	-		
1	ТУ 14-1-3023-80 Вст3 кп2-1 (с38/23)	- 200х200х5	200	23	2,51	**57,73**	
			—	—	—		

КМ

ООО "Каркасники"

Изм..	Кол.уч.	Лист	№док.	Подп.	Дата
Разработал		Саяпин П.			
Утвердил		Маркович П.В.			

Проект "Палома"

Стадия	Лист	Листов
РП	4	4

Спецификация к плану свайного поля.

dokadom.com

Копировал

Проект индивидуального жилого дома
по каркасной технологии

Проект "Палома"

Конструкции деревянные (КД)

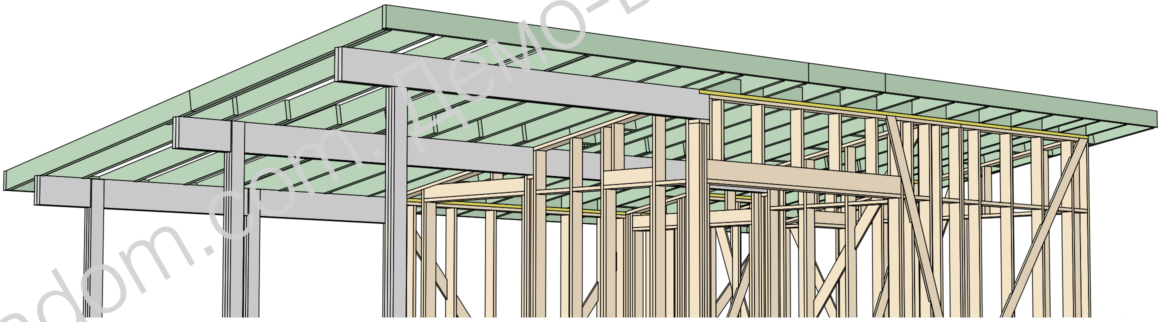

ОБЩИЕ УКАЗАНИЯ.

1. Рабочий проект жилого дома разработан на основании технического задания на проектирование, утвержденного заказчиком. Функциональное назначение здания - жилое.
2. Чертежи разработаны в соответствии с действующими нормами, правилами и стандартами.
3. Проект разработан для строительства в IIIВ климатическом подрайоне с температурой наружного воздуха наиболее холодной пятидневки -30°С с обеспеченностью 0.92 по СНиП 23-01-99* "Строительная климатология";
- расчетное значение веса снегового покрова для III-го снегового р-на по СНиП 2.01.07-85* "Нагрузки и воздействия" составляет - 180 кг/м²;
- скоростной напор ветра для III-го ветрового р-на по СНиП 2.01.07-85* составляет - 38 кгс/м²;

4. **Строительные конструкции запроектированы с учетом требований:**
- СНиП II-25-80 "Деревянные конструкции";
- СП 31-105-2002 "Проектирование и строительство энергоэффективных одноквартирных жилых домов с деревянным каркасом";
- СНиП 2.01.07-85* "Нагрузки и воздействия" (с изменением от 29 мая 2003 года);
- СНиП 2.08.01-89* "Жилые здания";
- СП 31-105-2002.

5. **Характеристика сооружения и конструктивные решения:**
- проектируемый жилой дом имеет в плане форму прямоугольника, кровля скатная;
- по конструктивной схеме здание запроектировано каркасным с несущими продольными стенами;
- несущие деревянные элементы стоек стен запроектированы из доски сечением 40х150мм (наружные стены);
- ненесущие деревянные элементы стоек стен запроектированы из доски сечением 40х100мм (стены несущие, перегородки);
- балки перекрытий запроектированы из доски сечением 50х200мм;
- несущие элементы стропил запроектированы из доски сечением 50х200мм;
- крыша жилого дома запроектирована скатной с наружным организованным водоотводом.

6. Деревянные конструкции запроектированы из пиленного леса хвойных пород II сорта по ГОСТ

твии с

ами
элементов
о выбору

ганизация

ВЕДОМОСТЬ ЧЕРТЕЖЕЙ ЕОМПЛЕКТА КД

Лист	Наименование	Примечание
	Титульный лист	
1	Общие данные. Ведомость чертежей конструкций деревянных. (начало)	
2	Ведомость чертежей конструкций деревянных. (окончание)	
3	Разбивочный план осей. М 1:50.	
4	Конструктивная деталь устройства каркаса наружной стены.	
5	План бруса обвязки фундамента (низ отм. -0,450). М 1:50.	
6	Спецификация к плану бруса обвязки фундамента. (начало)	
7	Спецификация к плану бруса обвязки фундамента. (окончание) Узел 1.	
8	Брус обвязки поз. 1-9.	
9	Брус обвязки поз. 10-15.	
10	План обвязочной доски Б-1. (низ отм. -0,250) М 1:50.	
11	Спецификация к плану доски обвязки Б-1.	
12	План балок перекрытия 1-го этажа (низ отм. -0,200). М 1:50.	
13	Спецификация к плану балок перекрытия 1-го этажа.	
14	Узел 2.	
15	Схема стеновых щитов 1-го этажа. М 1:50.	
16	Стеновой щит Щ-1. Спецификация элементов щита.	
17	Стеновой щит Щ-2. Спецификация элементов щита.	
18	Стеновой щит Щ-3. Спецификация элементов щита.	
19	Стеновой щит Щ-4. Спецификация элементов щита.	

Изм..	Кол.уч.	Лист	№док.	Подп.	Дата
Разработал		*Саянин П.*			
Утвердил		*Маркович П.В.*			

КД

ООО "Каркасники"

Проект "Палома"

Стадия	Лист	Листов
РП	1	53

Общие данные. Ведомость чертежей конструкций деревянных. (начало)

dokadom.com

Копировал

Лист	Наименование	Примечание
20	Стеновой щит Щ-5. Спецификация элементов щита.	
21	Стеновой щит Щ-6. Спецификация элементов щита.	
22	Стеновой щит Щ-7. Спецификация элементов щита.	
23	Стеновой щит Щ-8. Спецификация элементов щита.	
24	Стеновой щит Щ-9. Спецификация элементов щита.	
25	Стеновой щит Щ-10. Спецификация элементов щита.	
26	План обвязочной доски Б-2 над стеновыми щитами 1-го этажа. М 1:50.	
27	Спецификация к плану доски обвязки Б-2. Спецификация элементов колонн террасы. Поз. КТ-1.	
28	Спецификация элементов колонн террасы. Поз. КТ-2. Поз. КТ-3.	
29	План балок террасы. М 1:50.	
30	Спецификация к плану балок крыльца. Узел 3. Узел 4. Узел 5.	
31	План кровли. М 1:50.	
32	Общие данные к плану кровли. Спецификация элементов	

Лист	Наименование	Примечание
46	Общий вид стеновых щитов 1-го этажа с доской обвязки Б-2. Точка 1.	
47	Общий вид стеновых щитов 1-го этажа с доской обвязки Б-2. Точка 2.	
48	Общий вид стеновых щитов 1-го этажа с доской обвязки Б-2. Точка 3.	
49	Общий вид стеновых щитов 1-го этажа с доской обвязки Б-2. Точка 4.	
50	Общий вид стропильной системы. Точка 1.	
51	Общий вид стропильной системы. Точка 2.	
52	Общий вид стропильной системы. Точка 3.	
53	Общий вид стропильной системы. Точка 4.	

КД

Изм.. Кол.уч. Лист №док. Подп. Дата
Разработал Саяпин П.
Утвердил Маркович П.В.

ООО "Каркасники"

Проект "Палома"

Стадия	Лист	Листов
РП	2	53

Ведомость чертежей конструкций деревянных. (окончание)

dokadom.com

Копировал

РАЗБИВОЧНЫЙ ПЛАН ОСЕЙ. М 1:50.

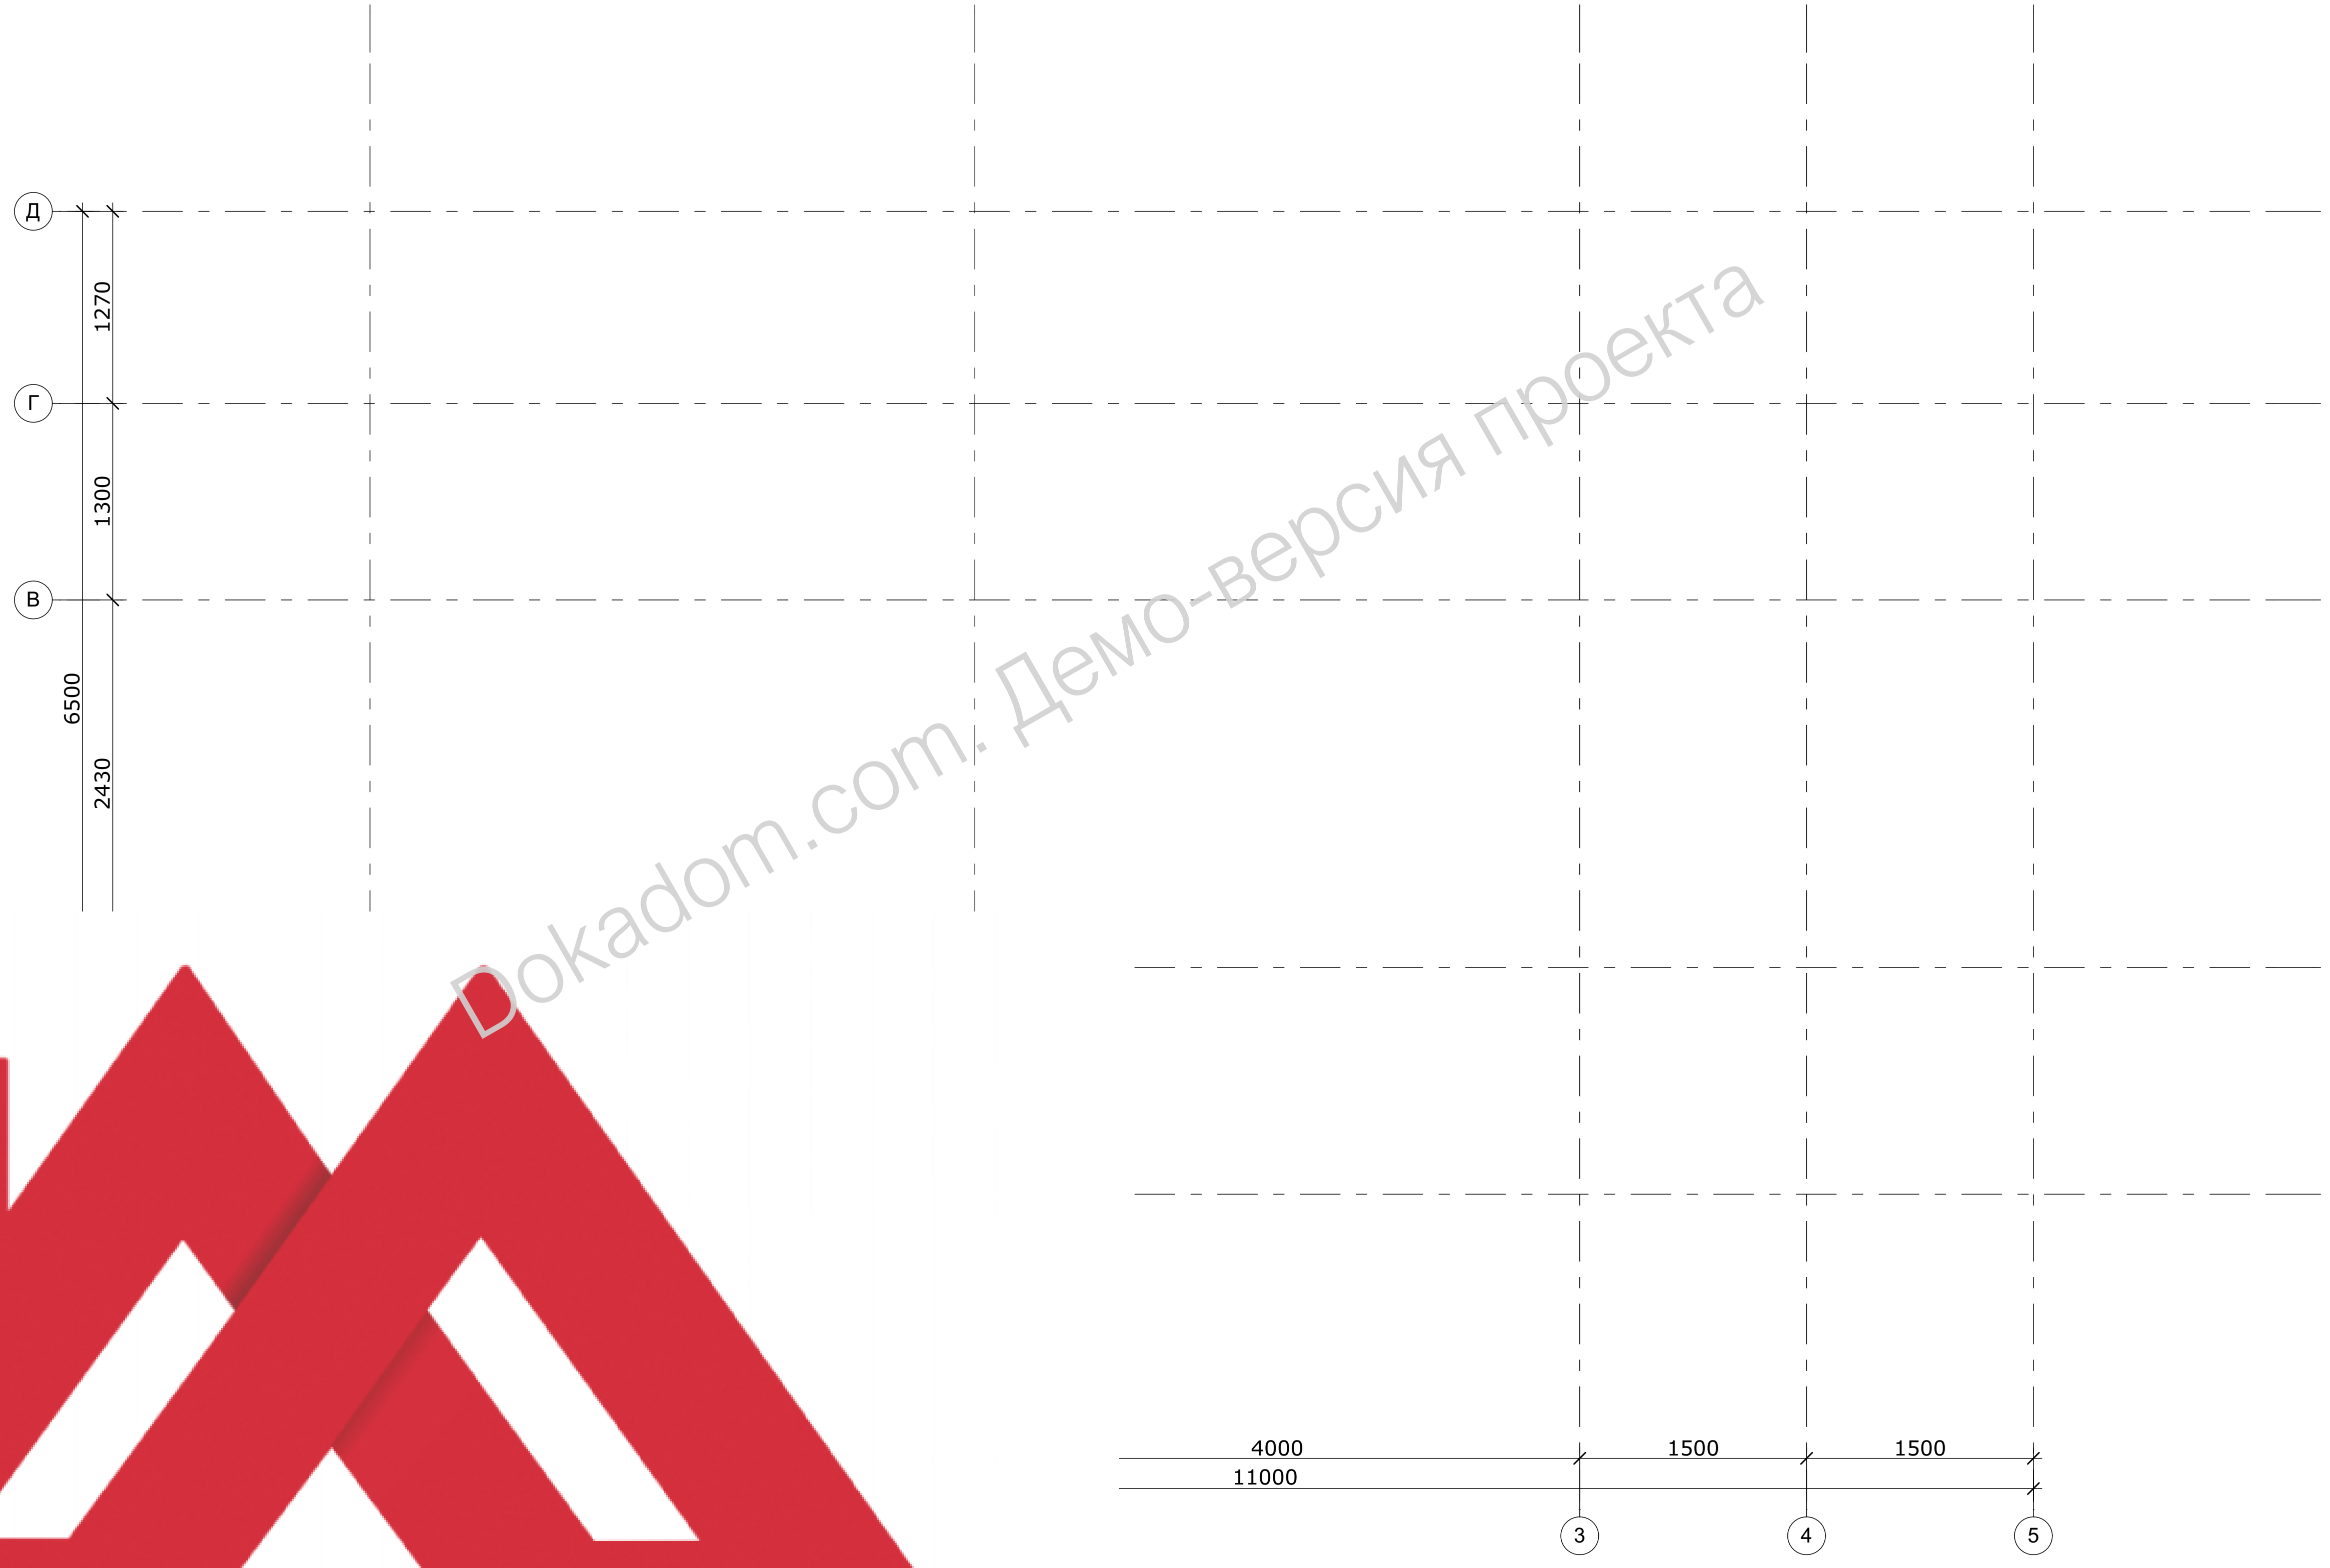

Изм..	Кол.уч.	Лист	№док.	Подп.	Дата
Разработал		Саяпин П.			
Утвердил		Маркович П.В.			

КД

ООО "Каркасники"

Проект "Палома"

Стадия	Лист	Листов
РП	3	53

Разбивочный план осей. М 1:50.

dokadom.com

Копировал

КОНСТРУКТИВНАЯ ДЕТАЛЬ УСТРОЙСТВА КАРКАСА НАРУЖНОЙ СТЕНЫ

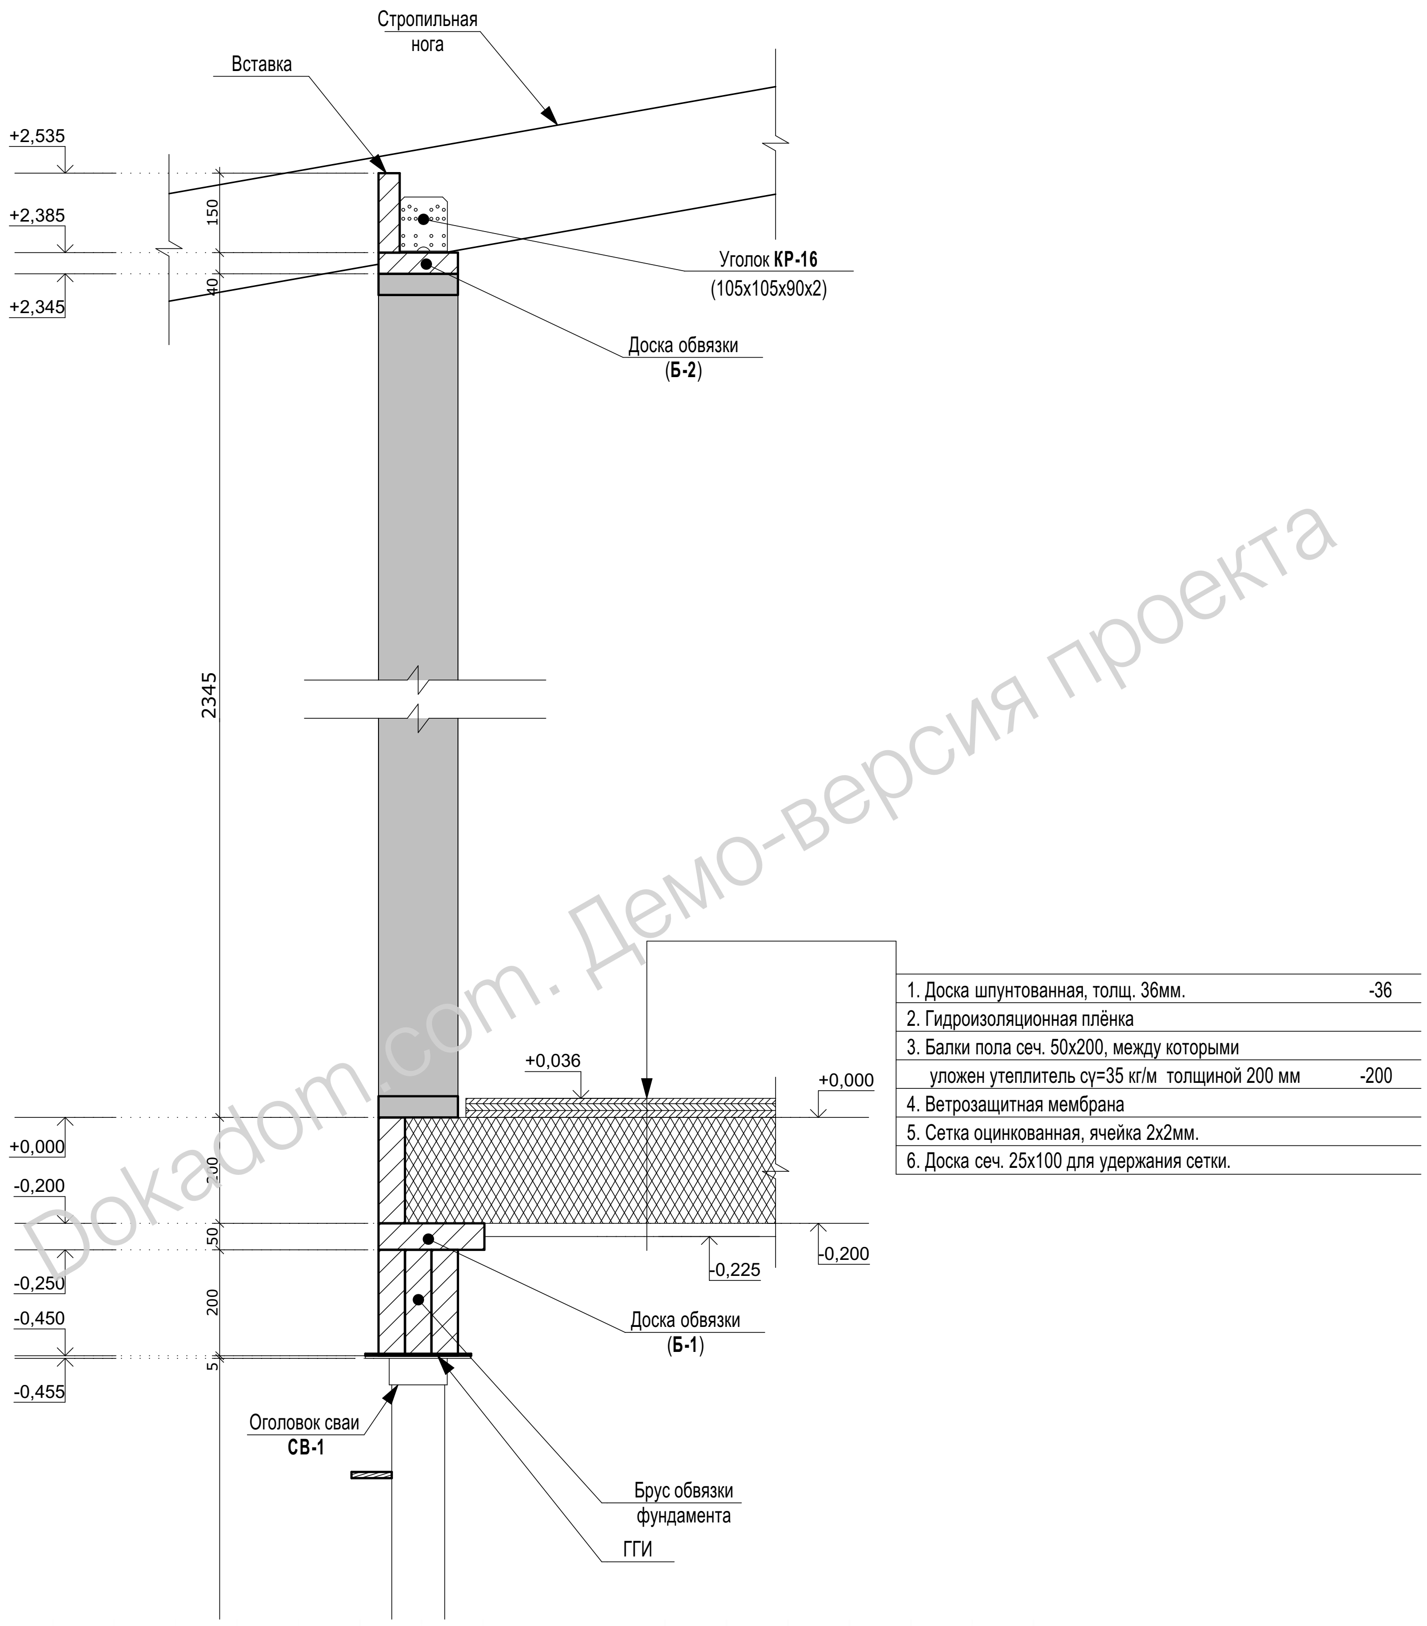
Стропильная нога
Вставка
+2,535
+2,385
+2,345
150
40
Уголок КР-16
(105х105х90х2)
Доска обвязки
(Б-2)
2345
1. Доска шпунтованная, толщ. 36мм. -36
2. Гидроизоляционная плёнка
3. Балки пола сеч. 50х200, между которыми
уложен утеплитель су=35 кг/м толщиной 200 мм -200
4. Ветрозащитная мембрана
5. Сетка оцинкованная, ячейка 2х2мм.
6. Доска сеч. 25х100 для удержания сетки.
+0,036
+0,000
+0,000
-0,200
200
50
-0,250
-0,450
200
5
-0,455
-0,225
-0,200
Доска обвязки
(Б-1)
Оголовок сваи
СВ-1
Брус обвязки
фундамента
ГГИ

Обшивки наружной стены условно не показаны.

КД			
ООО "Каркасники"			
алома"	Стадия	Лист	Листов
	РП	4	53
аль устройства ой стены.	dokadom.com		

ПЛАН БРУСА ОБВЯЗКИ (низ отм. -0,450), М 1:50.

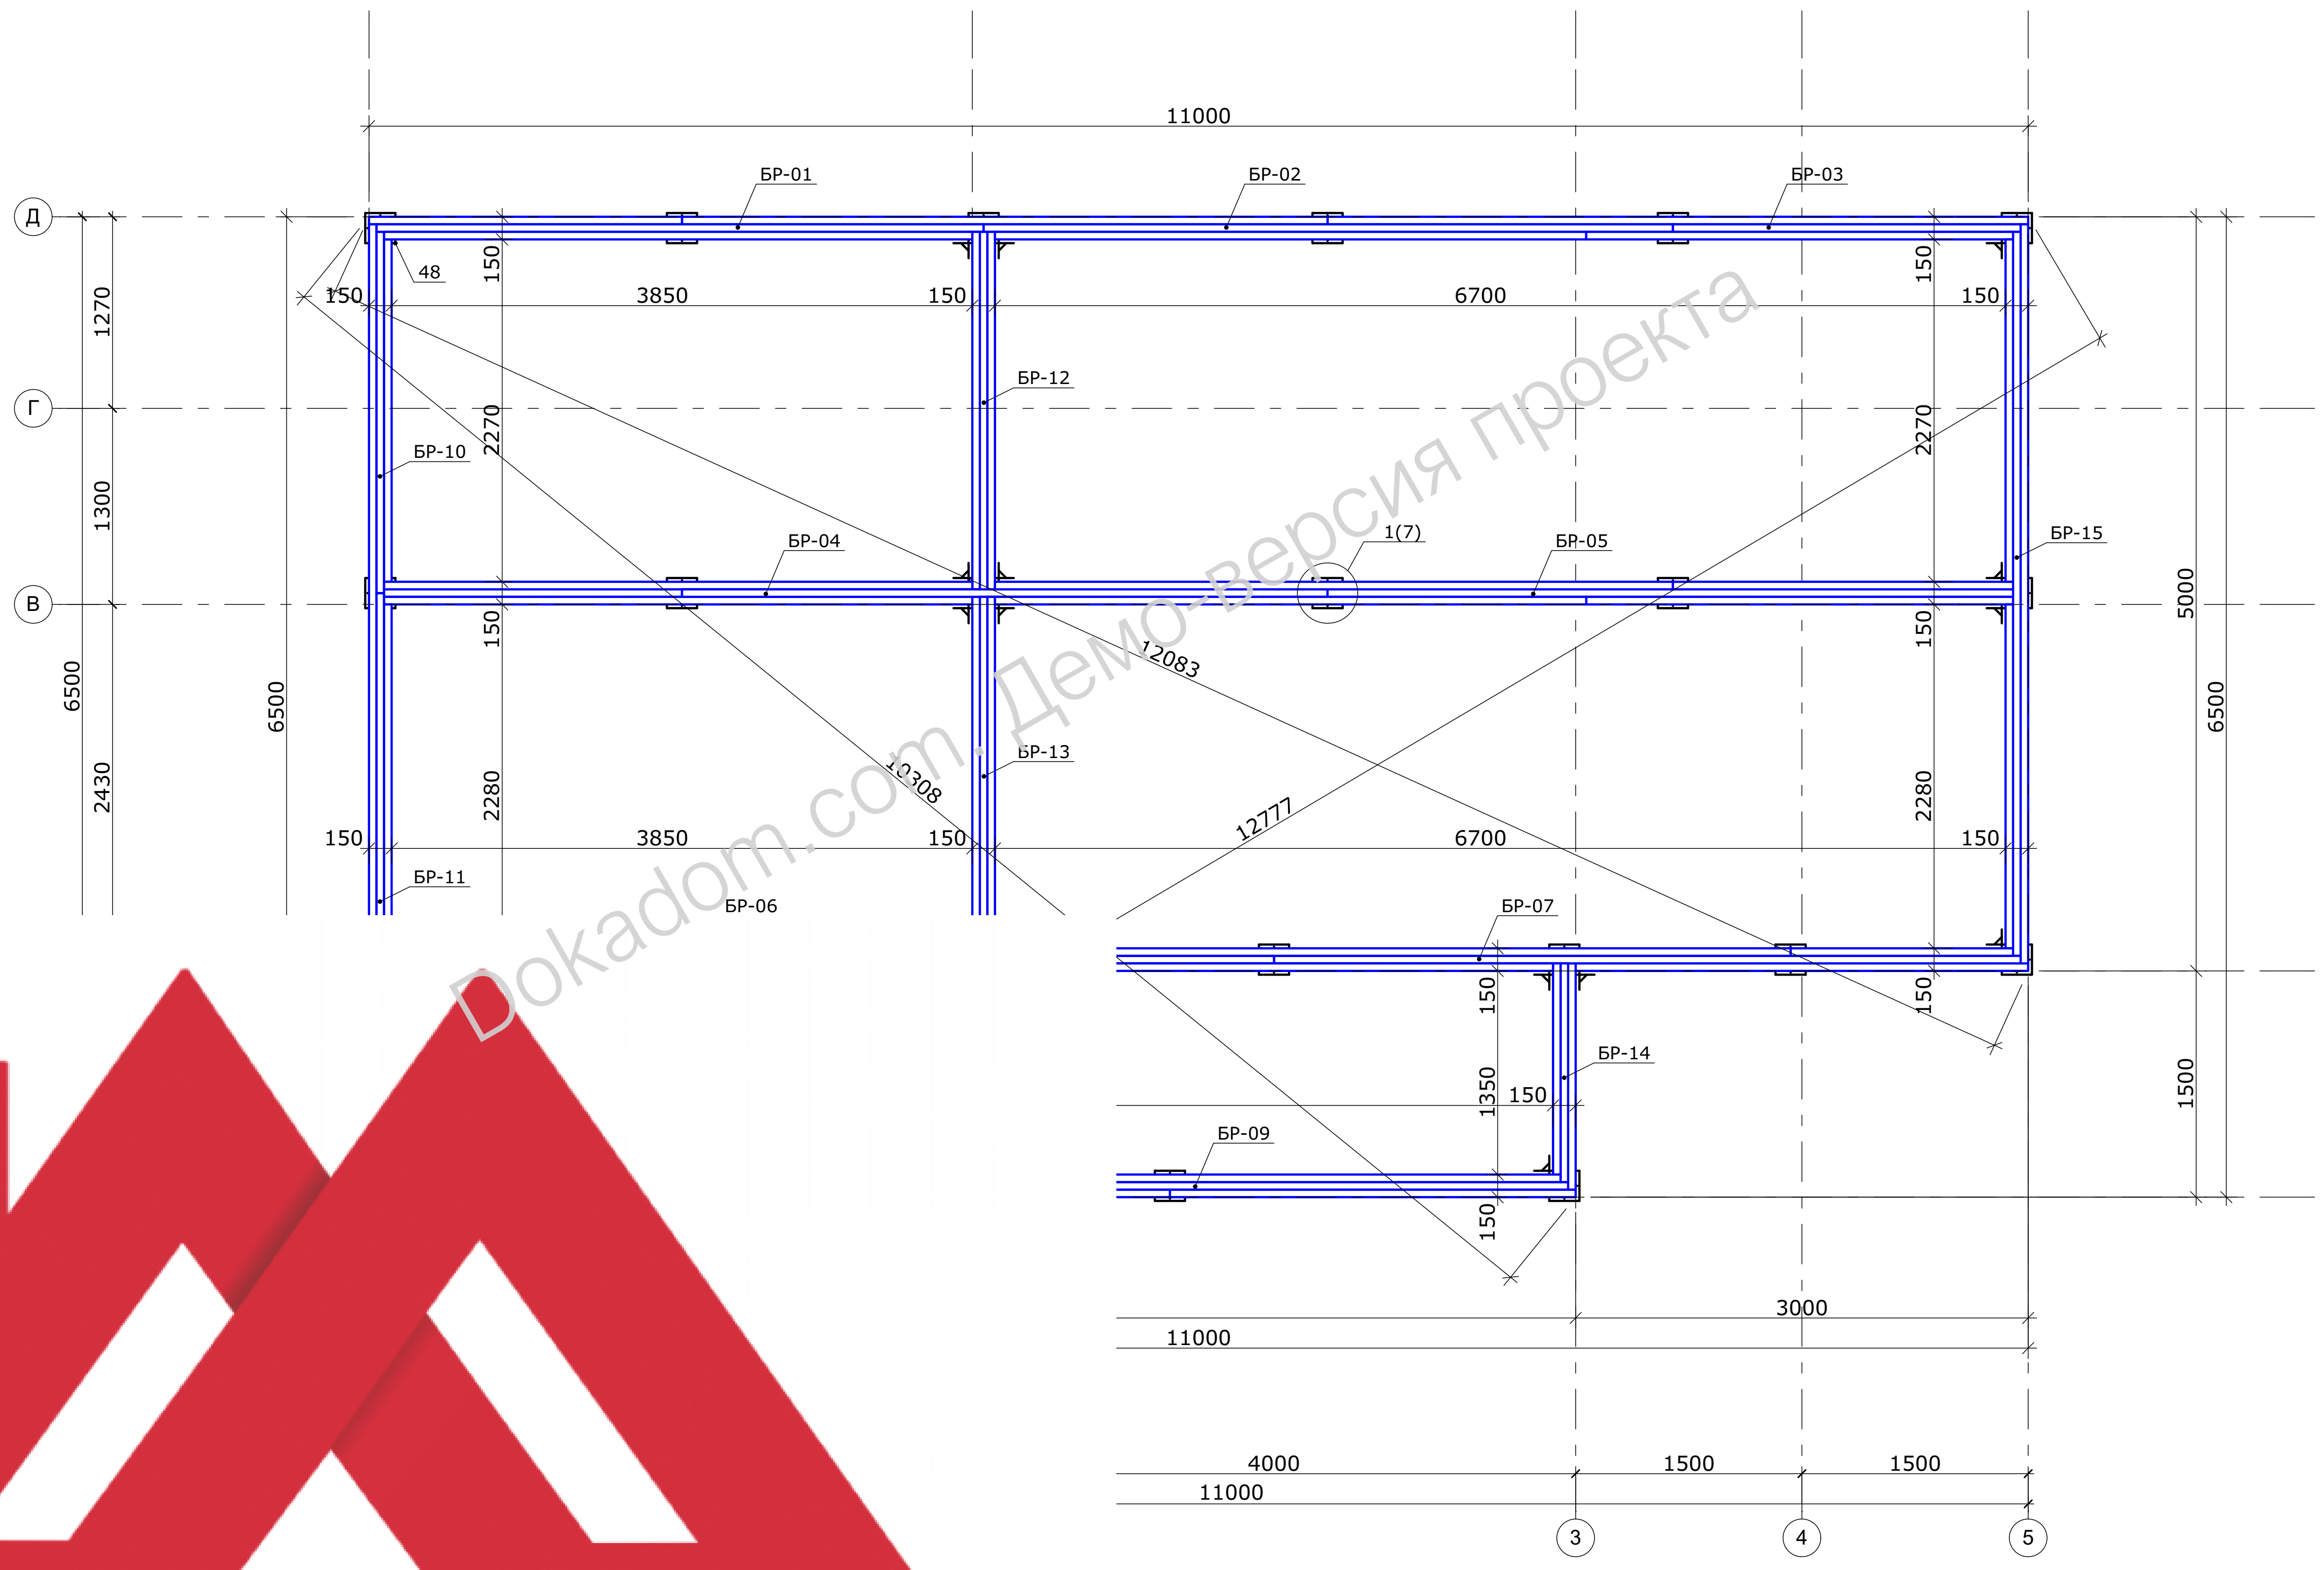

КД

ООО "Каркасники"

Изм..	Кол.уч.	Лист	№док.	Подп.	Дата
Разработал		Саяпин П.			
Утвердил		Маркович П.В.			

Проект "Палома"

Стадия	Лист	Листов
РП	5	53

План бруса обвязки фундамента (низ отм. -0,450). М 1:50.

dokadom.com

Копировал

Спецификация к плану балок обвязки фундамента. БР-01.

Поз.	Сечениение	Наименование	Длина 1 поз.	Кол-во поз. шт.	Общий объем поз. м.3	Масса 1 поз. кг.	Примечание
1	п/м 50х200	балка ростверка	4025	1	0,040	28,18	
2	п/м 50х200	балка ростверка	3900	1	0,039	27,30	
3	п/м 50х200	балка ростверка	2075	1	0,021	14,53	
					0,100 м³	70,00	

Спецификация к плану балок обвязки фундамента. БР-02.

Поз.	Сечениение	Наименование	Длина 1 поз.	Кол-во поз. шт.	Общий объем поз. м.3	Масса 1 поз. кг.	Примечание
4	п/м 50х200	балка ростверка	4570	1	0,046	31,99	
5	п/м 50х200	балка ростверка	4280	1	0,043	29,96	
6	п/м 50х200	балка ростверка	3920	1	0,039	27,44	
					0,128 м³	89,39	

Спецификация к плану балок обвязки фундамента. БР-03.

Поз.	Сечениение	Наименование	Длина 1 поз.	Кол-во поз. шт.	Общий объем поз. м.3	Масса 1 поз. кг.	Примечание
7	п/м 50х200	балка ростверка	4645	1	0,046	32,51	
8	п/м 50х200	балка ростверка	2830	1	0,028	19,81	
9	п/м 50х200	балка ростверка	2305	1	0,023	16,14	

Спецификация к плану балок обвязки фундамента. БР-06.

Поз.	Сечениение	Наименование	Длина 1 поз.	Кол-во поз. шт.	Общий объем поз. м.3	Масса 1 поз. кг.	Примечание
18	п/м 50х200	балка ростверка	5900	1	0,059	41,30	
19	п/м 50х200	балка ростверка	3900	1	0,039	27,30	
20	п/м 50х200	балка ростверка	1975	1	0,020	13,83	
					0,118 м³	82,42	

Спецификация к плану балок обвязки фундамента. БР-07.

Поз.	Сечениение	Наименование	Длина 1 поз.	Кол-во поз. шт.	Общий объем поз. м.3	Масса 1 поз. кг.	Примечание
21	п/м 50х200	балка ростверка	5775	1	0,058	40,42	
22	п/м 50х200	балка ростверка	5275	1	0,053	36,93	
23	п/м 50х200	балка ростверка	4950	1	0,050	34,65	
24	п/м 50х200	балка ростверка	3000	1	0,030	21,00	
25	п/м 50х200	балка ростверка	1475	1	0,015	10,33	
					0,206 м³	143,33	

Спецификация к плану балок обвязки фундамента. БР-08.

Поз.	Сечениение	Наименование	Длина 1 поз.	Кол-во поз. шт.	Общий объем поз. м.3	Масса 1 поз. кг.	Примечание
26	п/м 50х200	балка ростверка	5310	1	0,053	37,17	
27	п/м 50х200	балка ростверка	3245	1	0,032	22,72	
28	п/м 50х200	балка ростверка	2640	1	0,026	18,48	
					0,111 м³	78,37	

Спецификация к плану балок обвязки фундамента. БР-09.

Поз.	Сечениение	Наименование	Длина 1 поз.	Кол-во поз. шт.	Общий объем поз. м.3	Масса 1 поз. кг.	Примечание
29	п/м 50х200	балка ростверка	5260	1	0,053	36,82	
30	п/м 50х200	балка ростверка	4555	1	0,046	31,88	
31	п/м 50х200	балка ростверка	2690	1	0,027	18,83	
					0,126 м³	87,53	

Изм..	Кол.уч.	Лист	№док.	Подп.	Дата
Разработал		Саяпин П.			
Утвердил		Маркович П.В.			

КД

ООО "Каркасники"

Проект "Палома"

Стадия	Лист	Листов
РП	6	53

Спецификация к плану бруса обвязки фундамента. (начало)

dokadom.com

Копировал

Спецификация к плану балок обвязки фундамента. БР-10.

Поз.	Сеченение	Наименование	Длина 1 поз.	Кол-во поз. шт.	Общий объем поз. м.3	Масса 1 поз. кг.	Примечание
32	п/м 50x200	балка ростверка	4875	1	0,049	34,13	
33	п/м 50x200	балка ростверка	2395	1	0,024	16,76	
34	п/м 50x200	балка ростверка	2270	1	0,023	15,89	
					0,096 м³	66,78	

Спецификация к плану балок обвязки фундамента. БР-11.

Поз.	Сеченение	Наименование	Длина 1 поз.	Кол-во поз. шт.	Общий объем поз. м.3	Масса 1 поз. кг.	Примечание
35	п/м 50x200	балка ростверка	3905	1	0,039	27,34	
36	п/м 50x200	балка ростверка	2280	1	0,023	15,96	
37	п/м 50x200	балка ростверка	1525	1	0,015	10,67	
38	п/м 50x200	балка ростверка	1350	1	0,014	9,45	
					0,091 м³	63,42	

Спецификация к плану балок обвязки фундамента. БР-12.

Поз.	Сеченение	Наименование	Длина 1 поз.	Кол-во поз. шт.	Общий объем поз. м.3	Масса 1 поз. кг.	Примечание
39	п/м 50x200	балка ростверка	2370	3	0,072	16,59	
					0,072 м³	49,77	

СПЕЦИФИКАЦИЯ МЕТАЛЛИЧЕСКИХ КРЕПЕЖНЫХ ИЗДЕЛИЙ

Поз.	Обозначение	Наименование	Длина 1 поз.	Кол-во шт.	Общий объем поз. м.3	Масса 1поз. кг.	Примечание
48		Уголок металлический усиленный (105x105x90x2,5)		21			
49		Шуруп (глухарь) М10x120		92			

КРЕПЛЕНИЕ БРУСА ОБВЯЗКИ К СВАЯМ.

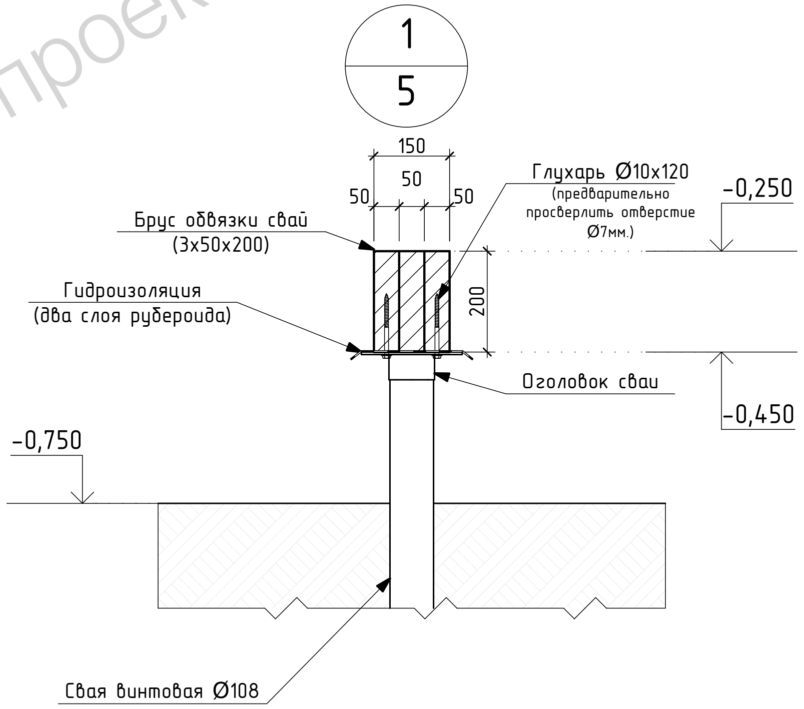

Изм..	Кол.уч.	Лист	№док.	Подп.	Дата
Разработал		Саяпин П.			
Утвердил		Маркович П.В.			

КД

ООО "Каркасники"

Проект "Палома"

Стадия	Лист	Листов
РП	7	53

Спецификация к плану бруса обвязки фундамента. (окончание) Узел 1.

dokadom.com

Копировал

Балка БР-1

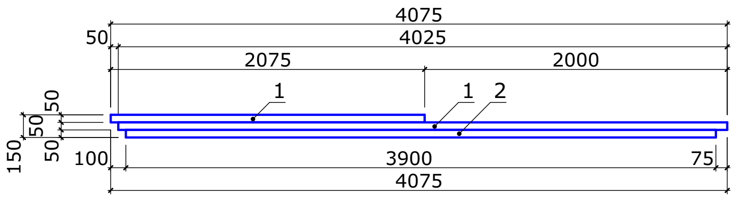

Балка БР-2

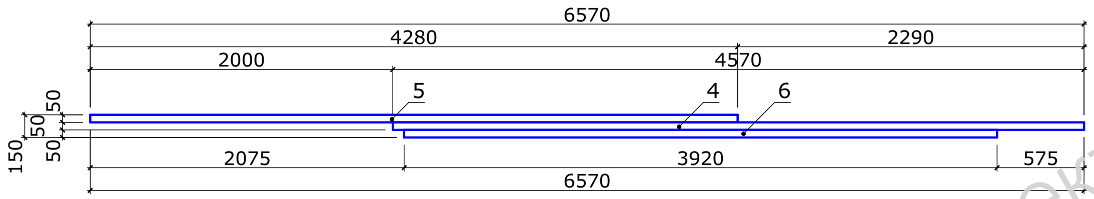

Балка БР-3

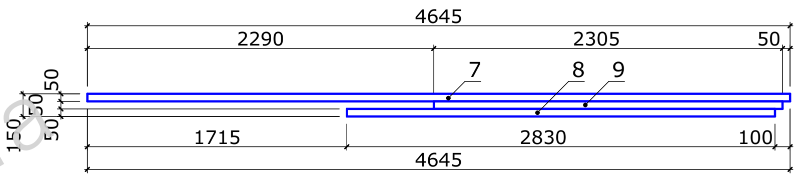

Балка БР-4

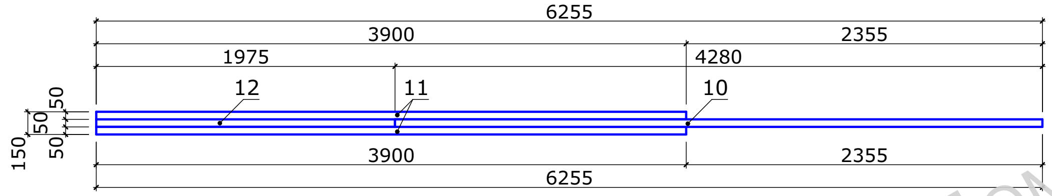

Балка БР-5

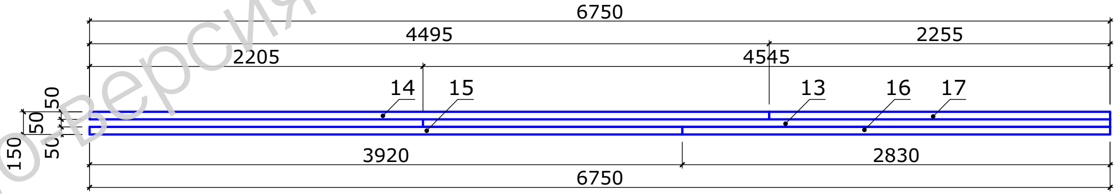

Балка БР-6

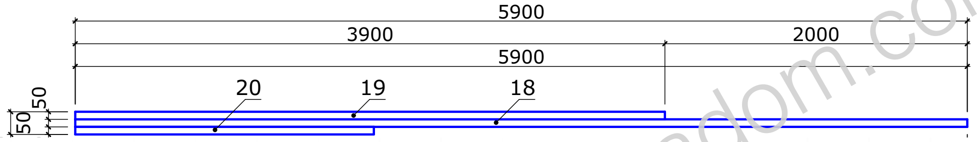

Балка БР-7

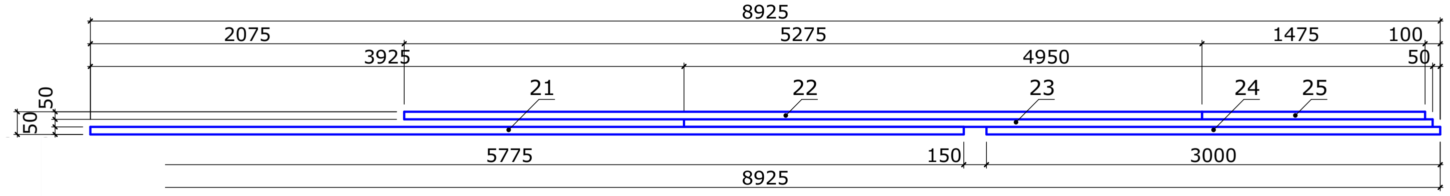

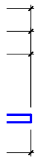

Балка БР-9

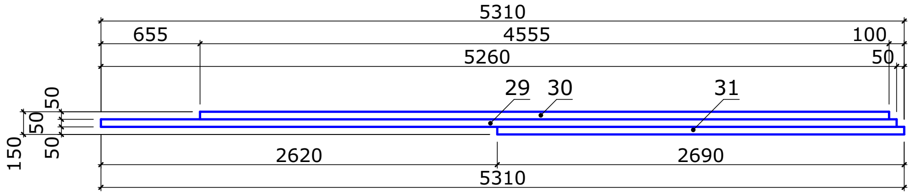

Изм..	Кол.уч.	Лист	№док.	Подп.	Дата	
Разработал	Саяпин П.					
Утвердил	Маркович П.В.					

КД

ООО "Каркасники"

	Стадия	Лист	Листов
Проект "Палома"	РП	8	53
Брус обвязки поз. 1-9.	dokadom.com		

Копировал

Балка Б-10

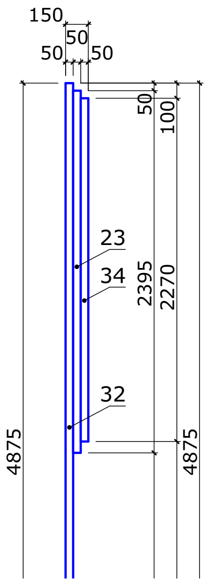

Балка Б-11

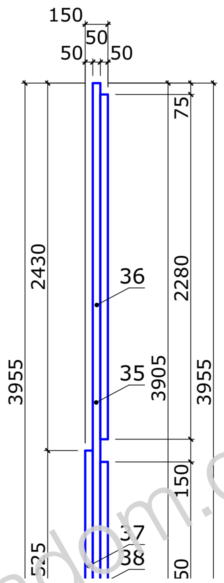

Балка Б-12

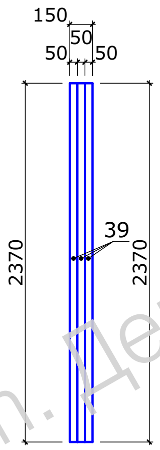

Балка Б-13

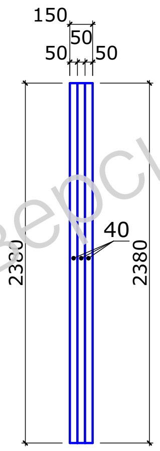

Балка Б-14

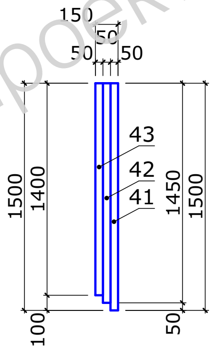

Балка Б-15

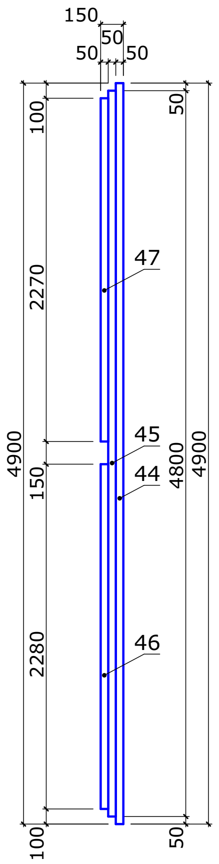

Изм..	Кол.уч.	Лист	№док.	Подп.	Дата
Разработал	*Саяпин П.*				
Утвердил	*Маркович П.В.*				

КД

ООО "Каркасники"

Проект "Палома"

Стадия	Лист	Листов
РП	9	53

Брус обвязки поз. 10-15.

dokadom.com

Копировал

ПЛАН ОБВЯЗОЧНОЙ ДОСКИ Б-1 . (низ отм. -0,250) М 1:50.

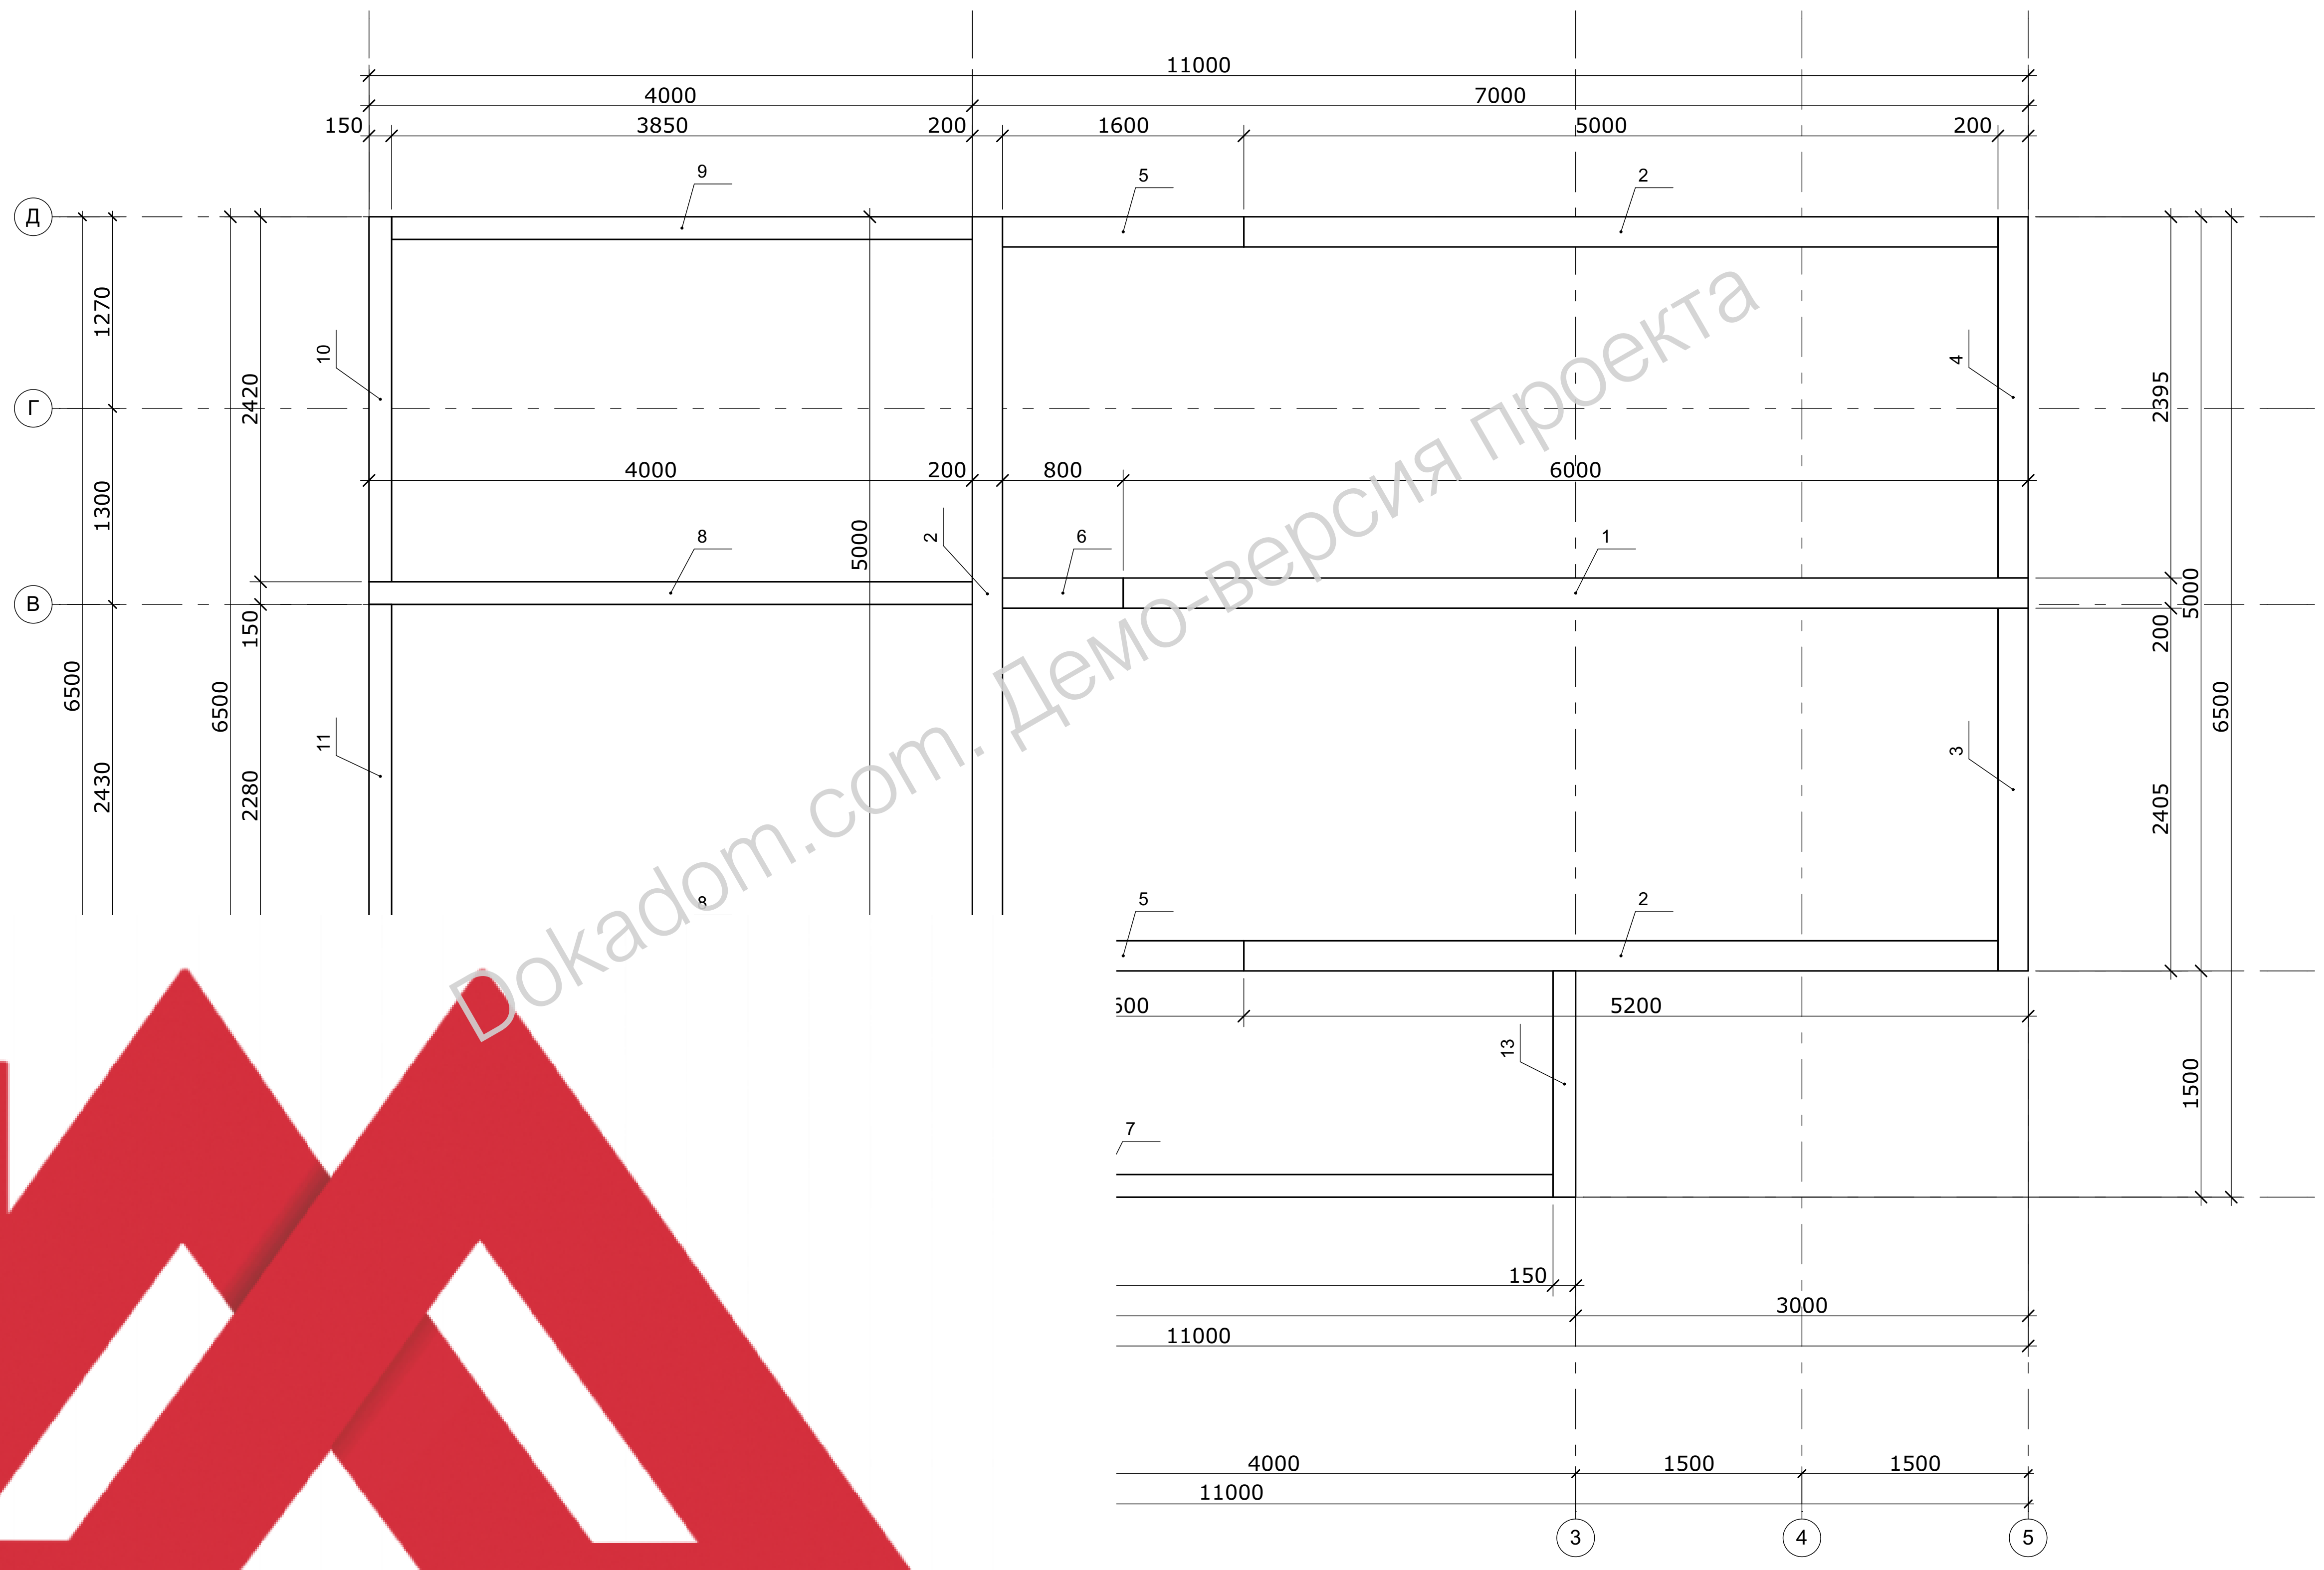

						КД		
						ООО "Каркасники"		
Изм..	Кол.уч.	Лист	№док.	Подп.	Дата			
Разработал	Саяпин П.					Проект "Палома"	Стадия	Лист	Листов
Утвердил	Маркович П.В.						РП	10	53
						План обвязочной доски Б-1. (низ отм. - 0,250) М 1:50.	dokadom.com		

Копировал

Спецификация к плану обвязочной доски Б-1.

Поз.	Сечениение	Наименование	Длина 1 поз.	Кол-во поз. шт.	Общий объем поз. м.3	Масса 1 поз. кг.	Примечание
1	п/м 50x200	доска обвязки	6000	1	0,060	42,00	
2	п/м 50x200	доска обвязки	5000	3	0,150	35,00	
3	п/м 50x200	доска обвязки	2405	1	0,024	16,84	
4	п/м 50x200	доска обвязки	2395	1	0,024	16,76	
5	п/м 50x200	доска обвязки	1600	2	0,032	11,20	
6	п/м 50x200	доска обвязки	800	1	0,008	5,60	
					0,298 м^3	208,60	
7	п/м 50x150	доска обвязки	6000	1	0,045	31,50	
8	п/м 50x150	доска обвязки	4000	2	0,060	21,00	
9	п/м 50x150	доска обвязки	3850	1	0,029	20,21	
10	п/м 50x150	доска обвязки	2420	1	0,018	12,70	
11	п/м 50x150	доска обвязки	2280	1	0,017	11,97	
12	п/м 50x150	доска обвязки	1700	1	0,013	8,92	
13	п/м 50x150	доска обвязки	1500	2	0,022	7,88	
					0,204 м^3	143,06	
		Общий расход древесины			0,502 м^3	351,66	

						КД
						ООО "Каркасники"
Изм..	Кол.уч.	Лист	№док.	Подп.	Дата	
Разработал	Саяпин П.					Проект "Палома"
Утвердил	Маркович П.В.					
						Спецификация к плану доски обвязки Б-1.

Стадия	Лист	Листов
РП	11	53

dokadom.com

Копировал

ПЛАН БАЛОК ПЕРЕКРЫТИЯ 1-ГО ЭТАЖА (низ отм. -0,200) М 1:50.

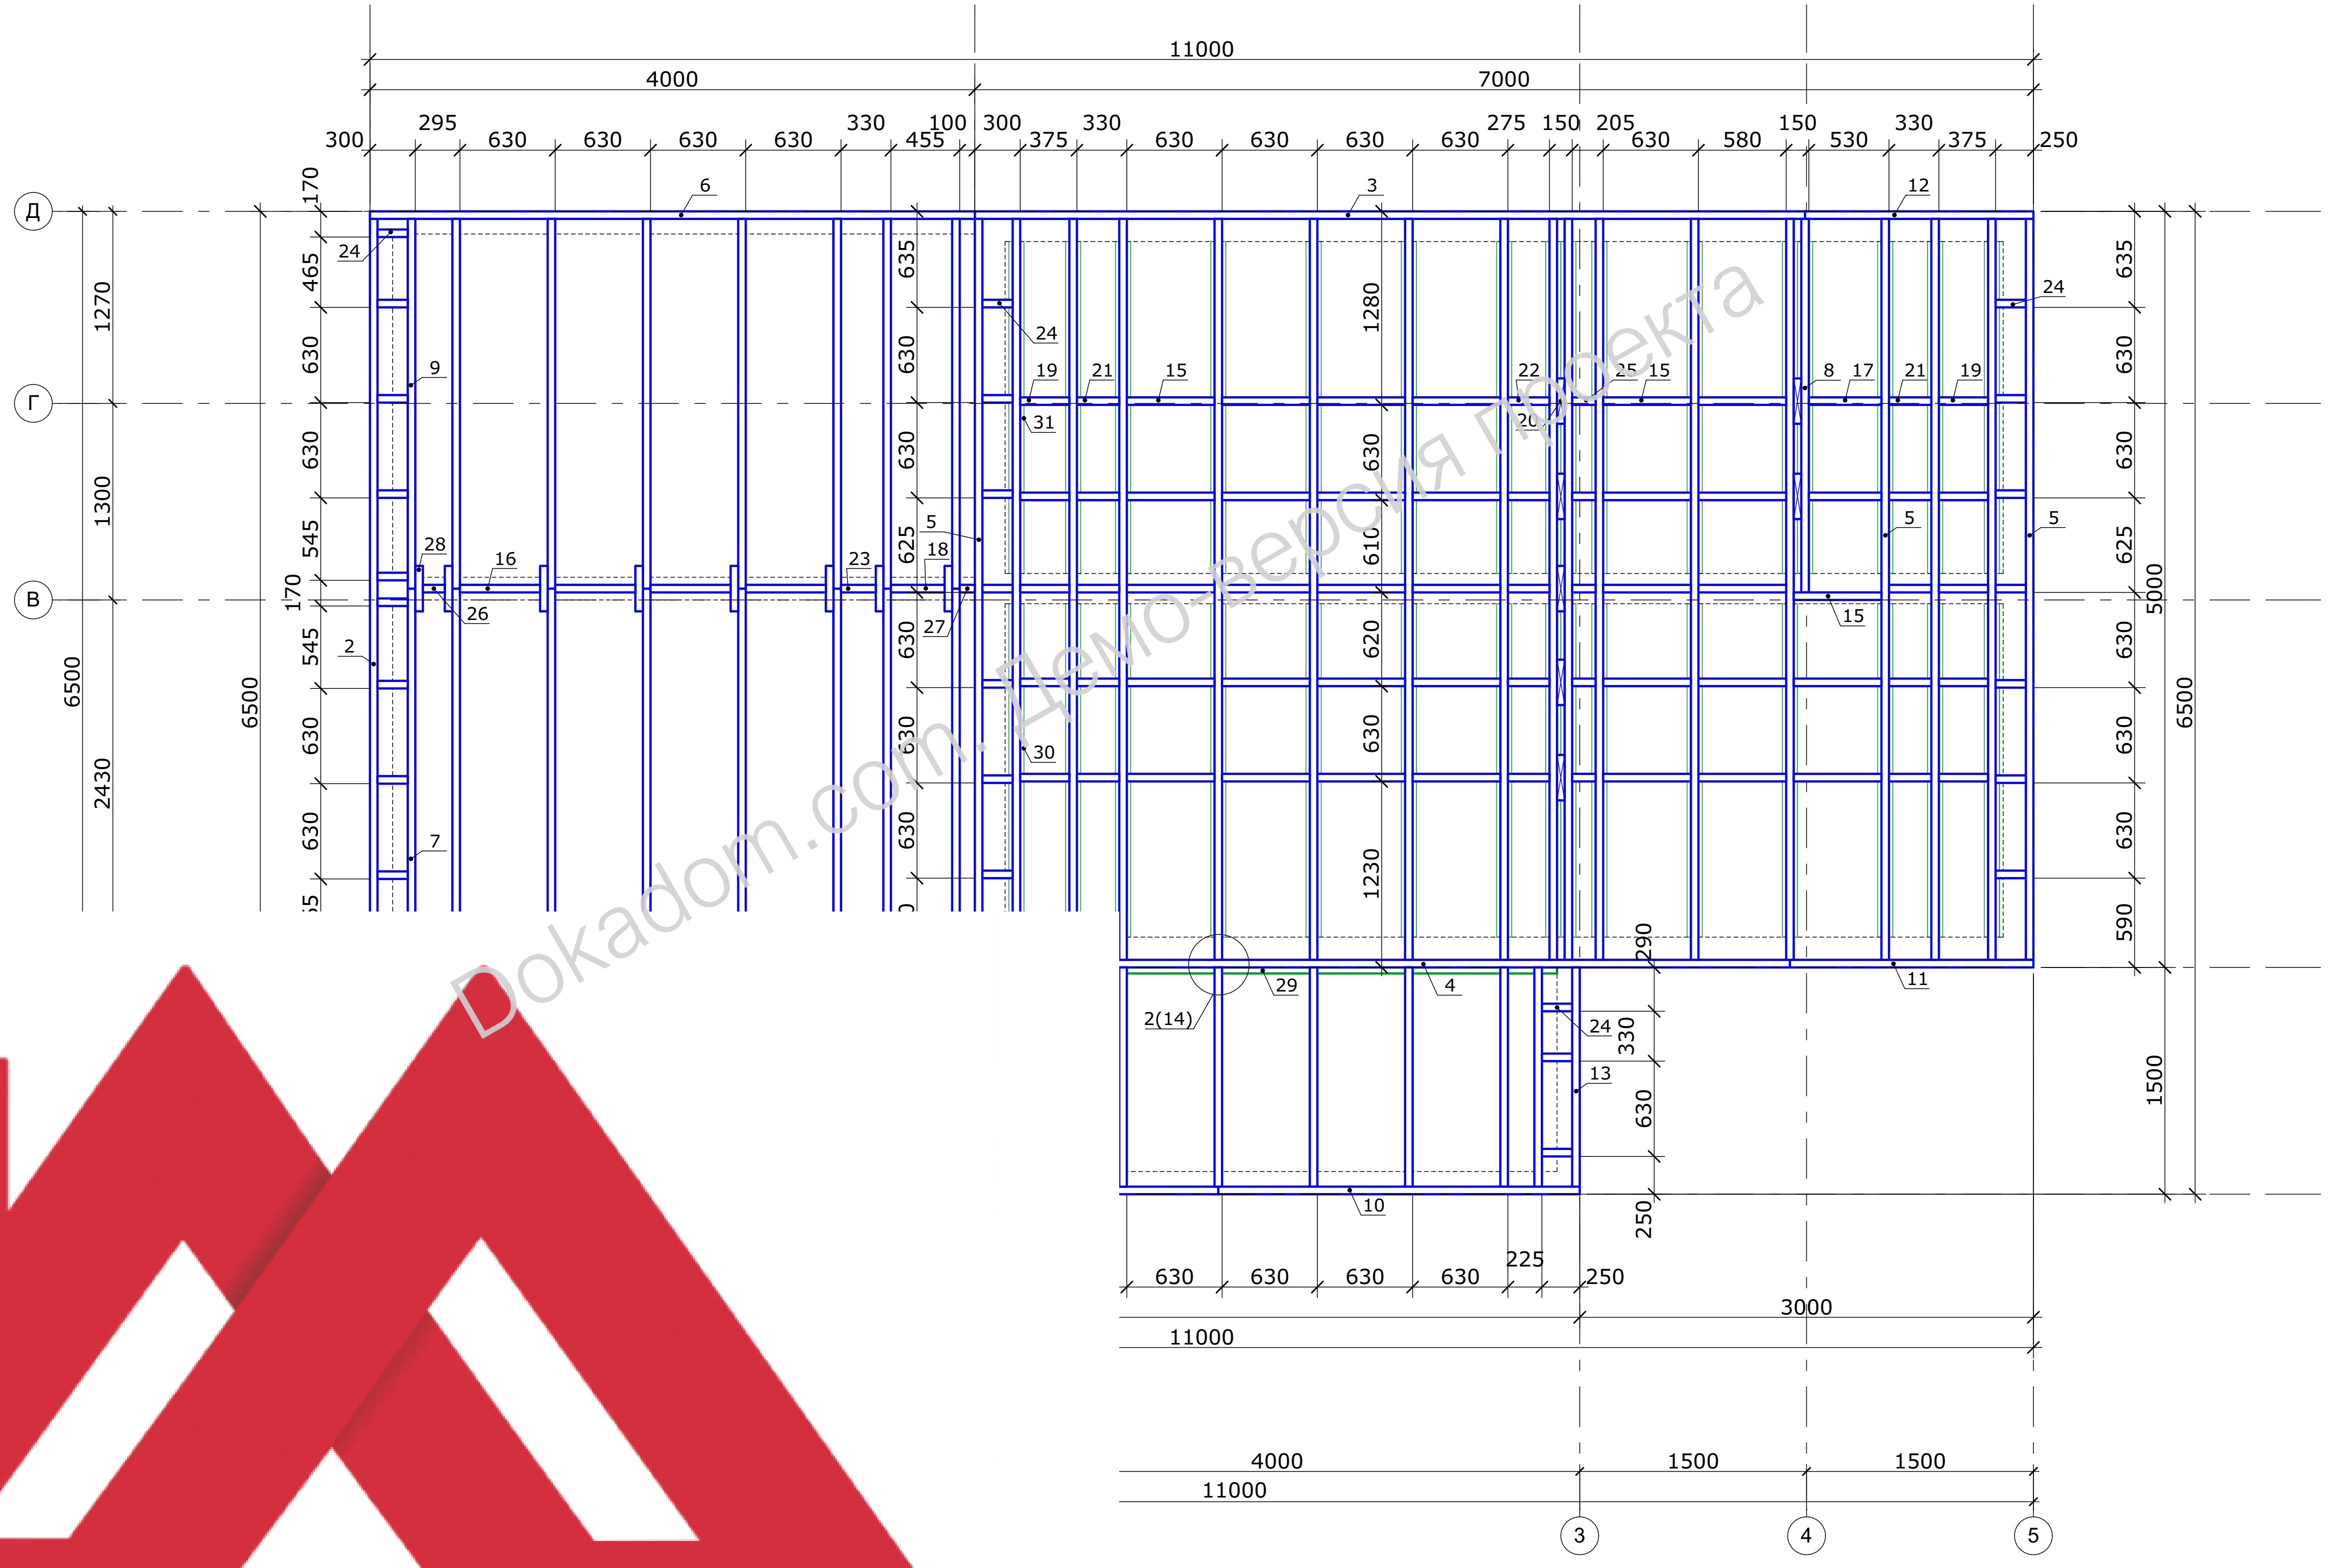

Изм..	Кол.уч.	Лист	№док.	Подп.	Дата
Разработал		*Саянин П.*			
Утвердил		*Маркович П.В.*			

КД

ООО "Каркасники"

Проект "Палома"

Стадия	Лист	Листов
РП	12	53

План балок перекрытия 1-го этажа (низ отм. -0,200). М 1:50.

dokadom.com

Копировал

Спецификация к плану балок 1-го этажа

Поз.	Сечение	Наименование	Длина 1 поз.	Кол-во поз. шт.Кол-во	Общий объем поз. м.3	Масса 1 поз. кг.	Примечание
1	п/м 50х200	балка перекрытия	5610	1	0,056	39,27	
2	п/м 50х200	балка перекрытия	5545	1	0,055	38,82	
3	п/м 50х200	балка перекрытия	5490	1	0,055	38,43	
4	п/м 50х200	балка перекрытия	5390	1	0,054	37,73	
5	п/м 50х200	балка перекрытия	4900	17	0,833	34,30	
6	п/м 50х200	балка перекрытия	4000	1	0,040	28,00	
7	п/м 50х200	балка перекрытия	3955	9	0,360	27,69	
8	п/м 50х200	балка перекрытия	2470	1	0,025	17,29	
9	п/м 50х200	балка перекрытия	2445	9	0,216	17,11	
10	п/м 50х200	балка перекрытия	2390	1	0,024	16,73	
11	п/м 50х200	балка перекрытия	1610	1	0,016	11,27	
12	п/м 50х200	балка перекрытия	1510	1	0,015	10,57	
13	п/м 50х200	балка перекрытия	1450	8	0,120	10,15	
14	п/м 50х200	балка перекрытия	855	1	0,009	5,98	
15	п/м 50х200	вставка	580	33	0,198	4,06	
16	п/м 50х200	вставка	530	4	0,020	3,71	
17	п/м 50х200	вставка	480	2	0,010	3,36	
18	п/м 50х200	вставка	355	1	0,004	2,48	

Поз.	Сечение	Наименование	Длина 1 поз.	Кол-во поз. шт.Кол-во	Общий объем поз. м.3	Масса 1 поз. кг.	Примечание
		Сетка для удержания утеплителя					
32		Сетка оцинкованная 2х2мм.	38,50	м²			
		Чистый пол					
33		Доска шпунтованная, толщ. 36мм	29,48	м²			
		Покрытие открытых пространств					
34		Доска террасная	32	м²			

1. При установке и монтаже балок перекрытия пола необходимо руководствоваться требованиями СП 31-105-202 "Проектирование и строительство энергоэффективных одноквартирных жилых домов с деревянным каркасом" п.. 6 Перекрытия и СНиП 31-02.
2. Все металлические элементы крепить к деревянным при помощи саморезов по дереву длинной в зависимости от толщин соединяемых элементов.
3. Балки перекрытия составного сечения (спаренных балки) сбивать между собой гвоздями в соответствии с требованиями п.. 6.2.6.1, 6.2.6.2 и 6.2.6.3 СП 31-105-2002.
4. Гвоздевые соединения элементов каркаса перекрытий должны осуществляться в соответствии с таблицей 6-1 (п.. 6.2.12.1) СП 31-105-2002.

КД

ООО "Каркасники"

Изм..	Кол.уч.	Лист	№док.	Подп.	Дата
Разработал		Саяпин П.			
Утвердил		Маркович П.В.			

Проект "Палома"

Стадия	Лист	Листов
РП	13	53

Спецификация к плану балок перекрытия 1-го этажа.

dokadom.com

Копировал

УЗЕЛ КРЕПЛЕНИЯ БАЛОК НА ОПОРНОЙ ДОСКЕ

2

12

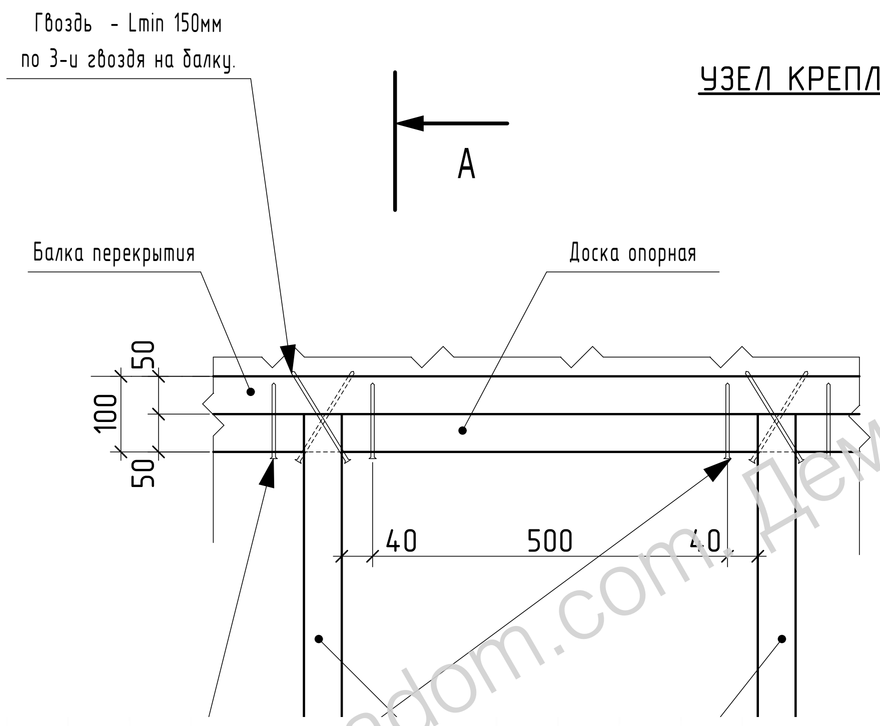

А-А

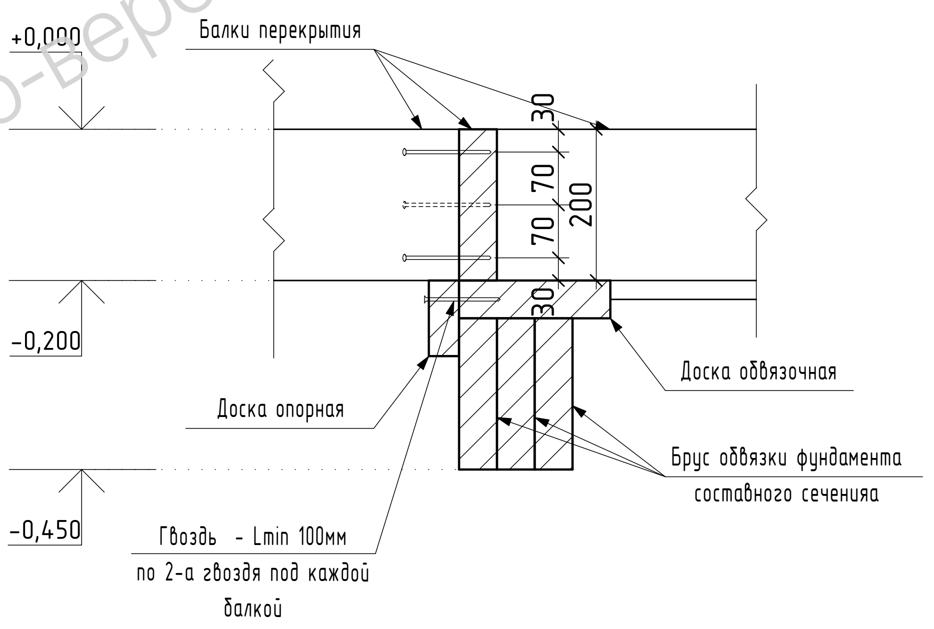

Изм..	Кол.уч.	Лист	№док.	Подп.	Дата
Разработал		Саяпин П.			
Утвердил		Маркович П.В.			

КД

ООО "Каркасники"

Проект "Палома"

Стадия	Лист	Листов
РП	14	53

Узел 2.

dokadom.com

Копировал

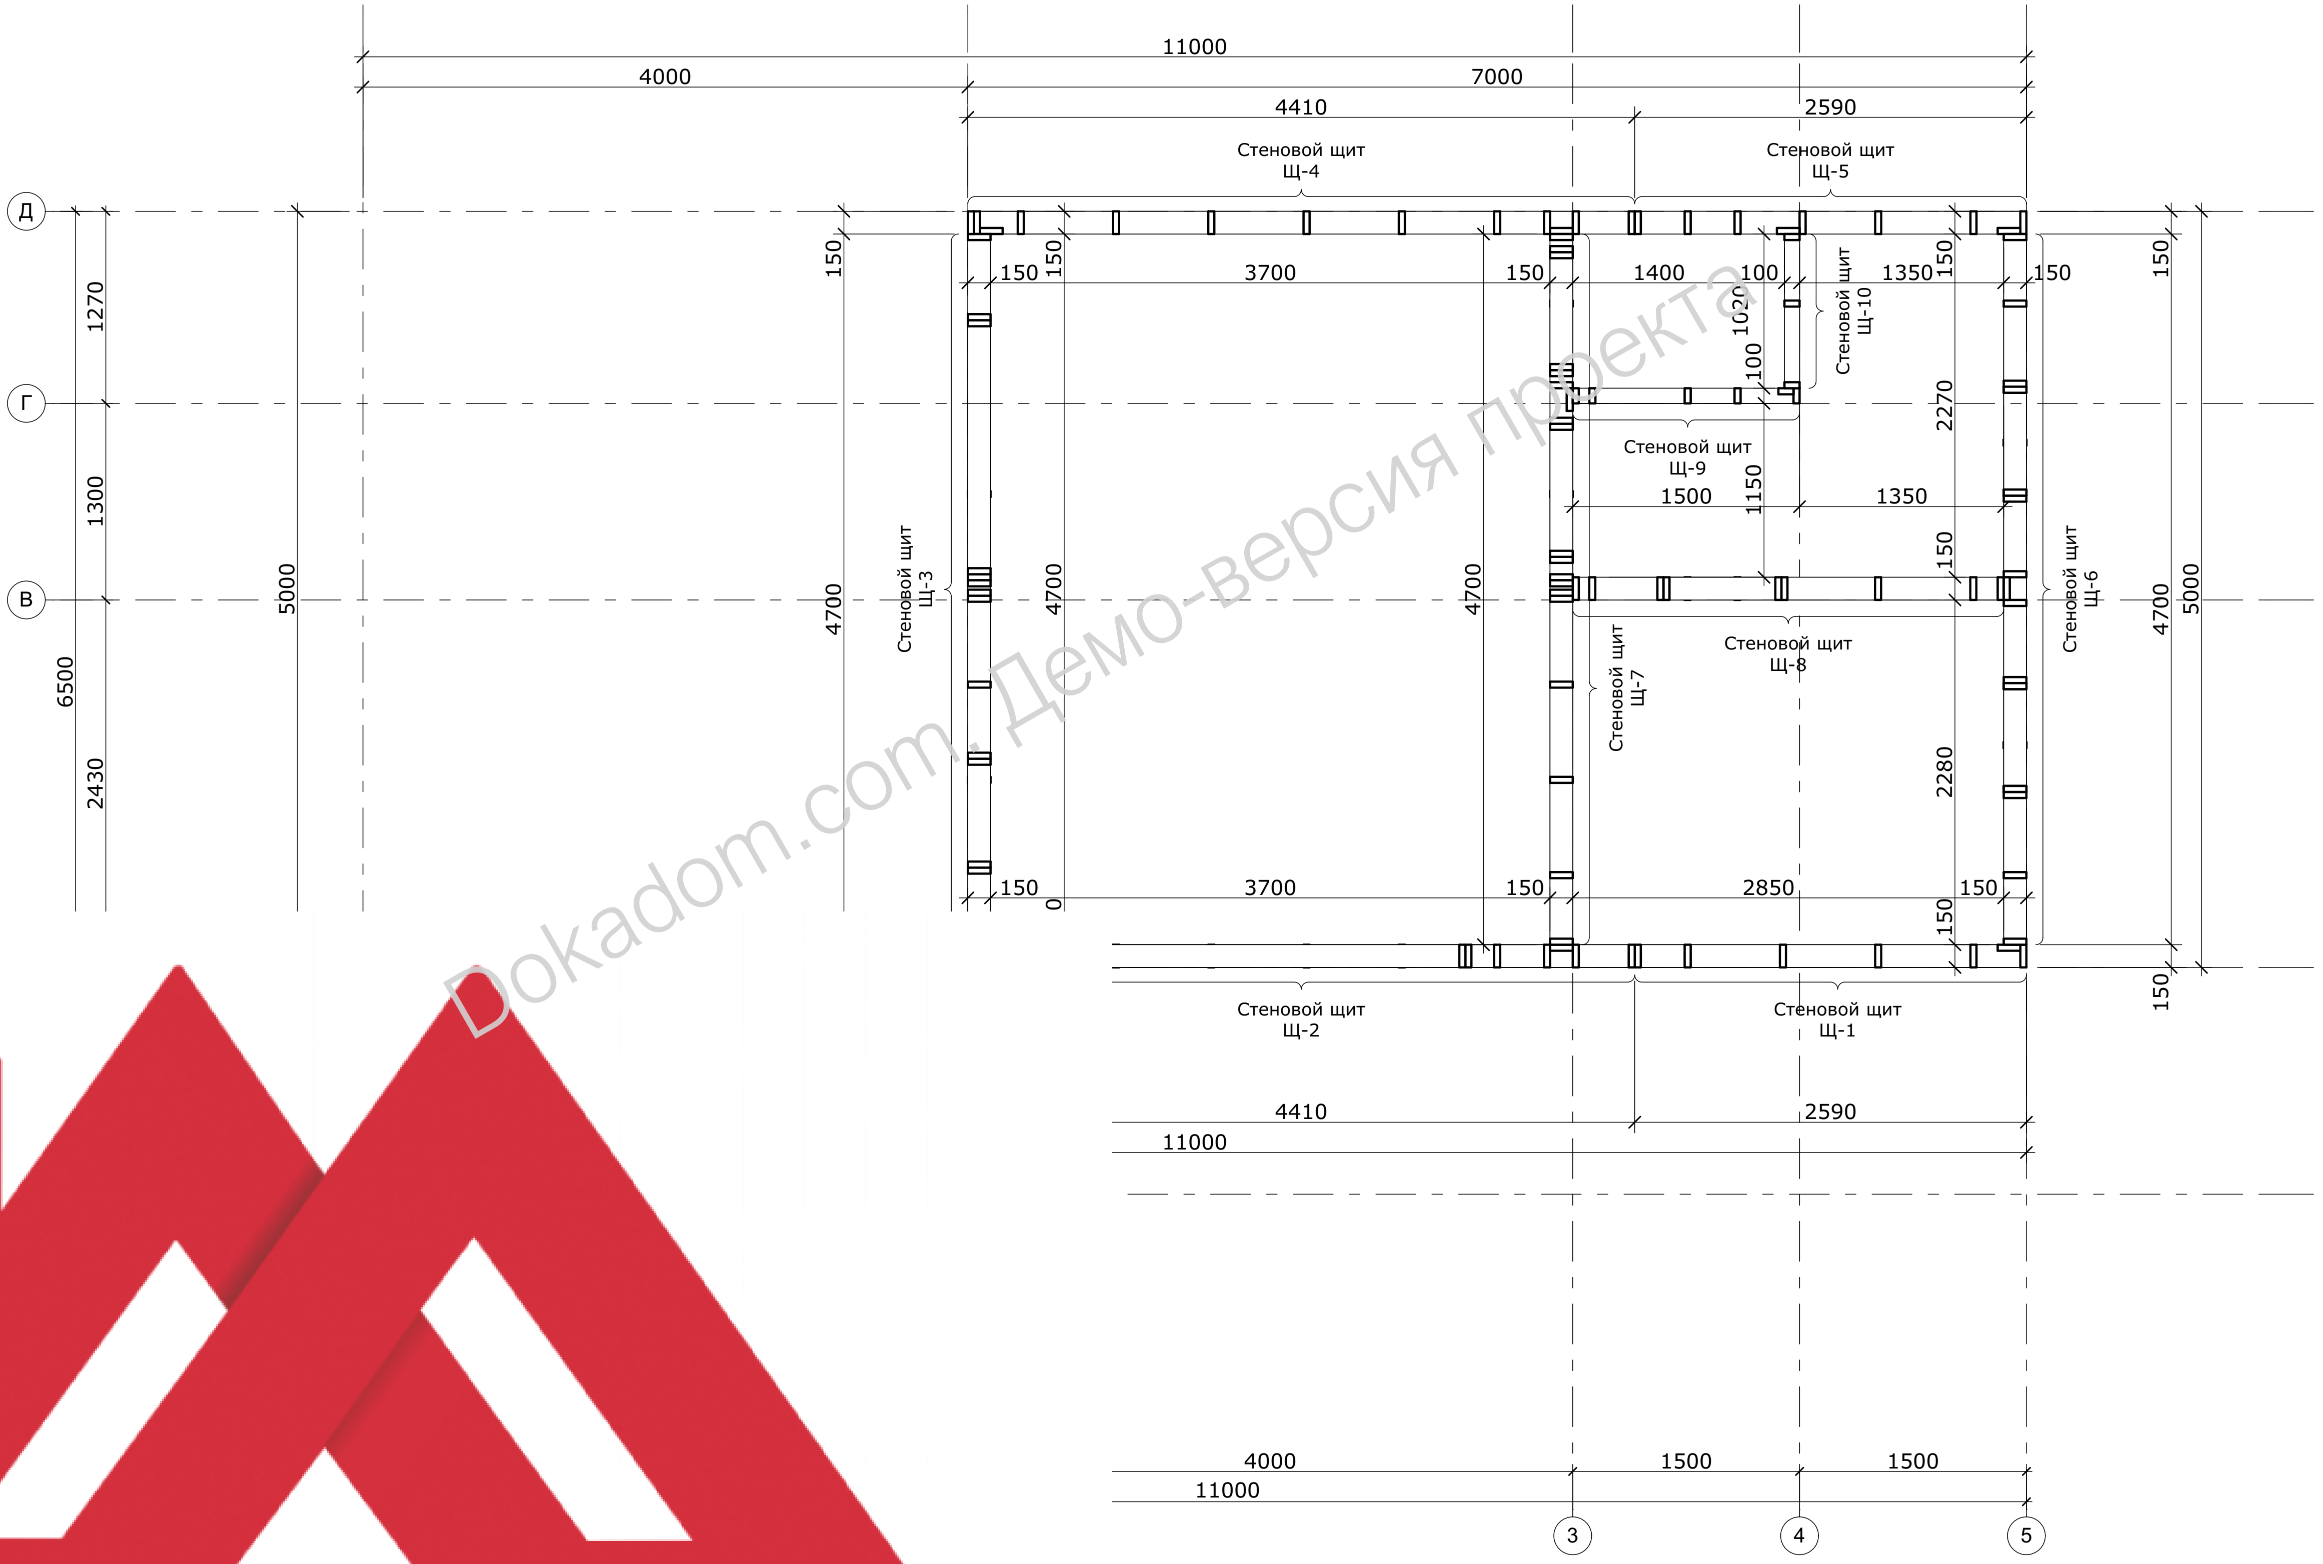

Изм..	Кол.уч.	Лист	№док.	Подп.	Дата
Разработал	Саяпин П.				
Утвердил	Маркович П.В.				

КД

ООО "Каркасники"

Проект "Палома"

Стадия	Лист	Листов
РП	15	53

Схема стеновых щитов 1-го этажа. М 1:50.

dokadom.com

Копировал

Стеновой щит Щ-1

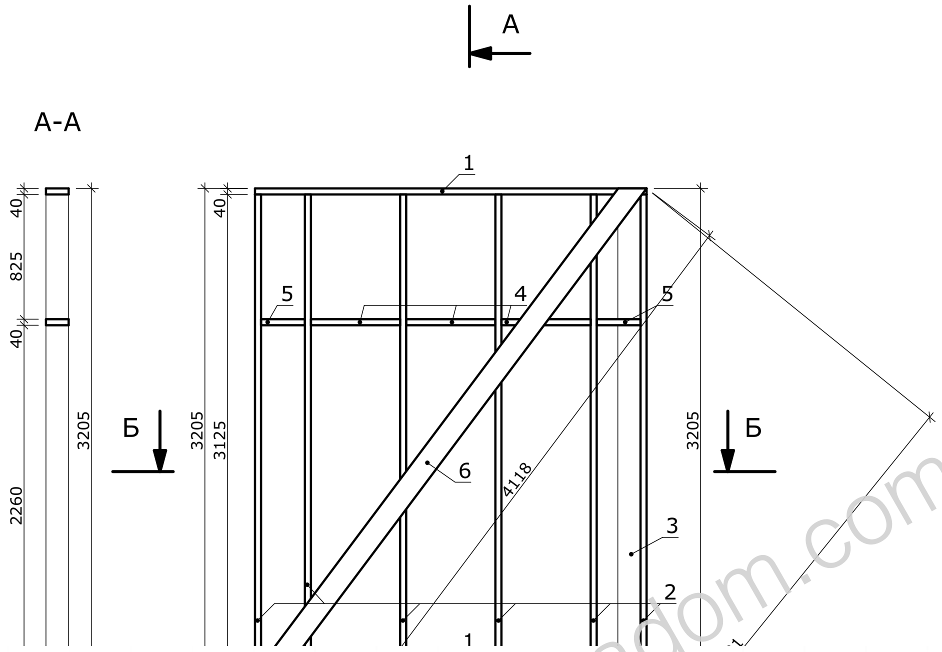

Спецификация элементов щита Щ-1							
Поз.	Сечениение	Наименование	Длина 1 поз.	Кол-во поз. шт.	Общий объем поз. м.3	Масса 1 поз. кг.	Примечание
1	п/м 40х150	лежень	2590	2	0,032	10,88	
2	п/м 40х150	стойка	3125	6	0,114	13,12	
3	п/м 40х150	стойка торцевая	3125	1	0,019	13,12	
4	п/м 40х150	вставка	590	3	0,012	2,48	
5	п/м 40х150	вставка	290	2	0,004	1,22	
					0,181 м^3	123,50	
6	п/м 25х150	укосина	4118	1	0,015	10,81	
					0,015 м^3	10,81	
		Общий расход древесины всех сечений			0,196 м^3	134,31	

Изм..	Кол.уч.	Лист	№док.	Подп.	Дата
Разработал		Саяпин П.			
Утвердил		Маркович П.В.			

КД

ООО "Каркасники"

Проект "Палома"

Стадия	Лист	Листов
РП	16	53

Стеновой щит Щ-1. Спецификация элементов щита.

dokadom.com

Копировал

Стеновой щит Щ-2

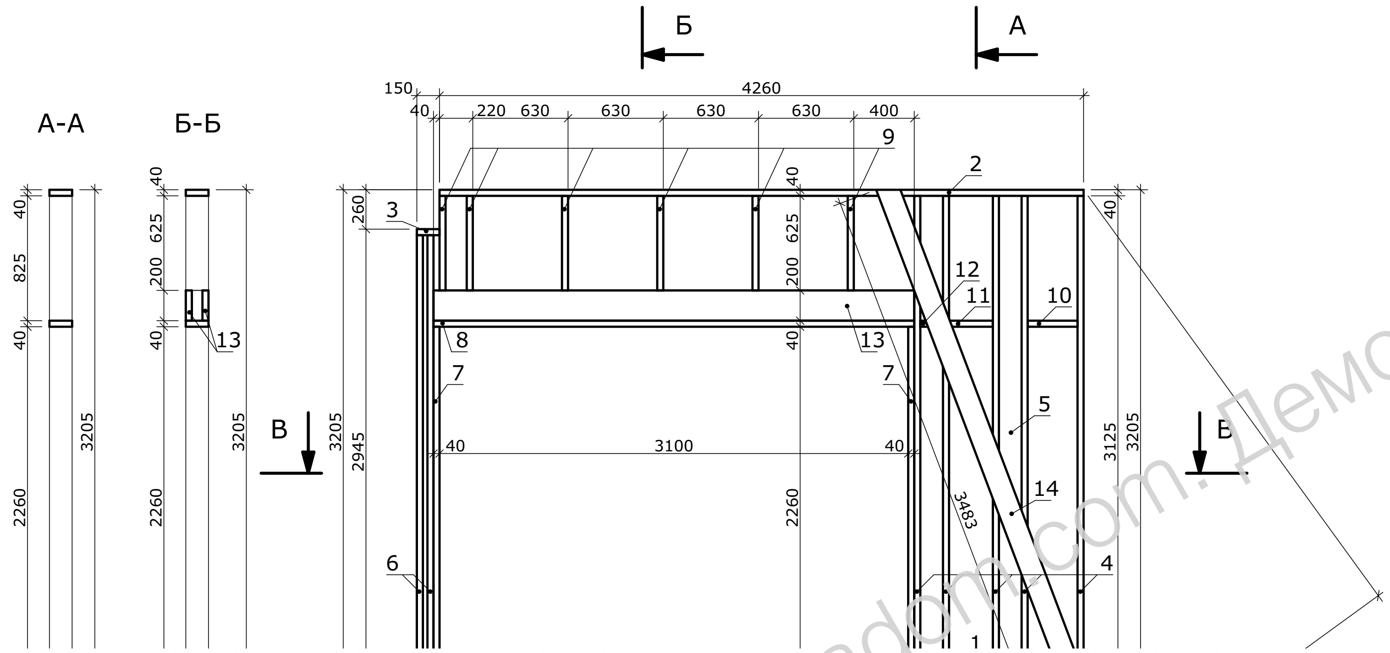

Спецификация элементов щита Щ-2							
Поз.	Сечениение	Наименование	Длина 1 поз.	Кол-во поз. шт.	Общий объем поз. м.3	Масса 1 поз. кг.	Примечание
1	п/м 40х150	лежень	4410	1	0,026	18,52	
2	п/м 40х150	лежень	4260	1	0,026	17,89	
3	п/м 40х150	лежень	150	1	0,001	0,63	
4	п/м 40х150	стойка	3125	5	0,095	13,12	
5	п/м 40х150	стойка торцевая	3125	1	0,019	13,12	
6	п/м 40х150	стойка опорная	2865	2	0,034	12,03	
7	п/м 40х150	накладка	2260	2	0,028	9,49	
8	п/м 40х150	обвязка проема	3180	1	0,019	13,36	
9	п/м 40х150	вставка	625	6	0,024	2,62	
10	п/м 40х150	вставка	330	1	0,002	1,39	
11	п/м 40х150	вставка	290	1	0,002	1,22	
12	п/м 40х150	вставка	150	1	0,001	0,63	
13	п/м 50х200	ригель проема	3180	2	0,064	22,26	
					0,341 м^3	235,70	
14	п/м 25х150	укосина	3483	1	0,013	9,14	
					0,013 м^3	9,14	
		Общий расход древесины всех сечений			0,354 м^3	244,85	

						КД			
Изм..	Кол.уч.	Лист	№док.	Подп.	Дата	ООО "Каркасники"			
Разработал	Саяпин П.					Проект "Палома"	Стадия	Лист	Листов
Утвердил	Маркович П.В.						РП	17	53
						Стеновой щит Щ-2. Спецификация элементов щита.	dokadom.com		

Копировал

Стеновой щит Щ-3

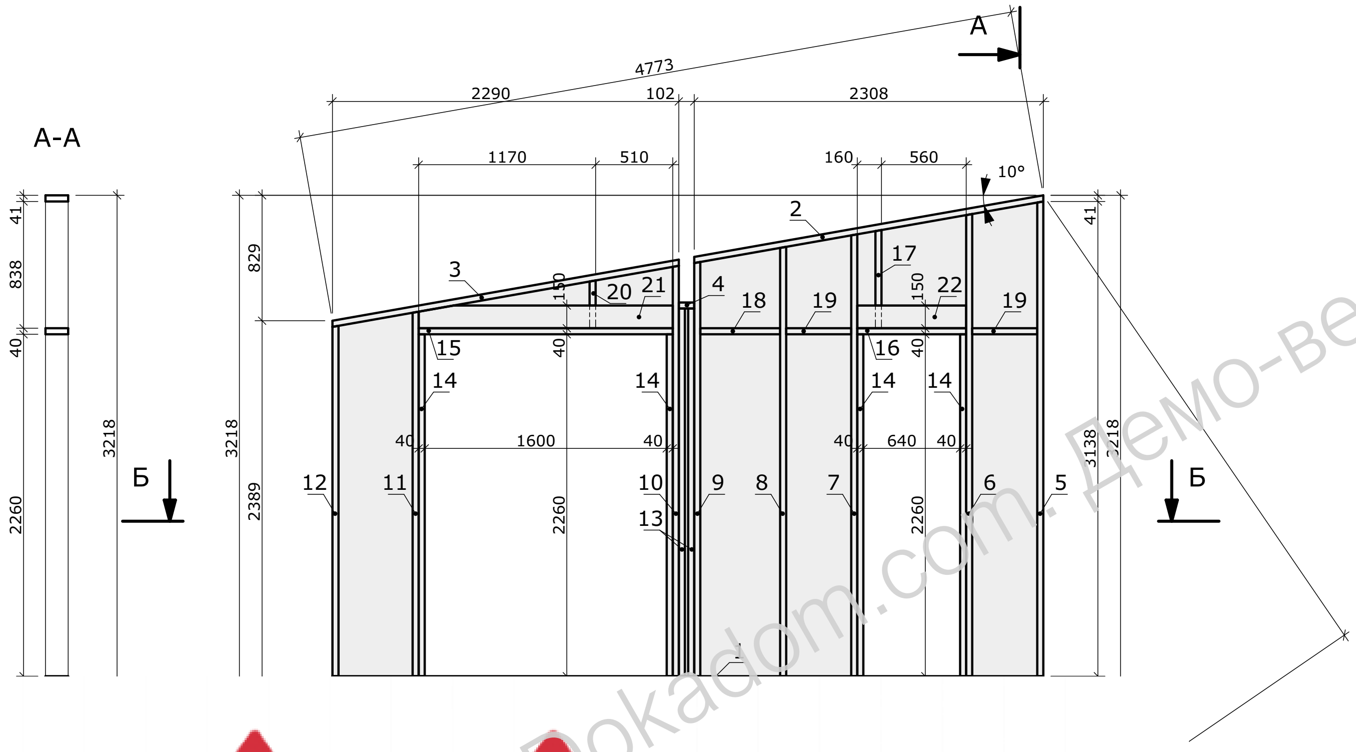

Спецификация элементов щита Щ-3

Поз.	Сечениение	Наименование	Длина 1 поз.	Кол-во поз. шт.	Общий объем поз. м.3	Масса 1 поз. кг.	Примечание
1	п/м 40x150	лежень	4700	1	0,028	19,74	
2	п/м 40x150	лежень	2351	1	0,014	9,87	
3	п/м 40x150	лежень	2332	1	0,014	9,80	
4	п/м 40x150	лежень	102	1	0,001	0,43	
5	п/м 40x150	стойка	3138	1	0,019	13,18	
6	п/м 40x150	стойка	3055	1	0,018	12,83	
7	п/м 40x150	стойка	2921	1	0,018	12,27	
8	п/м 40x150	стойка	2838	1	0,017	11,92	
9	п/м 40x150	стойка	2738	1	0,016	11,50	
10	п/м 40x150	стойка	2713	1	0,016	11,39	
11	п/м 40x150	стойка	2409	1	0,014	10,12	
12	п/м 40x150	стойка	2316	1	0,014	9,73	
13	п/м 40x150	стойка опорная	2430	2	0,030	10,21	
14	п/м 40x150	накладка	2260	4	0,056	9,49	
15	п/м 40x150	обвязка проема	1680	1	0,010	7,06	
16	п/м 40x150	обвязка проема	720	1	0,004	3,02	
17	п/м 40x150	вставка	649	1	0,004	2,73	
18	п/м 40x150	вставка	528	1	0,003	2,22	
19	п/м 40x150	вставка	430	2	0,006	1,81	
20	п/м 40x150	вставка	316	1	0,002	1,33	
21	п/м 40x150	ригель проема	1680	1	0,010	7,06	
22	п/м 40x150	ригель проема	720	1	0,004	3,02	
		Общий расход древесины			0,318 м^3	221,19	

	Общие данные					
	Площадь обшивки панели жестким плитным материалом толщ. мин. 9мм.	8,00 м²				

Изм..	Кол.уч.	Лист	№док.	Подп.	Дата
Разработал		Саяпин П.			
Утвердил		Маркович П.В.			

КД

ООО "Каркасники"

Проект "Палома"

Стадия	Лист	Листов
РП	18	53

Стеновой щит Щ-3. Спецификация элементов щита.

dokadom.com

Копировал

Стеновой щит Ш-4

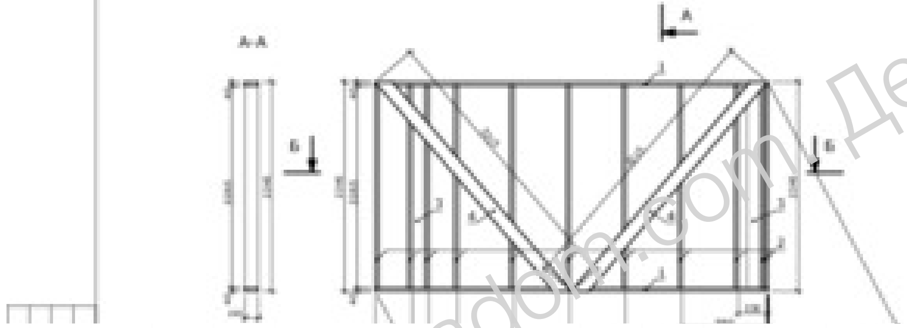

Спецификация элементов щита Ш-4							
Поз.	Сечение	Наименование	Длина 1 поз.	Кол-во поз. шт.	Общий объем поз. м3	Масса 1 поз. кг	Примечание
1	[illegible] 40х150	обвязка	4410	2	0,052	18,52	
2	[illegible] 40х150	стойки	2265	11	0,154	9,51	
3	[illegible] 40х150	стойки торцевые	2265	2	0,028	9,51	
					0,234м³	160,71	
4	[illegible] 25х150	раскосы	3215	2	0,024	8,44	
					0,024м³	16,88	
		Общий расход древесины всех сечений			0,258м³	177,59	

						КД			
Изм.	Кол.уч.	Лист	№док.	Подп.	Дата	ООО "Каркасники"			
Разработал		Самин П.				Проект "Паломa"	Стадия	Лист	Листов
Утвердил		Миронов Л.В.					РП	19	53
						Стеновой щит Ш-4. Спецификация элементов щита.	dokadom.com		

Копировал

Стеновой щит Ш-5

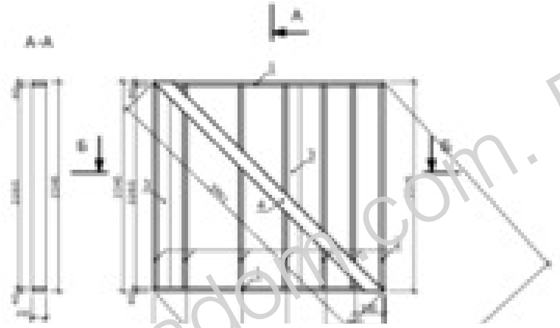

Спецификация элементов щита Ш-5							
Поз.	Сечение	Наименование	Длина 1 поз.	Кол-во поз. шт	Общий объем поз. м3	Масса 1 поз. кг	Примечание
1	п/м 40х150	обвязка	2500	2	0,032	10,69	
2	п/м 40х150	стойка	2265	7	0,098	9,61	
3	п/м 40х150	стойка торцевая	2265	2	0,028	9,61	
					0,158 м³	107,37	
4	п/м 25х150	укосина	3491	1	0,013	9,16	
					0,013 м³	9,16	
		Общий расход древесины всех сечений			0,171 м³	116,54	

						КД
						ООО "Каркасники"
Изм.	Кол.уч.	Лист	№док.	Подп.	Дата	
Разработал	Санько П.					Проект "Палома"
Утвердил	Миронюк П.В.					

Стадия	Лист	Листов
РП	20	53

Стеновой щит Ш-5. Спецификация элементов щита.

dokadom.com

Копировал

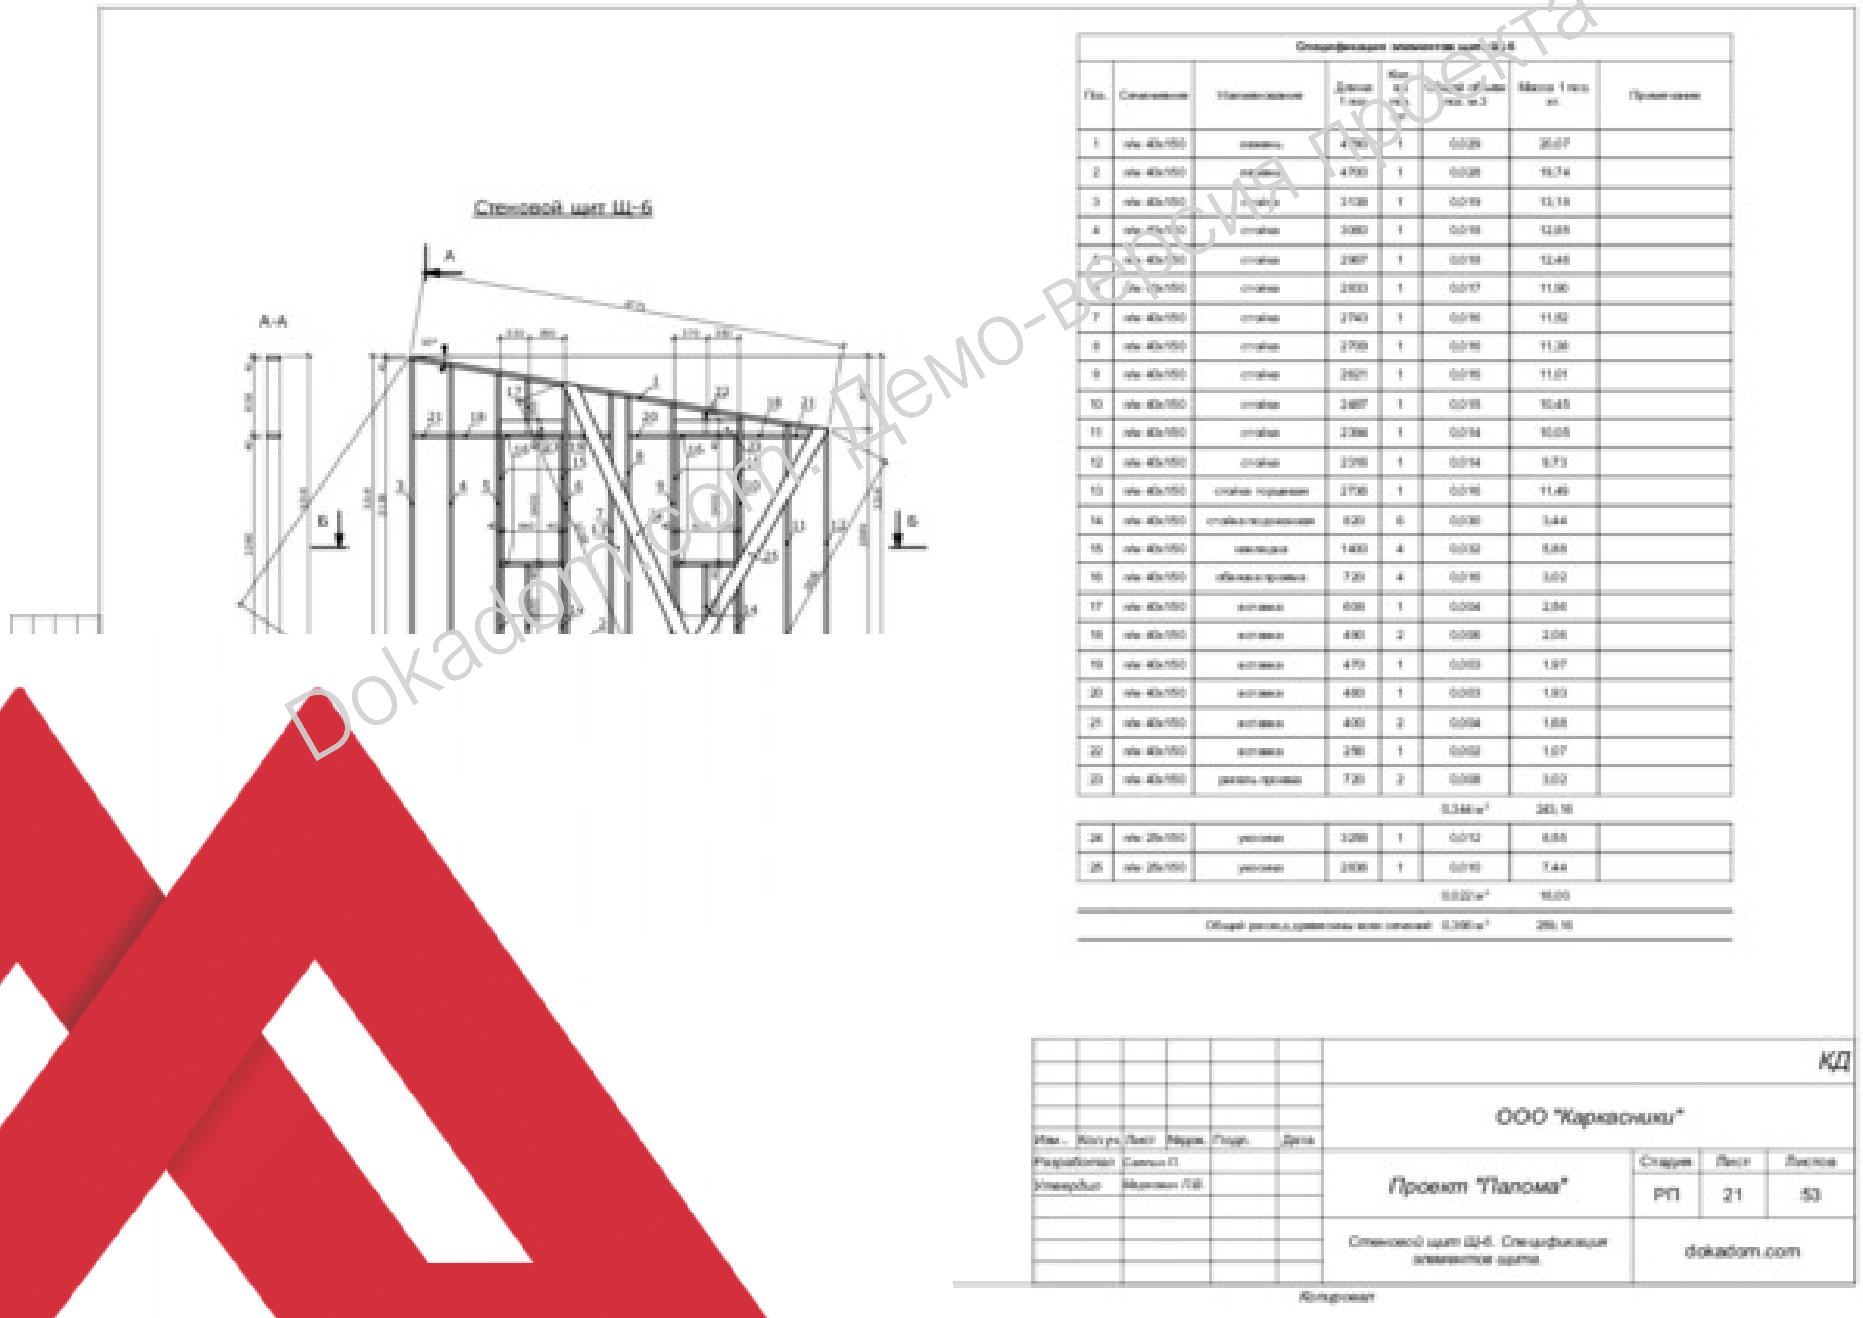

Стеновой щит Ш-6

КД

ООО "Каркасники"

Изм.	Кол.уч.	Лист	№док.	Подп.	Дата
Разработал		Савчук П.			
Утвердил		Марченко Л.В.			

Проект "Палома"

Стадия	Лист	Листов
РП	21	53

Стеновой щит Ш-6. Спецификация элементов щита.

dokadom.com

Копировал

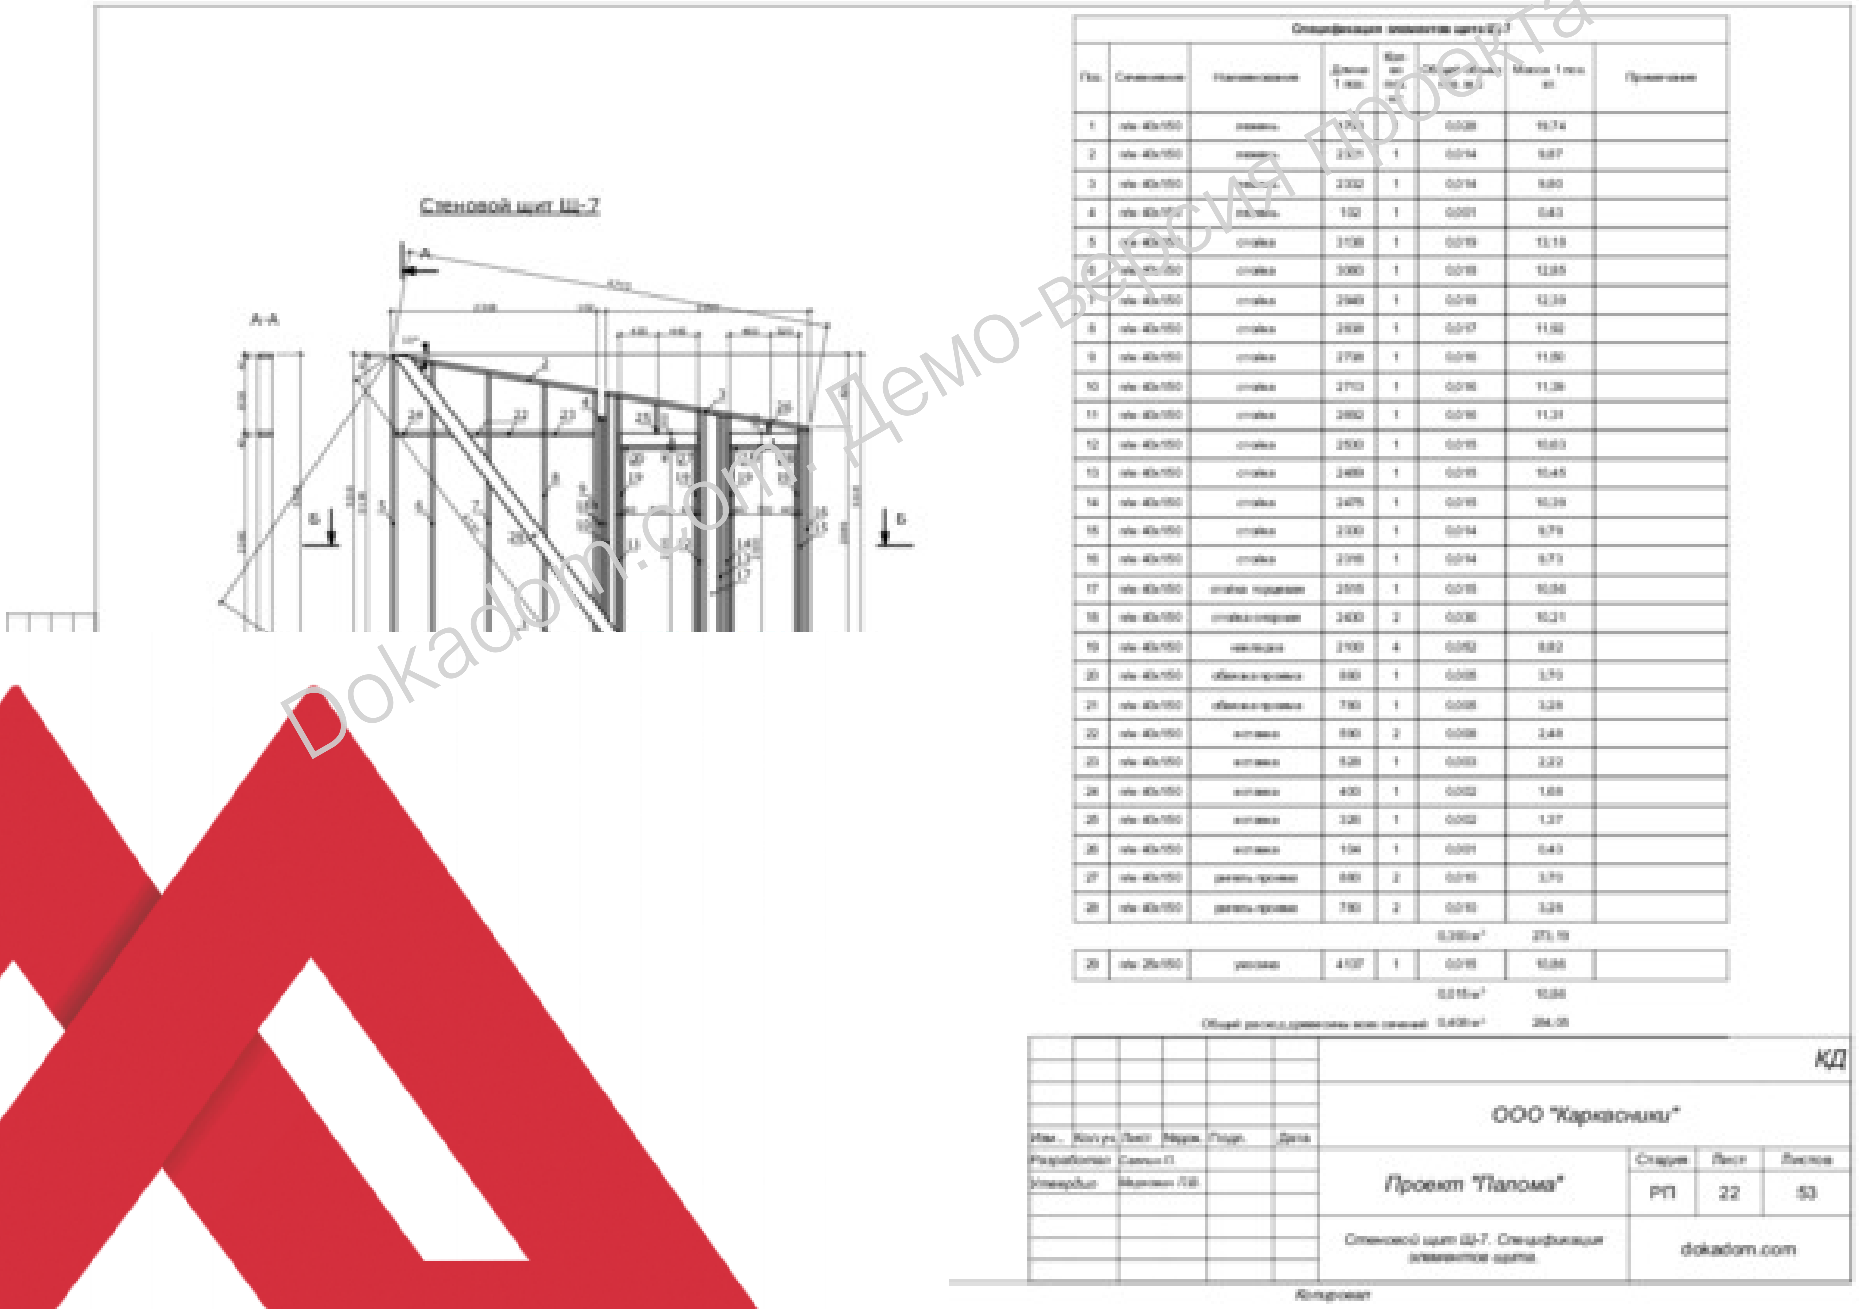

Спецификация элементов щита Ш-7							
Поз.	Сечение	Наименование	Длина 1 поз.	Кол-во, шт.	Общий объем, м³	Масса 1 поз. кг	Примечание
1	доска 40х150	обвязка	[illegible]	1	0,028	19,74	
2	доска 40х150	обвязка	[illegible]	1	0,014	9,87	
3	доска 40х150	обвязка	2332	1	0,014	9,80	
4	доска 40х150	обвязка	102	1	0,001	0,43	
5	доска 40х150	стойка	3138	1	0,019	13,18	
6	доска 40х150	стойка	3060	1	0,018	12,85	
7	доска 40х150	стойка	2948	1	0,018	12,39	
8	доска 40х150	стойка	2808	1	0,017	11,82	
9	доска 40х150	стойка	2738	1	0,016	11,50	
10	доска 40х150	стойка	2713	1	0,016	11,39	
11	доска 40х150	стойка	2692	1	0,016	11,31	
12	доска 40х150	стойка	2530	1	0,015	10,63	
13	доска 40х150	стойка	2489	1	0,015	10,45	
14	доска 40х150	стойка	2475	1	0,015	10,39	
15	доска 40х150	стойка	2330	1	0,014	9,79	
16	доска 40х150	стойка	2316	1	0,014	9,73	
17	доска 40х150	стойка торцевая	2515	1	0,015	10,56	
18	доска 40х150	стойка опорная	2430	2	0,030	10,21	
19	доска 40х150	накладка	2100	4	0,050	8,82	
20	доска 40х150	обвязка проема	880	1	0,005	3,70	
21	доска 40х150	обвязка проема	780	1	0,005	3,28	
22	доска 40х150	вставка	590	2	0,007	2,48	
23	доска 40х150	вставка	528	1	0,003	2,22	
24	доска 40х150	вставка	400	1	0,002	1,68	
25	доска 40х150	вставка	326	1	0,002	1,37	
26	доска 40х150	вставка	104	1	0,001	0,43	
27	доска 40х150	ригель проема	880	2	0,010	3,70	
28	доска 40х150	ригель проема	780	2	0,010	3,28	
					0,390 м³	273,19	
29	доска 25х150	раскос	4107	1	0,015	10,86	
					0,015 м³	10,86	
		Общий расход древесины всех сечений:			0,405 м³	284,05	

КД

ООО "Каркасники"

Изм.	Кол.уч.	Лист	№док.	Подп.	Дата
Разработал	[illegible]				
Утвердил	[illegible]				

Проект "Палома"

Стадия	Лист	Листов
РП	22	53

Стеновой щит Ш-7. Спецификация элементов щита.

dokadom.com

Копировал

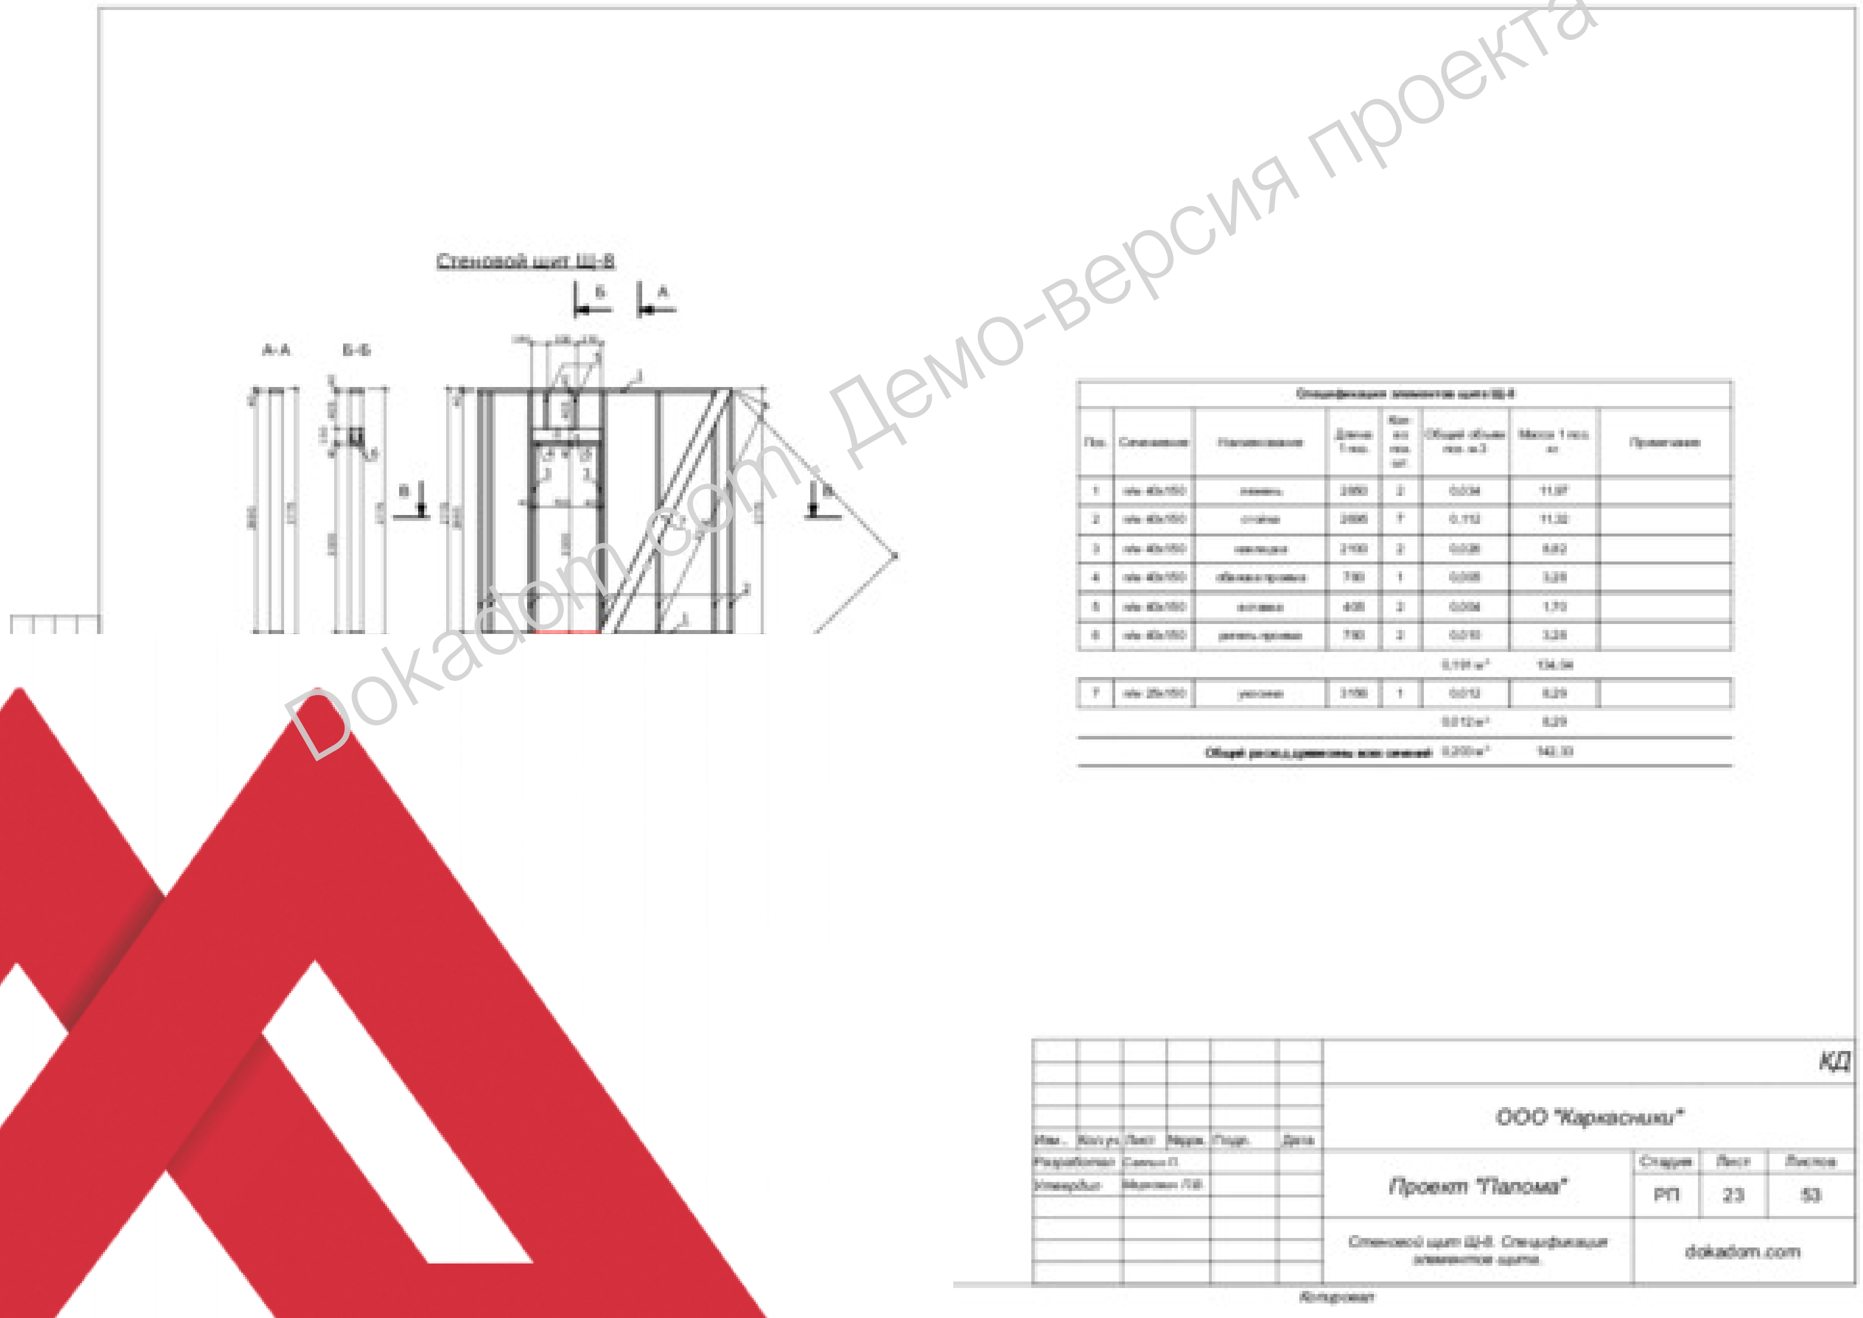

Стеновой щит Щ-8

Спецификация элементов щита Щ-8

КД

ООО "Каркасники"

Проект "Палома"

Стадия	Лист	Листов
РП	23	53

Стеновой щит Щ-8. Спецификация элементов щита.

dokadom.com

Копировал

Стеновой щит Ш-9

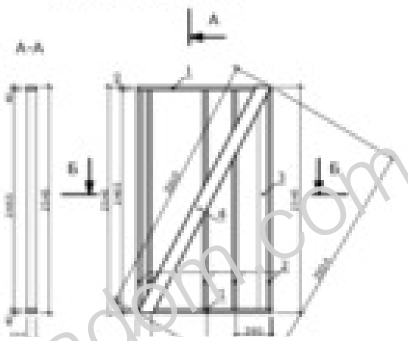

Спецификация элементов щита Ш-09

Поз.	Сечениние	Наименование	Длина 1 поз.	Кол-во поз. шт.	Общий объем поз. м3	Масса 1 поз. кг	Примечание
1	п/м 40х100	лежень	1500	2	0,012	4,20	
2	п/м 40х100	стойка	2465	5	0,050	6,90	
3	п/м 40х100	стойка торцевая	2465	1	0,010	6,90	
					0,072 м³	48,01	
4	п/м 25х150	укосина	2950	1	0,011	7,74	
					0,011 м³	7,74	
		Общий расход древесины всех сечений			0,083 м³	57,56	

Изм.	Кол.уч.	Лист	№док.	Подп.		Дата
Разработал		Савин П.				
Утвердил		Мирошин Л.В.				

КД

ООО "Каркасники"

Проект "Паломa"

Стадия	Лист	Листов
РП	24	53

Стеновой щит Ш-9. Спецификация элементов щита.

dokadom.com

Копировал

Стеновой щит Ш-10

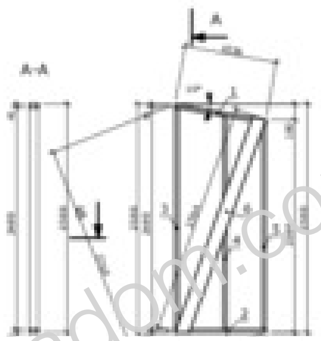

Спецификация элементов щита Ш-10							
Поз.	Сечение	Наименование	Длина 1 поз.	Кол-во поз. шт.	Общий объем поз. м.3	Масса 1 поз. кг.	Примечание
1	[illegible] 40х100	обвязка	1040	1	0,004	2,92	
2	[illegible] 40х100	обвязка	1020	1	0,004	2,86	
3	[illegible] 40х100	стойка	2489	1	0,010	6,97	
4	[illegible] 40х100	стойка	2394	1	0,010	6,70	
5	[illegible] 40х100	стойка	2316	1	0,009	6,48	
					0,037м³	25,93	
6	[illegible] 25х150	раскос	2594	1	0,010	6,81	
					0,010м³	6,81	
	Общий расход древесины всех сечений:				0,047м³	32,74	

						КД			
Изм.	Кол.уч.	Лист	№док.	Подп.	Дата	ООО "Каркасники"			
Разработал		Савчук П.				Проект "Палома"	Стадия	Лист	Листов
Утвердил		Миронов П.В.					РП	25	53
						Стеновой щит Ш-10. Спецификация элементов щита.	dokadom.com		

Копировал

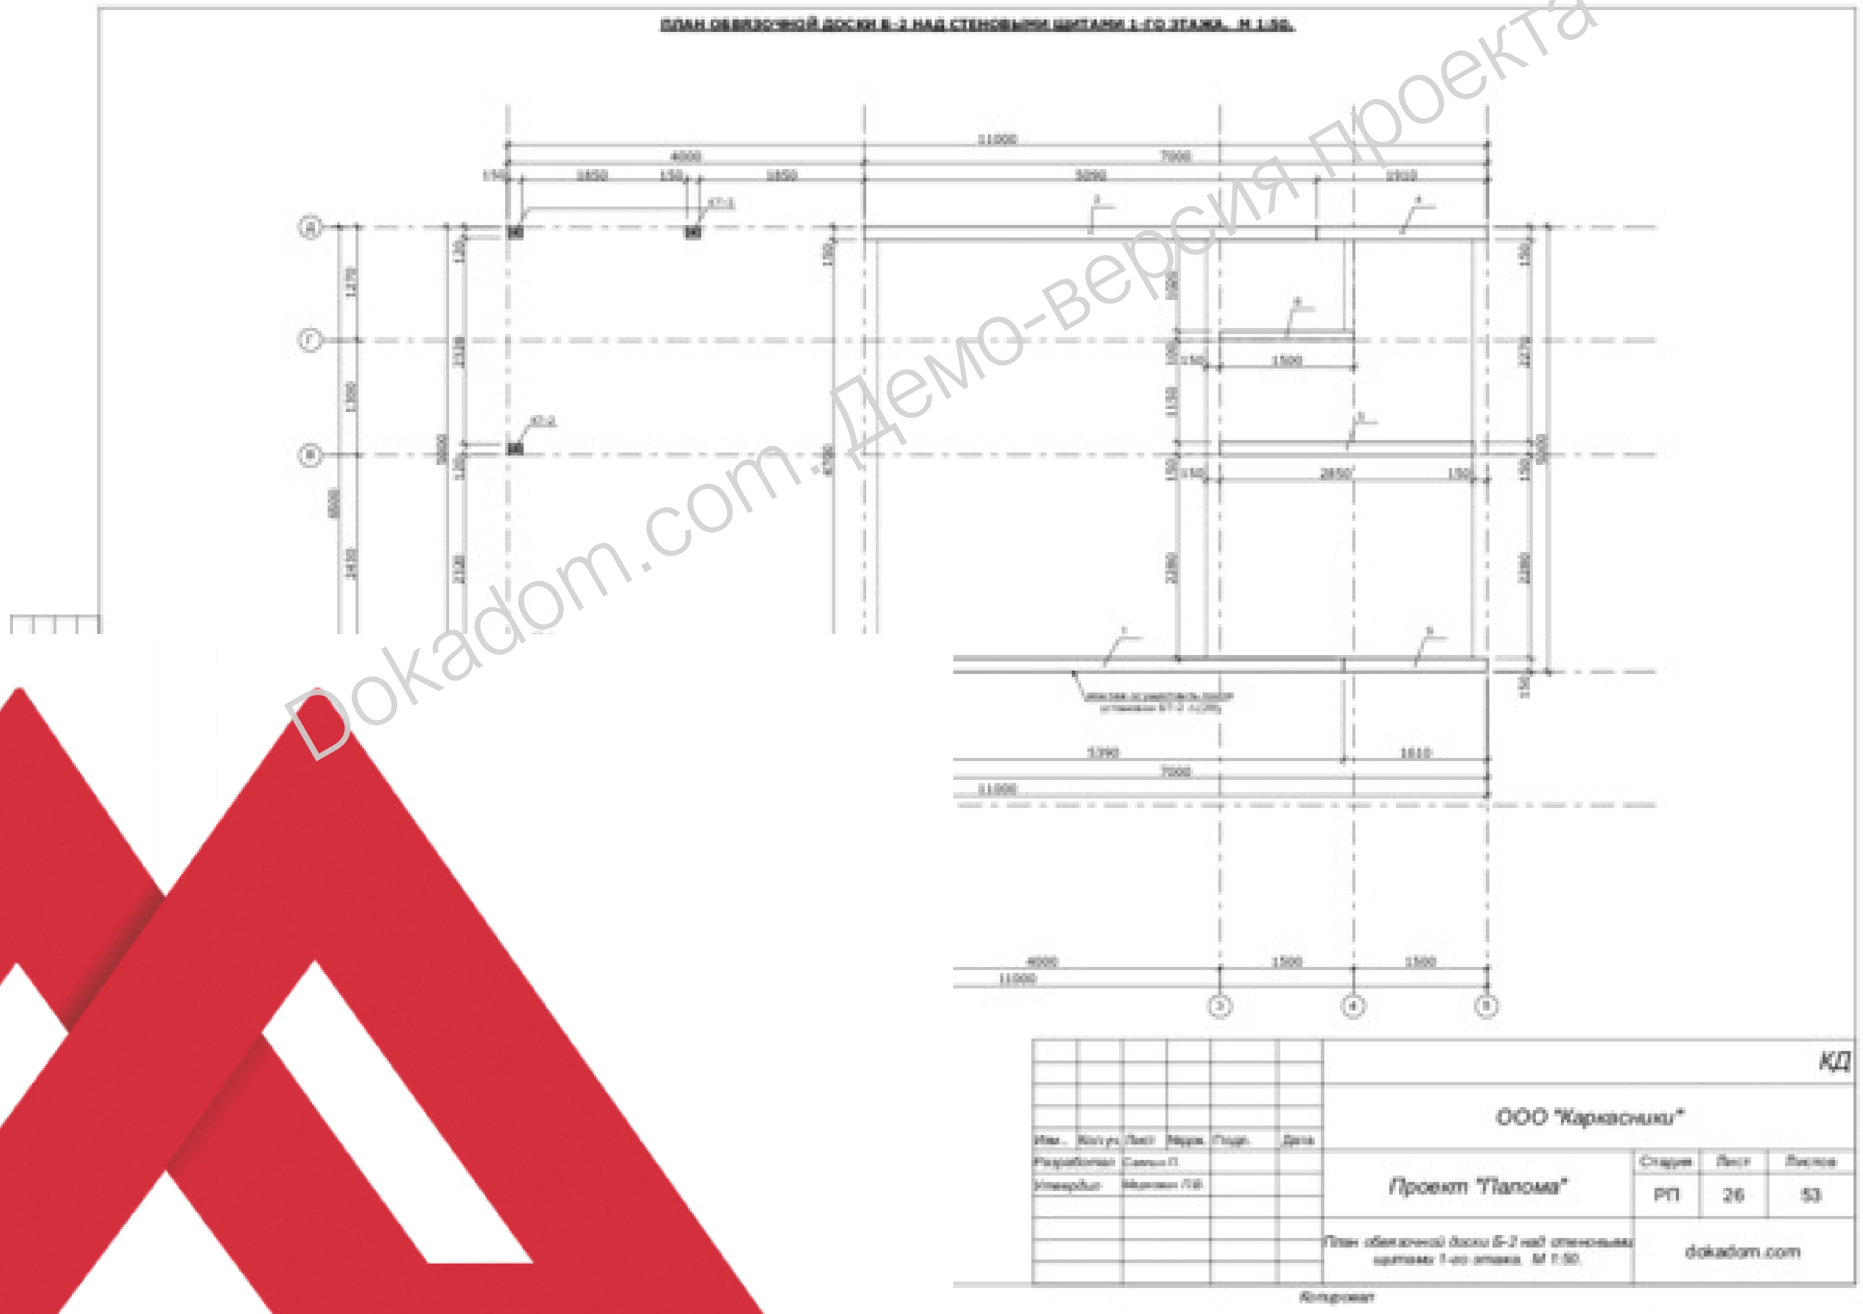
ПЛАН ОБВЯЗОЧНОЙ ДОСКИ Б-2 НАД СТЕНОВЫМИ ЩИТАМИ 1-ГО ЭТАЖА. М 1:50.
11000
4000
7000
1850
150
5090
1910
Д
Г
В
1270
1300
2330
2130
2450
6500
5000
1500
2850
2270
2280
5390
1610
КД
ООО "Каркасники"
Изм.
Кол.уч.
Лист
№док.
Подп.
Дата
Разработал
Самко П.
Утвердил
Миронов П.В.
Проект "Палома"
Стадия
Лист
Листов
РП
26
53
План обвязочной доски Б-2 над стеновыми щитами 1-го этажа. М 1:50.
dokadom.com
Копировал

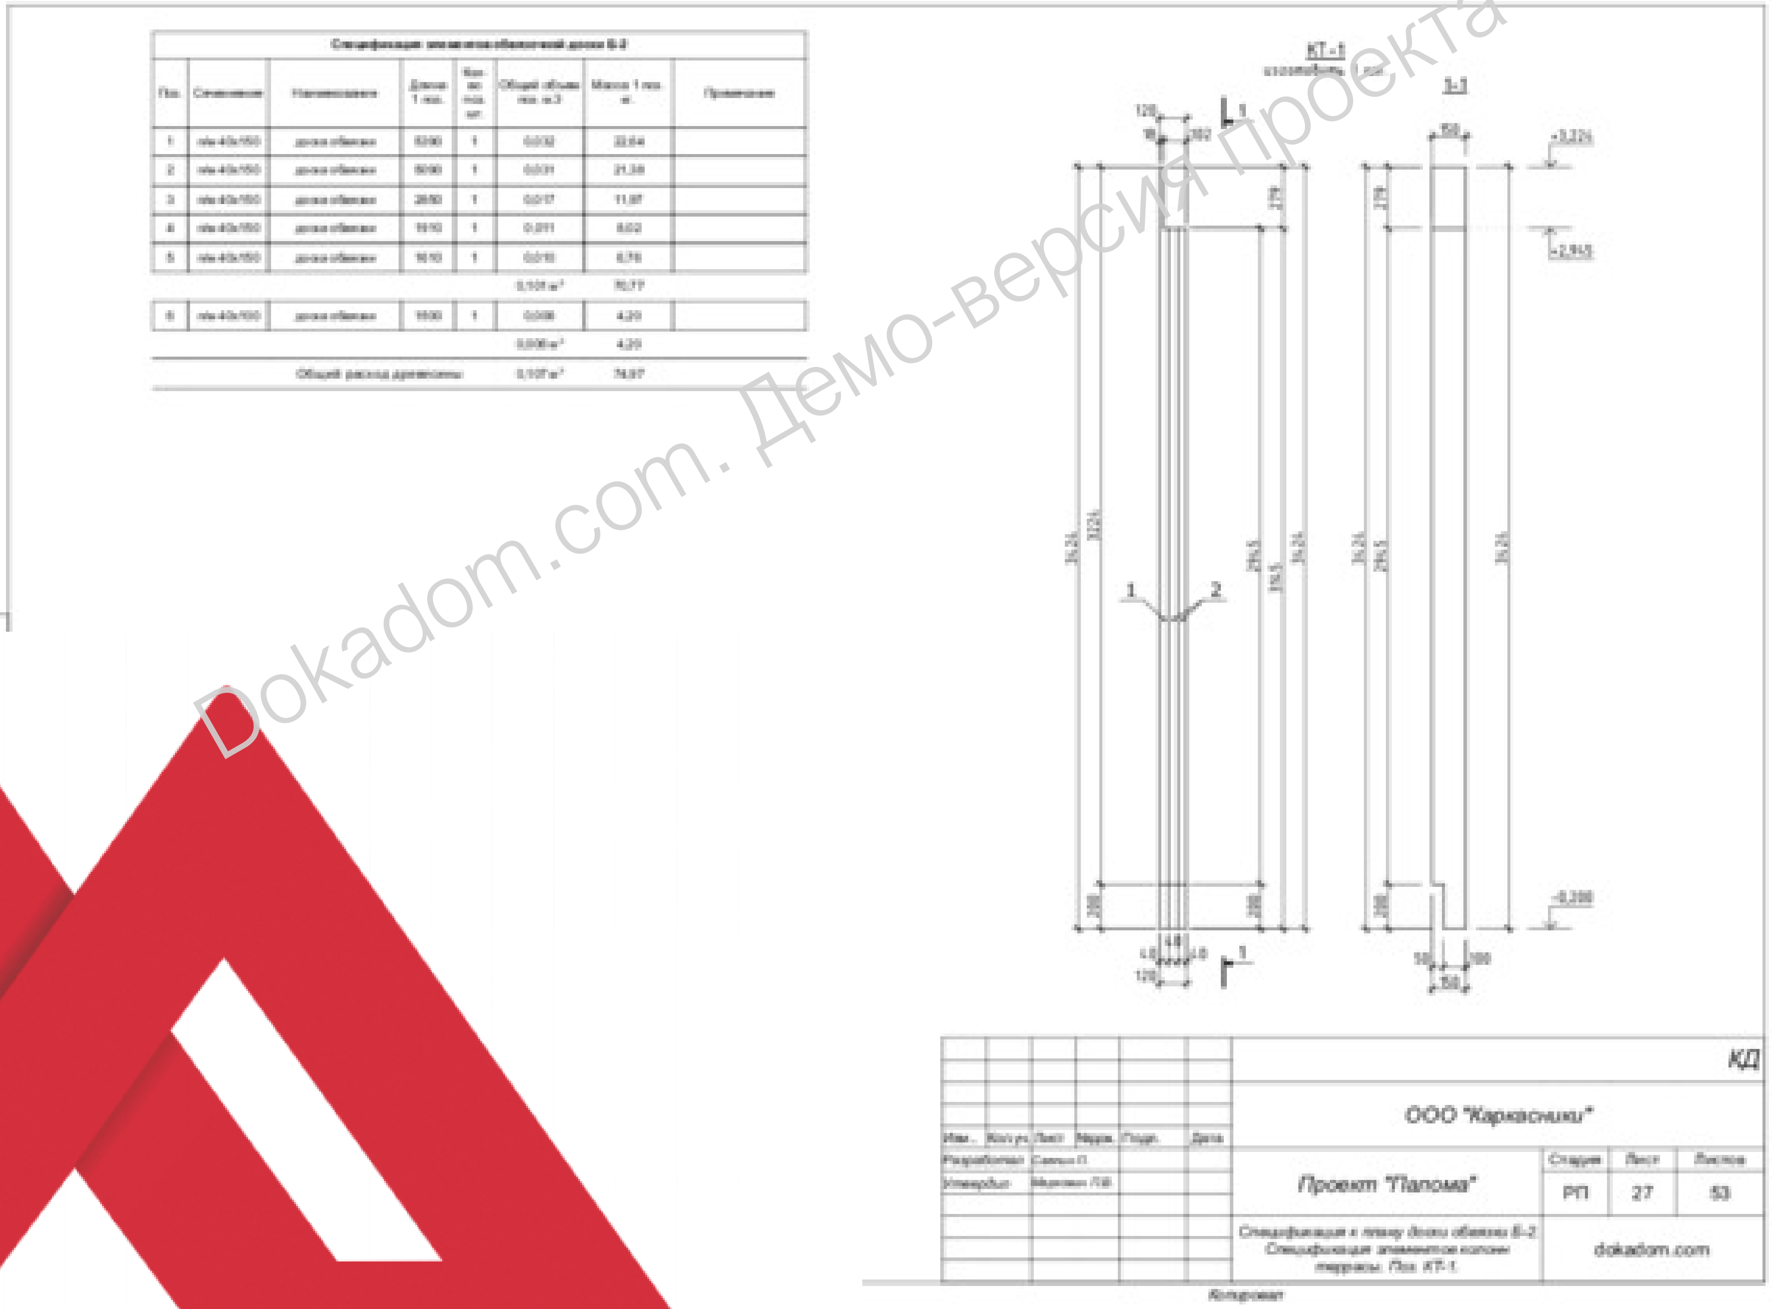

Спецификация элементов обвязочной доски Б-2

Поз.	Сечение	Наименование	Длина 1 поз.	Кол-во поз. шт.	Общий объем поз. м3	Масса 1 поз. кг	Примечание
1	[illegible]	доска обвязки	5300	1	0,032	22,64	
2	[illegible]	доска обвязки	5090	1	0,031	21,38	
3	[illegible]	доска обвязки	2650	1	0,017	11,87	
4	[illegible]	доска обвязки	1910	1	0,011	8,02	
5	[illegible]	доска обвязки	1610	1	0,010	6,76	
					0,101 м³	70,77	
6	[illegible]	доска обвязки	1500	1	0,006	4,20	
					0,006 м³	4,20	
		Общий расход древесины			0,107 м³	74,97	

КД

ООО "Каркасники"

Изм.	Кол.уч.	Лист	№док.	Подп.	Дата
Разработал		Самчук П.			
Утвердил		Миронов П.В.			

Проект "Палома"

Стадия	Лист	Листов
РП	27	53

Спецификация к плану доски обвязки Б-2
Спецификация элементов колонн террасы. Поз. КТ-1.

dokadom.com

Копировал

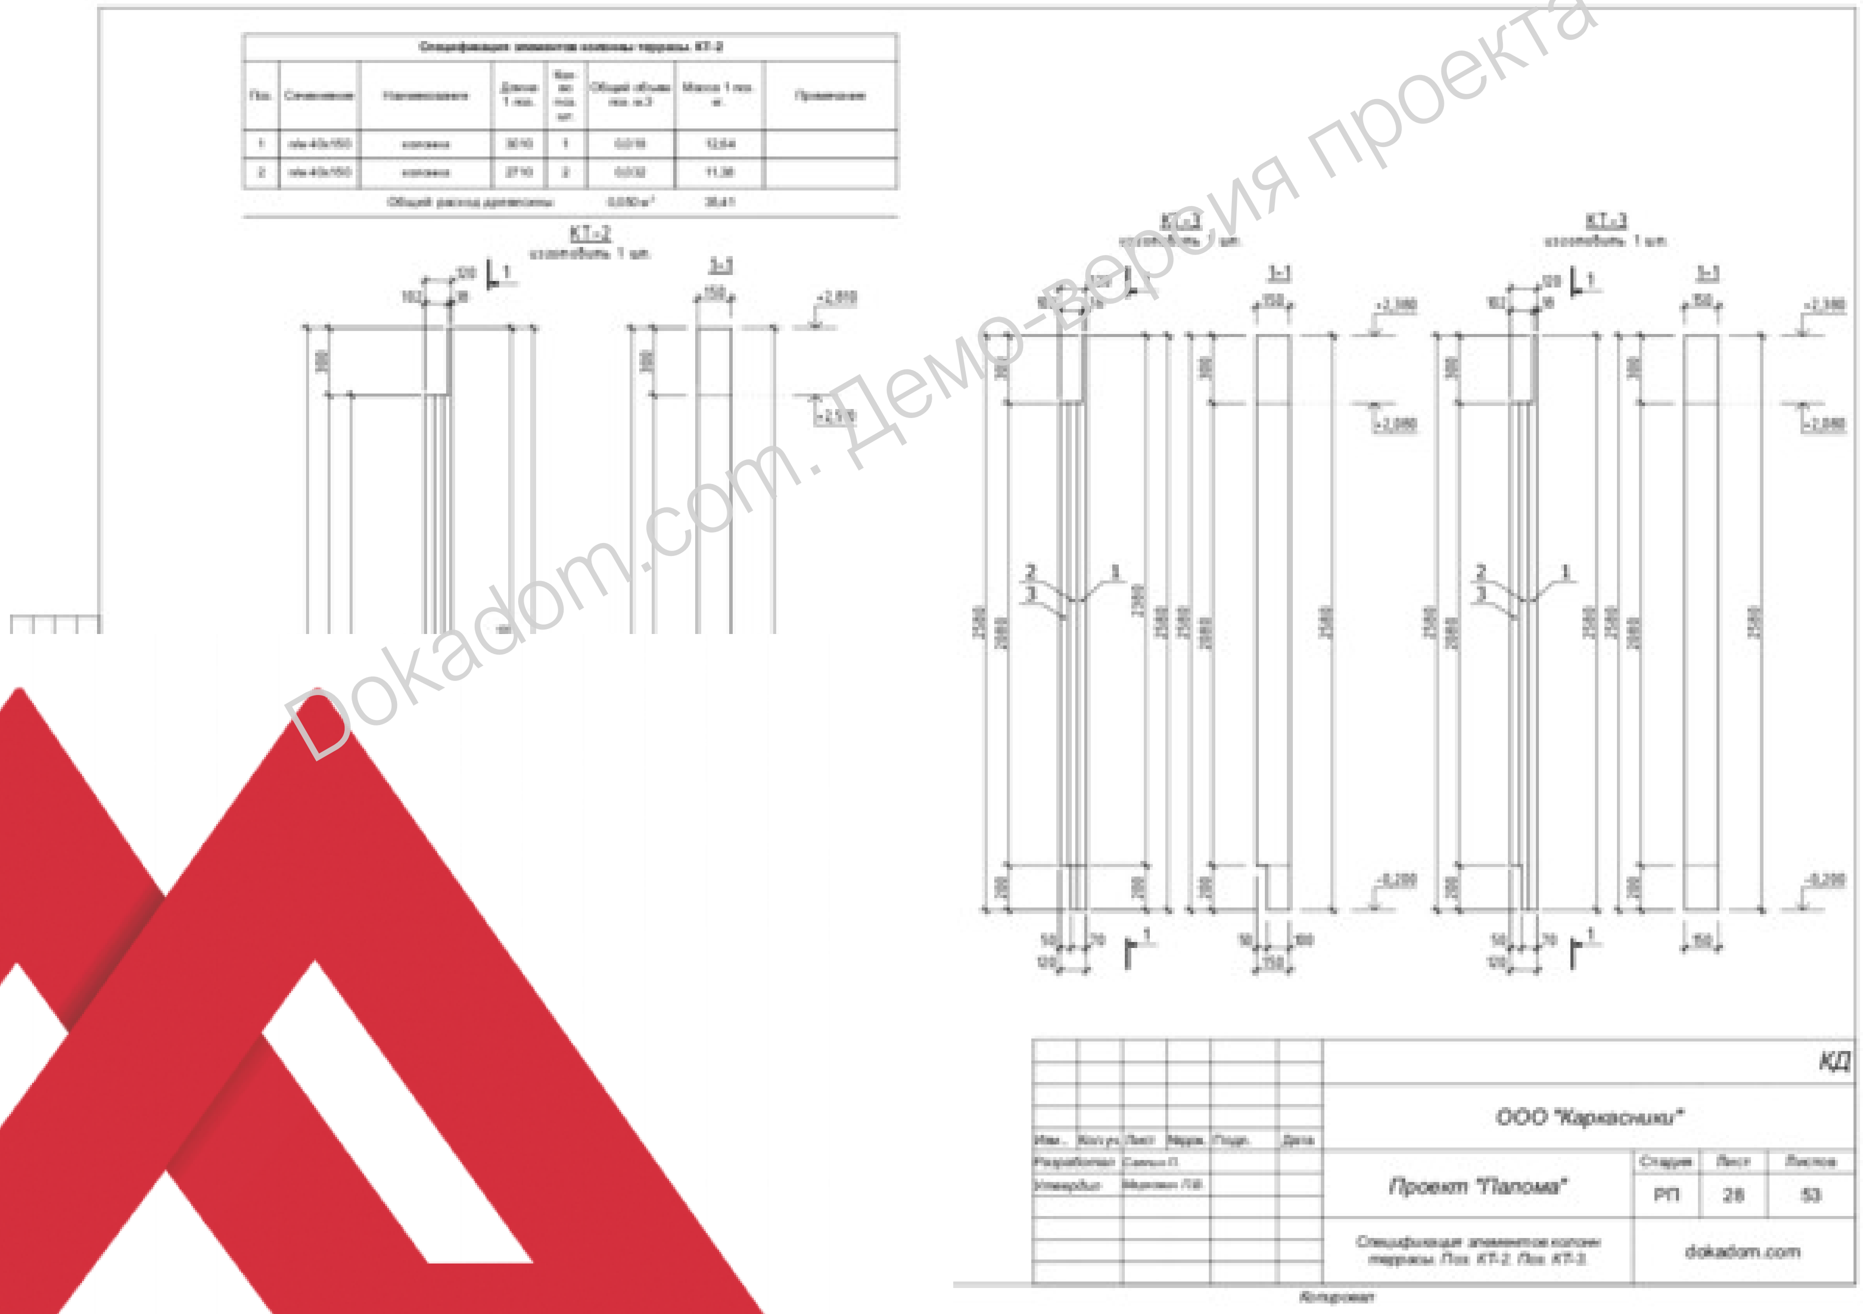

Поз.	Сечение	Наименование	Длина 1 поз.	Кол-во поз. шт.	Общий объем поз. м3	Масса 1 поз. кг	Примечание
1	[illegible] 40х150	колонна	3010	1	0,018	12,64	
2	[illegible] 40х150	колонна	2710	2	0,032	11,38	
	Общий расход древесины				0,050 м³	35,41	

Изм.	Кол.уч.	Лист	№док.	Подп.	Дата	
Разработал	[illegible]					
Утвердил	[illegible]					

КД

ООО "Каркасники"

Проект "Паломa"

Стадия	Лист	Листов
РП	28	53

Спецификация элементов колонн террасы. Поз. КТ-2. Поз. КТ-3.

dokadom.com

Копировал

ПЛАН БАЛОК ТЕРРАСЫ. М 1:50.

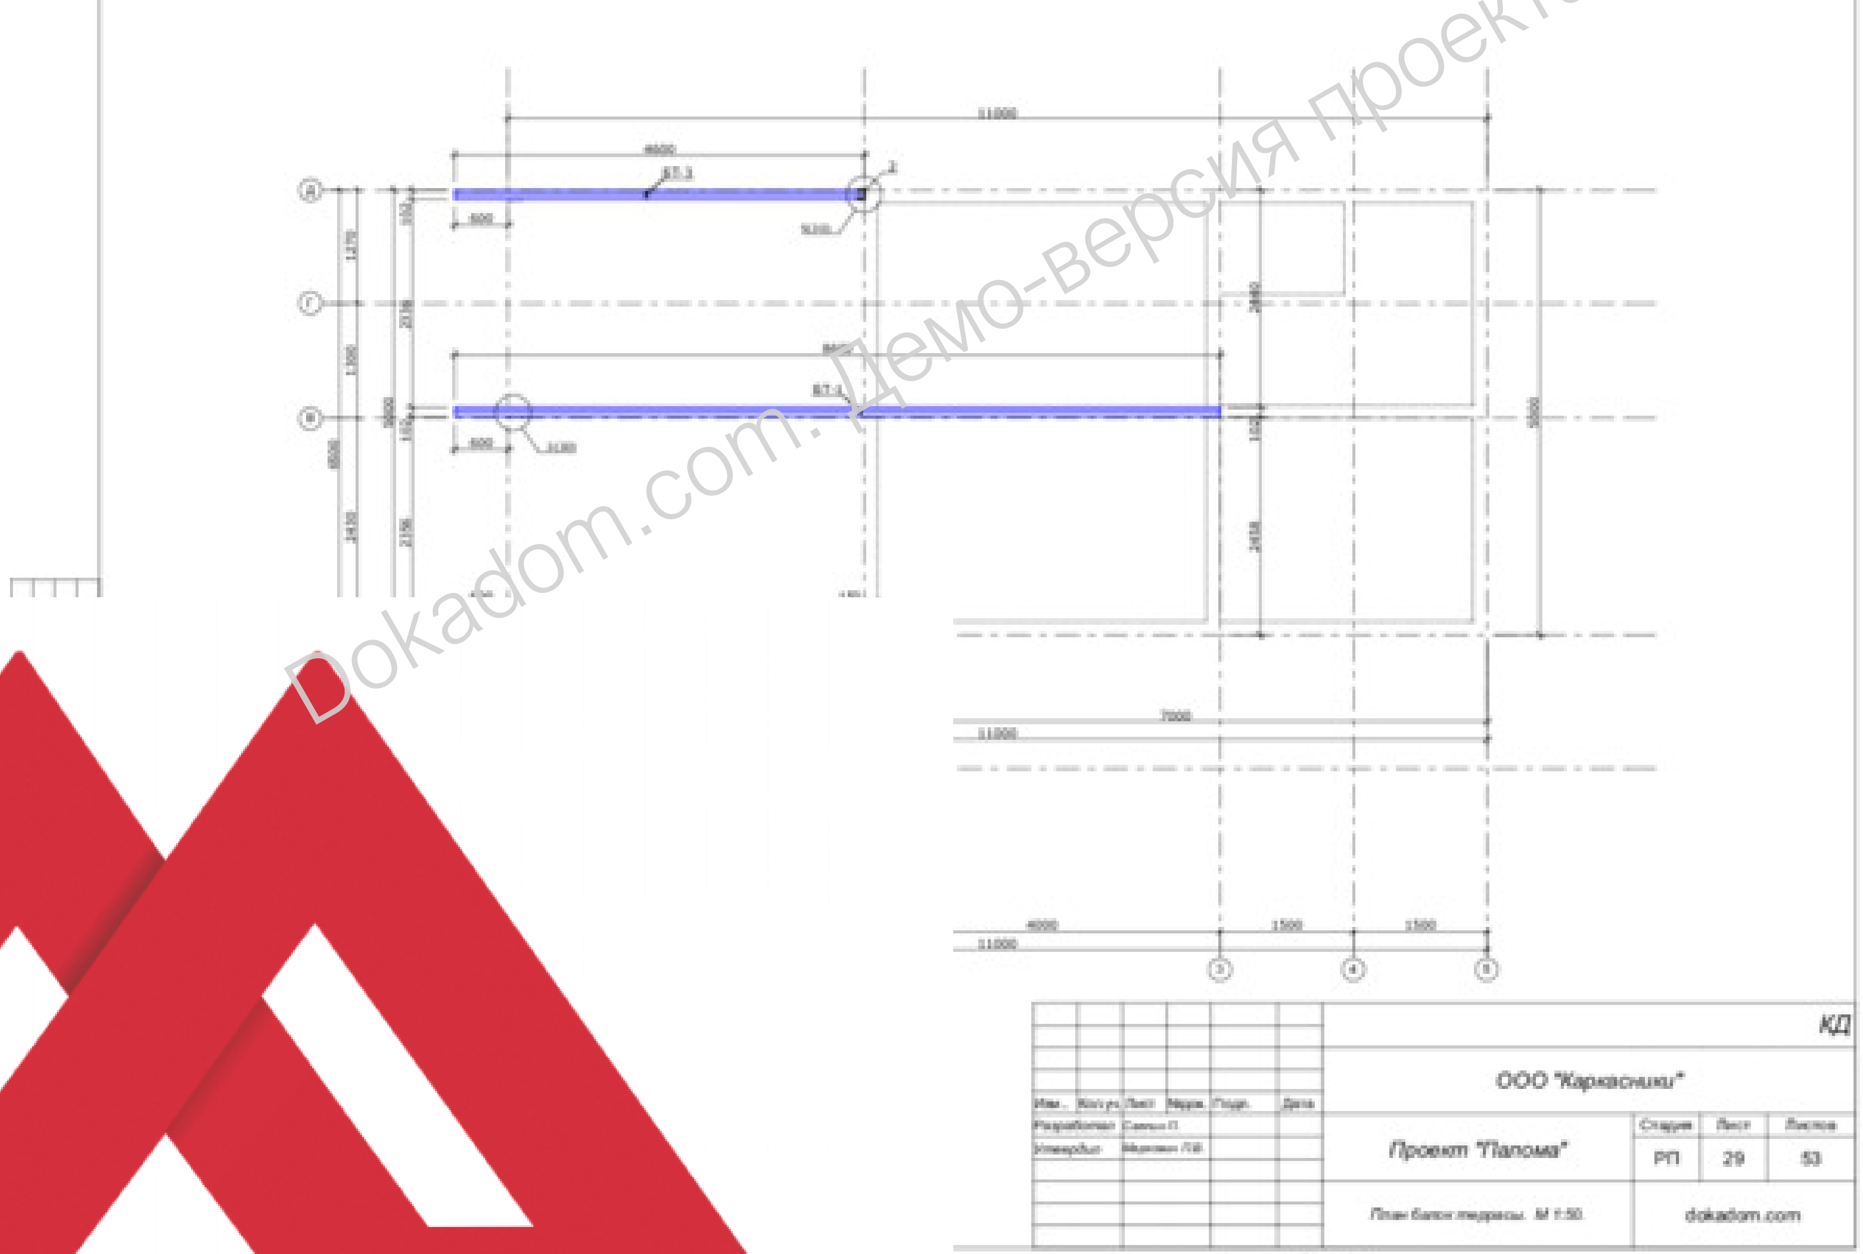

КД

ООО "Каркасники"

Изм.	Кол.уч.	Лист	№док.	Подп.	Дата
Разработал	[illegible]				
Утвердил	[illegible]				

Проект "Палома"

Стадия	Лист	Листов
РП	29	53

План балок террасы. М 1:50.

dokadom.com

Копировал

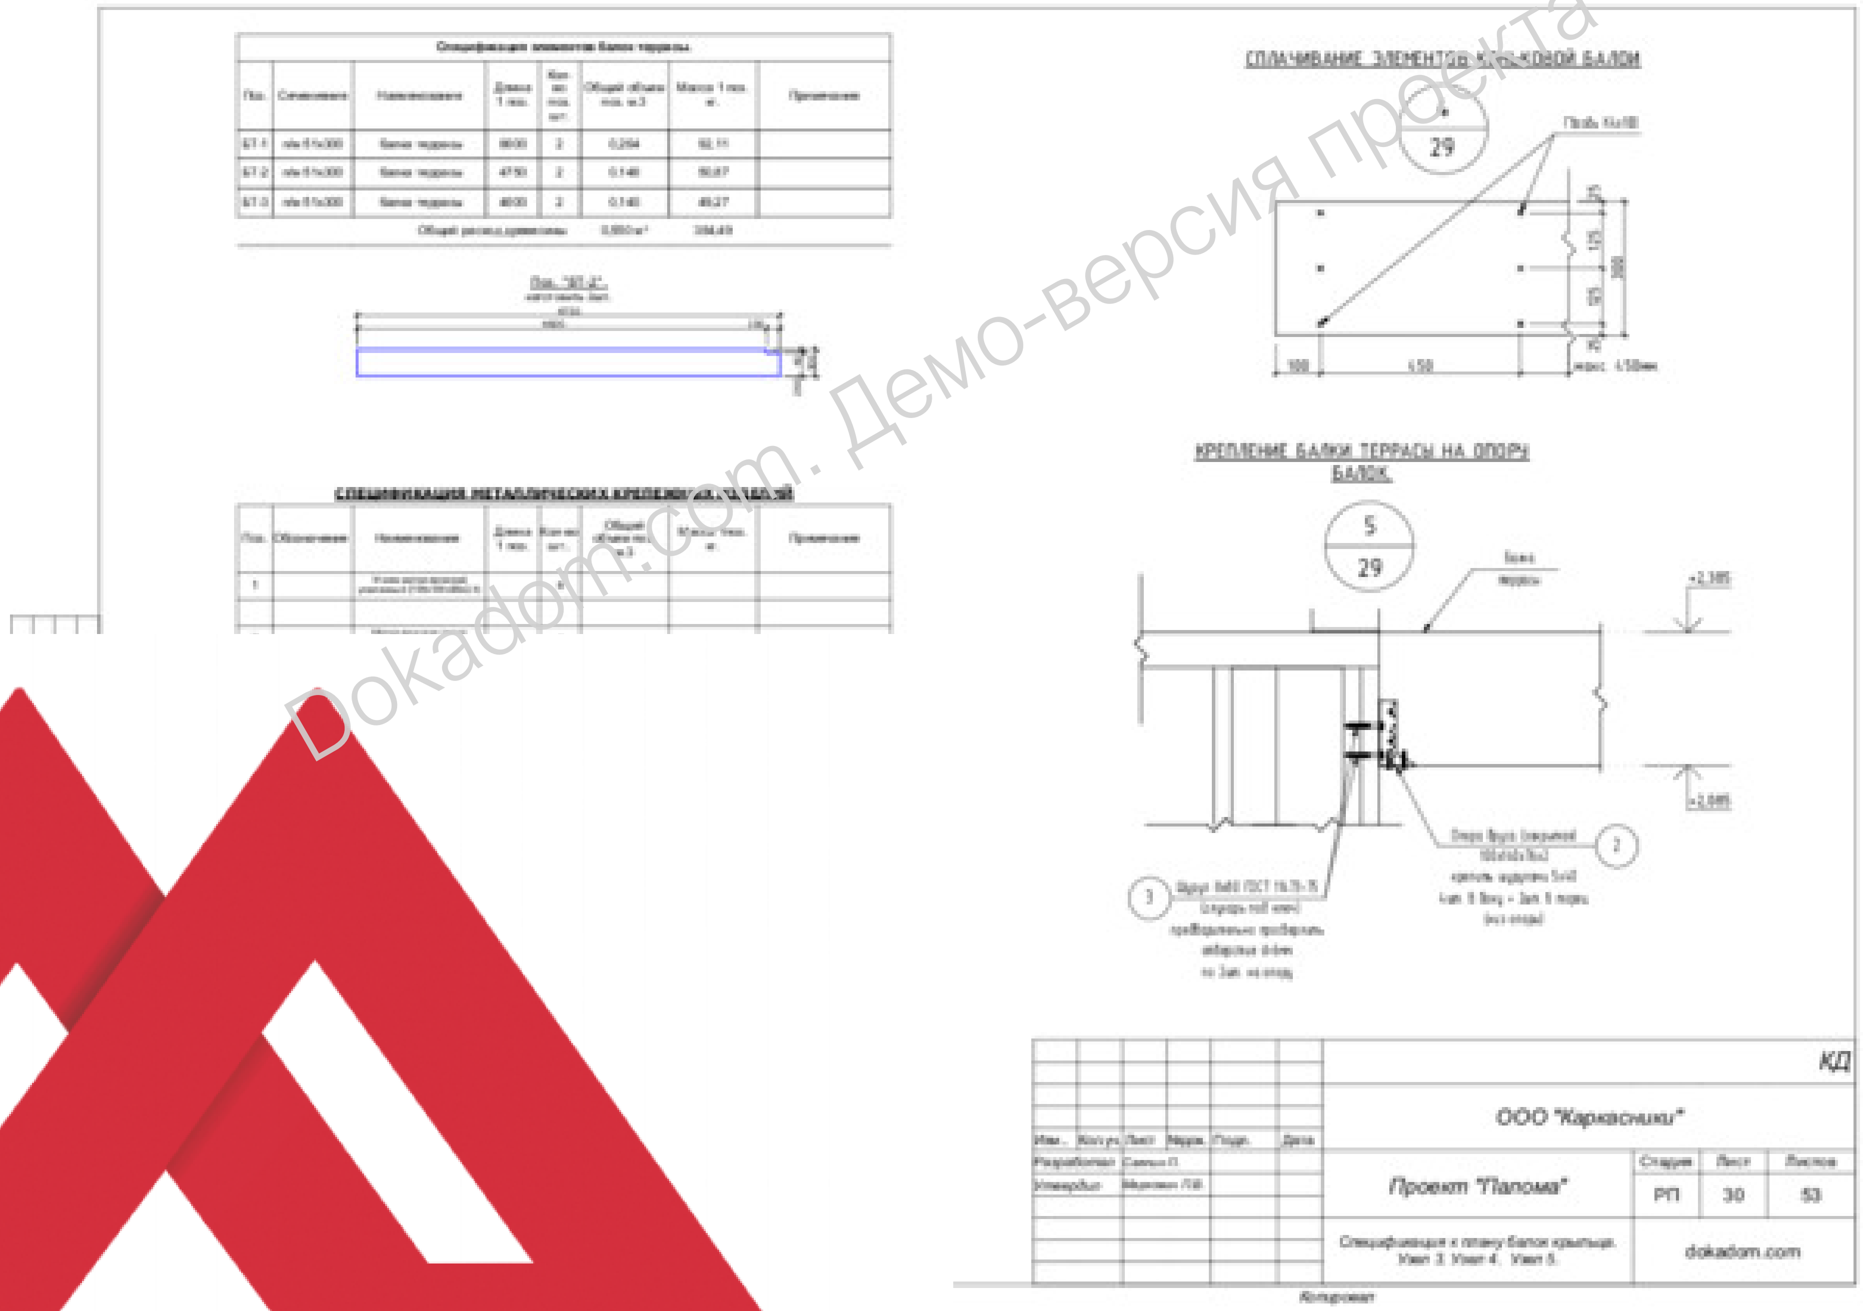

СПЛАЧИВАНИЕ ЭЛЕМЕНТОВ КОНЬКОВОЙ БАЛКИ

КРЕПЛЕНИЕ БАЛКИ ТЕРРАСЫ НА ОПОРУ БАЛОК

СПЕЦИФИКАЦИЯ МЕТАЛЛИЧЕСКИХ КРЕПЕЖНЫХ ИЗДЕЛИЙ

КД

ООО "Каркасники"

Проект "Палома"

Стадия	Лист	Листов
РП	30	53

Спецификация к плану балок крыльца.
Узел 3. Узел 4. Узел 5.

dokadom.com

Копировал

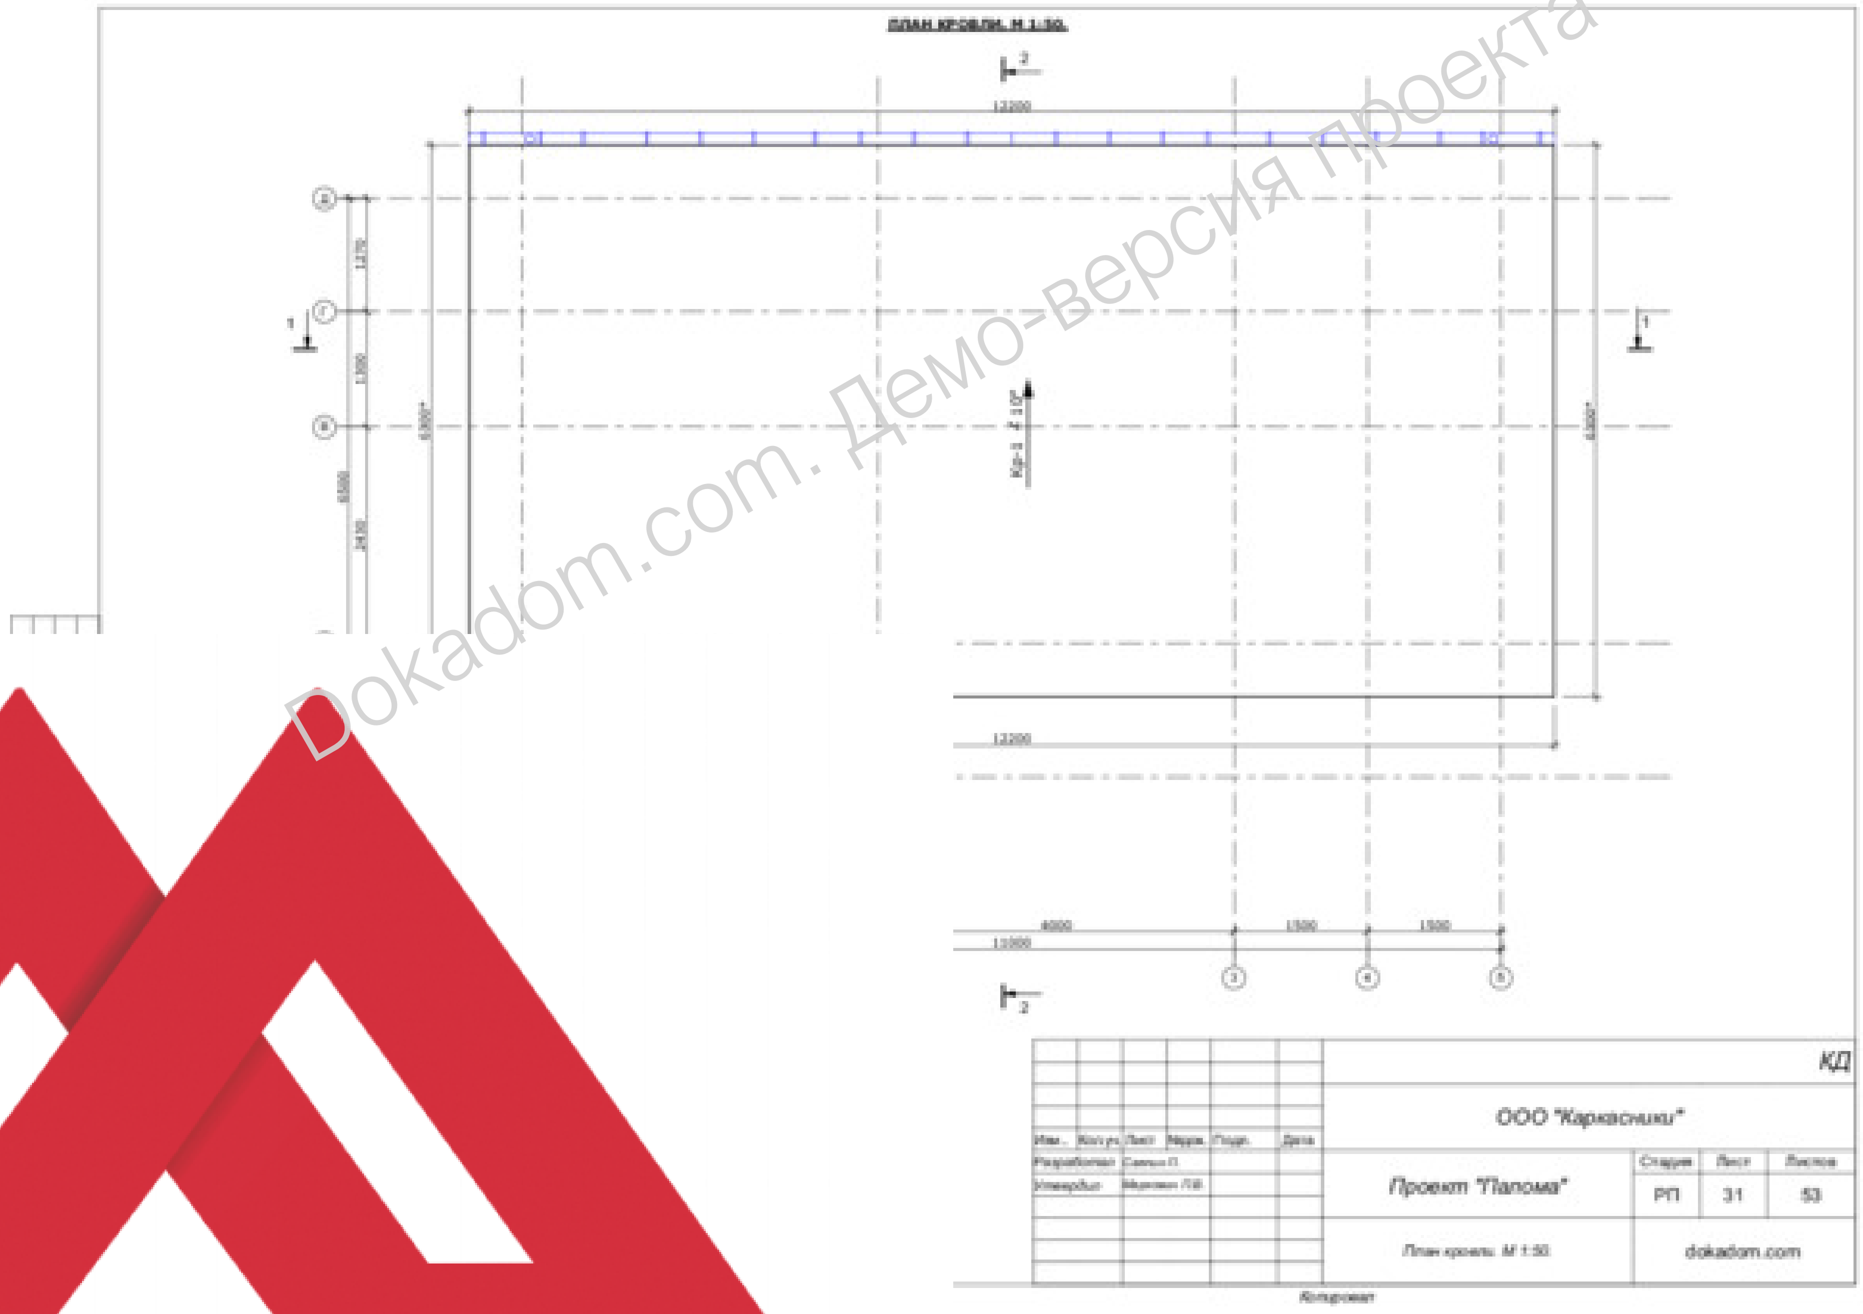
ПЛАН КРОВЛИ. М 1:50.
2
12200
1270
1500
6300*
6500
2430
1
Кр-1 i 10°
12200
4000
1500
1500
11000
2
КД
ООО "Каркасники"
Изм.
Кол.уч.
Лист
№док.
Подп.
Дата
Разработал
Самых П.
Утвердил
Марченко Л.В.
Проект "Палома"
Стадия
Лист
Листов
РП
31
53
План кровли. М 1:50
dokadom.com
Копировал

1. Площадь кровли - 78,81 м2 (отходы на раскрой не учтен).
длина коньков - 0,00 м;
длина торцов - 12,00 м;
длина карнизов - 24,40 м;
длина планки примыкания - 0,00 м.
длина ендовы - 0,00 м.
Кровельный материал - Металлочерепица, цвет:
2. Для вентиляции подкровельного пространства предусмотреть щелевую подшивку карнизов .
3. Поверх стропил утепленной кровли крепить гидроизоляционную мембрану диффузионная. Обрешётка выполняется из обрезной доски 25х100 мм с шагом 300 мм.
4. Кровельный материал укладывается согласно инструкции производителя.

Спецификация элементов водостока.

№ п/п	Наименование	Кол-во	Длина мм.
1	Желоб Водосточный 18	2	6100
2	Труба Водоотведения 18	2	1500
3	Отвод Трубы Водоотведения 18	2	877
4	Колено Трубы Водоотведения 18	2	291

Изм.	Кол.уч.	Лист	№док.	Подп.	Дата
Разработал		Савин П.			
Утвердил		Марченко П.В.			

КД

ООО "Каркасники"

Проект "Палома"

Стадия	Лист	Листов
РП	32	53

Общие данные к плану кровли.
Спецификация элементов водостока.

dokadom.com

Копировал

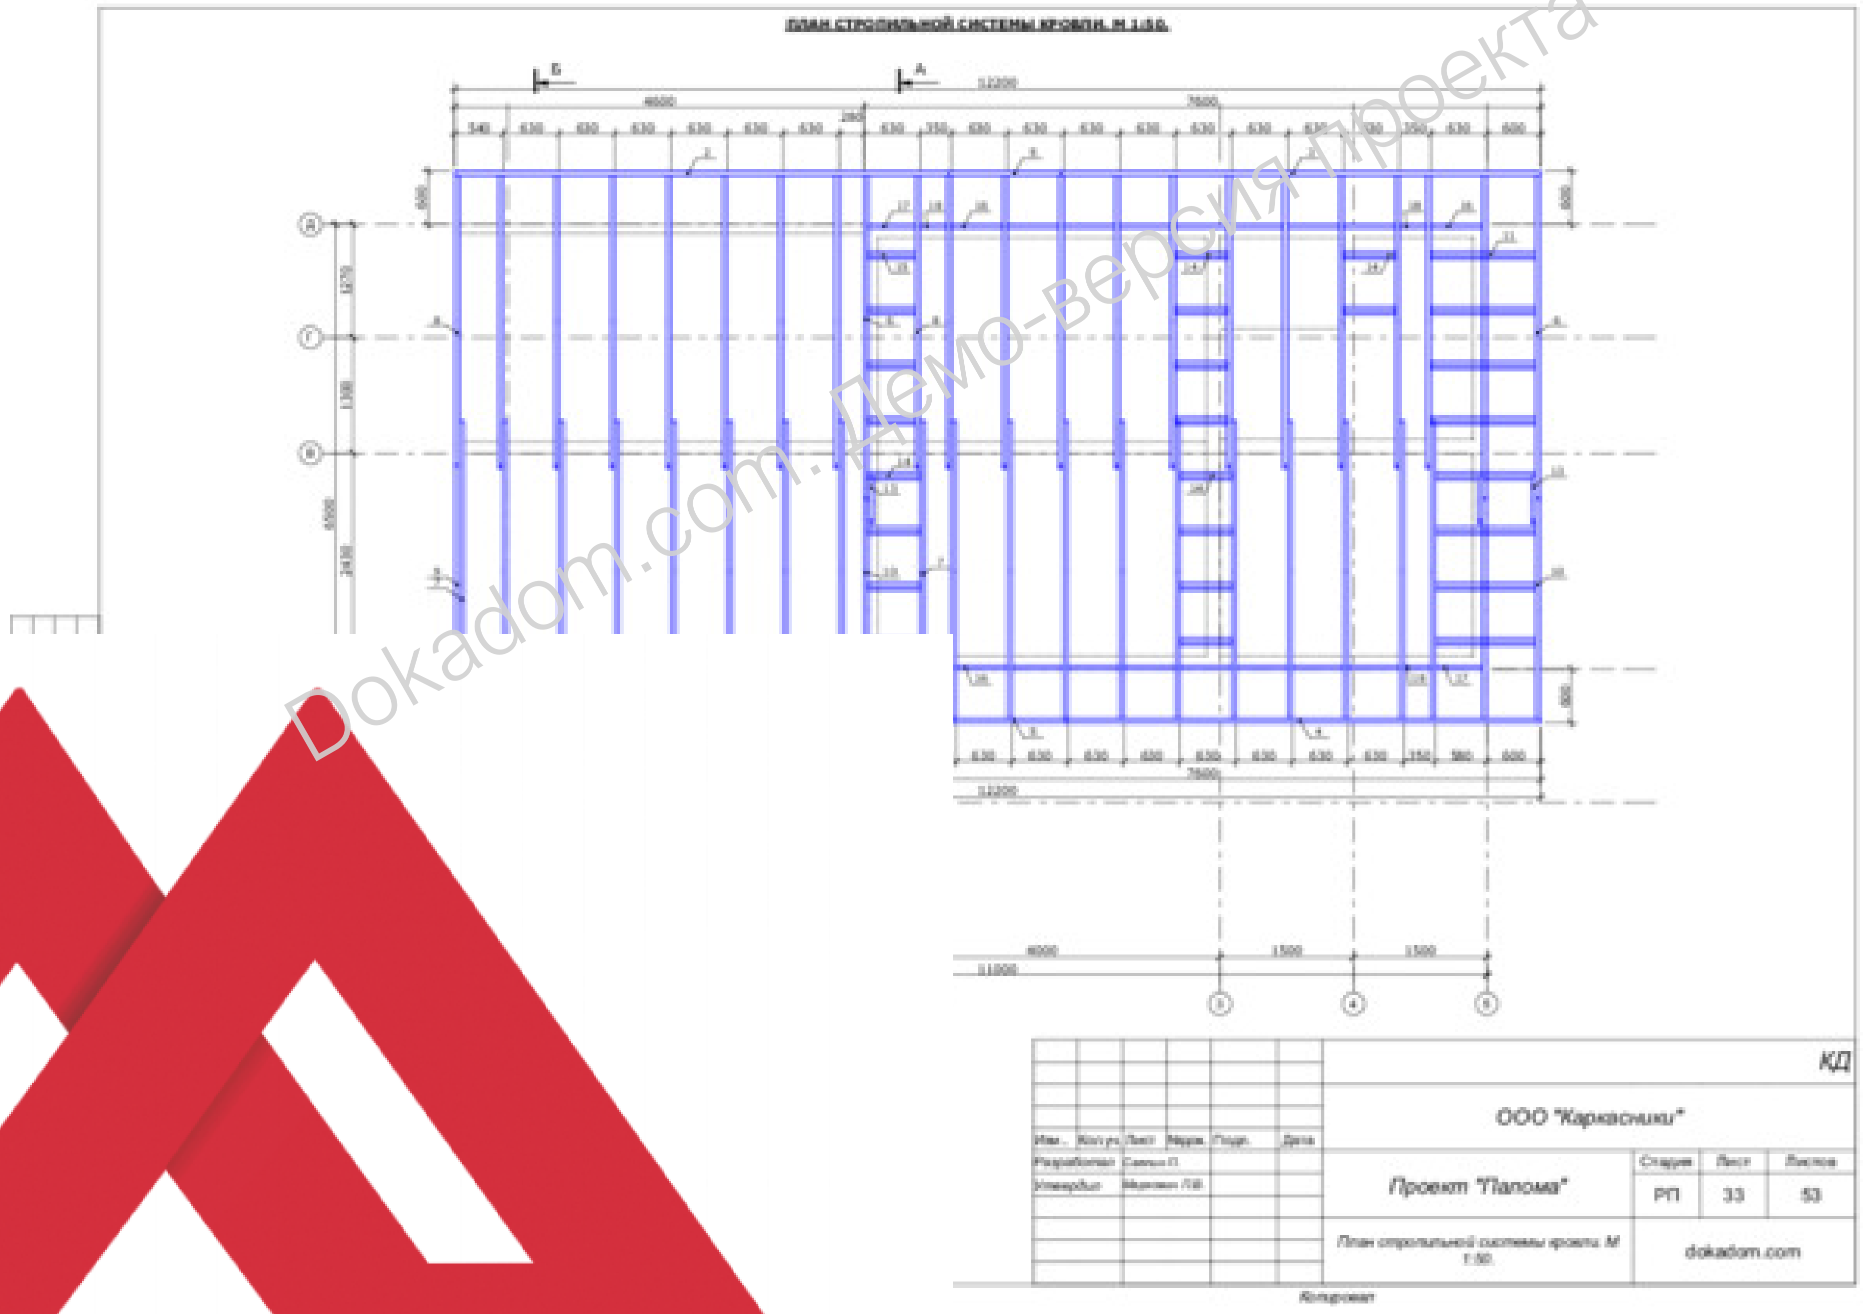

ПЛАН СТРОПИЛЬНОЙ СИСТЕМЫ КРОВЛИ. М 1:50.

КД

ООО "Каркасники"

Изм.	Кол.уч.	Лист	№док.	Подп.	Дата
Разработал		Савин П.			
Утвердил		Миронов П.В.			

Проект "Палома"

Стадия	Лист	Листов
РП	33	53

План стропильной системы кровли. М 1:50.

dokadom.com

Копировал

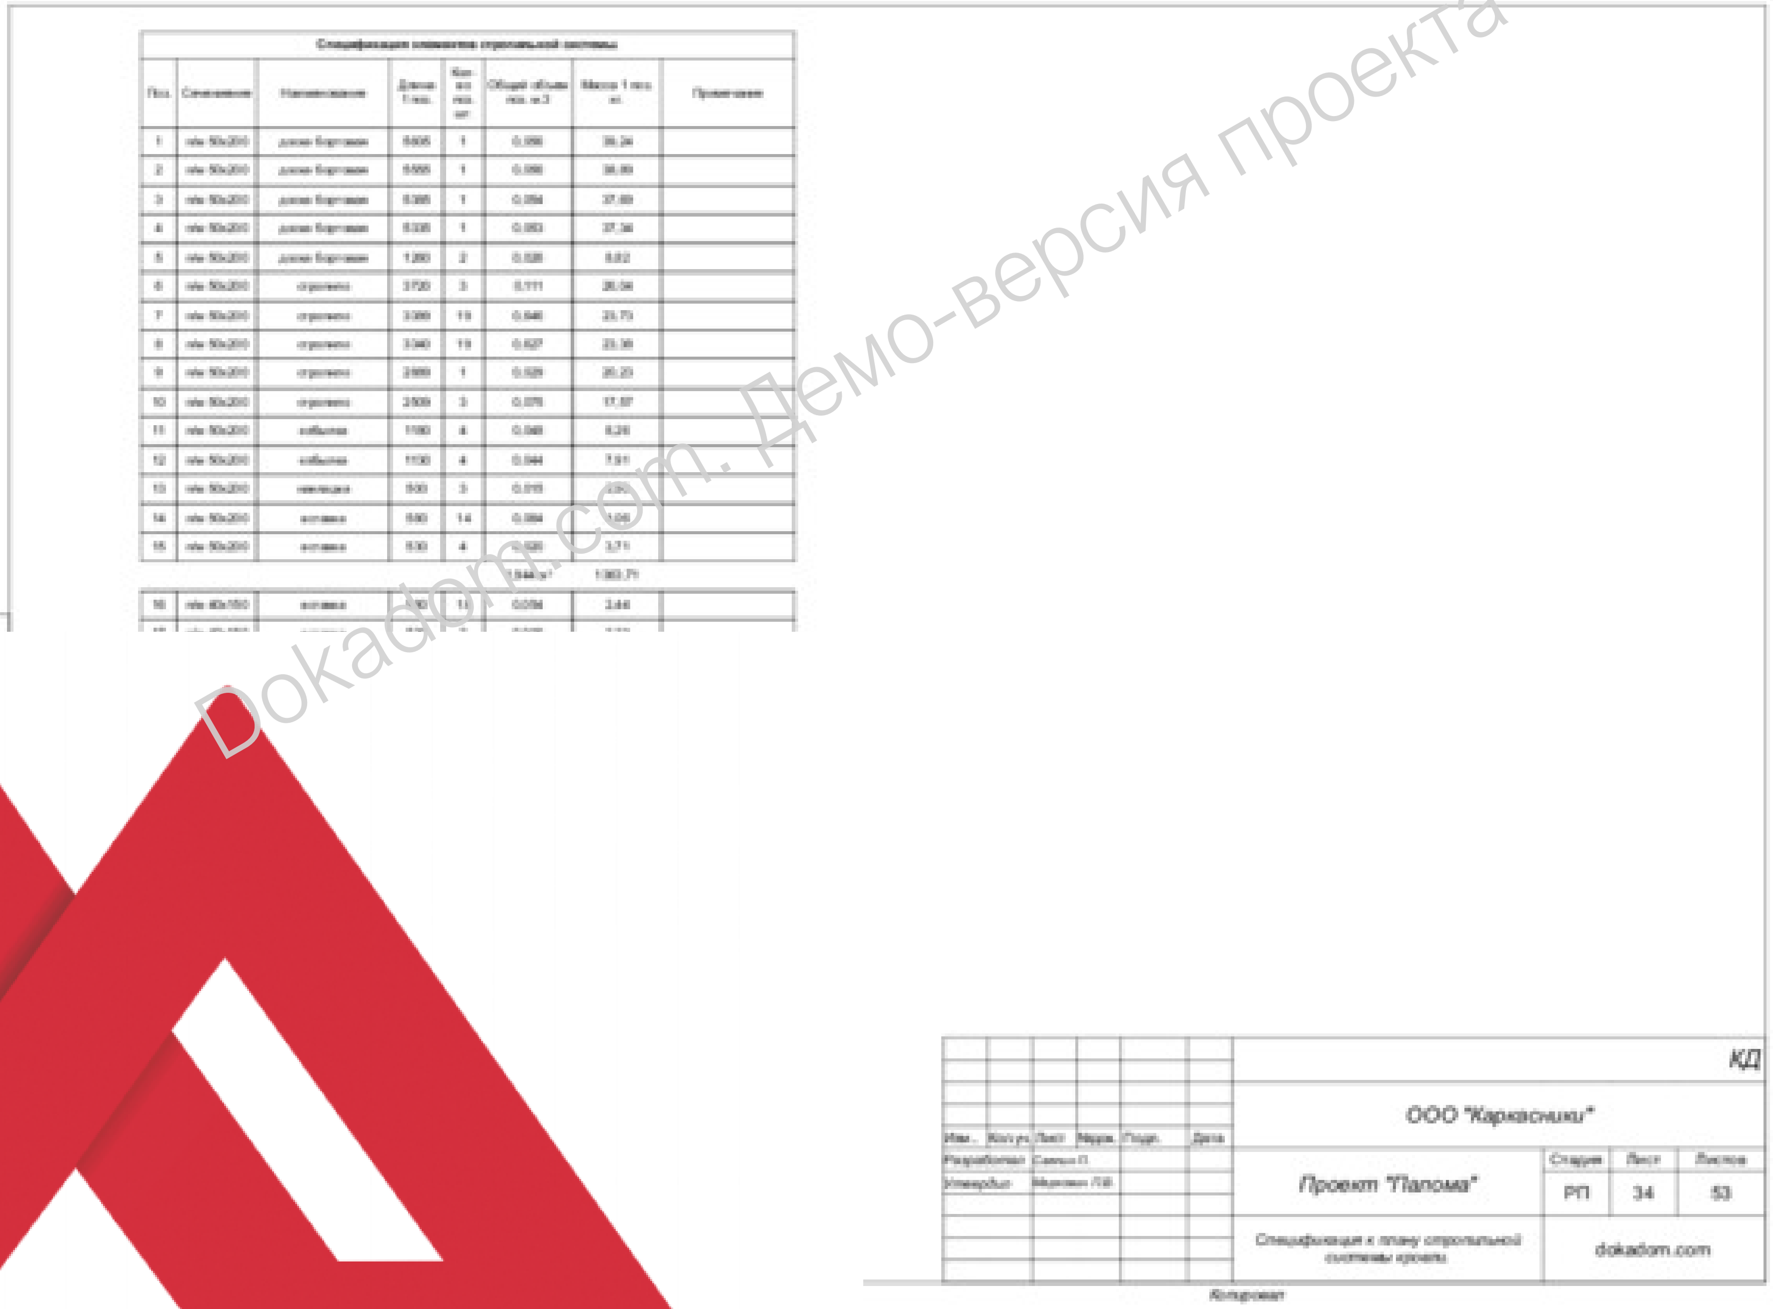

Спецификация элементов стропильной системы

Поз.	Сечение	Наименование	Длина 1 поз.	Кол-во поз. шт	Общий объем поз. м3	Масса 1 поз. кг	Примечание
1	п/м 50х200	доска бортовая	5605	1	0,056	39,24	
2	п/м 50х200	доска бортовая	5555	1	0,056	38,89	
3	п/м 50х200	доска бортовая	5385	1	0,054	37,69	
4	п/м 50х200	доска бортовая	5335	1	0,053	37,34	
5	п/м 50х200	доска бортовая	1260	2	0,026	8,82	
6	п/м 50х200	стропило	3720	3	0,111	26,04	
7	п/м 50х200	стропило	3390	19	0,646	23,73	
8	п/м 50х200	стропило	3340	19	0,627	23,38	
9	п/м 50х200	стропило	2889	1	0,029	20,23	
10	п/м 50х200	стропило	2509	3	0,075	17,57	
11	п/м 50х200	кобылка	1180	4	0,048	8,26	
12	п/м 50х200	кобылка	1130	4	0,044	7,91	
13	п/м 50х200	накладка	500	3	0,015	3,50	
14	п/м 50х200	вставка	580	14	0,084	4,06	
15	п/м 50х200	вставка	530	4	0,026	3,71	
					1,944 м³	1360,71	
16	п/м 40х150	вставка	580	11	0,058	2,44	

Изм.	Кол.уч.	Лист	№док.	Подп.	Дата
Разработал	[illegible]				
Утвердил	[illegible]				

КД

ООО "Каркасники"

Проект "Палома"

Стадия	Лист	Листов
РП	34	53

Спецификация к плану стропильной системы кровли

dokadom.com

Копировал

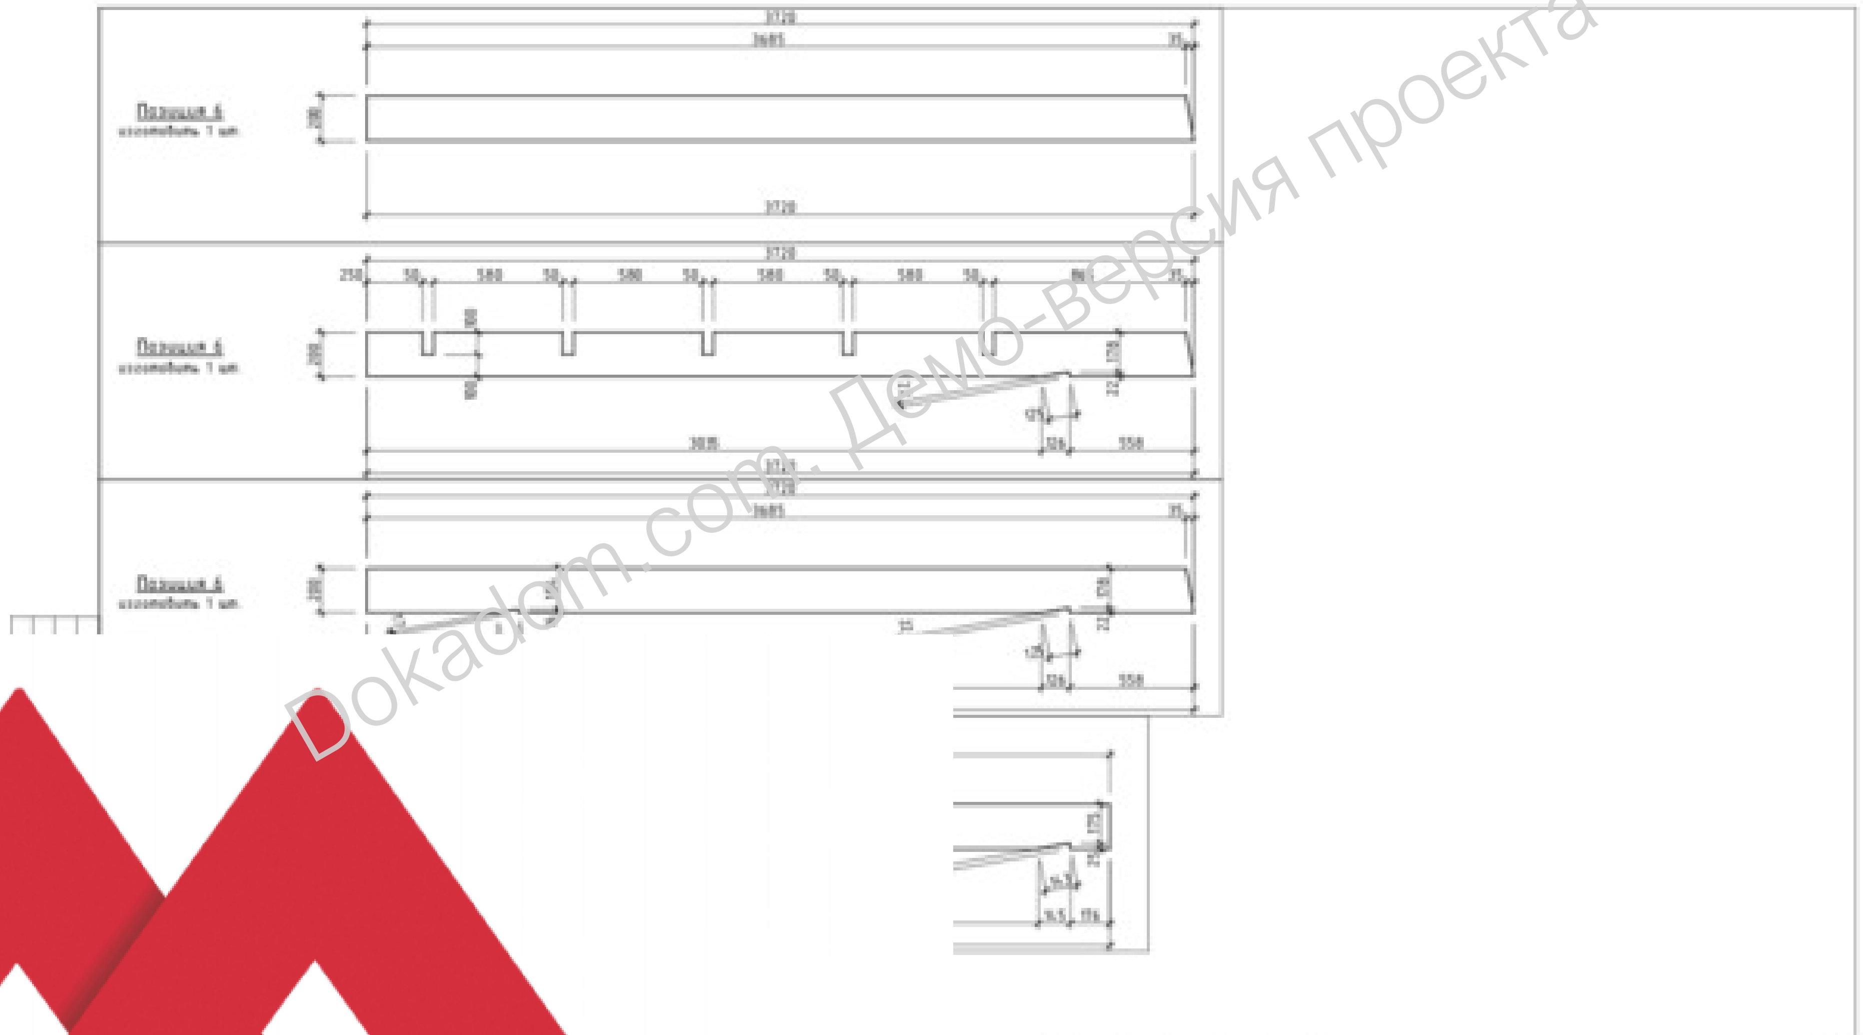

						КД			
						ООО "Каркасники"			
Изм.	Кол.уч.	Лист	№док.	Подп.	Дата				
Разработал		Санько П.				Проект "Палома"	Стадия	Лист	Листов
Утвердил		Марченко Л.В.					РП	35	53
						Стропила позиция "6", "7".	dokadom.com		

Копировал

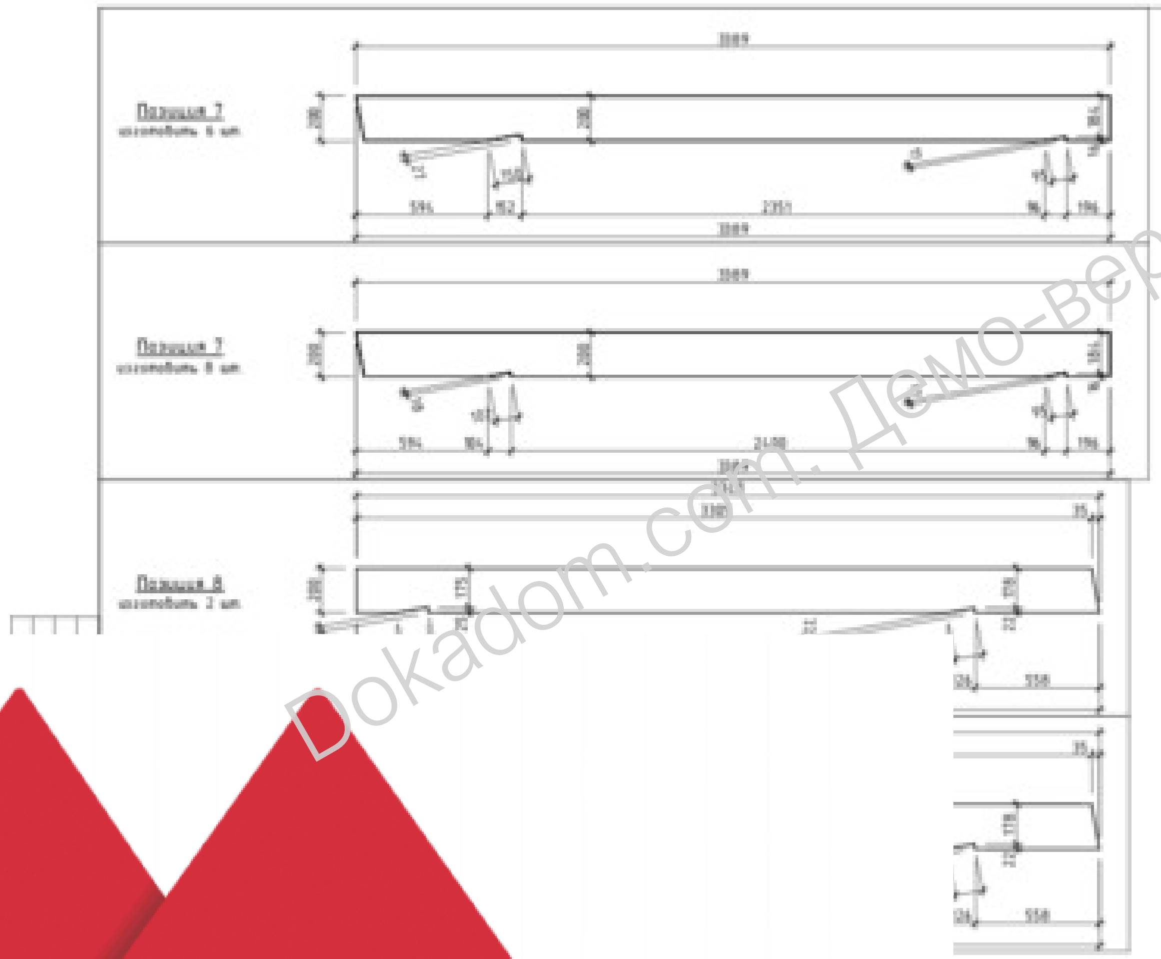

КД

ООО "Каркасники"

Изм. | Кол.уч. | Лист | №док. | Подп. | Дата

Разработал [illegible]

Утвердил [illegible]

Проект "Палома"

Стадия | Лист | Листов

РП | 36 | 53

Стропила позиция "7", "8".

dokadom.com

Копировал

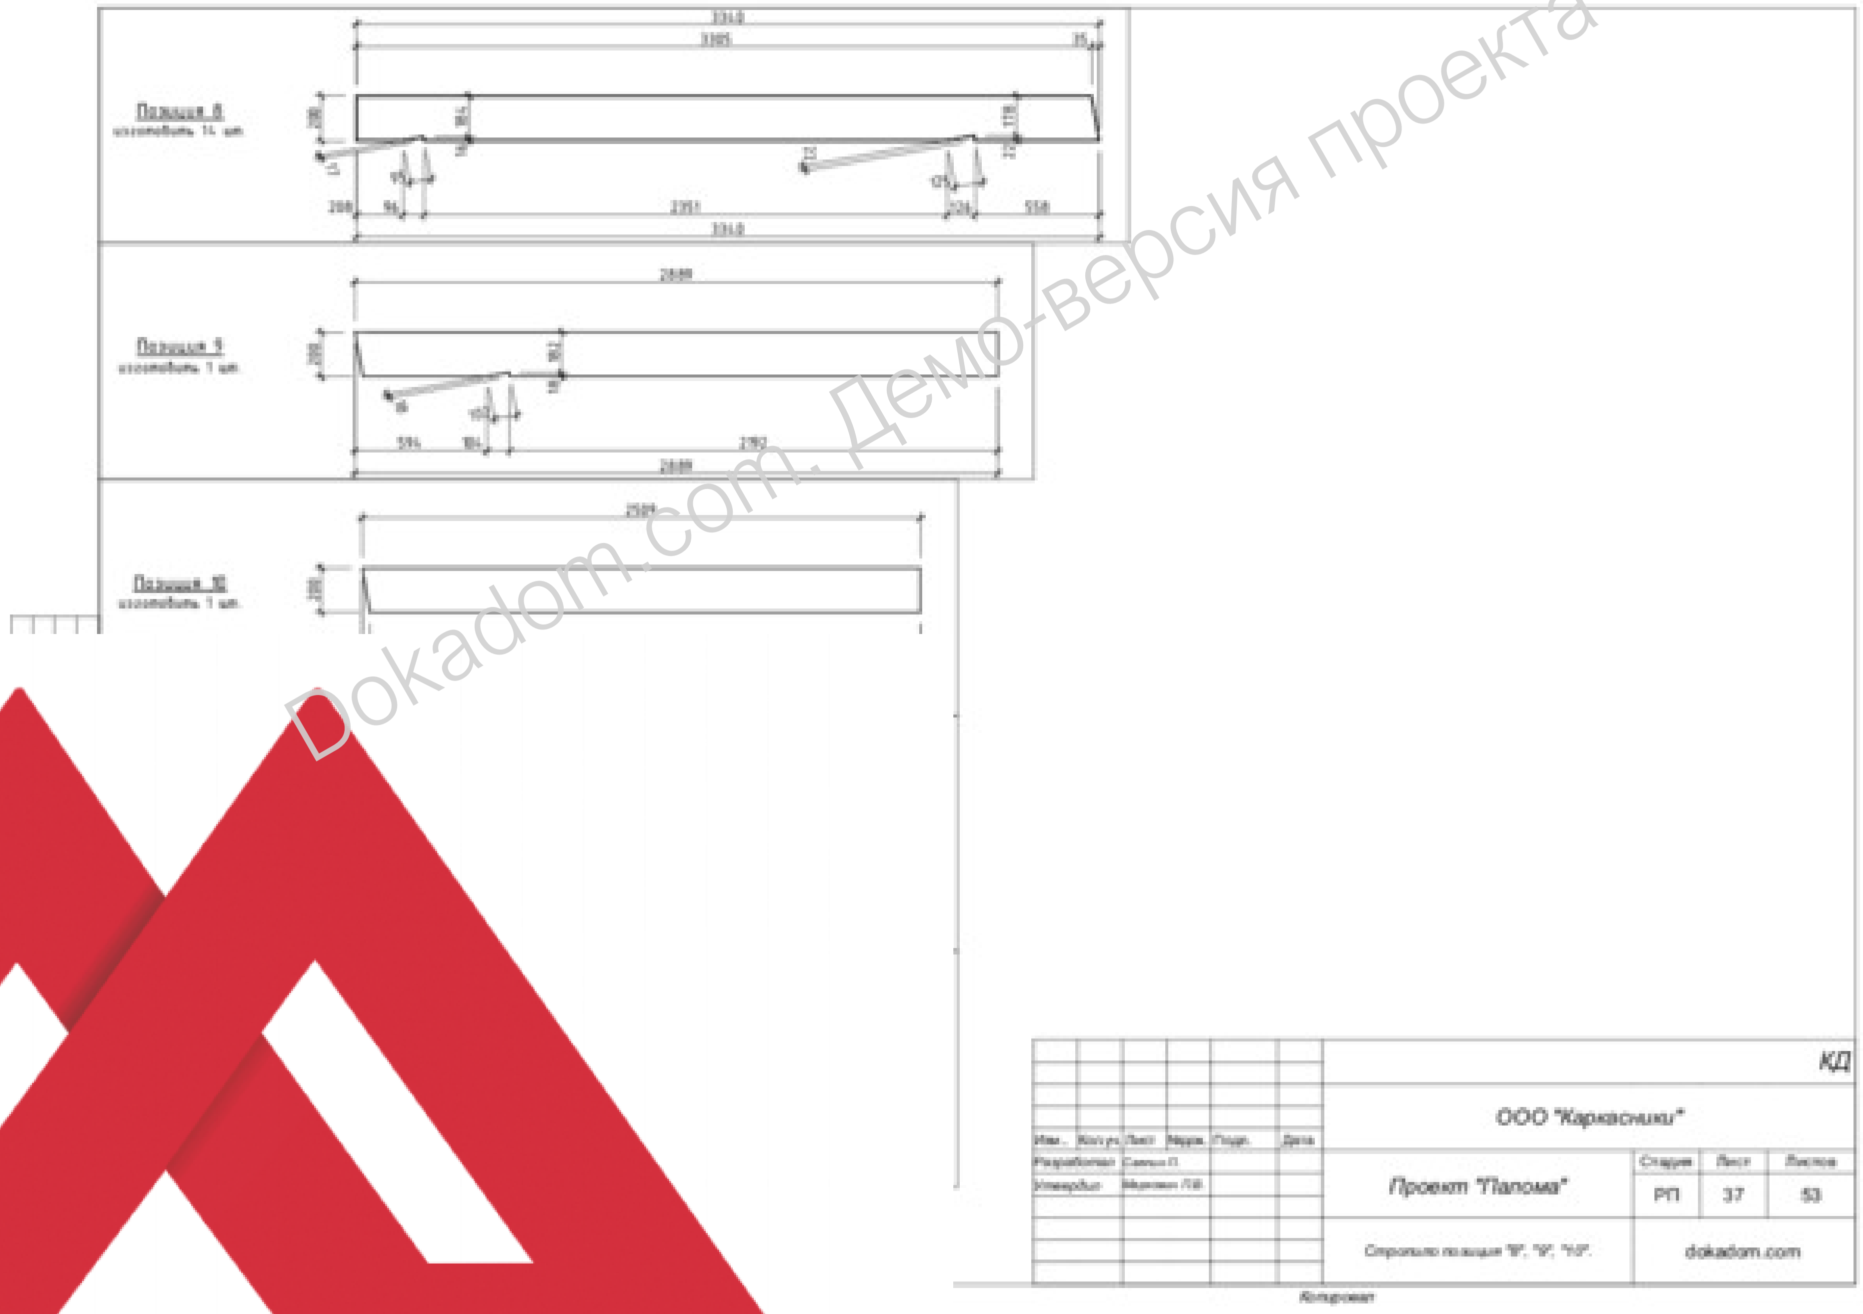

КД

ООО "Каркасники"

Изм.	Кол.уч.	Лист	№док.	Подп.	Дата
Разработал		Санько П.			
Утвердил		Миронов Л.В.			

Проект "Палома"

Стадия	Лист	Листов
РП	37	53

Стропила позиции "8", "9", "10".

dokadom.com

Копировал

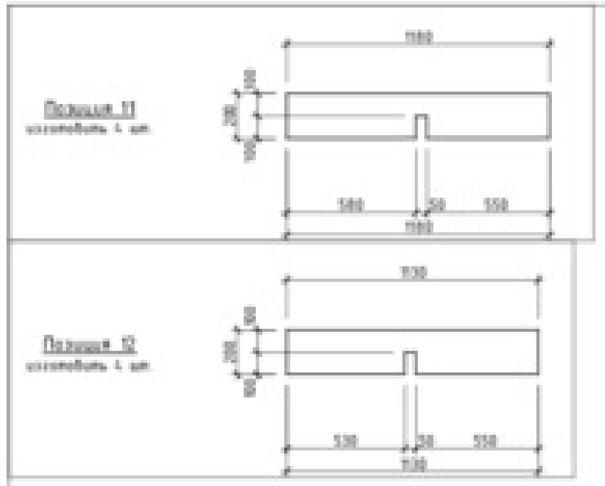

Изм.	Кол.уч.	Лист	№док.	Подп.	Дата
Разработал		Савиных П.			
Утвердил		Морозов П.В.			

КД

ООО "Каркасники"

Проект "Палома"

Стадия	Лист	Листов
РП	38	53

Стропила позиции "11", "12".

dokadom.com

Копировал

РАЗРЕЗ А-А. М 1:50.

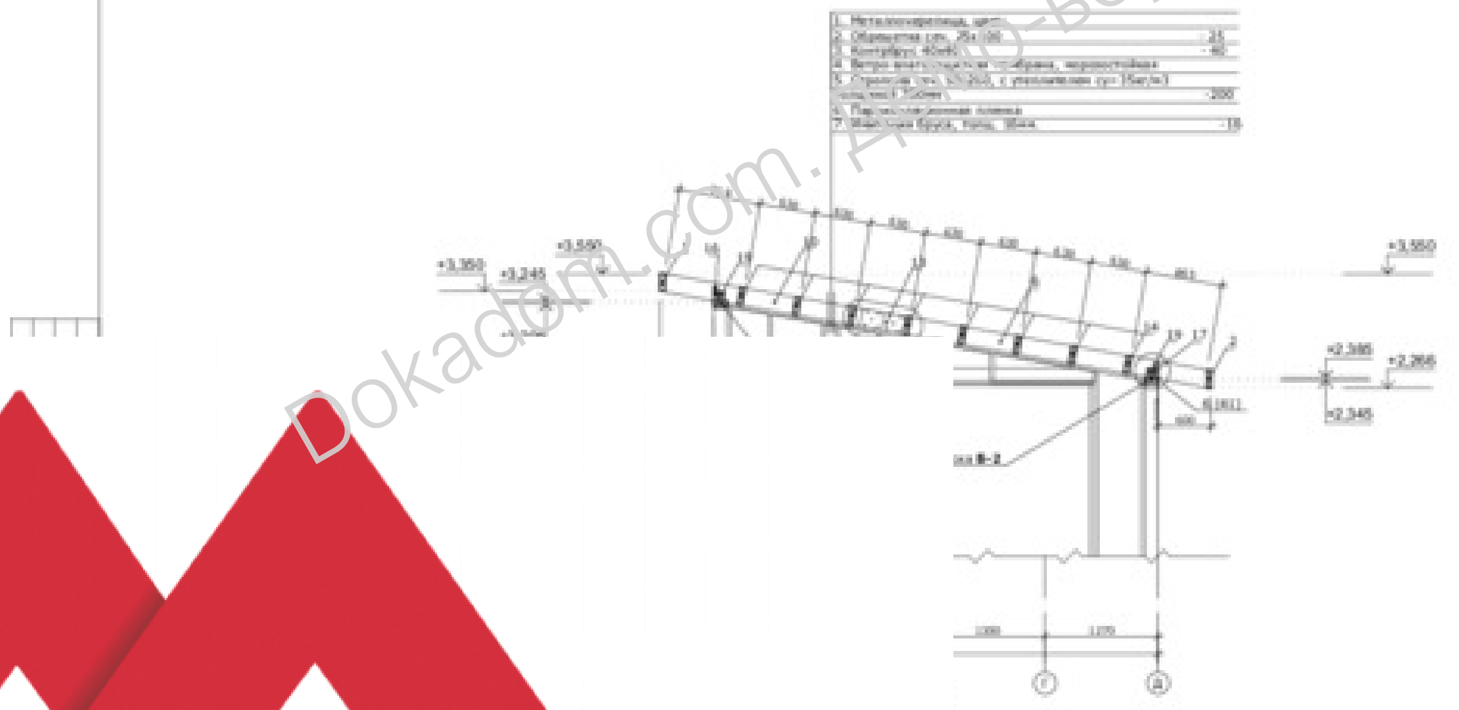
1. Металлочерепица, цвет
2. Обрешетка сеч. 25х100 - 25
3. Контрбрус 40х40 - 40
4. Ветро-влагозащитная мембрана, негорючестойкая
5. Стропила сеч. 50х200, с утеплением сут 35кг/м3
толщиной 200мм - 200
6. Пароизоляционная пленка
7. Имитация бруса, толщ. 18мм - 18
+3,350
+3,245
+3,550
+3,550
+2,385
+2,266
+2,345
1200
1270
Г
Д

Изм.	Кол.уч.	Лист	№док.	Подп.	Дата
Разработал		Савиных П.			
Утвердил		Марченко Л.В.			

КД

ООО "Каркасники"

Проект "Палома"

Стадия	Лист	Листов
РП	39	53

Разрез А-А. М 1:50

dokadom.com

Копировал

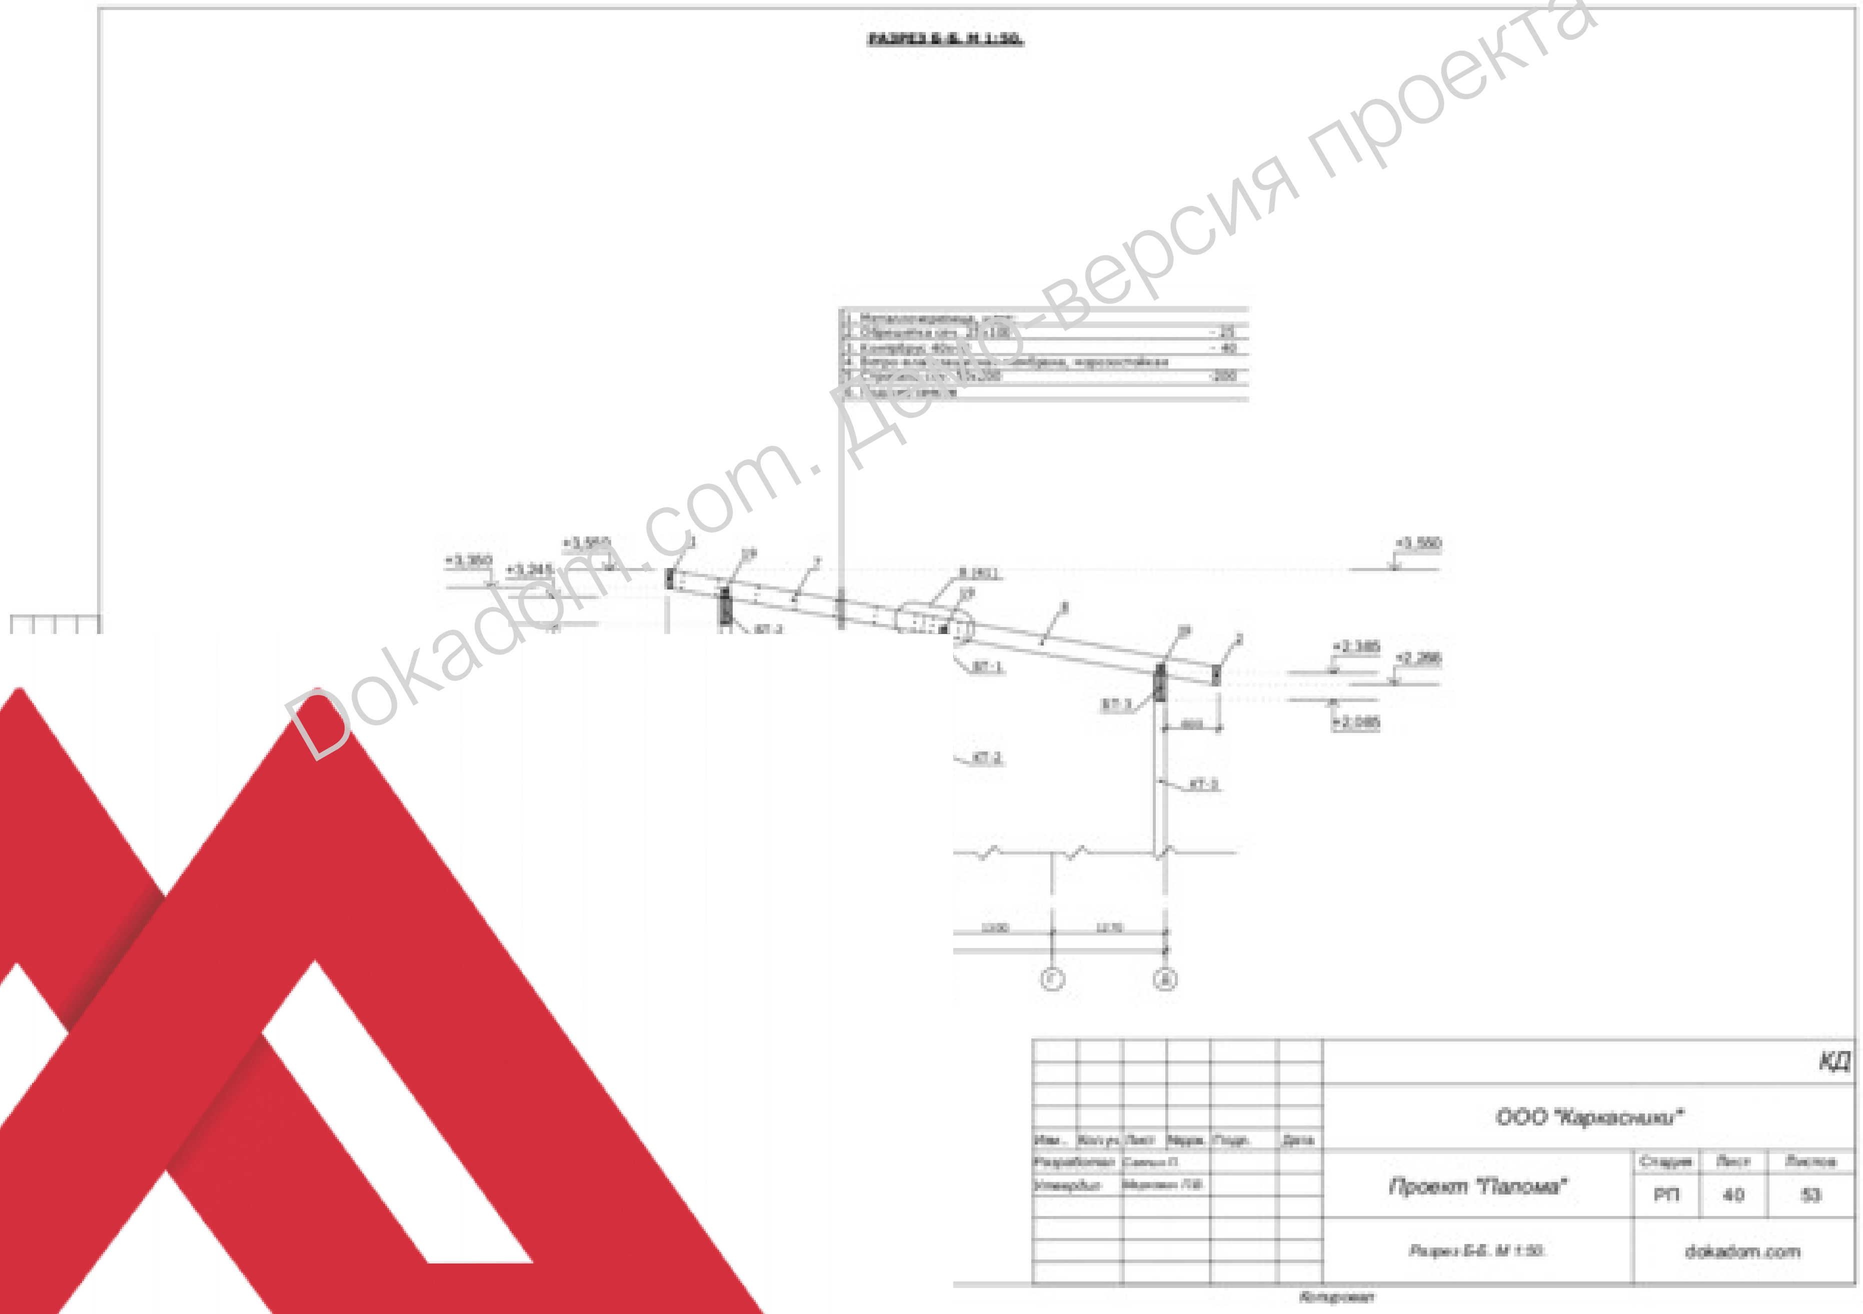
РАЗРЕЗ Б-Б. М 1:50.
+3,350
+3,245
+3,560
+3,550
+2,385
+2,288
+2,085
ВТ-2
ВТ-1
КТ-2
КТ-1
1300
1270
Г
Д
КД
ООО "Каркасники"
Изм.
Кол.уч.
Лист
№док.
Подп.
Дата
Разработал
Утвердил
Проект "Палома"
Стадия
Лист
Листов
РП
40
53
Разрез Б-Б. М 1:50.
dokadom.com
Копировал

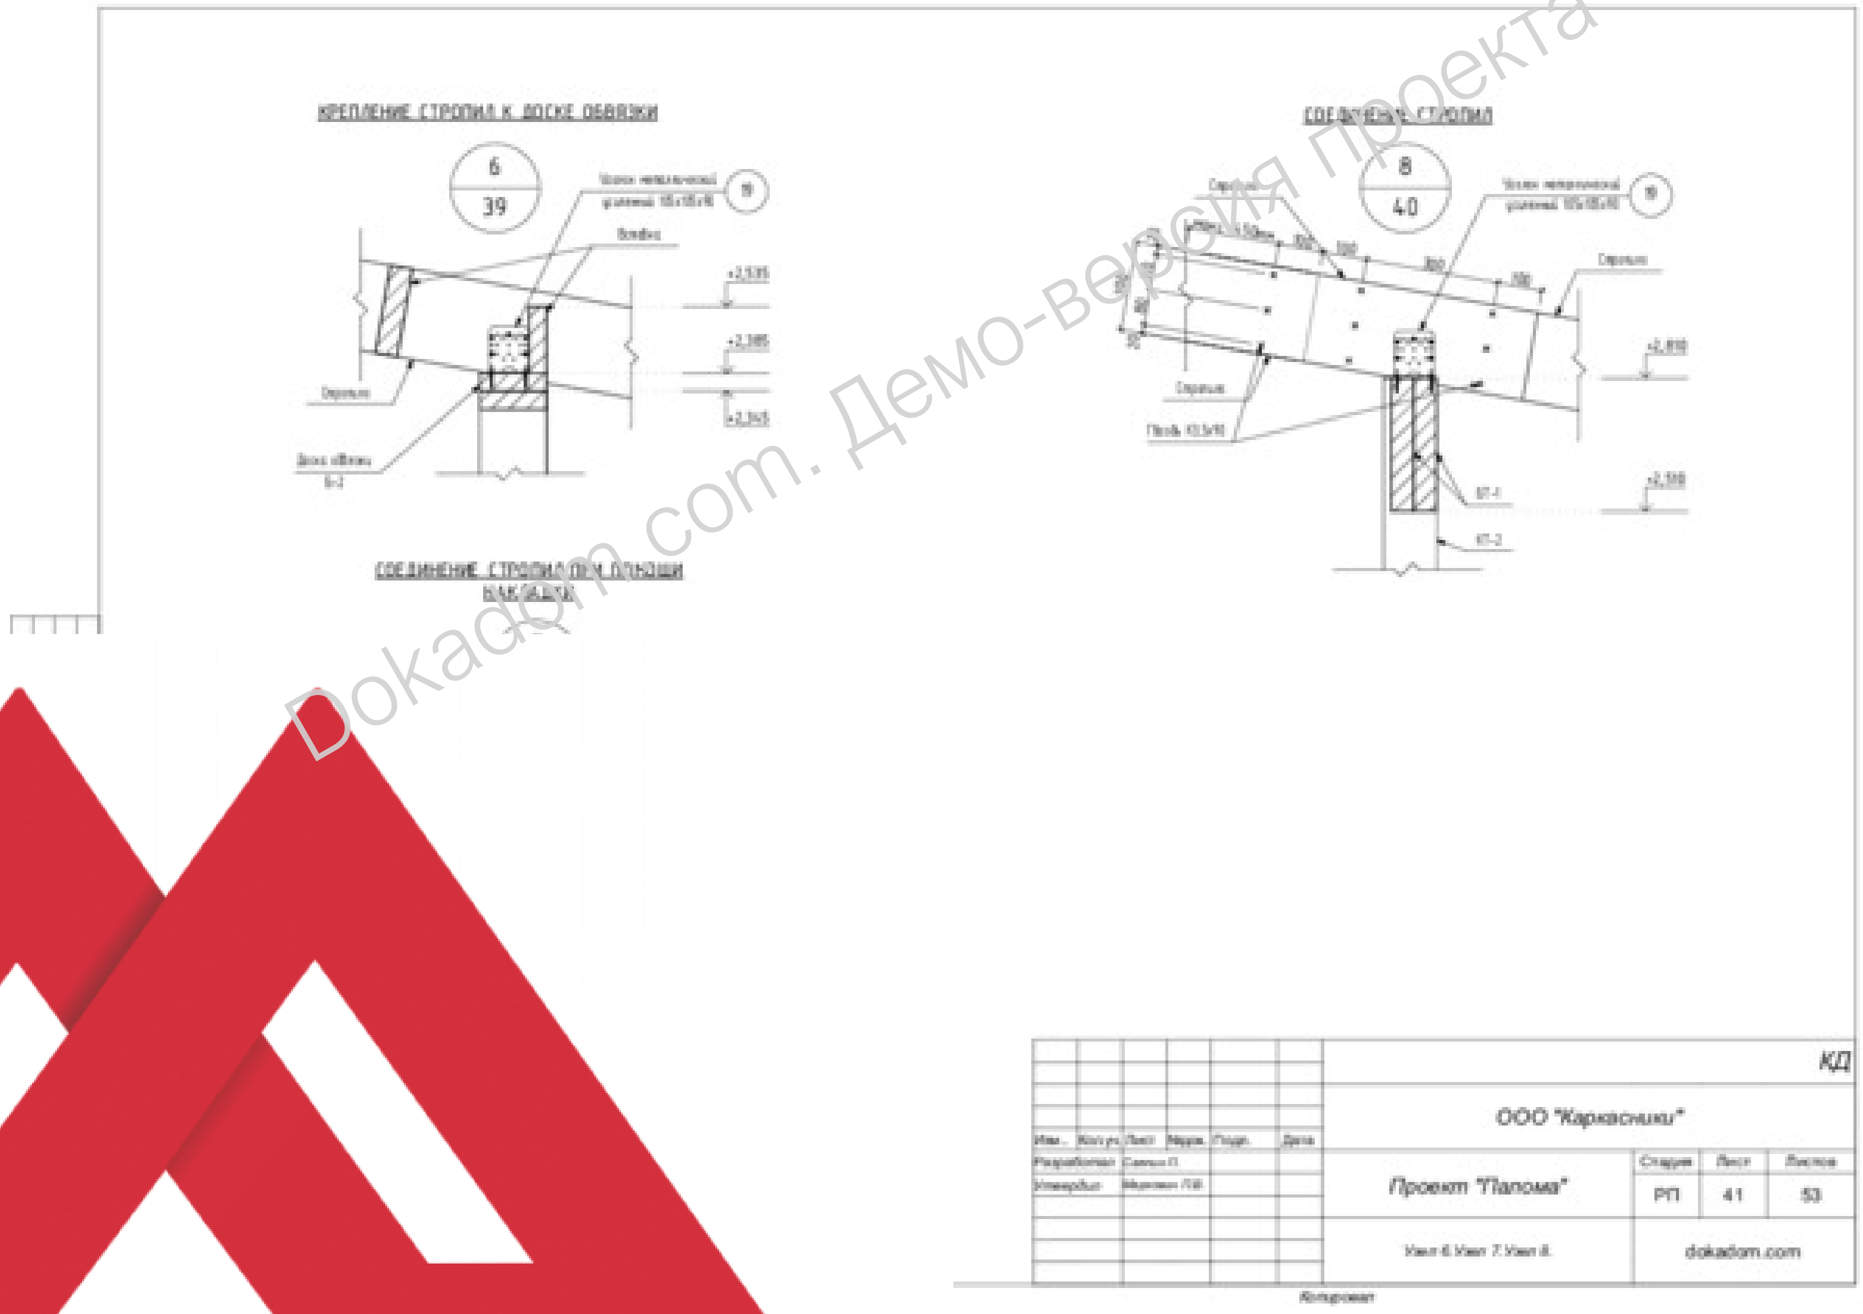
КРЕПЛЕНИЕ СТРОПИЛ К ДОСКЕ ОБВЯЗКИ
6
39
Уголок металлический усиленный 105х105х90
19
Вставка
Стропило
Доска обвязки
+2,535
+2,385
+2,345
СОЕДИНЕНИЕ СТРОПИЛ ПРИ ПОМОЩИ НАКЛАДКИ
СОЕДИНЕНИЕ СТРОПИЛ
8
40
Уголок металлический усиленный 105х105х90
19
Стропило
Гвоздь 4,0х90
БТ-1
БТ-2
+2,810
+2,550
КД
ООО "Каркасники"
Изм.
Кол.уч.
Лист
№док.
Подп.
Дата
Разработал
Утвердил
Проект "Палома"
Стадия
Лист
Листов
РП
41
53
Узел 6. Узел 7. Узел 8.
dokadom.com
Копировал

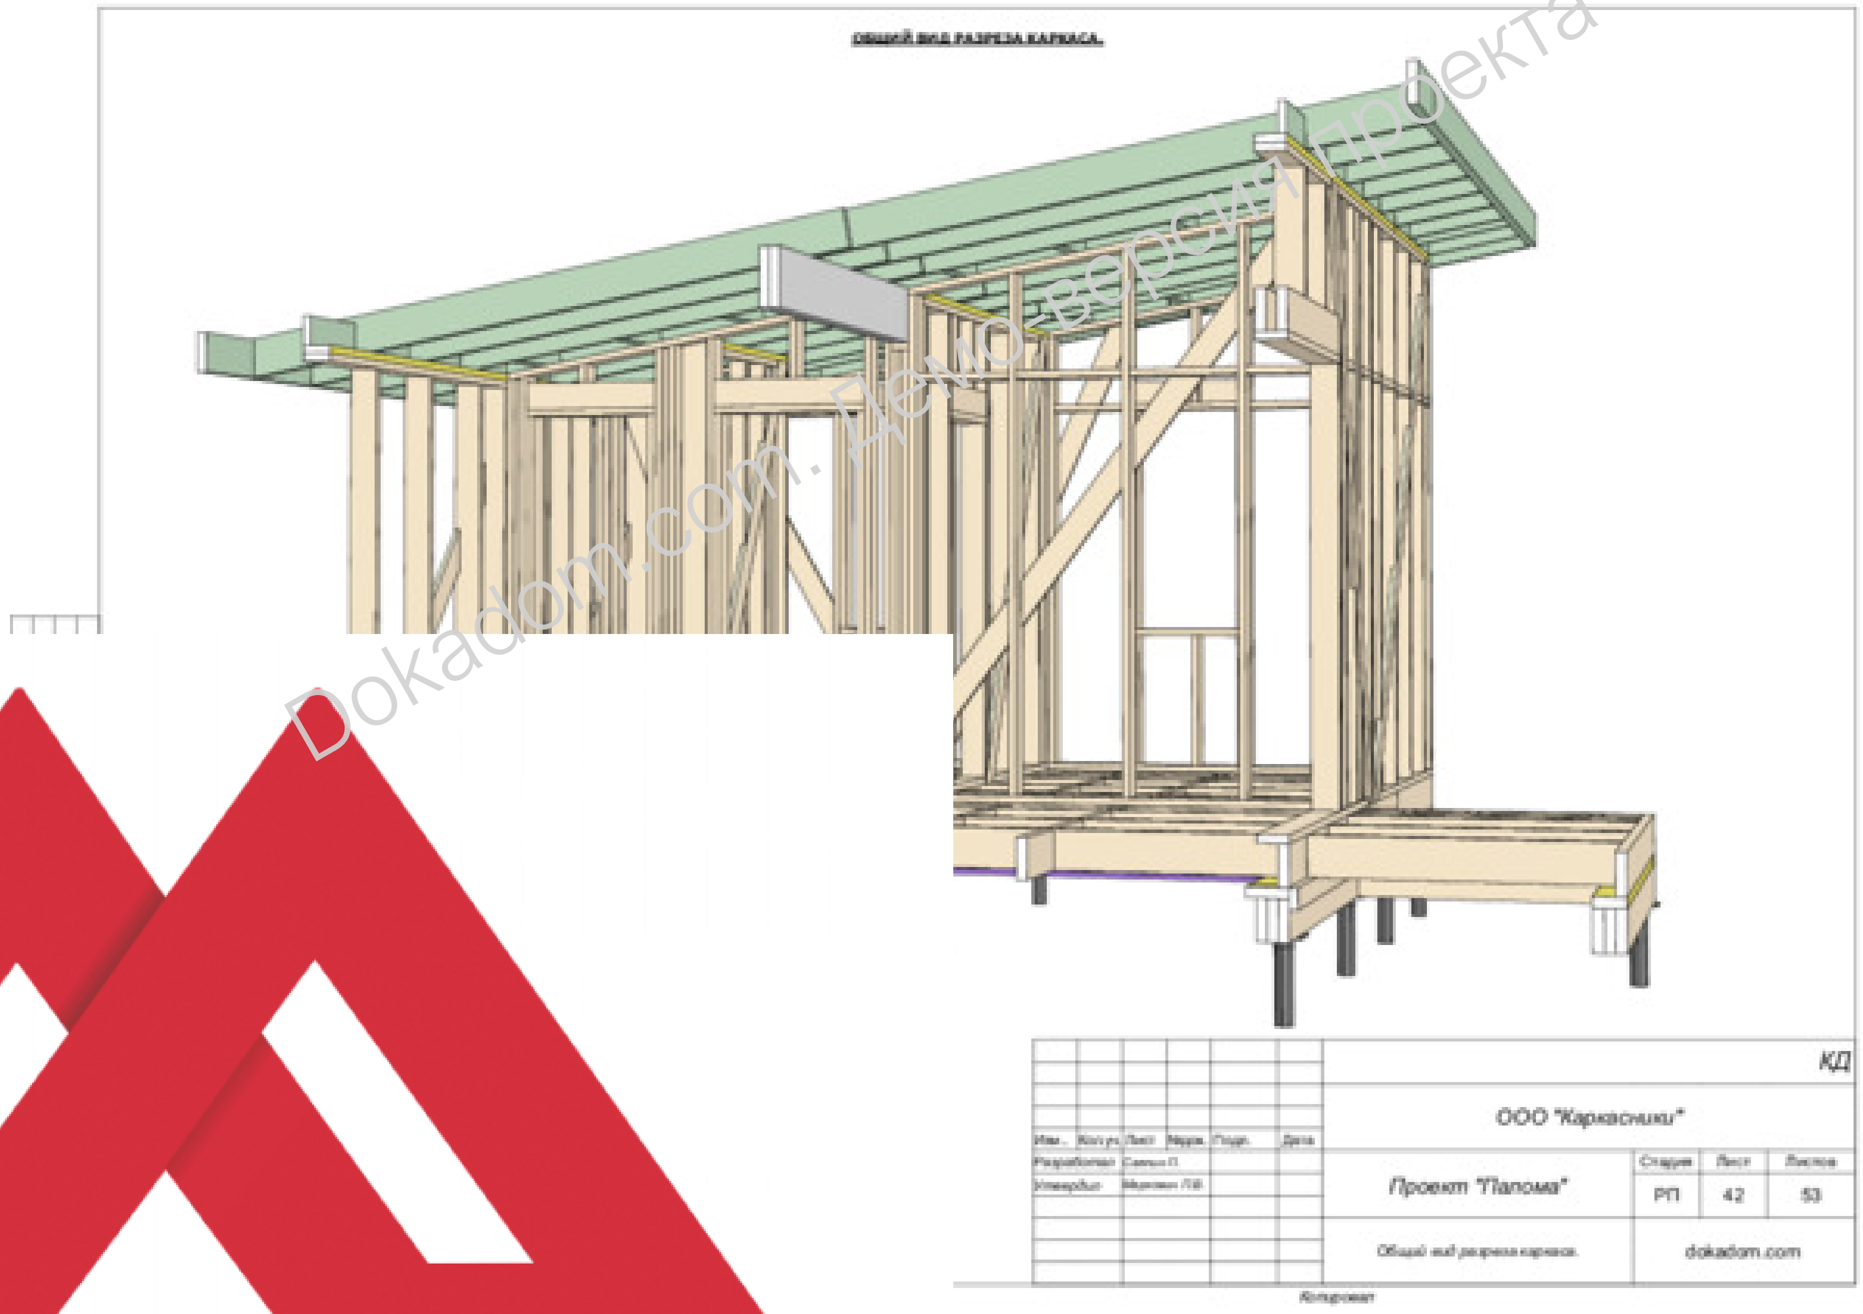

ОБЩИЙ ВИД РАЗРЕЗА КАРКАСА.

КД

ООО "Каркасники"

Изм.	Кол.уч.	Лист	№док.	Подп.	Дата
Разработал					
Утвердил					

Проект "Палома"

Стадия	Лист	Листов
РП	42	53

Общий вид разреза каркаса.

dokadom.com

Копировал

DOKADOM.COM

ДЕМО-ВЕРСИЯ ПРОЕКТА

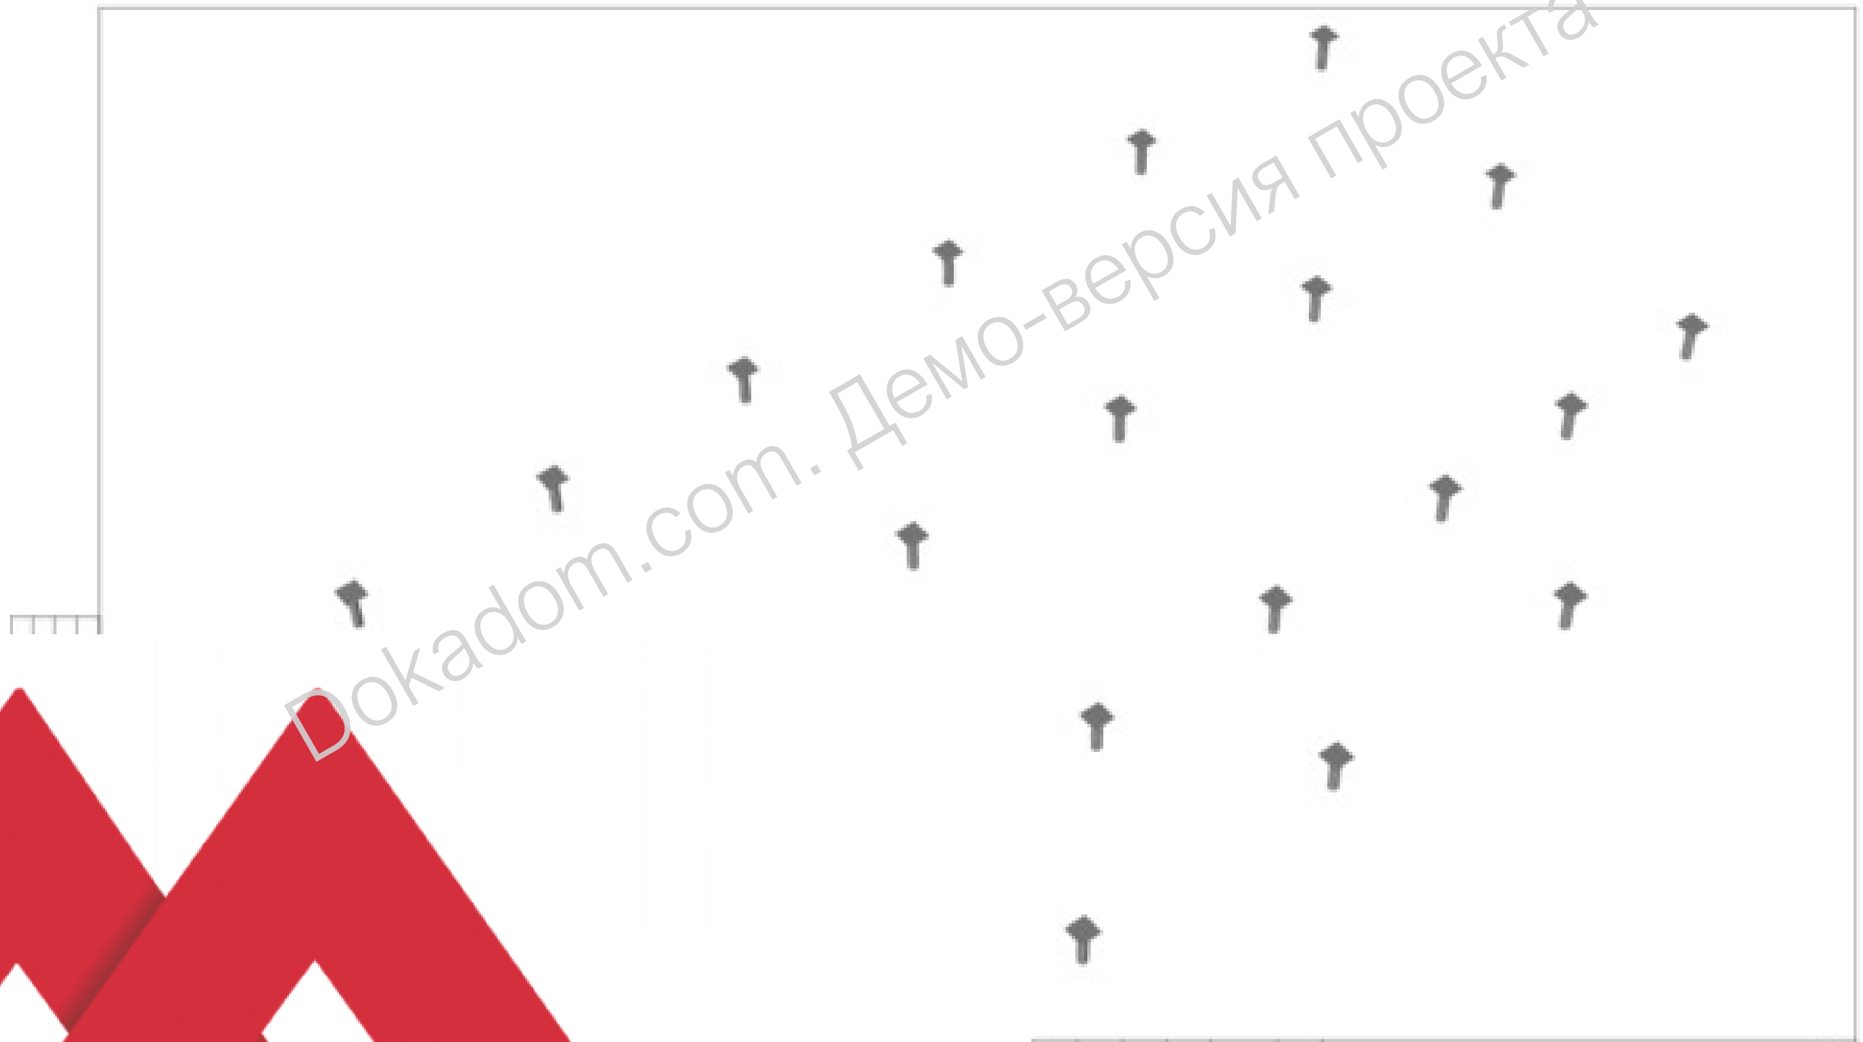

Изм.	Кол.уч.	Лист	№док.	Подп.	Дата
Разработал		Смелых П.			
Утвердил		Миронов П.В.			

КД

ООО "Каркасники"

Проект "Палома"

Стадия	Лист	Листов
РП	43	53

Общий вид свайного поля.

dokadom.com

Копировал

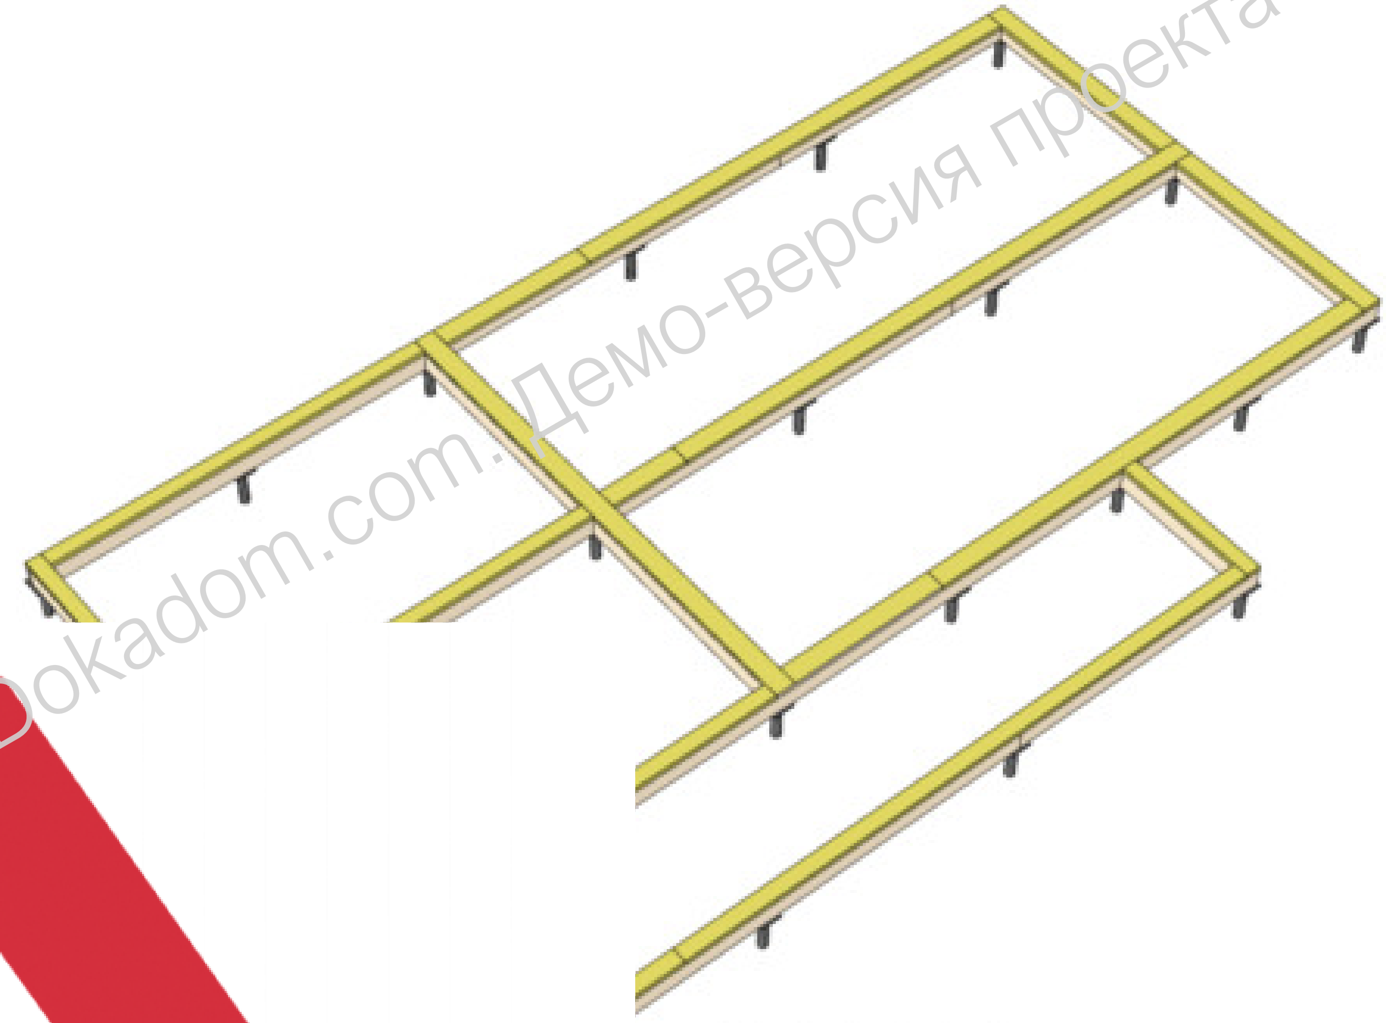

						КД
						ООО "Каркасники"
Изм.	Кол.уч.	Лист	№док.	Подп.	Дата	
Разработал		Савин П.				Проект "Палома"
Утвердил		Миронов Л.В.				

Стадия	Лист	Листов
РП	44	53

Общий вид бруса обвязки.

dokadom.com

Копировал

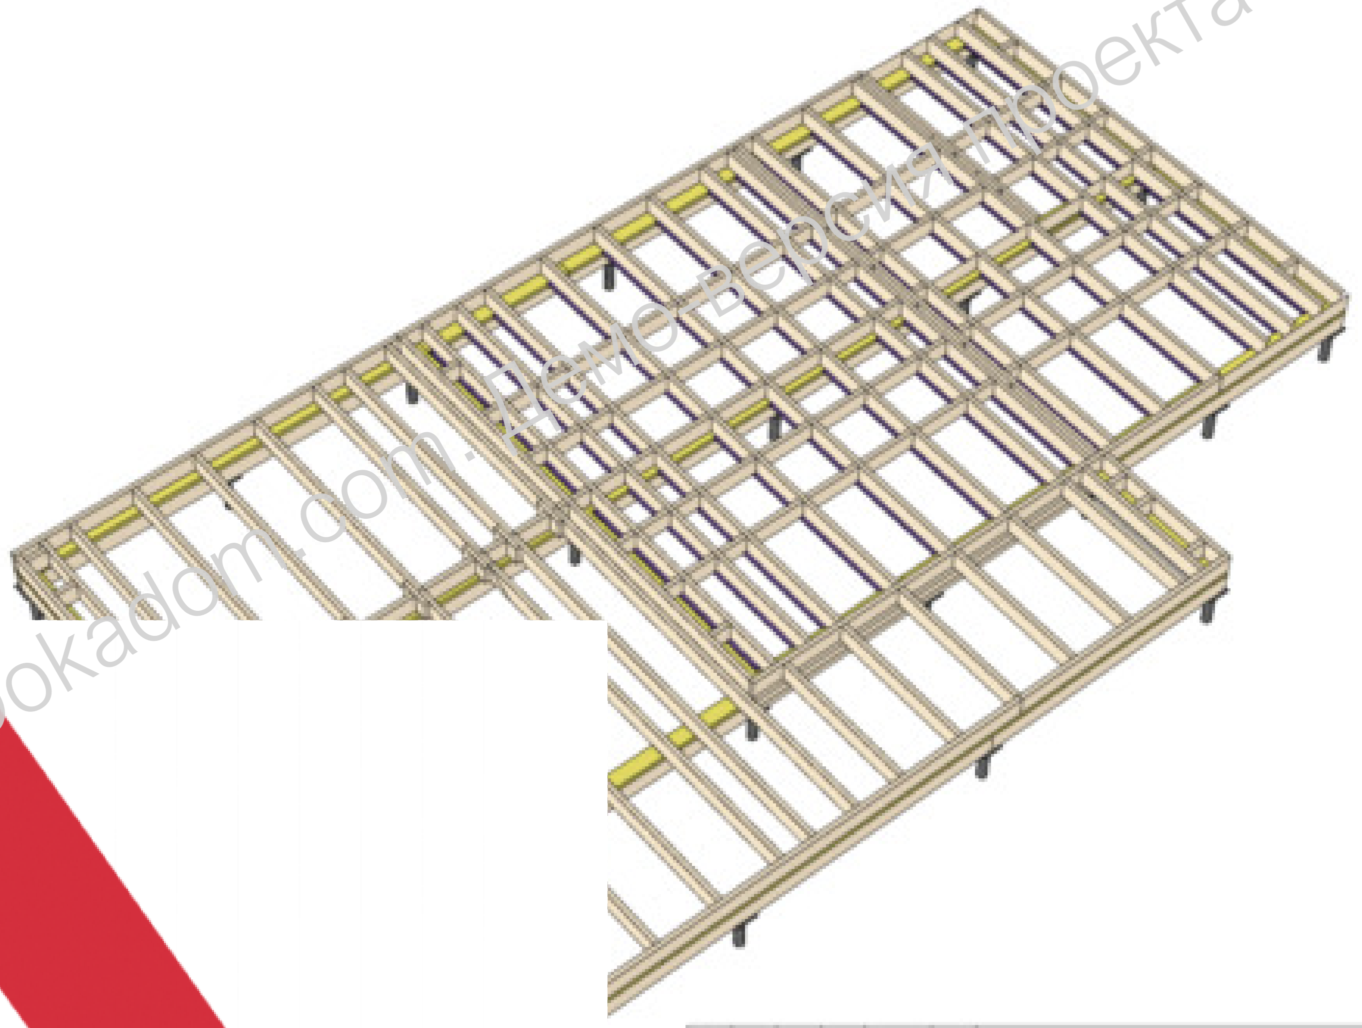

КД

ООО "Каркасники"

Изм.	Кол.уч	Лист	№док.	Подп.	Дата
Разработал	[illegible]				
Утвердил	[illegible]				

Проект "Палома"

Стадия	Лист	Листов
РП	45	53

Общий вид перекрытия 1-го этажа.

dokadom.com

Копировал

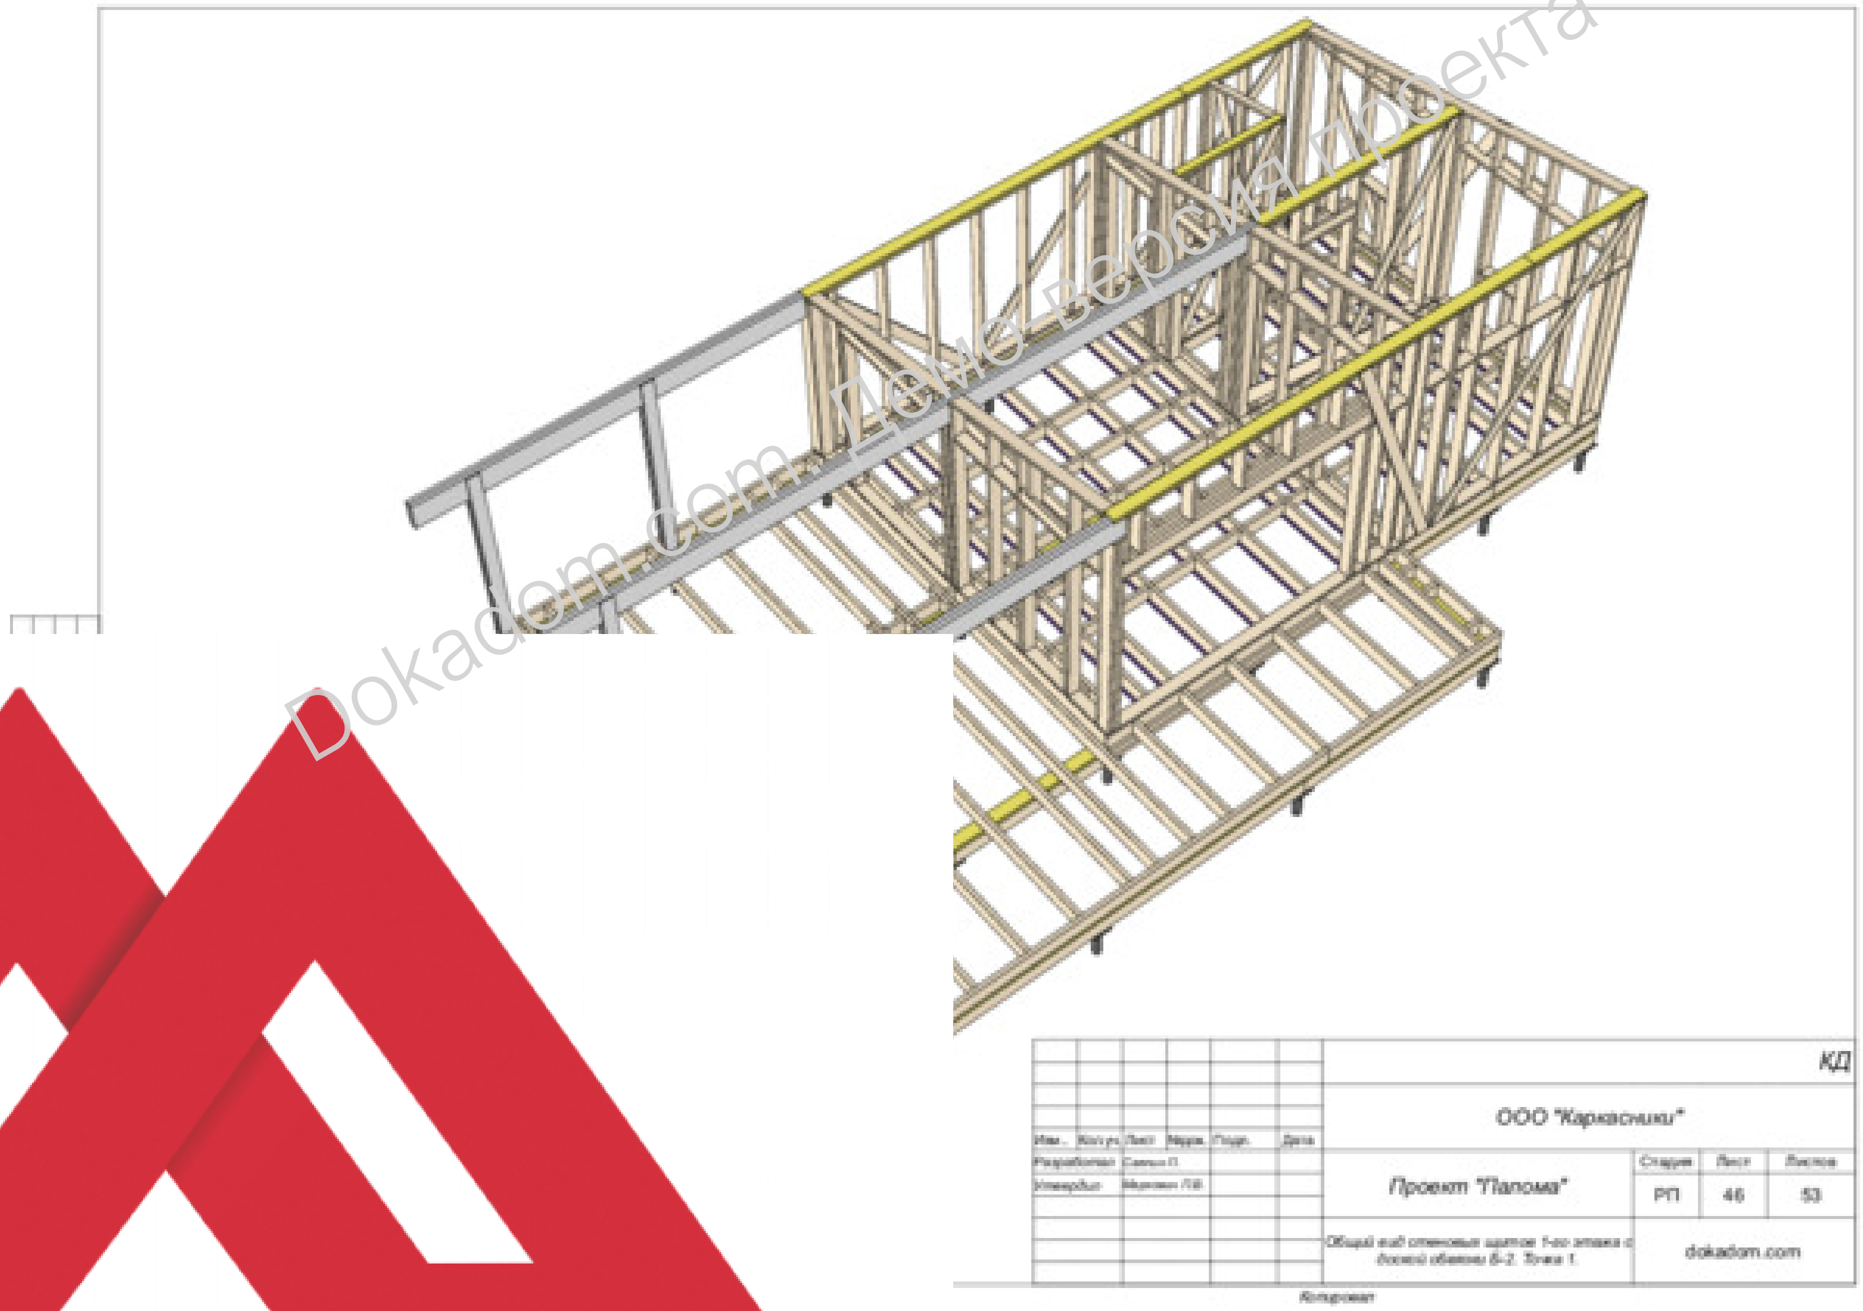

КД

ООО "Каркасники"

Изм.	Кол.уч.	Лист	№док.	Подп.	Дата
Разработал					
Утвердил					

Проект "Палома"

Стадия	Лист	Листов
РП	46	53

Общий вид стеновых щитов 1-го этажа с доской обвязки Б-2. Точка 1.

dokadom.com

Копировал

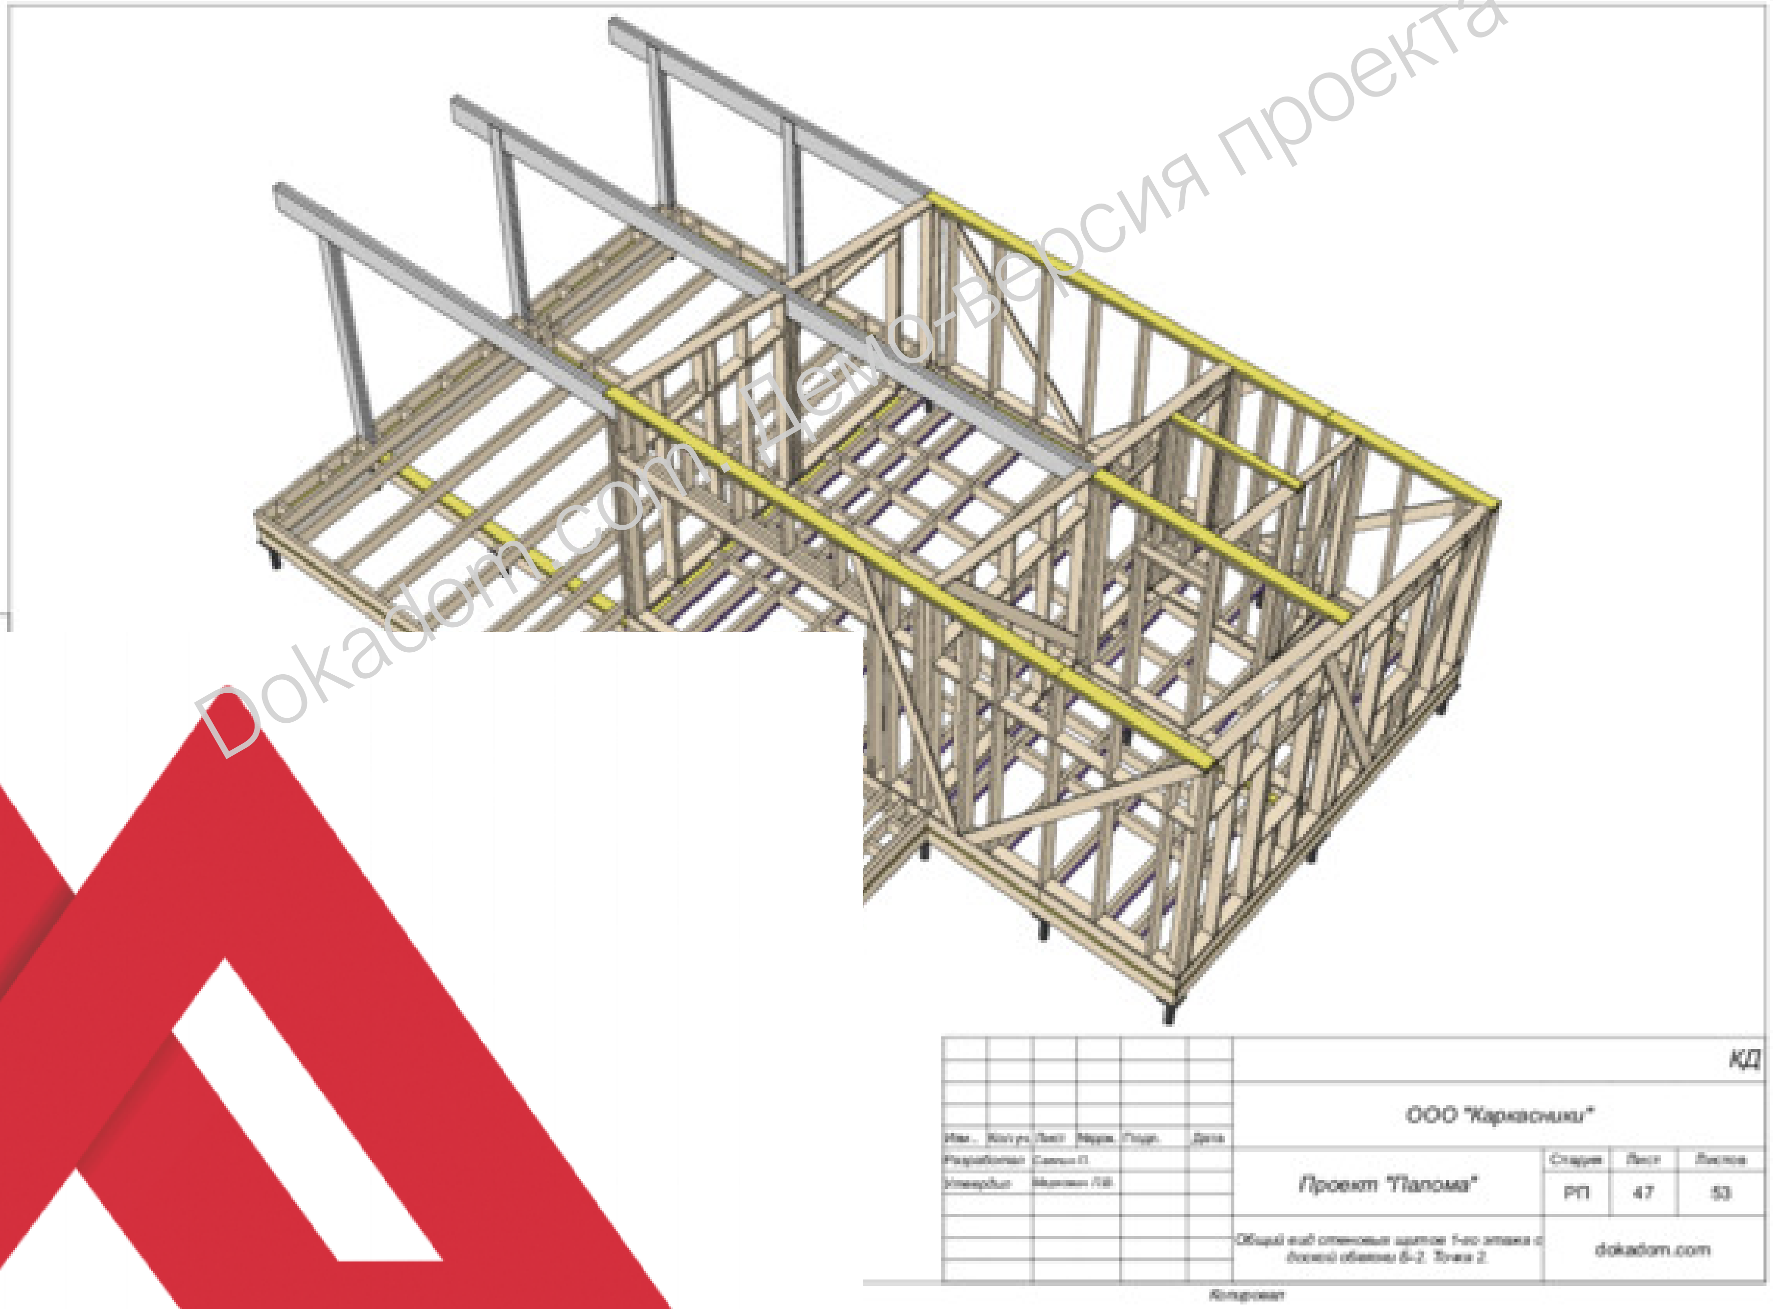

КД

ООО "Каркасники"

Изм.	Кол.уч.	Лист	№док.	Подп.	Дата
Разработал		Санько П.			
Утвердил		Миронов Л.В.			

Проект "Палома"

Стадия	Лист	Листов
РП	47	53

Общий вид стеновых щитов 1-го этажа с доской обвязки Б-2. Точка 2.

dokadom.com

Копировал

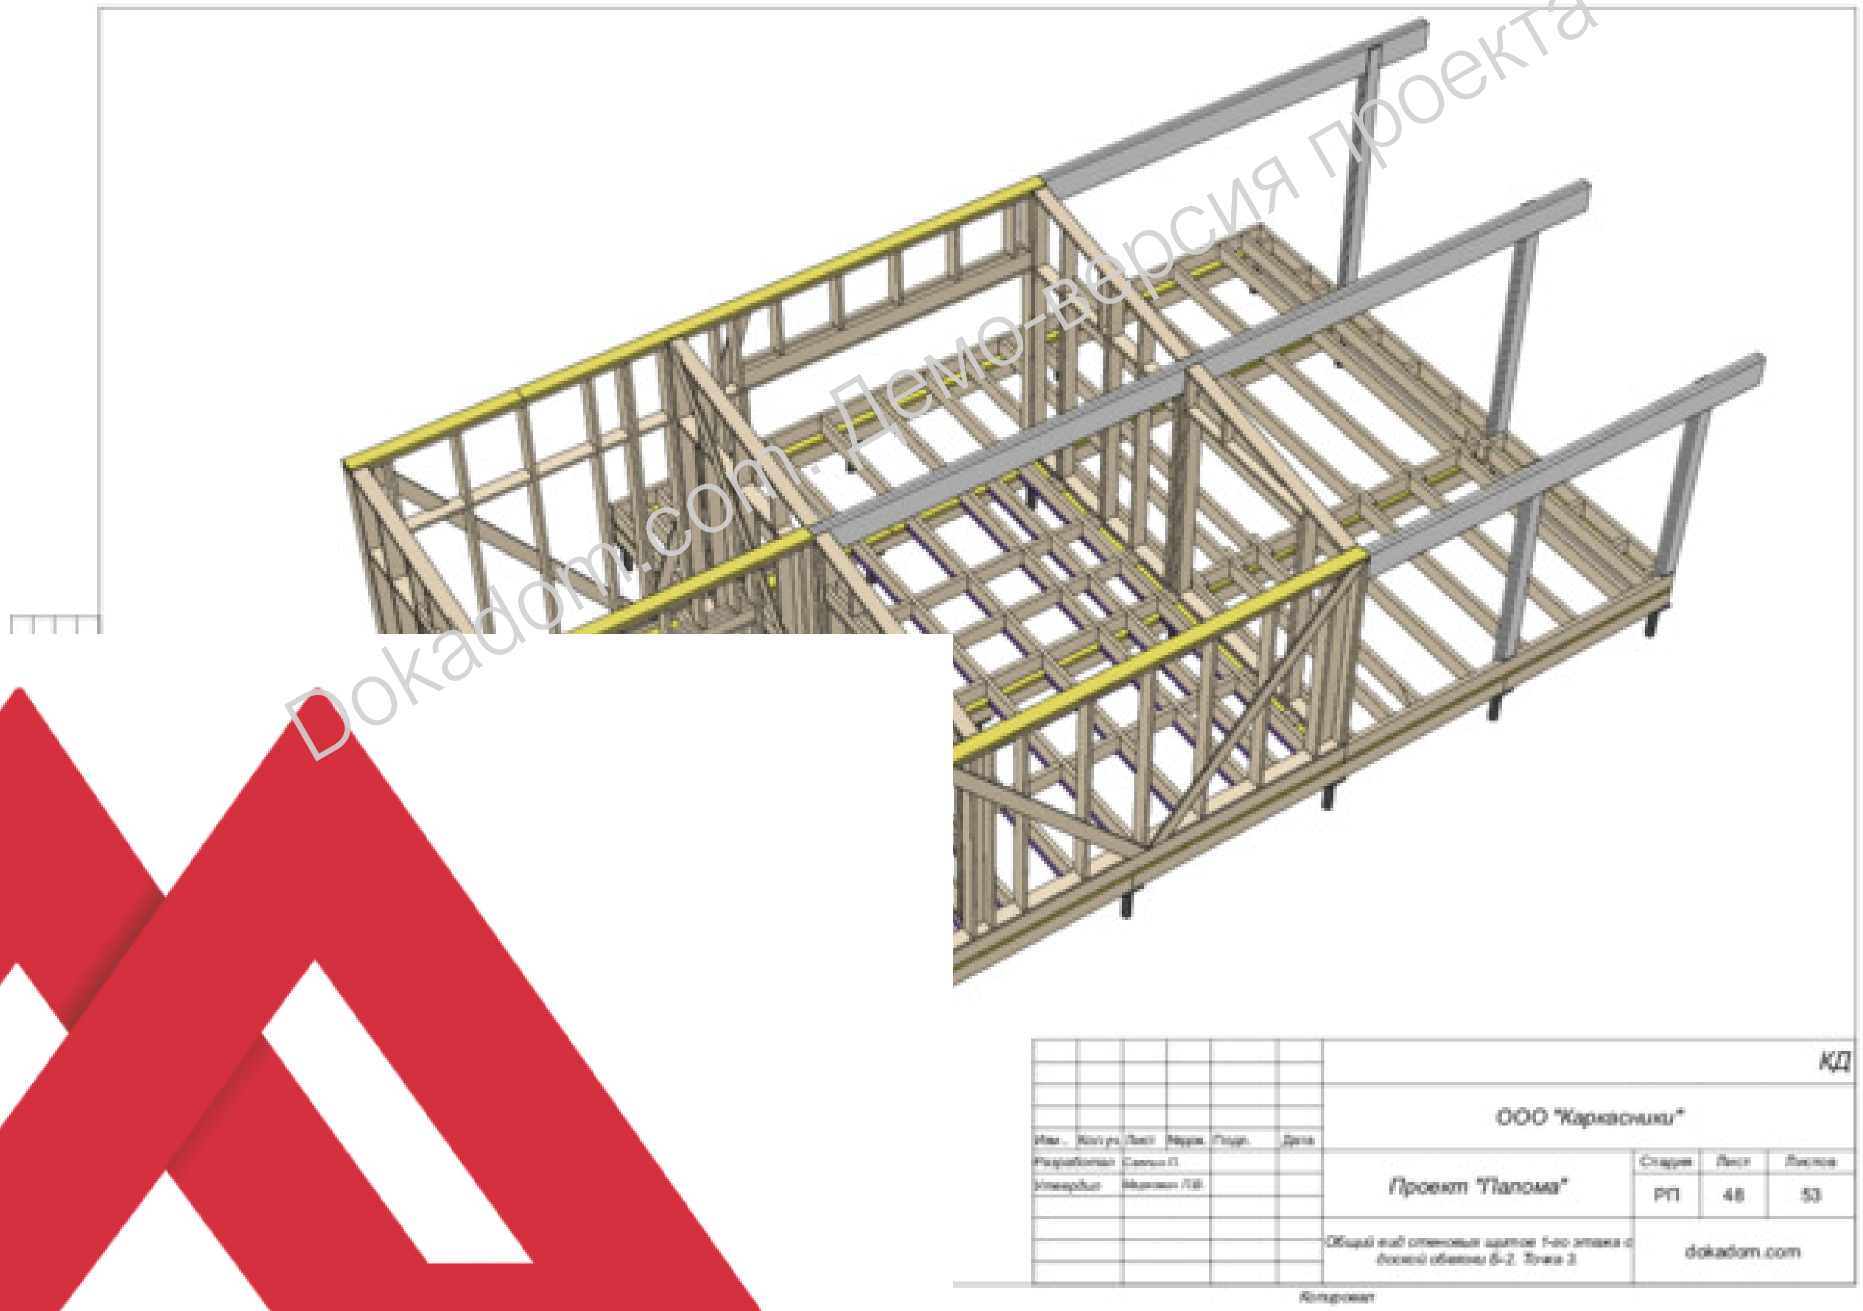

КД

ООО "Каркасники"

Проект "Палома"

Стадия	Лист	Листов
РП	48	53

Общий вид стеновых щитов 1-го этажа с доской обвязки Б-2. Точка 3.

dokadom.com

Изм.	Кол.уч.	Лист	№док.	Подп.	Дата
Разработал		Савин П.			
Утвердил					

Копировал

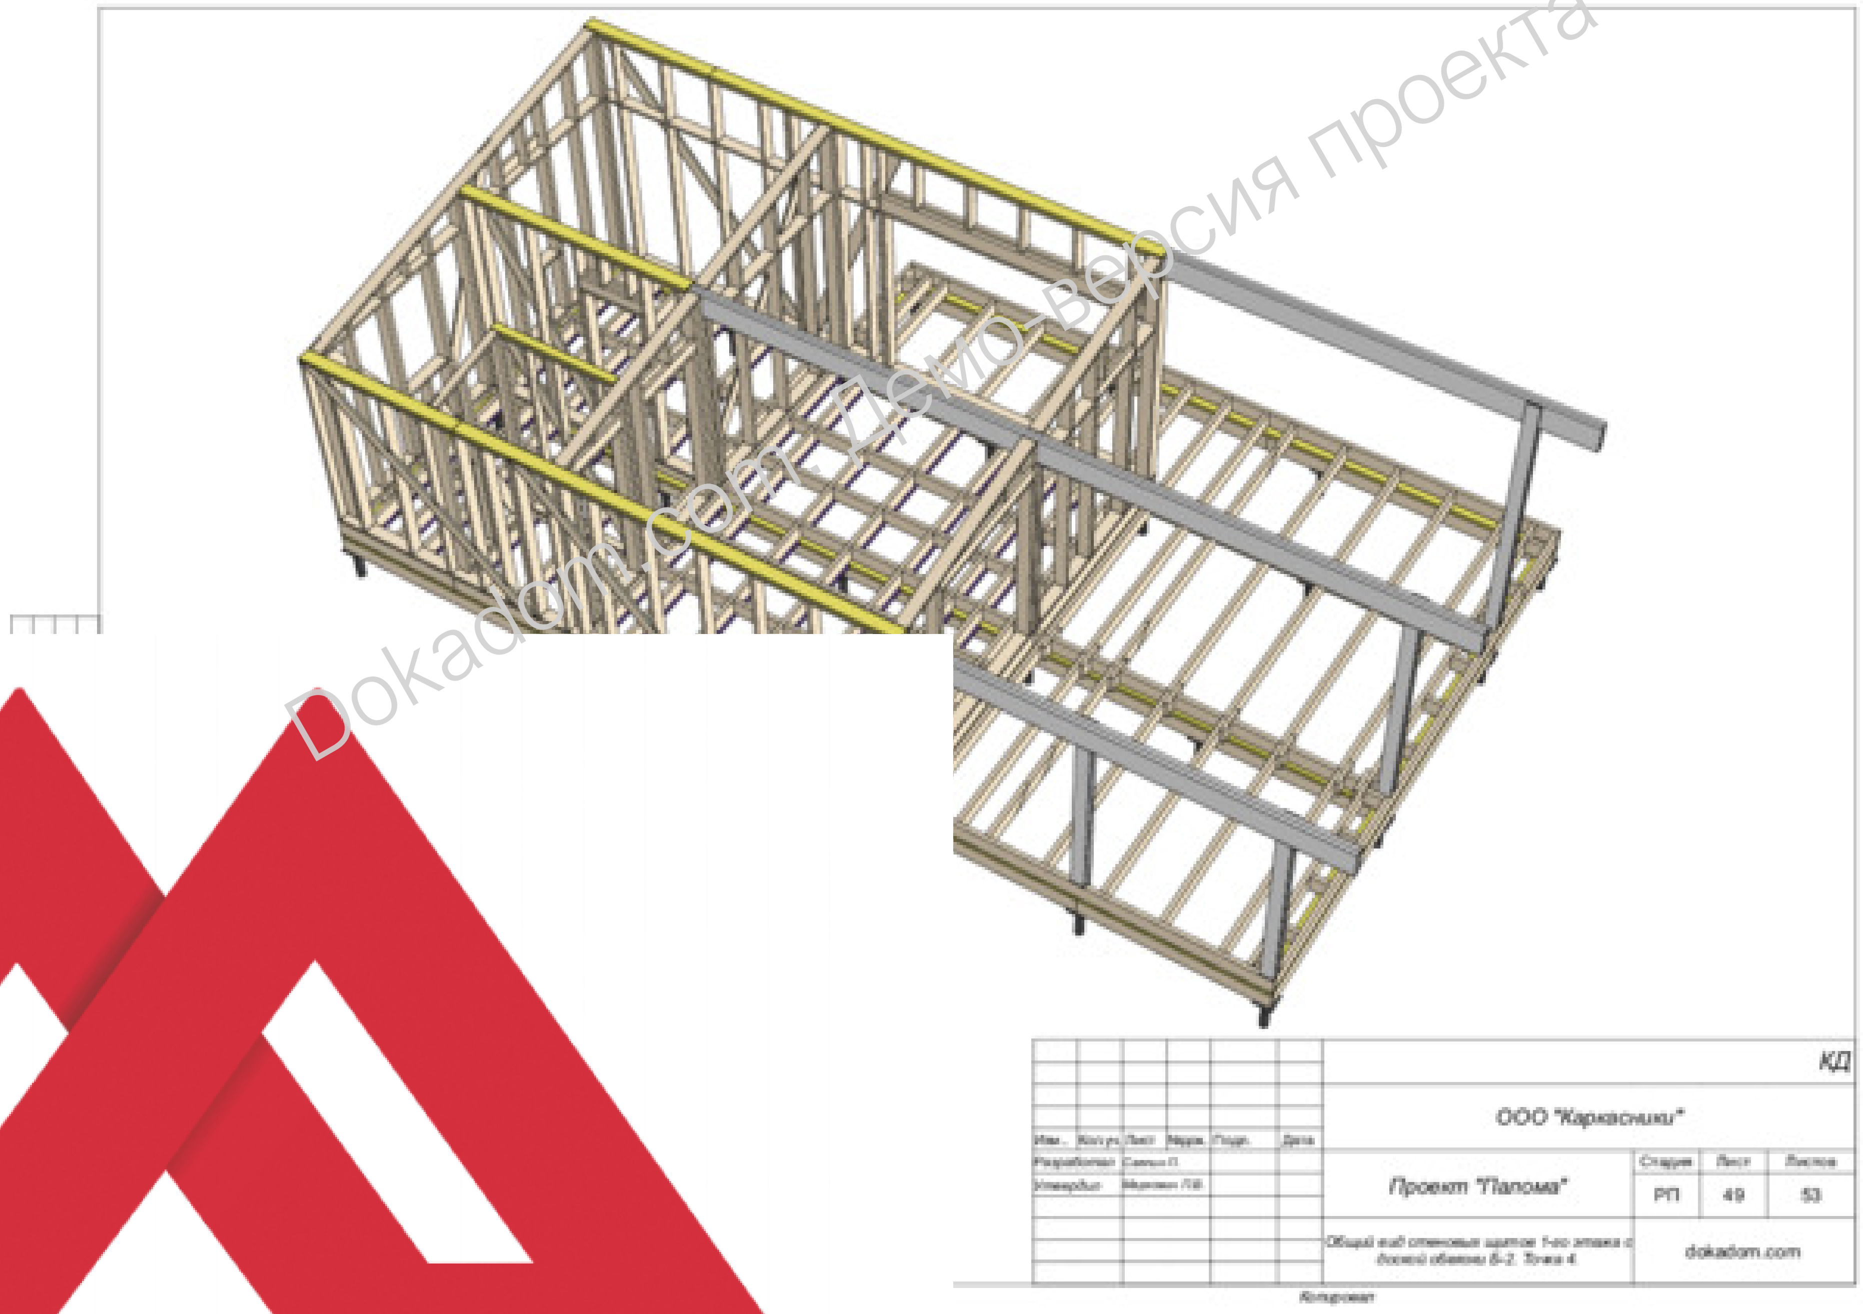

КД

ООО "Каркасники"

Проект "Палома"

Стадия	Лист	Листов
РП	49	53

Общий вид стеновых щитов 1-го этажа с доской обвязки Б-2. Точка 4.

dokadom.com

Изм. | Кол.уч. | Лист | №док. | Подп. | Дата

Разработал

Утвердил

Копировал

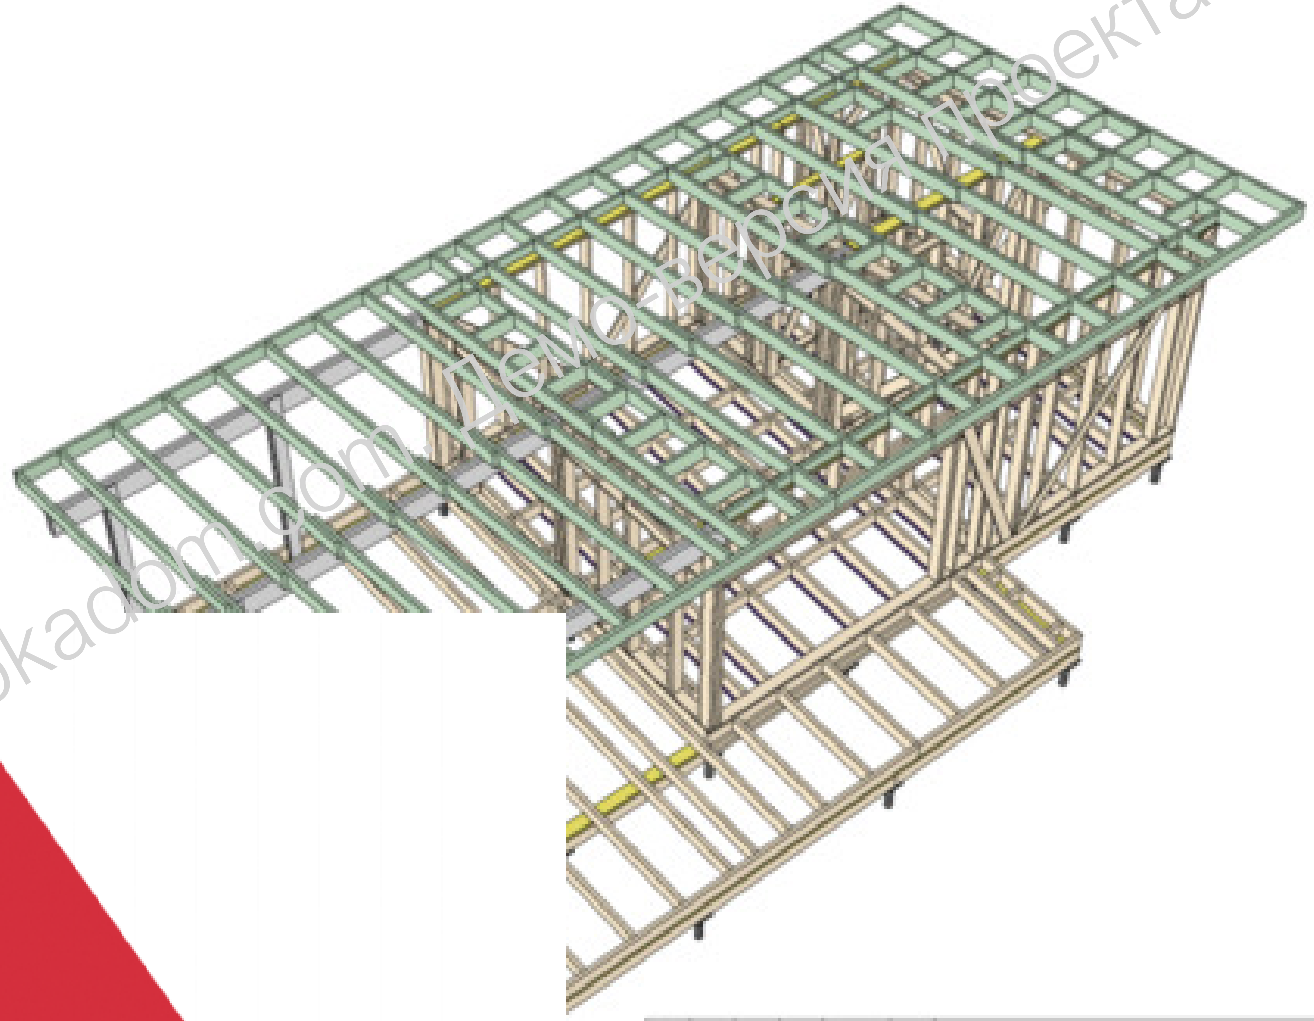

						КД
						ООО "Каркасники"
Изм.	Кол.уч.	Лист	№док.	Подп.	Дата	
Разработал	[illegible]					Проект "Палома"
Утвердил	[illegible]					

Стадия	Лист	Листов
РП	50	53

Общий вид стропильной системы. Точка 1

dokadom.com

Копировал

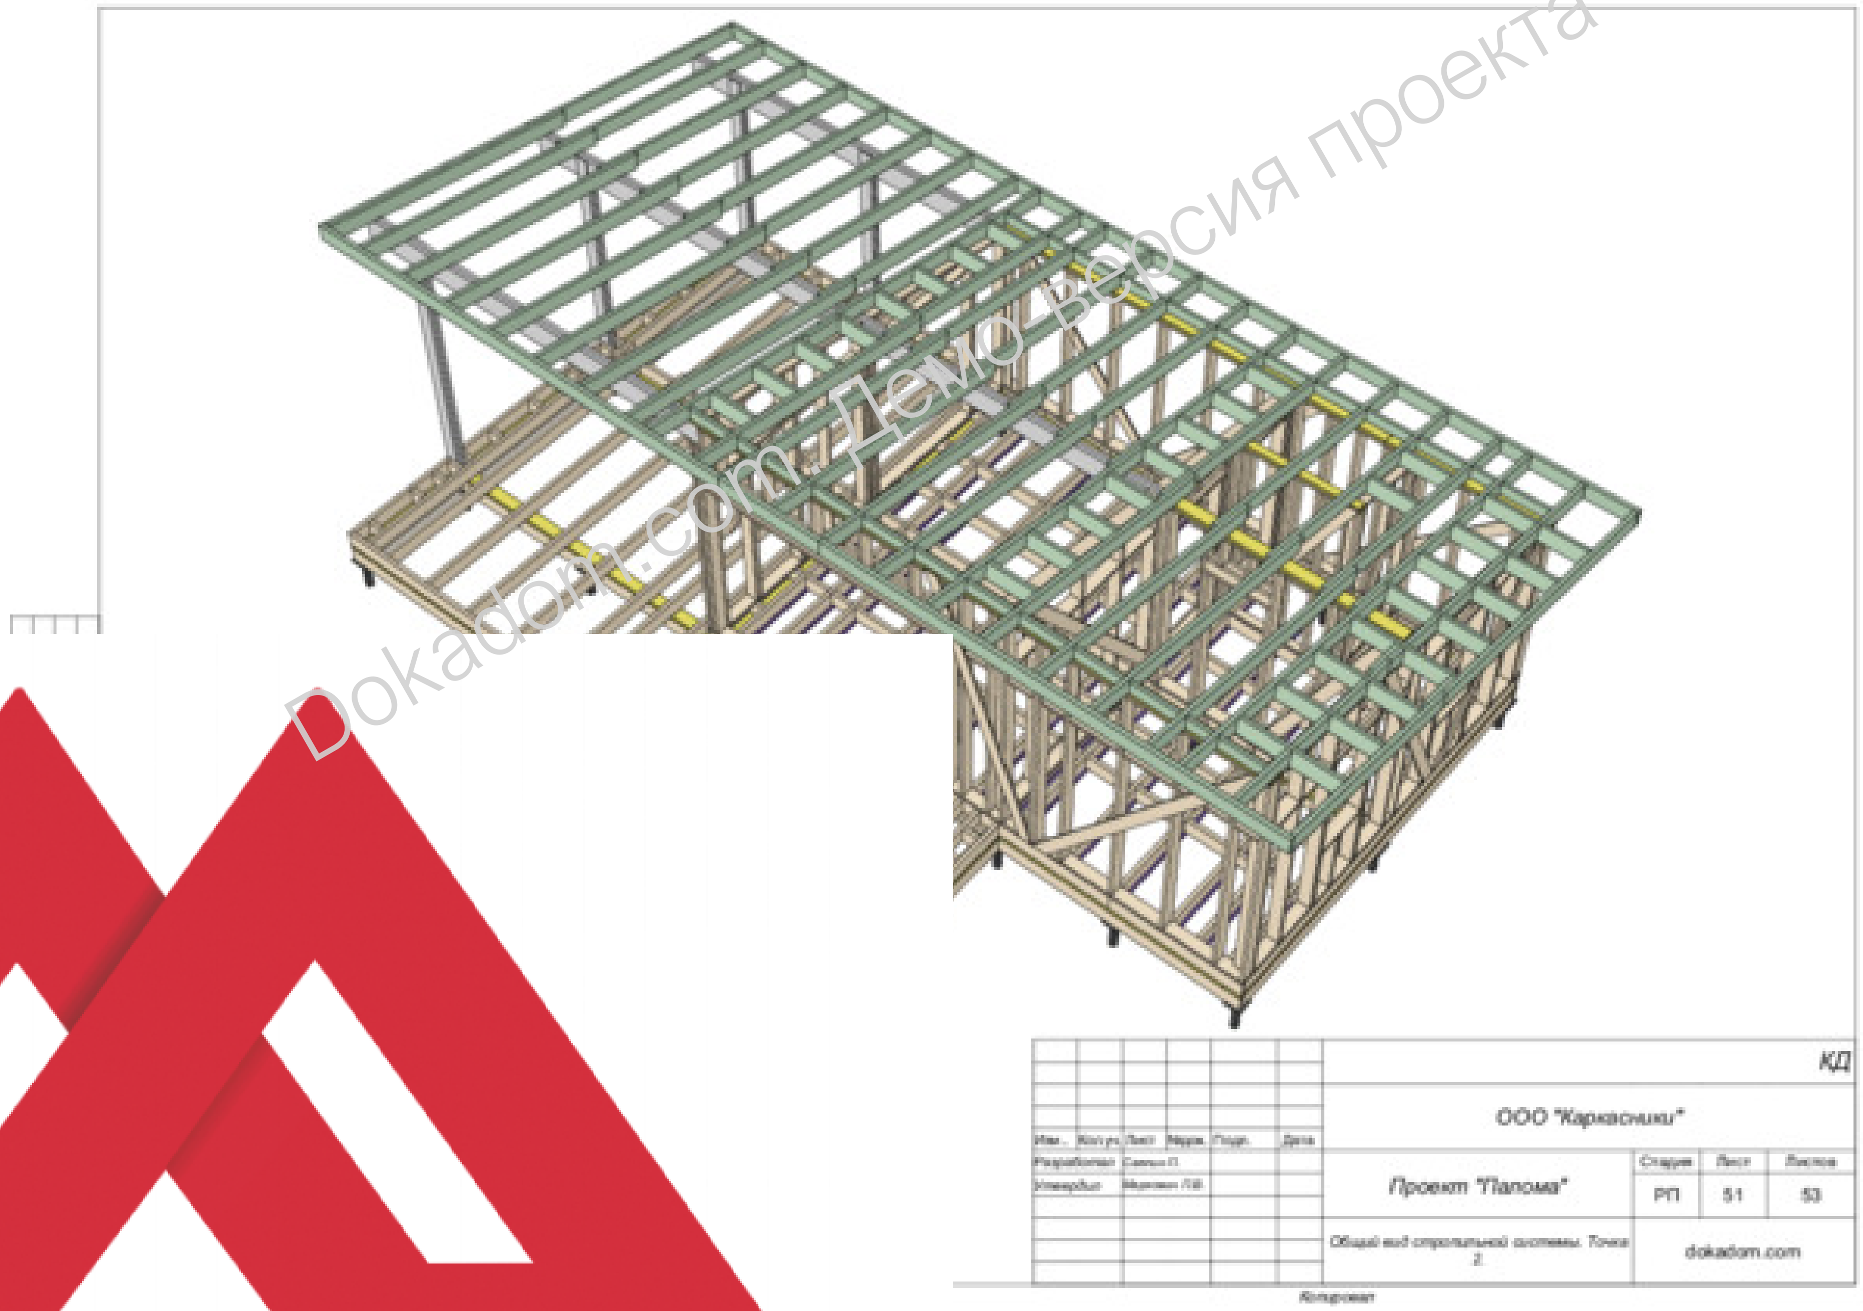

КД

ООО "Каркасники"

Изм. | Кол.уч. | Лист | №док. | Подп. | Дата

Разработал

Утвердил

Проект "Палома"

Стадия	Лист	Листов
РП	51	53

Общий вид стропильной системы. Точка 2.

dokadom.com

Копировал

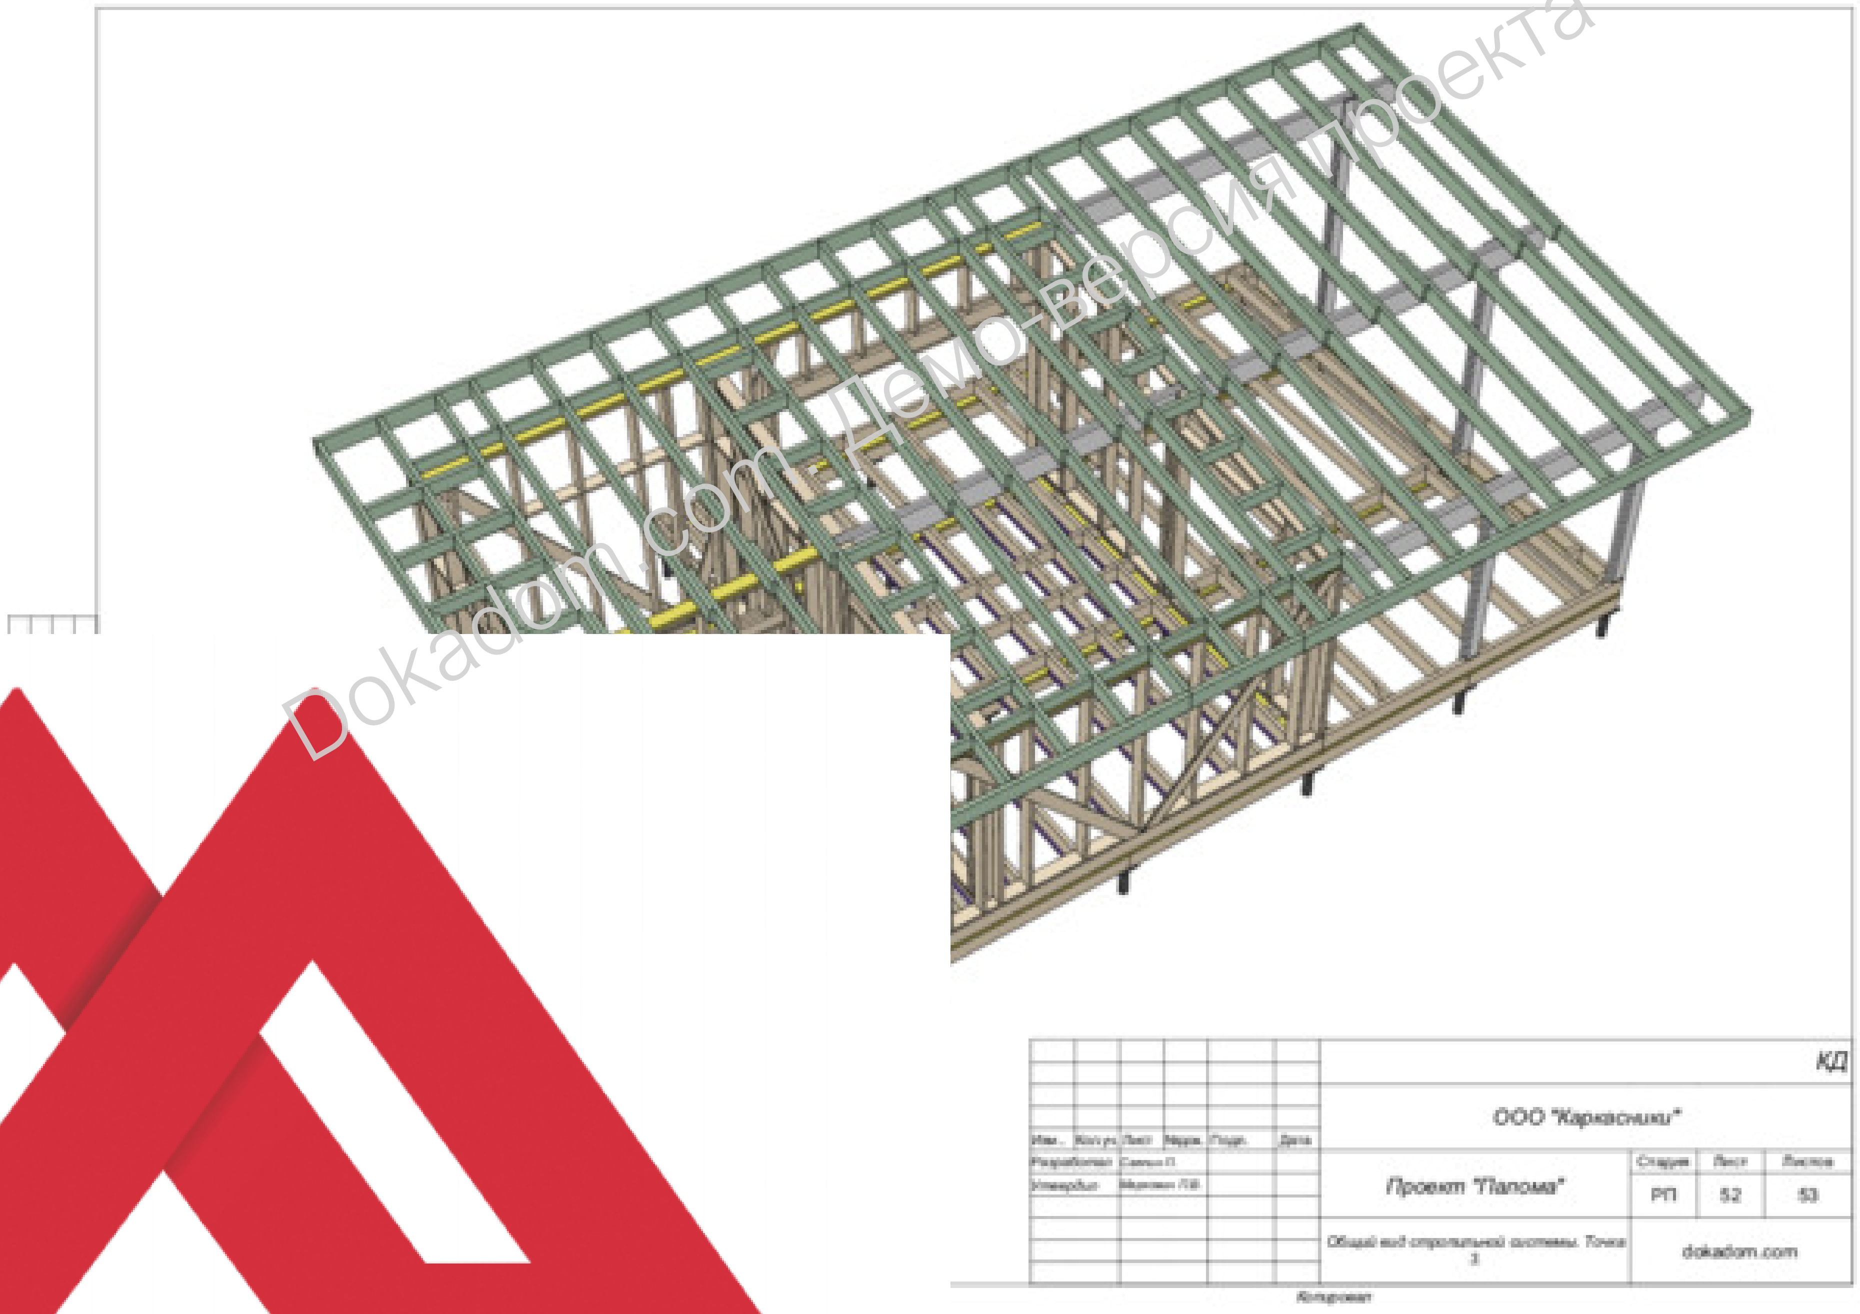

КД

ООО "Каркасники"

Изм.	Кол.уч.	Лист	№док.	Подп.	Дата
Разработал		Савин П.			
Утвердил		Миронов Л.В.			

Проект "Палома"

Стадия	Лист	Листов
РП	52	53

Общий вид стропильной системы. Точка 3

dokadom.com

Копировал

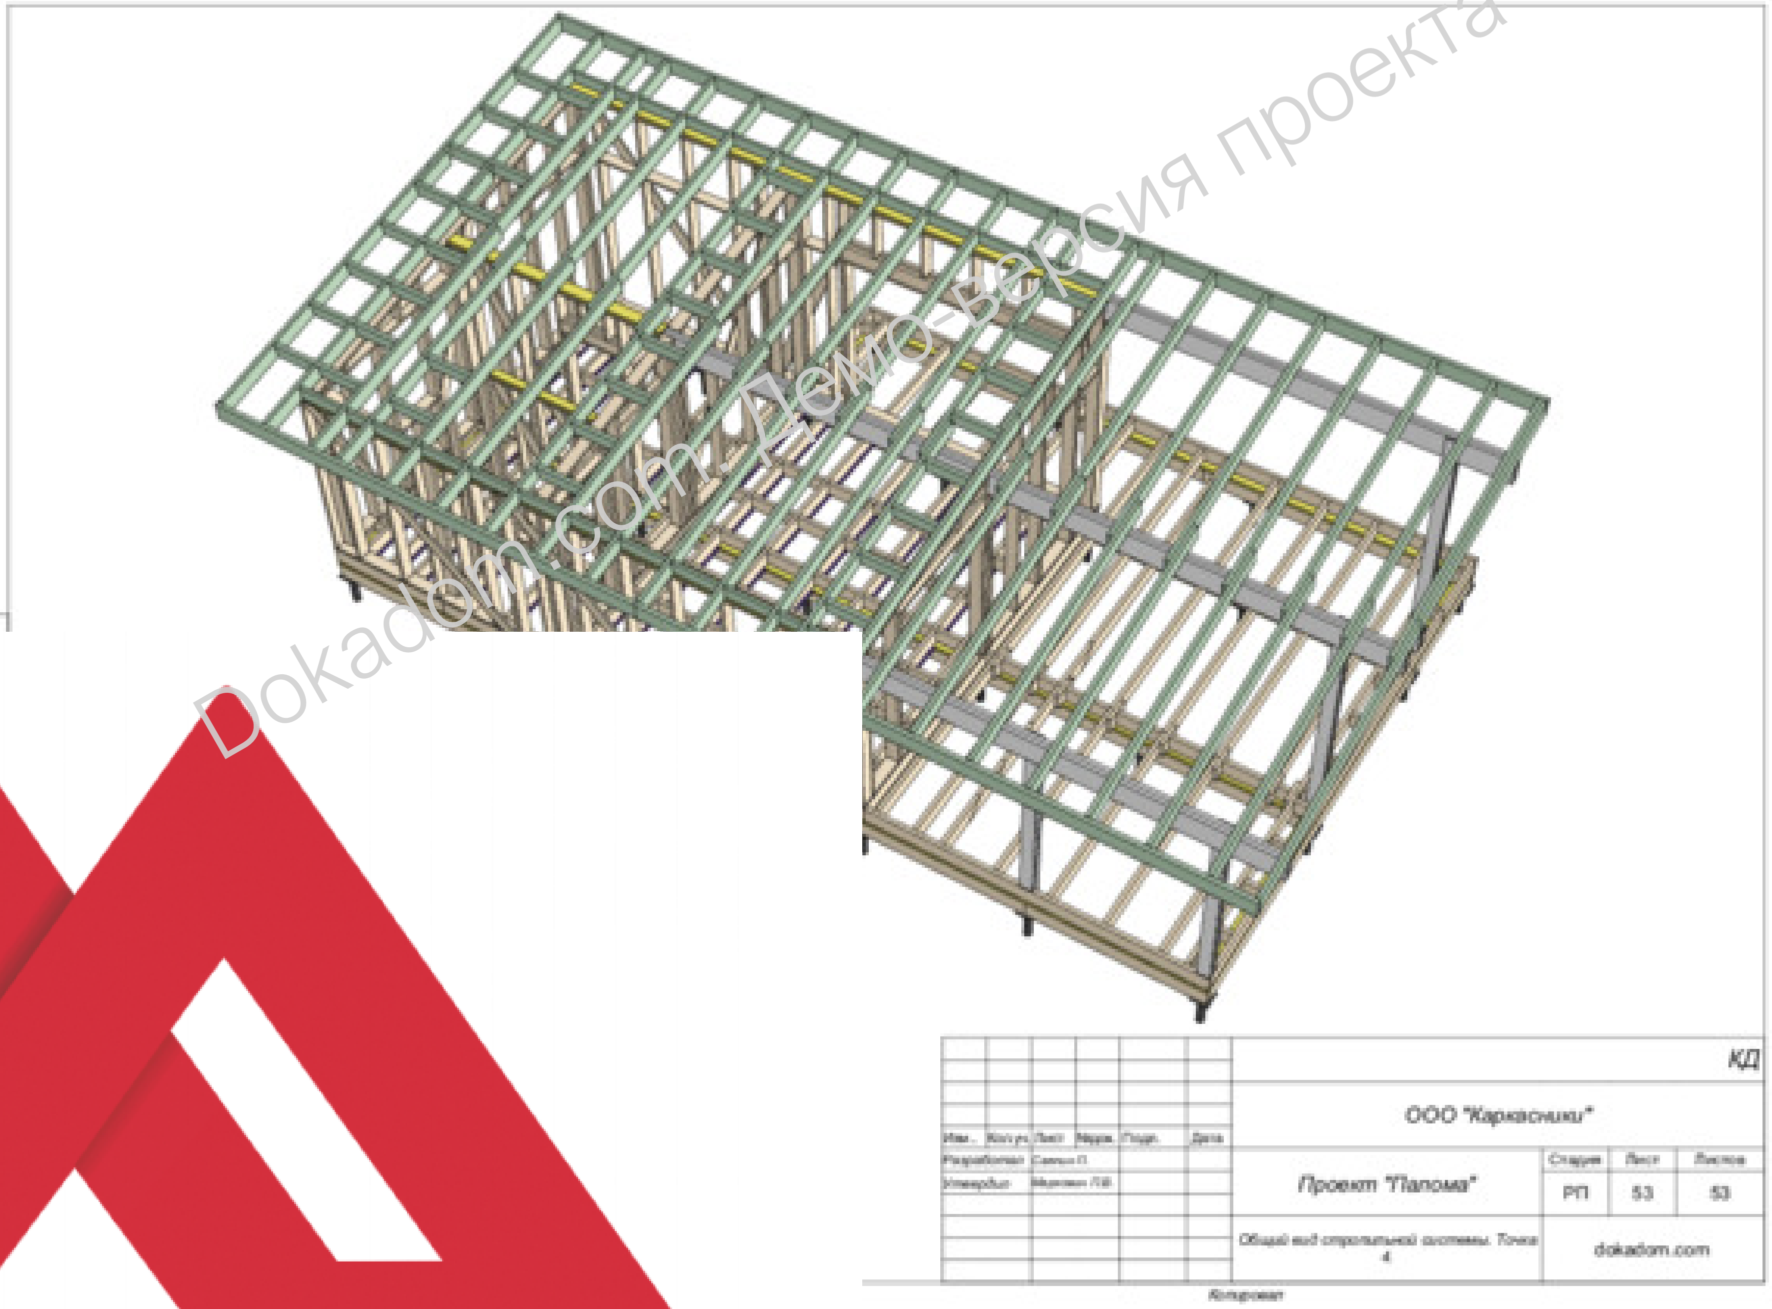

КД

ООО "Каркасники"

Проект "Палома"

Стадия	Лист	Листов
РП	53	53

Общий вид стропильной системы. Точка 4

dokadom.com

Копировал

DOKADOM.COM

ДЕМО-ВЕРСИЯ ПРОЕКТА