Демо-версия проекта
Заказать полную версию

Проект индивидуального жилого
дома по каркасной технологии

Проект "Марго"

Архитектурные решения (АР)



Ведомость чертежей комплекта АР

Лист	Наименование	Примечание
1	Ведомость чертежей. Общие данные	
2	Общий вид	
3	Общий вид	
4	План 1-го этажа обмерочный	
5	Разрез 1-1	
6	Разрез 2-2	
7	Фасад в осях 1-6	
8	Фасады в осях А-Е	
9	Фасады в осях 6-1	
10	Фасад в осях Е-А	
11	Ведомость заполнения проемов	
12	Ведомость заполнения проемов	
13	План кровли	

Технико-экономические показатели

Наименование	Значение
Этажность здания	1
Общая площадь, м2	75,28

Общие данные

1. Рабочий проект здания разработан на основании технического задания на проектирование, утвержденного заказчиком. Функциональное назначение здания - жилой дом.
2. Чертежи разработаны в соответствии с действующими нормами, правилами и стандартами.
3. Проект разработан для строительства в регионе со следующими характеристиками:
- Пермский край, пом.Горный;
- V снеговой р-н, расчетное значение веса снегового покрова по СНиП 2.01.07-85* составляет - 350 кг/м^2;
- I ветровой р-н, скоростной напор ветра по СНиП 2.01.07-85* составляет - 23 кг/м^2;
4. Строительные конструкции запроектированы с учетом требований:
- СНиП II-25-80 "Деревянные конструкции";
- СП 31-105-2002 "Проектирование и строительство одноквартирных жилых домов с деревянным каркасом";
- СНиП 2.01.07-85* "Нагрузки и воздействия" (с изменениями от 29 мая 2003 года);
- СНиП 2.08.01-89* "Жилые здания";
5. Характеристика сооружения и конструктивные решения:
- Конструктивная схема - продольные и поперечные несущие стены.
- Фундаменты - ж/б сваи с деревянной обвязкой.
- Стены наружные, внутренние и перегородки - деревянный каркас.
- Перекрытия - по деревянным балкам.
- Лестница наружная - по усмотрению заказчика.
- Крыша - скатная с наружным организованным водоотводом.
- Кровельное покрытие - гибкая черепица.
- Двери - наружные металлические; внутренние деревянные.
- Окна - с тройным остеклением, пластиковый профиль.
6. Деревянные конструкции запроектированы из леса хвойных пород I-II сорта по ГОСТ 8486-86*Е, для обрешетки - III сорта, с влажностью не более 20%.
7. Все деревянные конструкции обработать огнебиозащитным пропиточным составом, в соответствии с действующими нормами и правилами, в т.ч. и по пожарной безопасности.
8. Работы по антикоррозийной защите деревянным конструкций производить в соответствии с указаниями СНиП 3.04.01-87.
9. Защиту от возгорания выполнить в соответствии с действующими нормами и стандартами согласно требований фирмы-производителя. Противопожарную защиту конструкций и элементов здания выполнять путем обработки их огнезащитными пастами, красками, пропитками по выбору заказчика согласно действующих норм.
10. Строительство должно вестись в соответствии СНиП 3.01.01-85* "Организация строительного производства" и СП 31-105-2002.

Dokadom.com. Демо-версия проекта

DOKADOM.COM	Разработал	Мокеев Н.С.		"Марго" Раздел АР	Ведомость чертежей. Общие данные	Лист 1
	Проверил	Маркович П.В.				
	Заказчик					






DOKADOM.COM	Разработал	Мокеев Н.С.		"Марго"	Общий вид	Лист
	Проверил	Маркович П.В.		Раздел АР		2
	Заказчик					

Dokadom.com Демо-версия проекта




Dokadom.com. Демо-версия проекта

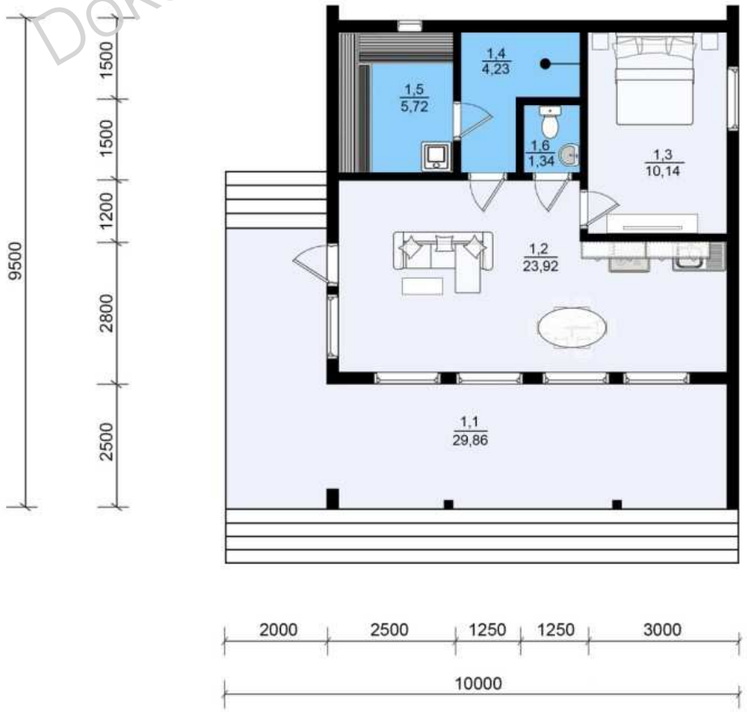

№	Наименование	Площадь
1.1	Терраса	29,86
1.2	Кухня – гостиная	23,92
1.3	Спальня	10,14
1.4	Душевая	4,23
1.5	Сауна	5,72
1.6	Санузел	1,34
		75,21 м²

DOKADOM.COM	Разработал	Мокеев Н.С.		"Марго" Раздел АР	Общий вид	Лист 3
	Проверил	Маркович П.В.				
	Заказчик					

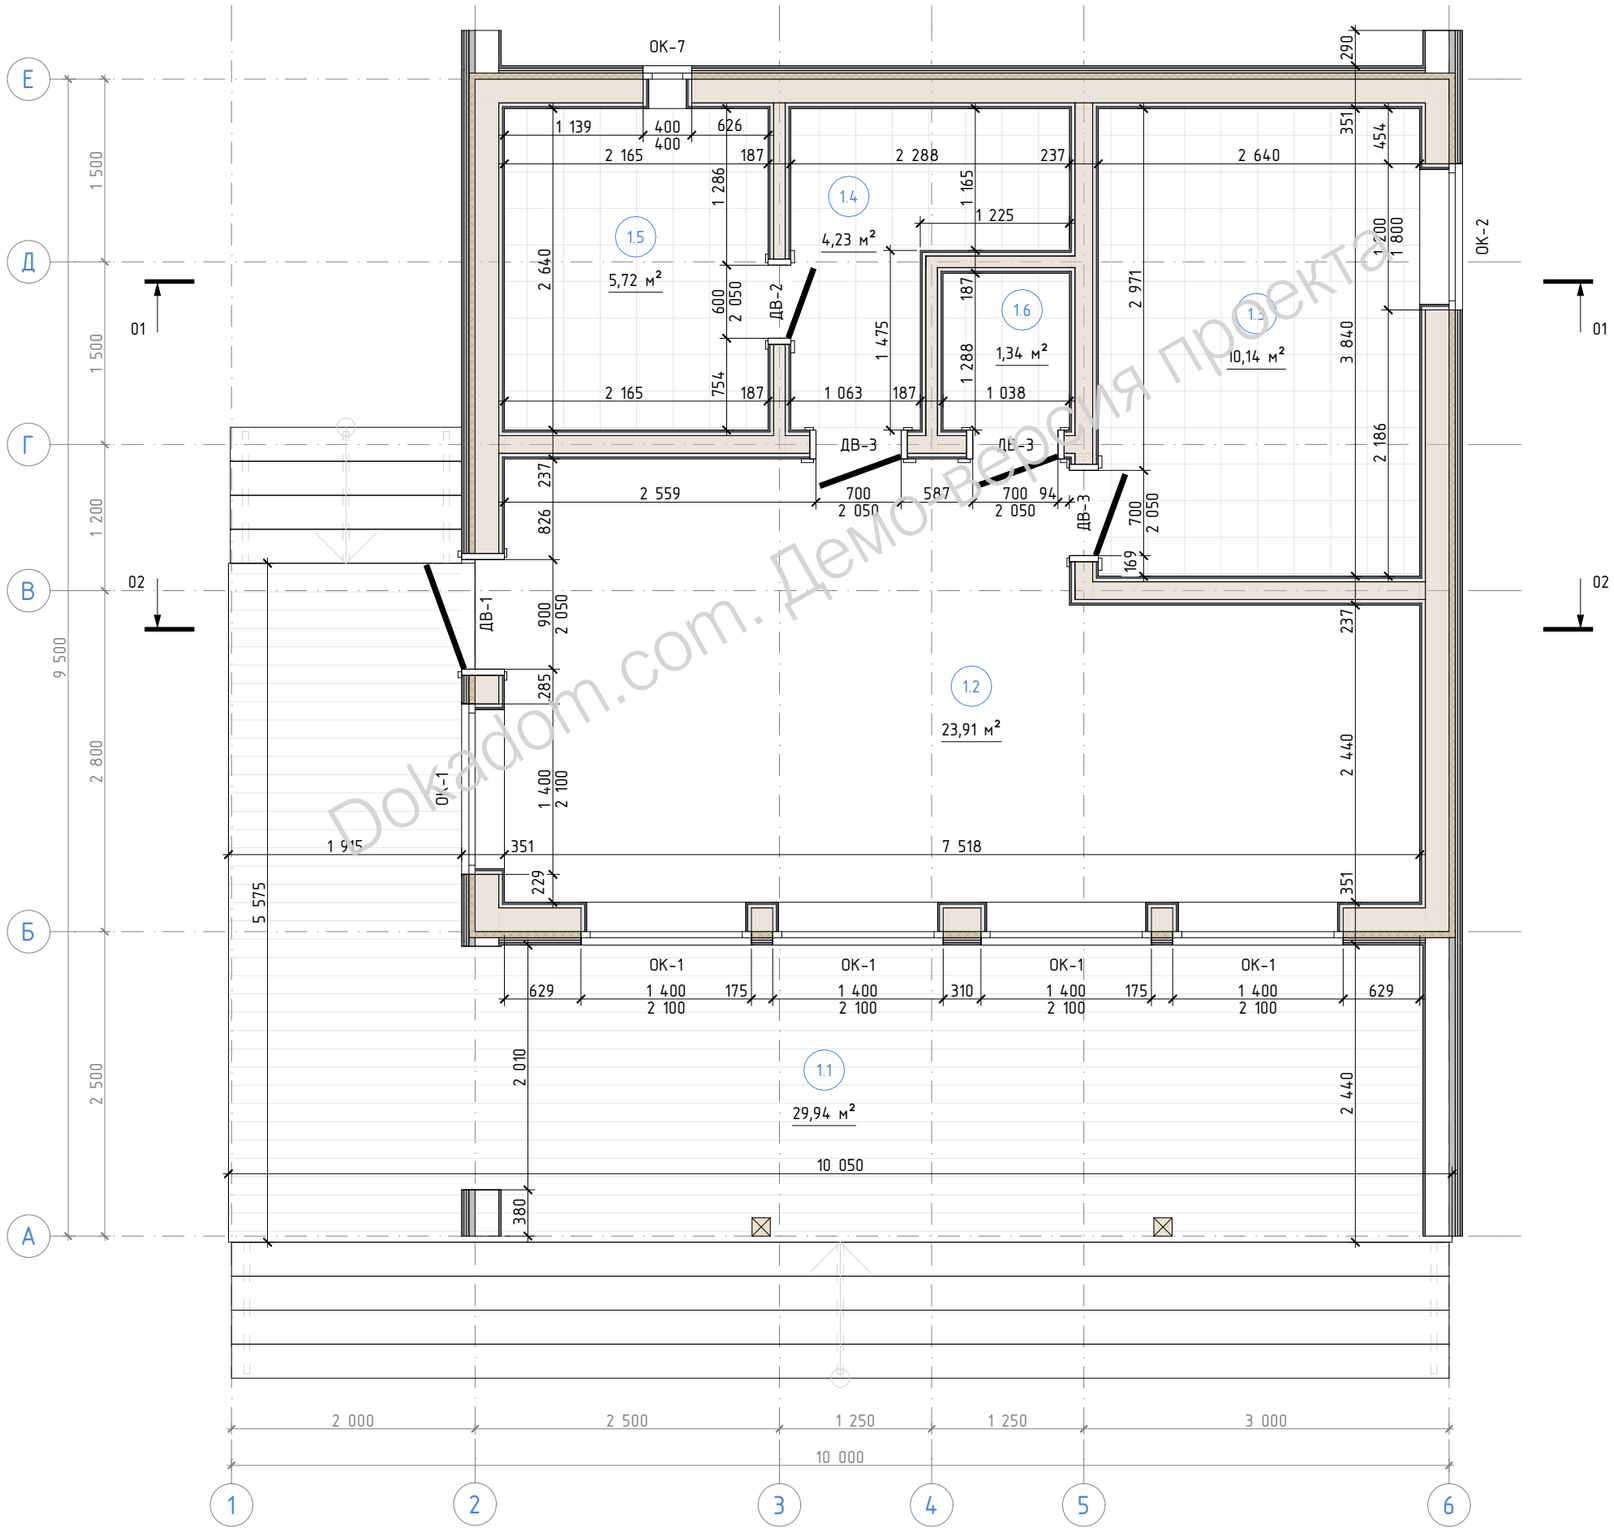

Dokadom.com. Демо-версия проекта

№	Наименование	Площадь
1.1	Терраса	29,94
1.2	Кухня – гостиная	23,91
1.3	Спальня	10,14
1.4	Душевая	4,23
1.5	Сауна	5,72
1.6	Санузел	1,34
		75,28 м²

DOKADOM.COM	Разработал	Мокеев Н.С.		"Марго" Раздел АР	План 1-го этажа обмерочный	Лист 4
	Проверил	Маркович П.В.				
	Заказчик					

Каркас перекрытия межэтажного с утеплителем	195
Доп. утепление перекрытий	50
Пароизоляция	0
Обрешетка, доска 25х100, шаг 300	25
Внутр. отделка потолка	20


Мягкая черепица	10
Обрешетка, доска 25х100, шаг 300	25
Обрешетка, брусок 50х50, шаг 630	50
Гидро-ветрозащита	0
Каркас стропильной системы с утеплителем	195
Доп. утепление кровли	50
Пароизоляция	0
Обрешетка, доска 25х100, шаг 300	25
Внутр. отделка потолка	20

Нар. отделка стен	20
Обрешетка, доска 20х100, шаг 630	20
Обрешетка, доска 20х100, шаг 630	20
Гидро-ветрозащита	0
Доп. утепление стен	50
Каркас стен наружных с утеплителем	195
Пароизоляция	0
Воздушный зазор, брусок 50х30, шаг 630	30
Внутр. отделка стен	16

Внутр. отделка стен	16
Воздушный зазор, брусок 50х30, шаг 630	30
Изоляционная пленка	0
Каркас стен внутренних с утеплителем	95
Изоляционная пленка	0
Воздушный зазор, брусок 50х30, шаг 630	30
Внутр. отделка стен	16


Внутр. отделка стен	16
Воздушный зазор, брусок 50х30, шаг 630	30
Изоляционная пленка	0
Каркас стен внутренних с утеплителем	145
Изоляционная пленка	0
Воздушный зазор, брусок 50х30, шаг 630	30
Внутр. отделка стен	16

Покрытие пола - Ламинат	10
Фанера	20
Обрешетка, доска 20х100, шаг 300	20
Пароизоляция	0
Каркас перекрытия цокольного с утеплителем	195
Доп. утепление перекрытий	50
Гидро-ветрозащита	0
Обрешетка, доска 25х100, шаг 630	25

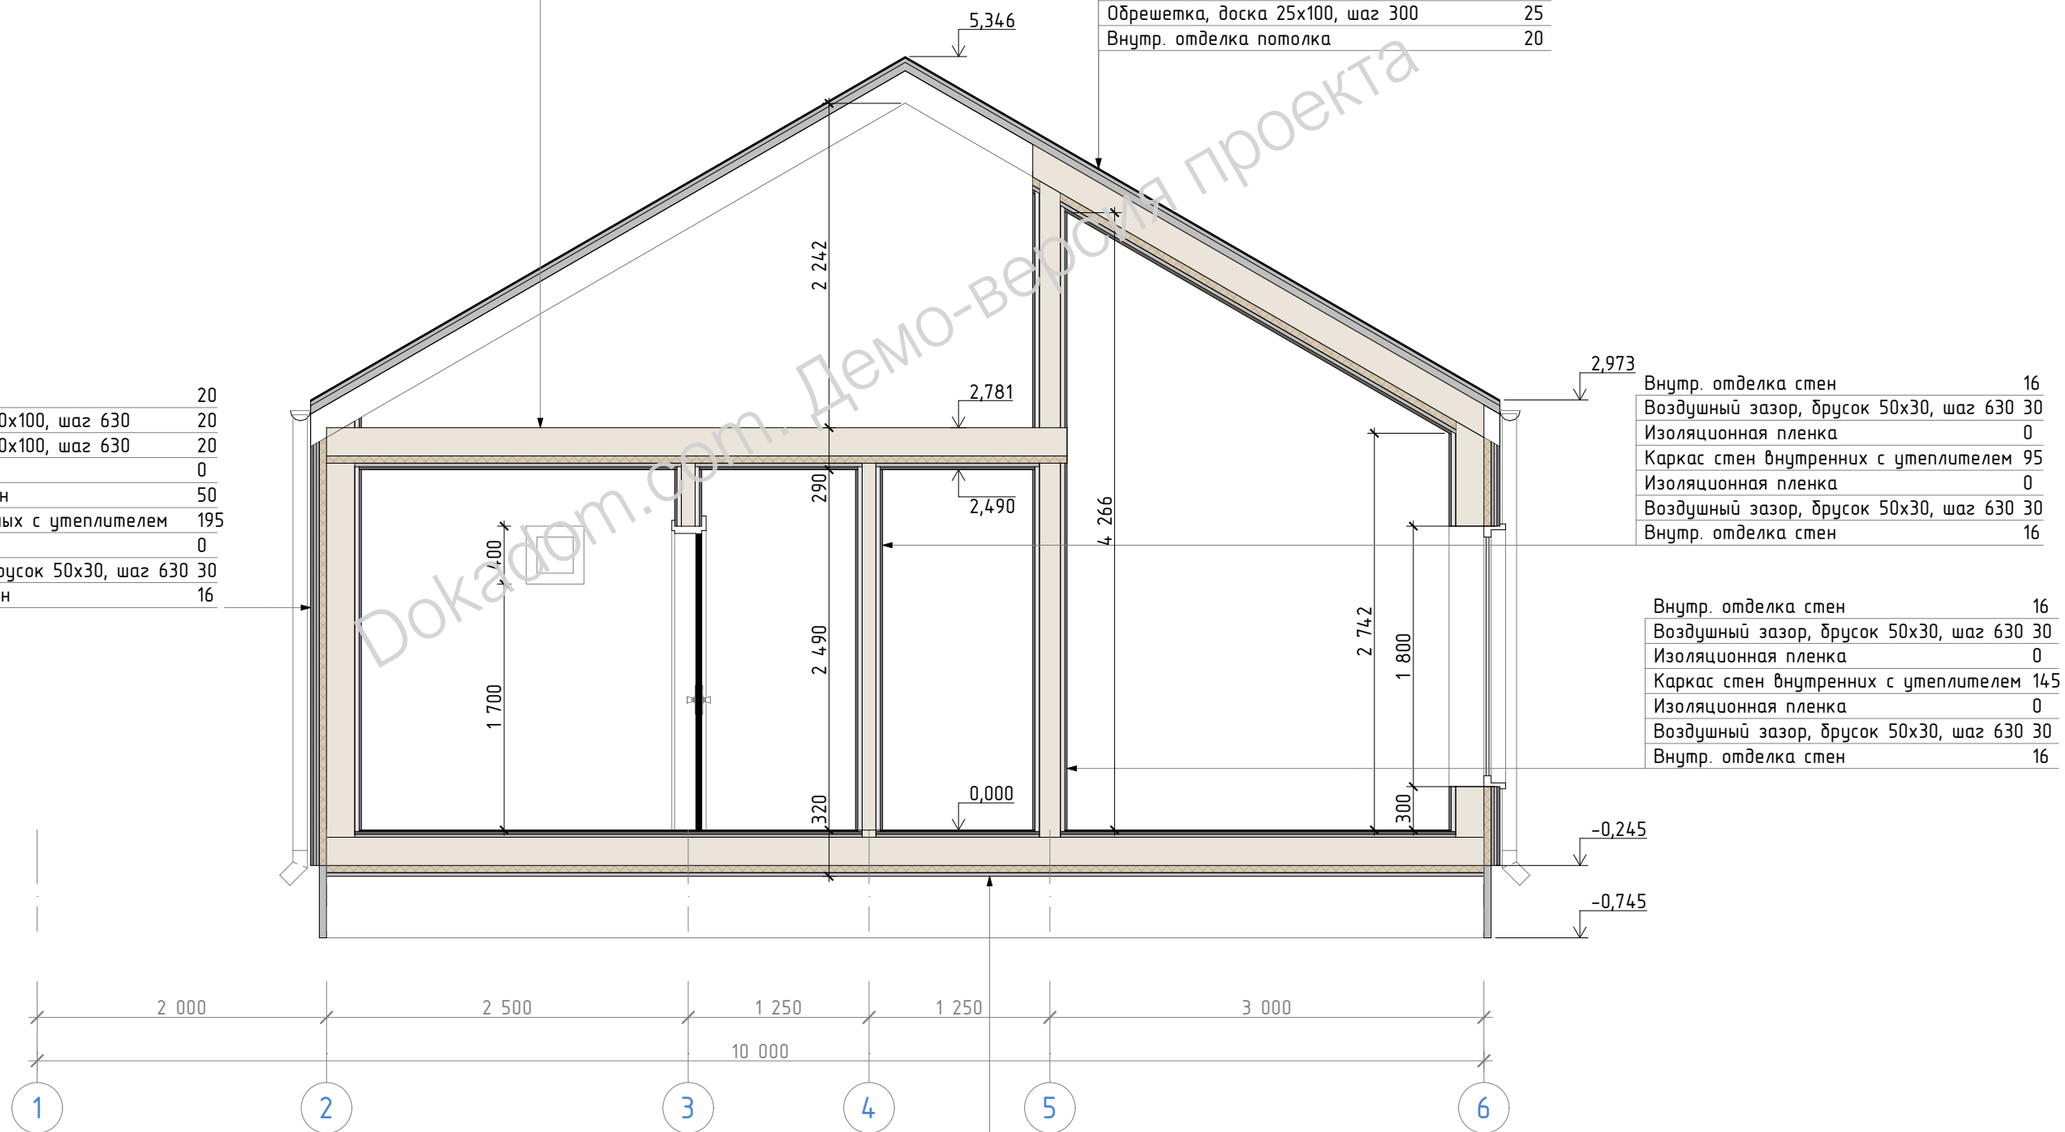

Dokadom.com. Демо-версия проекта

DOKADOM.COM	Разработал	Мокеев Н.С.		"Марго" Раздел АР	Разрез 1-1	Лист 5
	Проверил	Маркович П.В.				
	Заказчик					

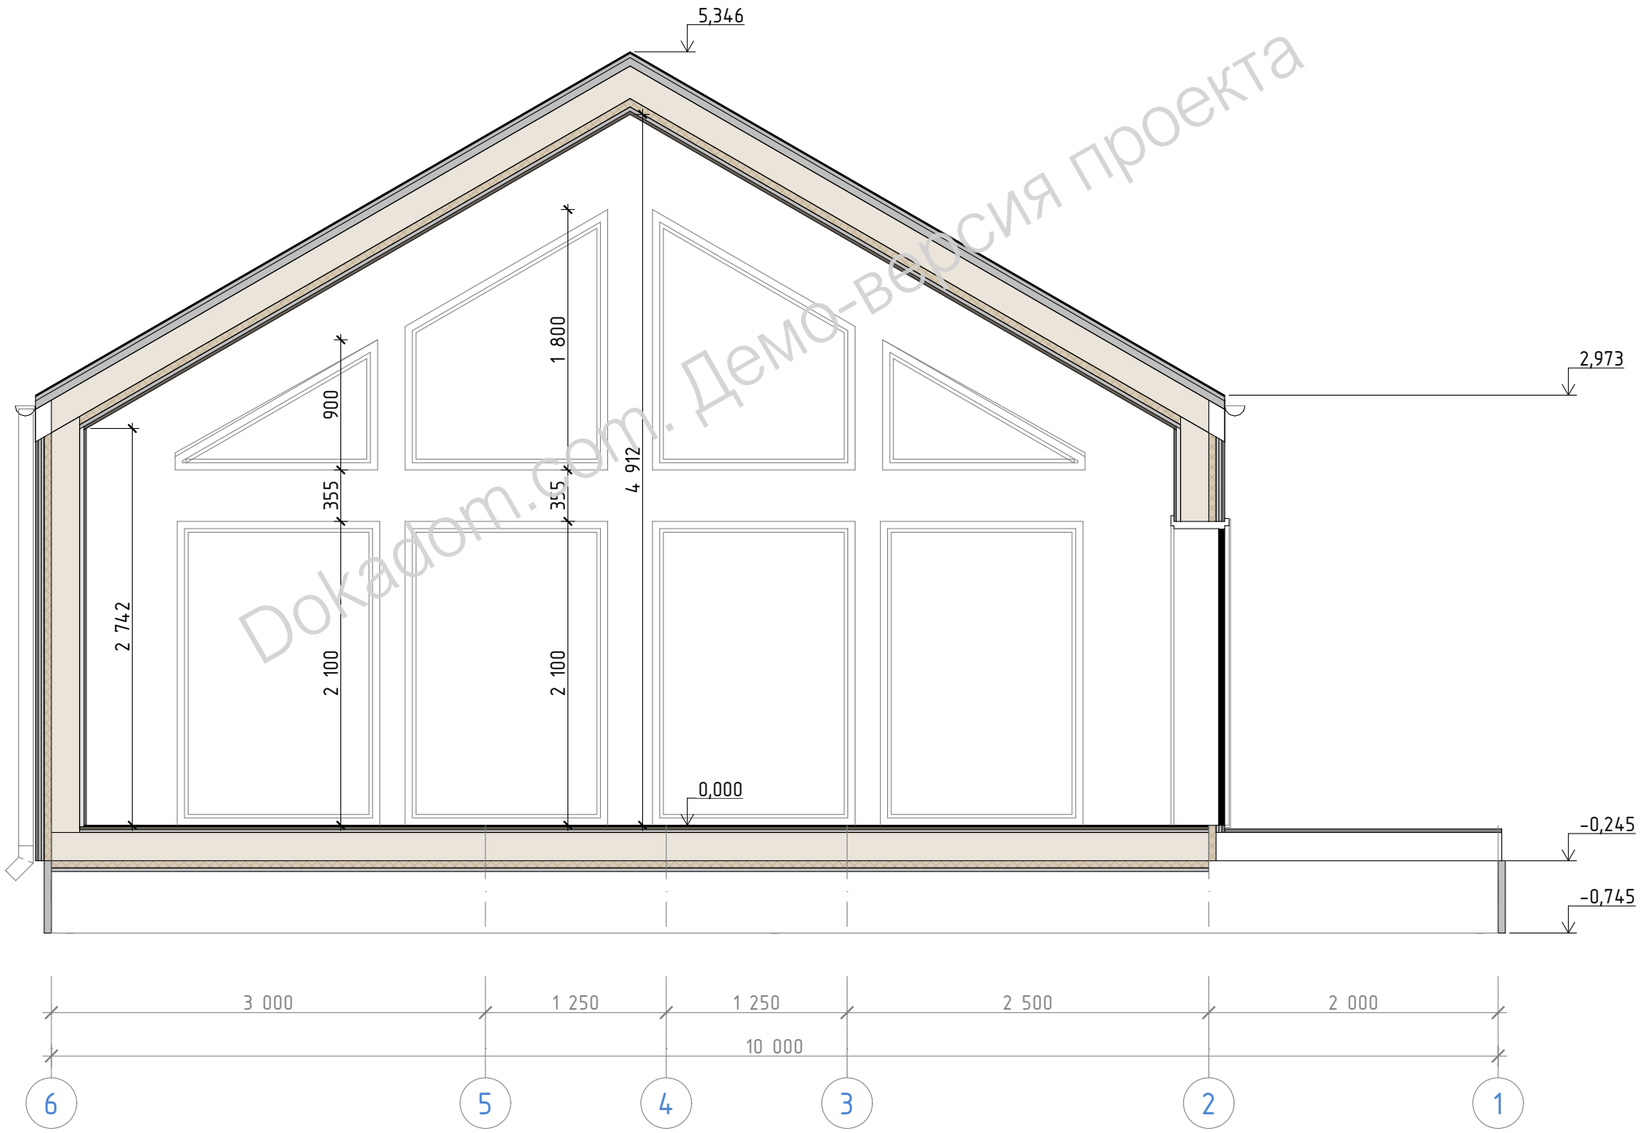


Dokadom.com. Демо-версия проекта

DOKADOM.COM	Разработал	Мокеев Н.С.		"Марго" Раздел АР	Разрез 2-2	Лист 6
	Проверил	Маркович П.В.				
	Заказчик					




Dokadom.com. Демо-версия проекта

DOKADOM.COM	Разработал	Мокеев Н.С.		"Марго"	Фасад в осях 1-6	Лист
	Проверил	Маркович П.В.		Раздел АР		7
	Заказчик					

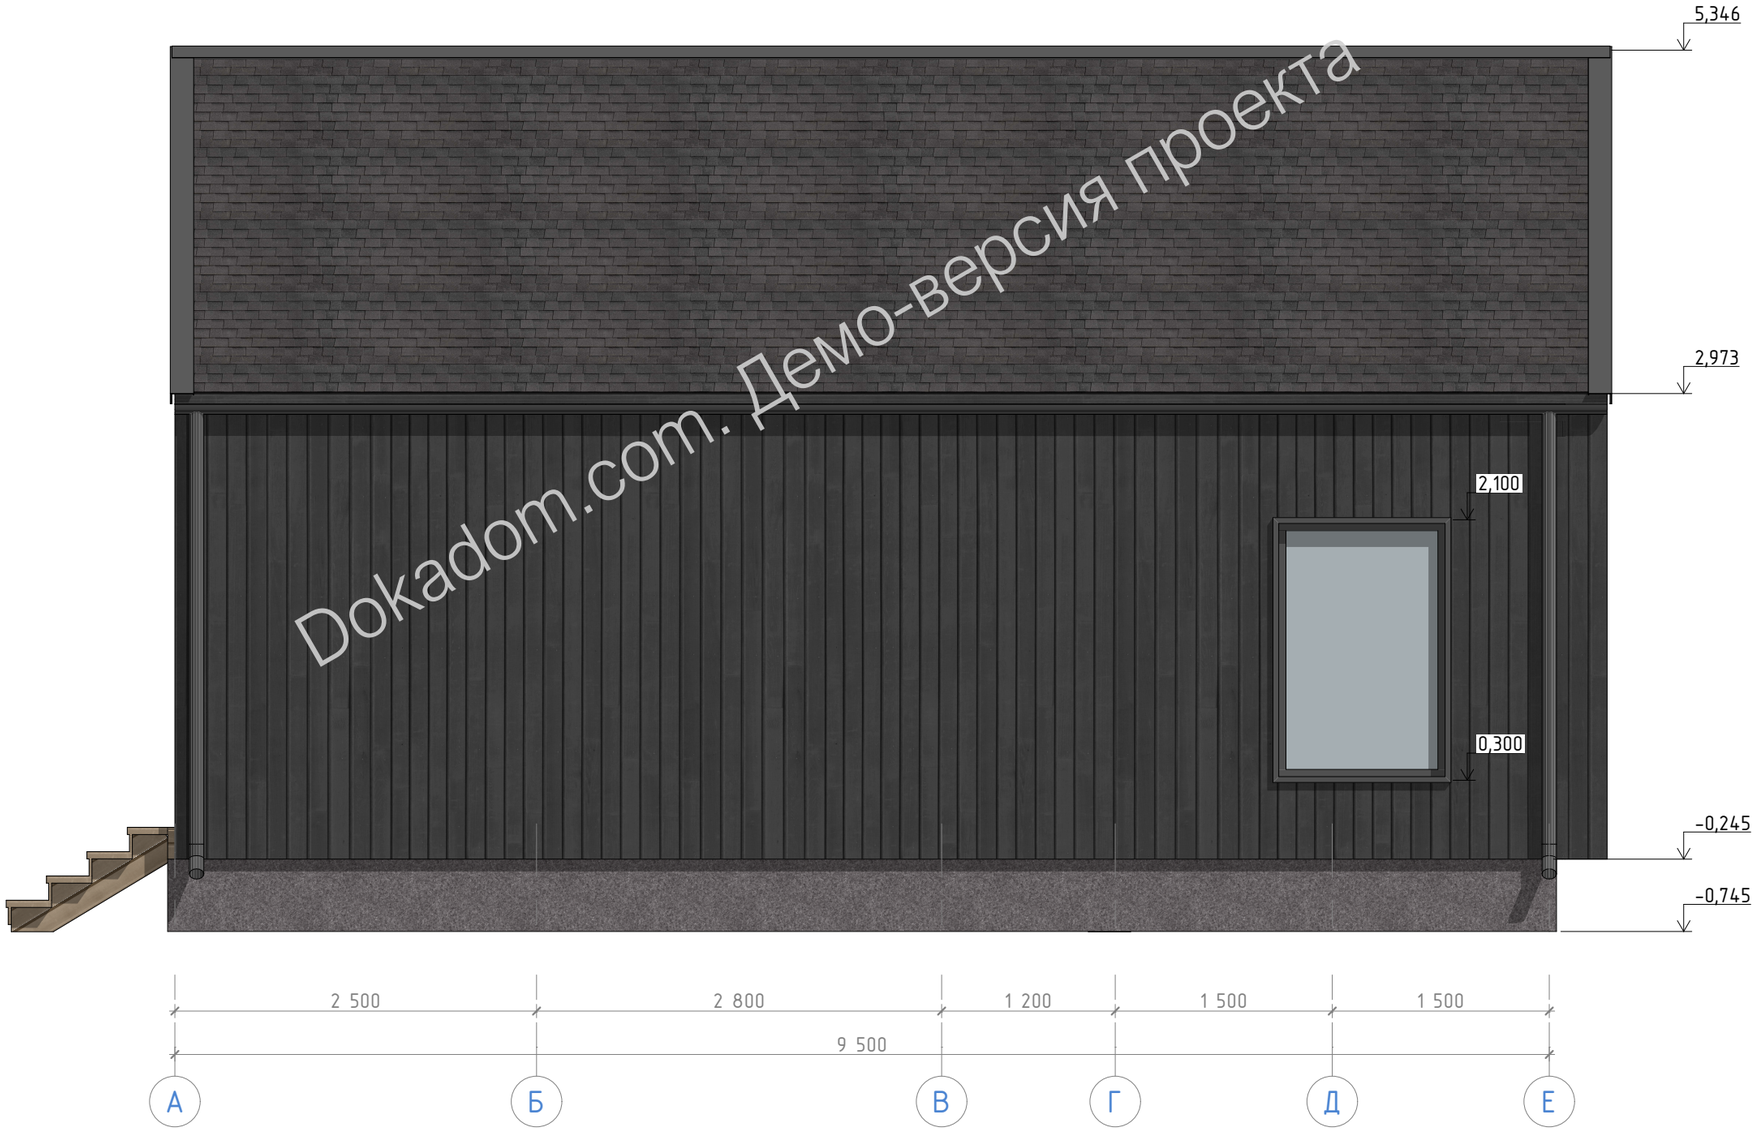

Dokadom.com. Демо-версия проекта

DOKADOM.COM	Разработал	Мокеев Н.С.		"Марго" Раздел АР	Фасады в осях А-Е	Лист 8
	Проверил	Маркович П.В.				
	Заказчик					

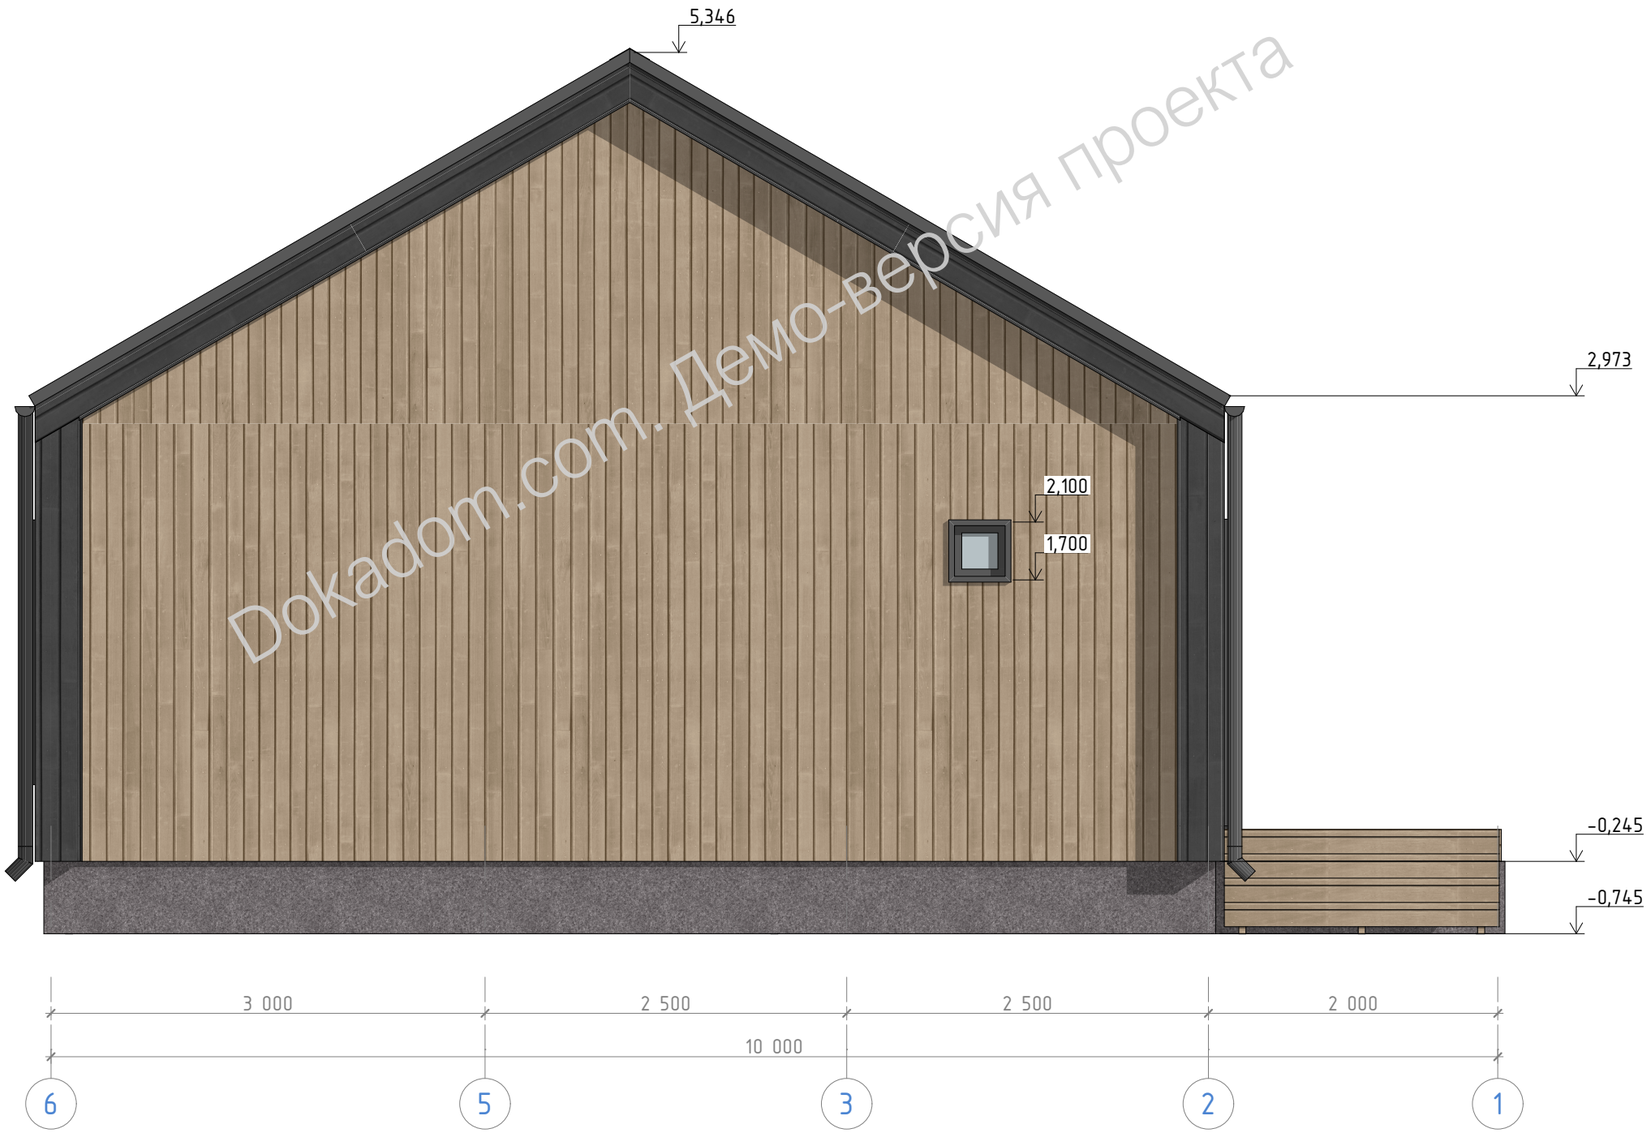







Dokadom.com. Демо-версия проекта

DOKADOM.COM	Разработал	Мокеев Н.С.		"Марго" Раздел АР	Фасады в осях 6-1	Лист 9
	Проверил	Маркович П.В.				
	Заказчик					



Dokadom.com. Демо-версия проекта





DOKADOM.COM	Разработал	Мокеев Н.С.		"Марго" Раздел АР	Фасад в осях Е-А	Лист 10
	Проверил	Маркович П.В.				
	Заказчик					

  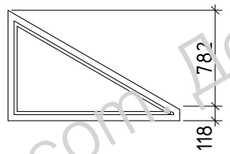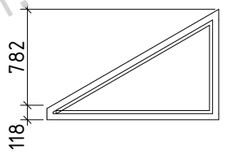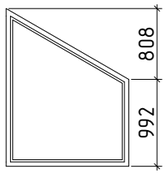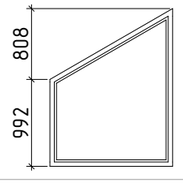Поз.	Вид с наружней стороны здания	Размеры оконного блока (Ш х В)	Кол-во	Площадь оконного блока
ОК-1		1 400×2 100	5	2,94
ОК-2		1 200×1 800	1	2,16
ОК-3		1 400×900	1	0,71
ОК-4		1 400×900	1	0,71
ОК-5		1 400×1 800	1	1,95
ОК-6		1 400×1 800	1	1,95
ОК-7		400×400	1	0,16
			11	22,35 м^2

Примечание:
1. Размеры оконного проема рассчитываются следующим образом:
- к размеру оконного блока прибавляется снизу 50мм на подставочный профиль, и по 20мм с остальных сторон на монтажный зазор.

Dokadom.com Демо-версия проекта


DOKADOM.COM	Разработал	Мокеев Н.С.		"Марго" Раздел АР	Ведомость заполнения проемов	Лист 11
	Проверил	Маркович П.В.				
	Заказчик					

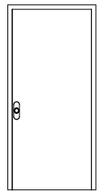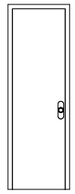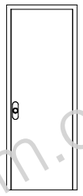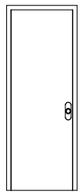Поз.	Вид спереди	Размеры полотна (Ш х В), мм	Размеры проема (Ш х В), мм	Откр.	Кол-во	Площадь проема
ДВ-1		900×2 050	1 000×2 100	П	1	2,10
ДВ-2		600×2 050	700×2 100	Л	1	1,47
ДВ-3		700×2 050	800×2 100	П	2	1,68
ДВ-3		700×2 050	800×2 100	Л	1	1,68
					5	8,61 м^2

Dokadom.com. Демо-версия проекта

Примечание:
1. Размеры дверного проема рассчитываются следующим образом:
- к размеру дверного блока прибавляется по 20мм сверху и по бокам на монтажный зазор.
- внизу балконной двери еще добавляется 50мм на подставочный профиль.

DOKADOM.COM	Разработал	Мокеев Н.С.		"Марго" Раздел АР	Ведомость заполнения проемов	Лист 12
	Проверил	Маркович П.В.				
	Заказчик					

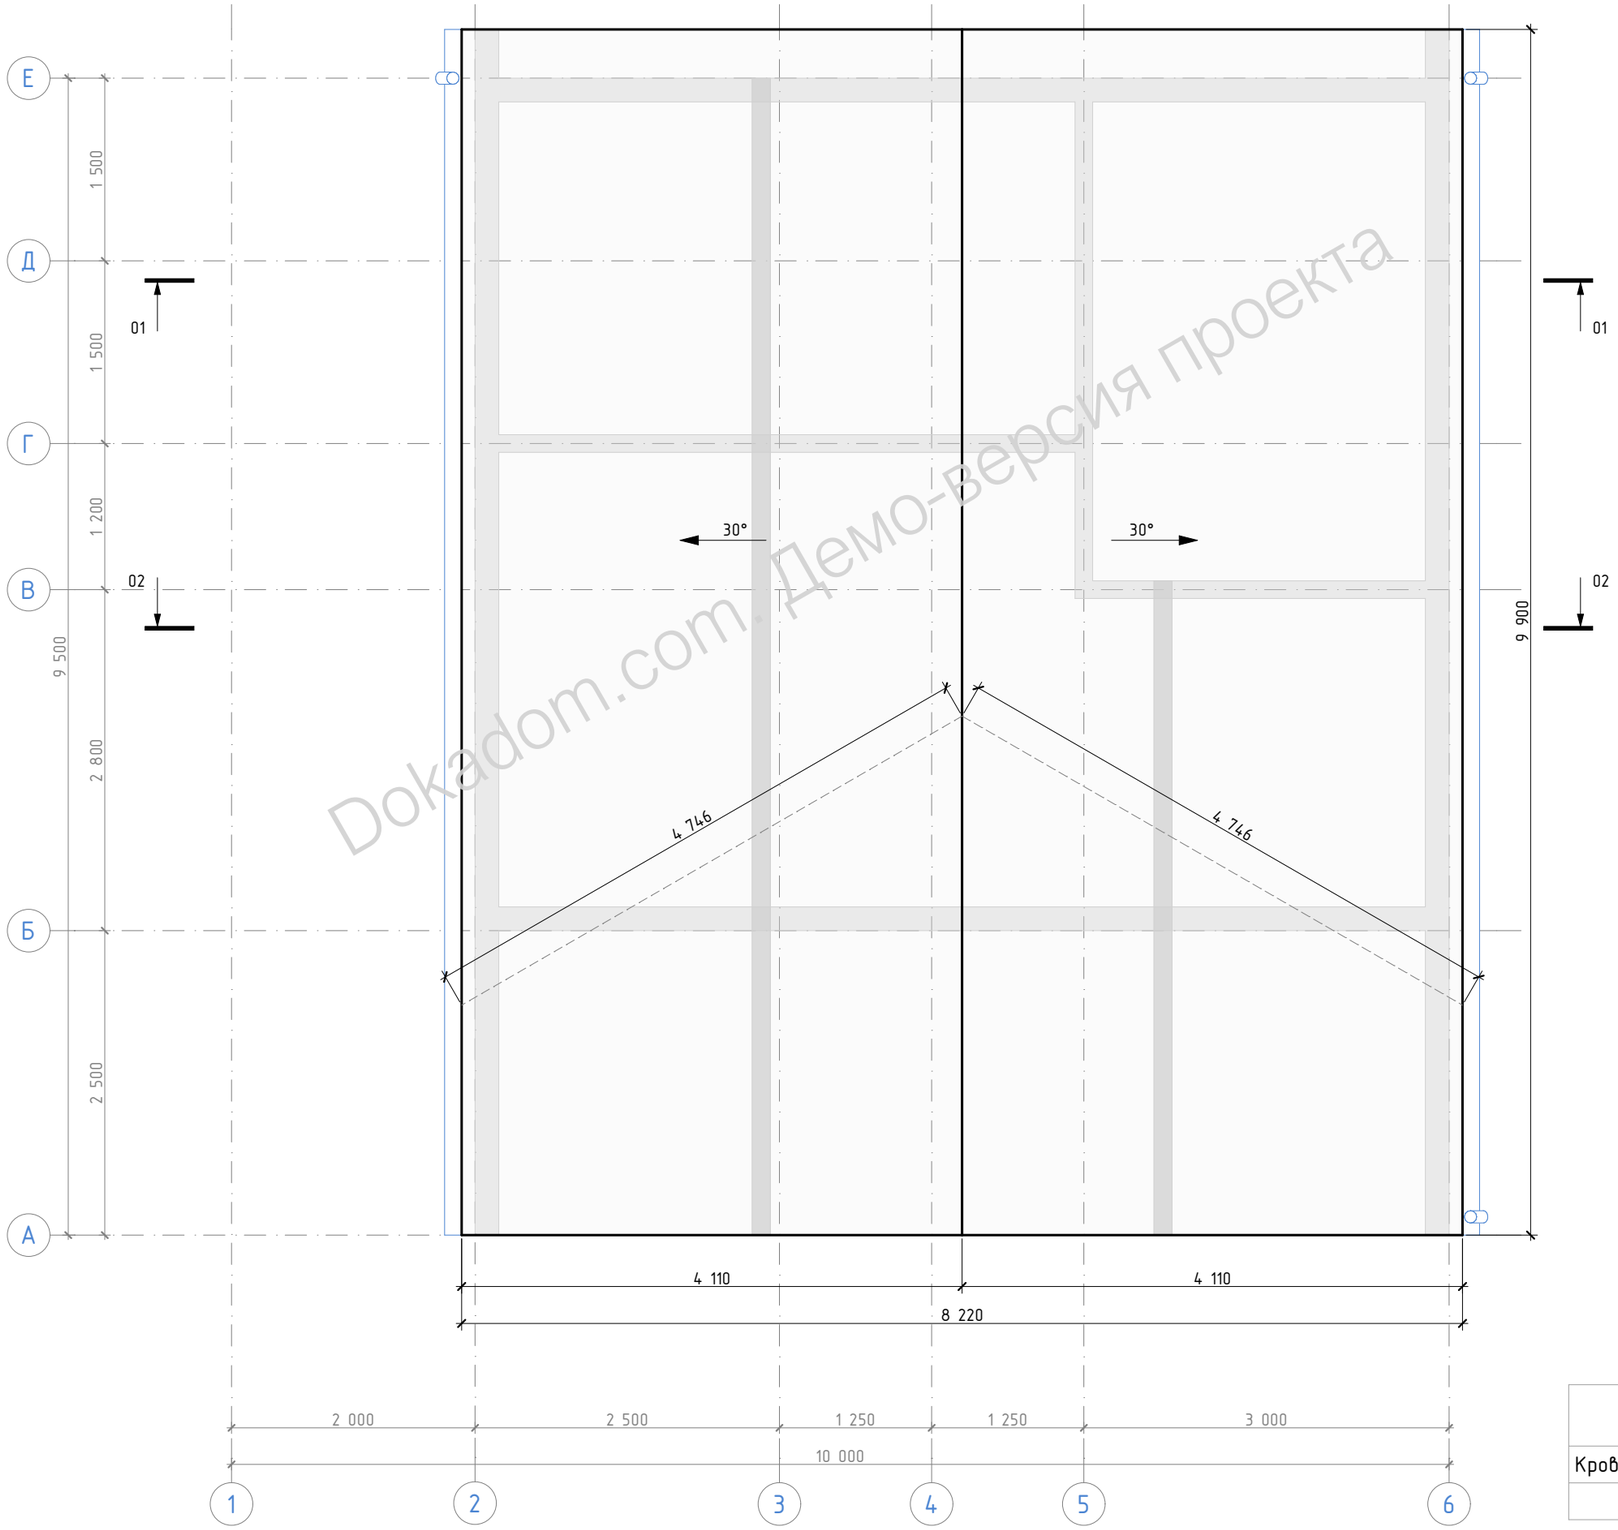

Dokadom.com. Демо-версия проекта

Наименование	Площадь
Кровля	93,97
	93,97 м²

DOKADOM.COM	Разработал	Мокеев Н.С.		"Марго" Раздел АР	План кровли	Лист 13
	Проверил	Маркович П.В.				
	Заказчик					


Проект индивидуального жилого дома
по каркасной технологии

Проект "Марго"

Конструктивные решения (КР)

Dokadom.com. Демо-версия проекта

DOKADOM.COM
ДЕМО-ВЕРСИЯ ПРОЕКТА

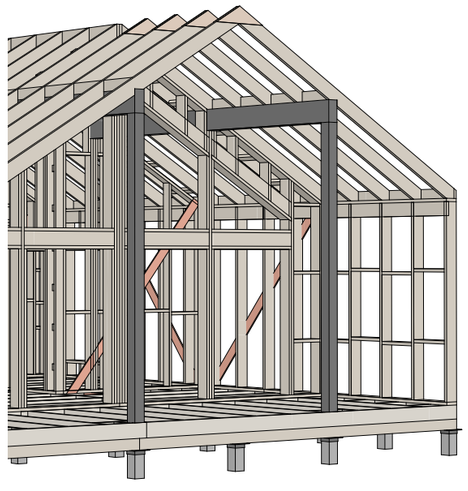

DOKADOM.COM


Ведомость чертежей комплекта КР

Лист	Наименование	Примечание
	Титульный лист	
1	Ведомость чертежей	
2	Модель каркаса, вид 1	
3	Модель каркаса, вид 2	
3	План фундамента	
5	Схема монтажа обвязки свай	
6	Модель обвязки свай и подкладочной доски	
7	Узлы обвязки свай	
8	Схема сборки цокольного перекрытия	
9	Модель цокольного перекрытия	
10	Узлы перекрытий 1	
11	Узлы перекрытий 2	
12	Схема монтажа стен 1-го этажа	
13	Модель стен 1-го этажа	
14	Модель стен 1-го этажа	
15	Схема сборки стен - Вид 1.01	
16	Схема сборки стен - Вид 1.02	
17	Схема сборки стен - Вид 1.03	
18	Схема сборки стен - Вид 1.04	

Лист	Наименование	Примечание
40	Разрезы 6-6, 7-7	
41	Разрез 8-8, 9-9	
42	Деталировка стропил	
43	Модель опорных конструкций	
44	Модель стропильной системы, вид 1	
45	Модель стропильной системы, вид 2	
46	Спецификация пиломатериала силового каркаса	
47	Сводные данные	


Dokadom.com. Демо-версия проекта
DOKADOM.COM
ДЕМО-ВЕРСИЯ ПРОЕКТА

OKADOM.COM	Разработал	Мокеев Н.С.		"Марго"	Ведомость чертежей	Лист
	Проверил	Маркович П.В.		Раздел КР		1
	Заказчик					

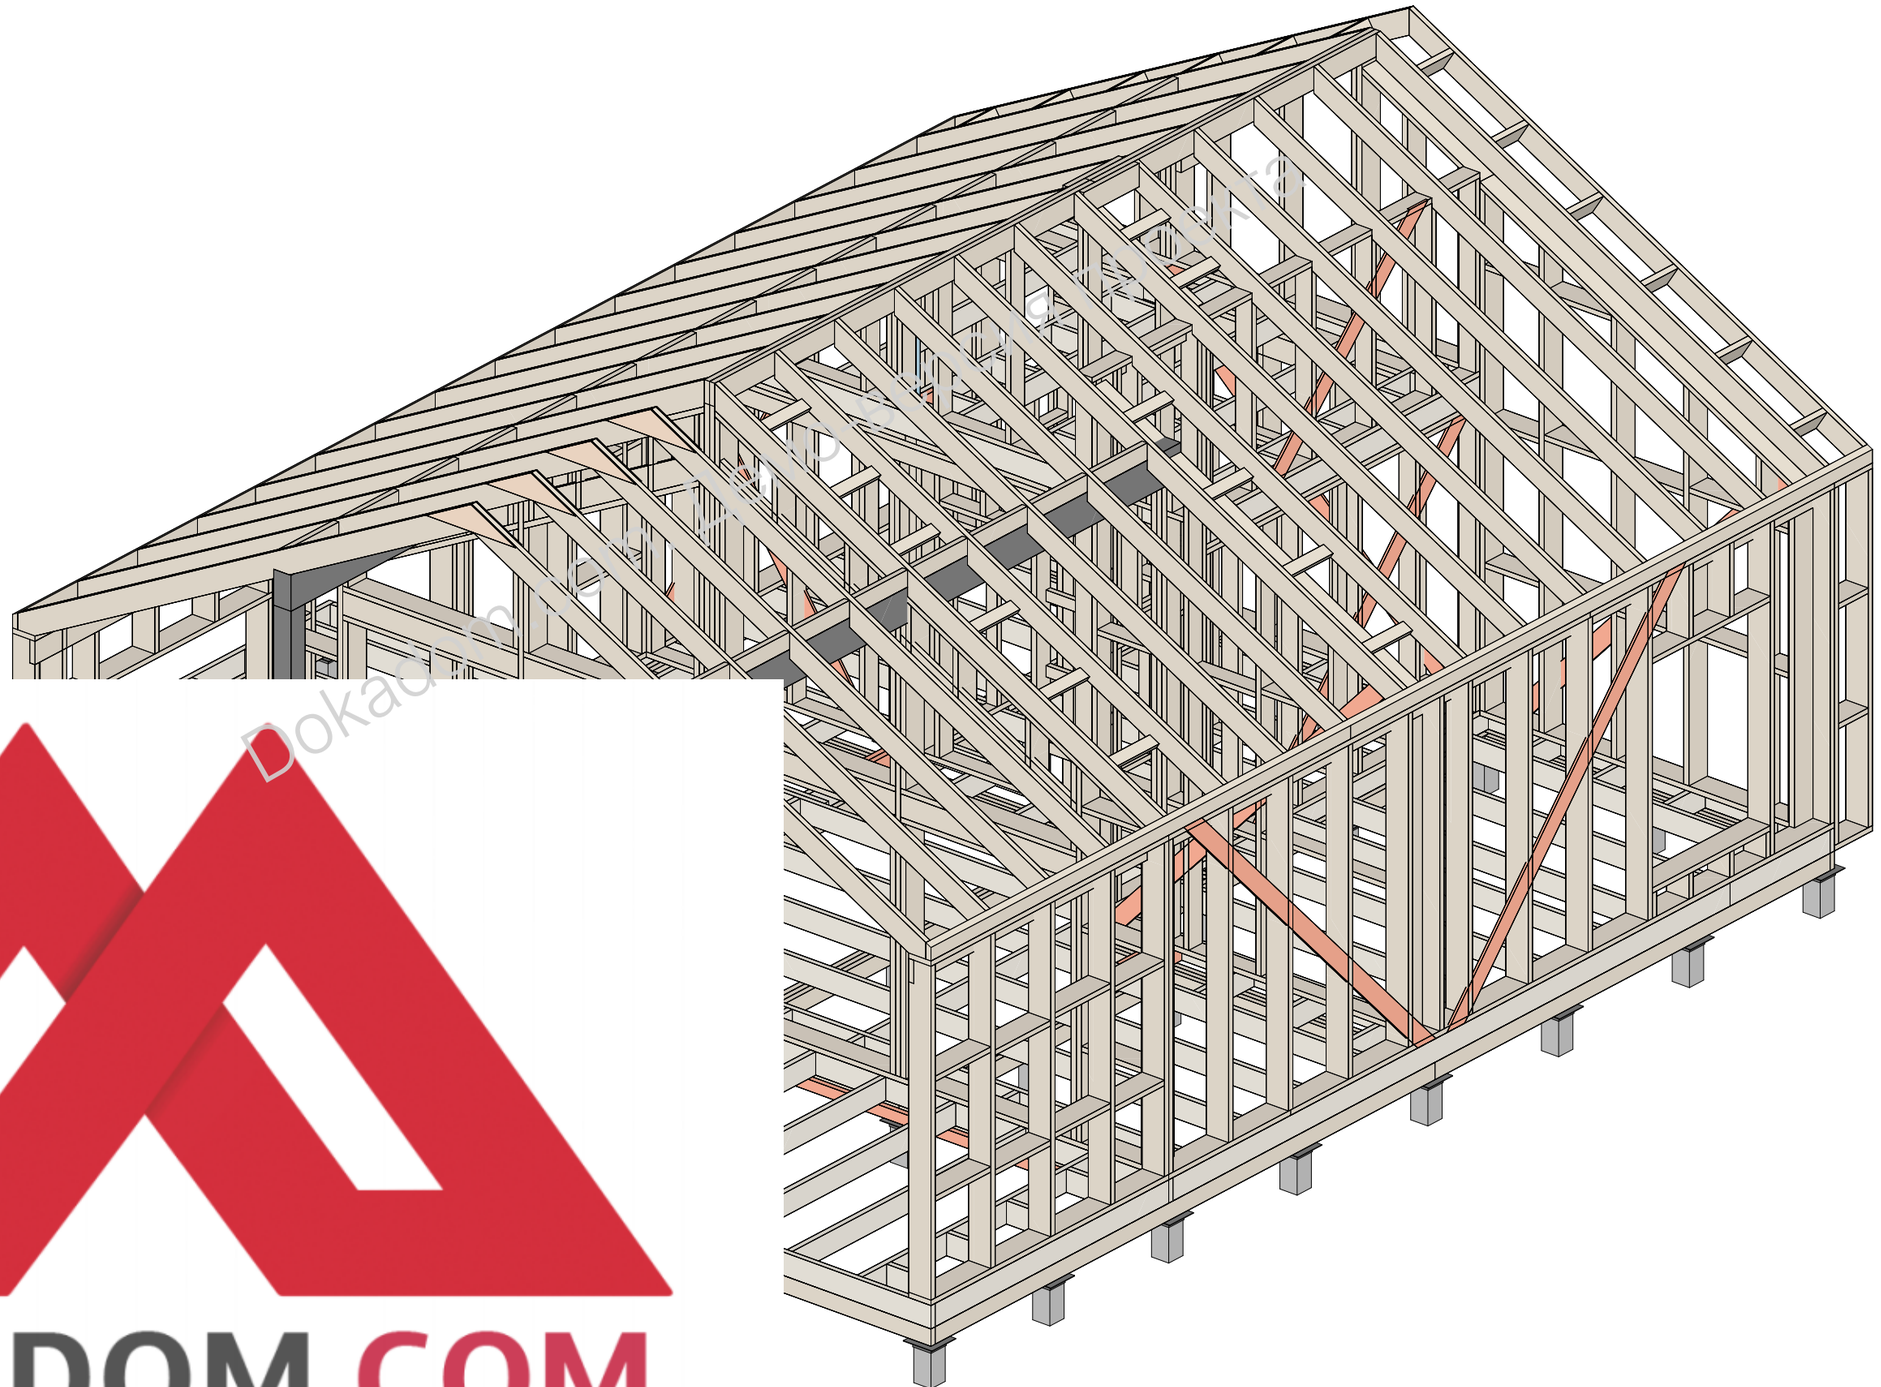


DOKADOM.COM
ДЕМО-ВЕРСИЯ ПРОЕКТА

DOKADOM.COM	Разработал	Мокеев Н.С.		"Марго" Раздел КР	Модель каркаса, вид 1	Лист 2
	Проверил	Маркович П.В.				
	Заказчик					

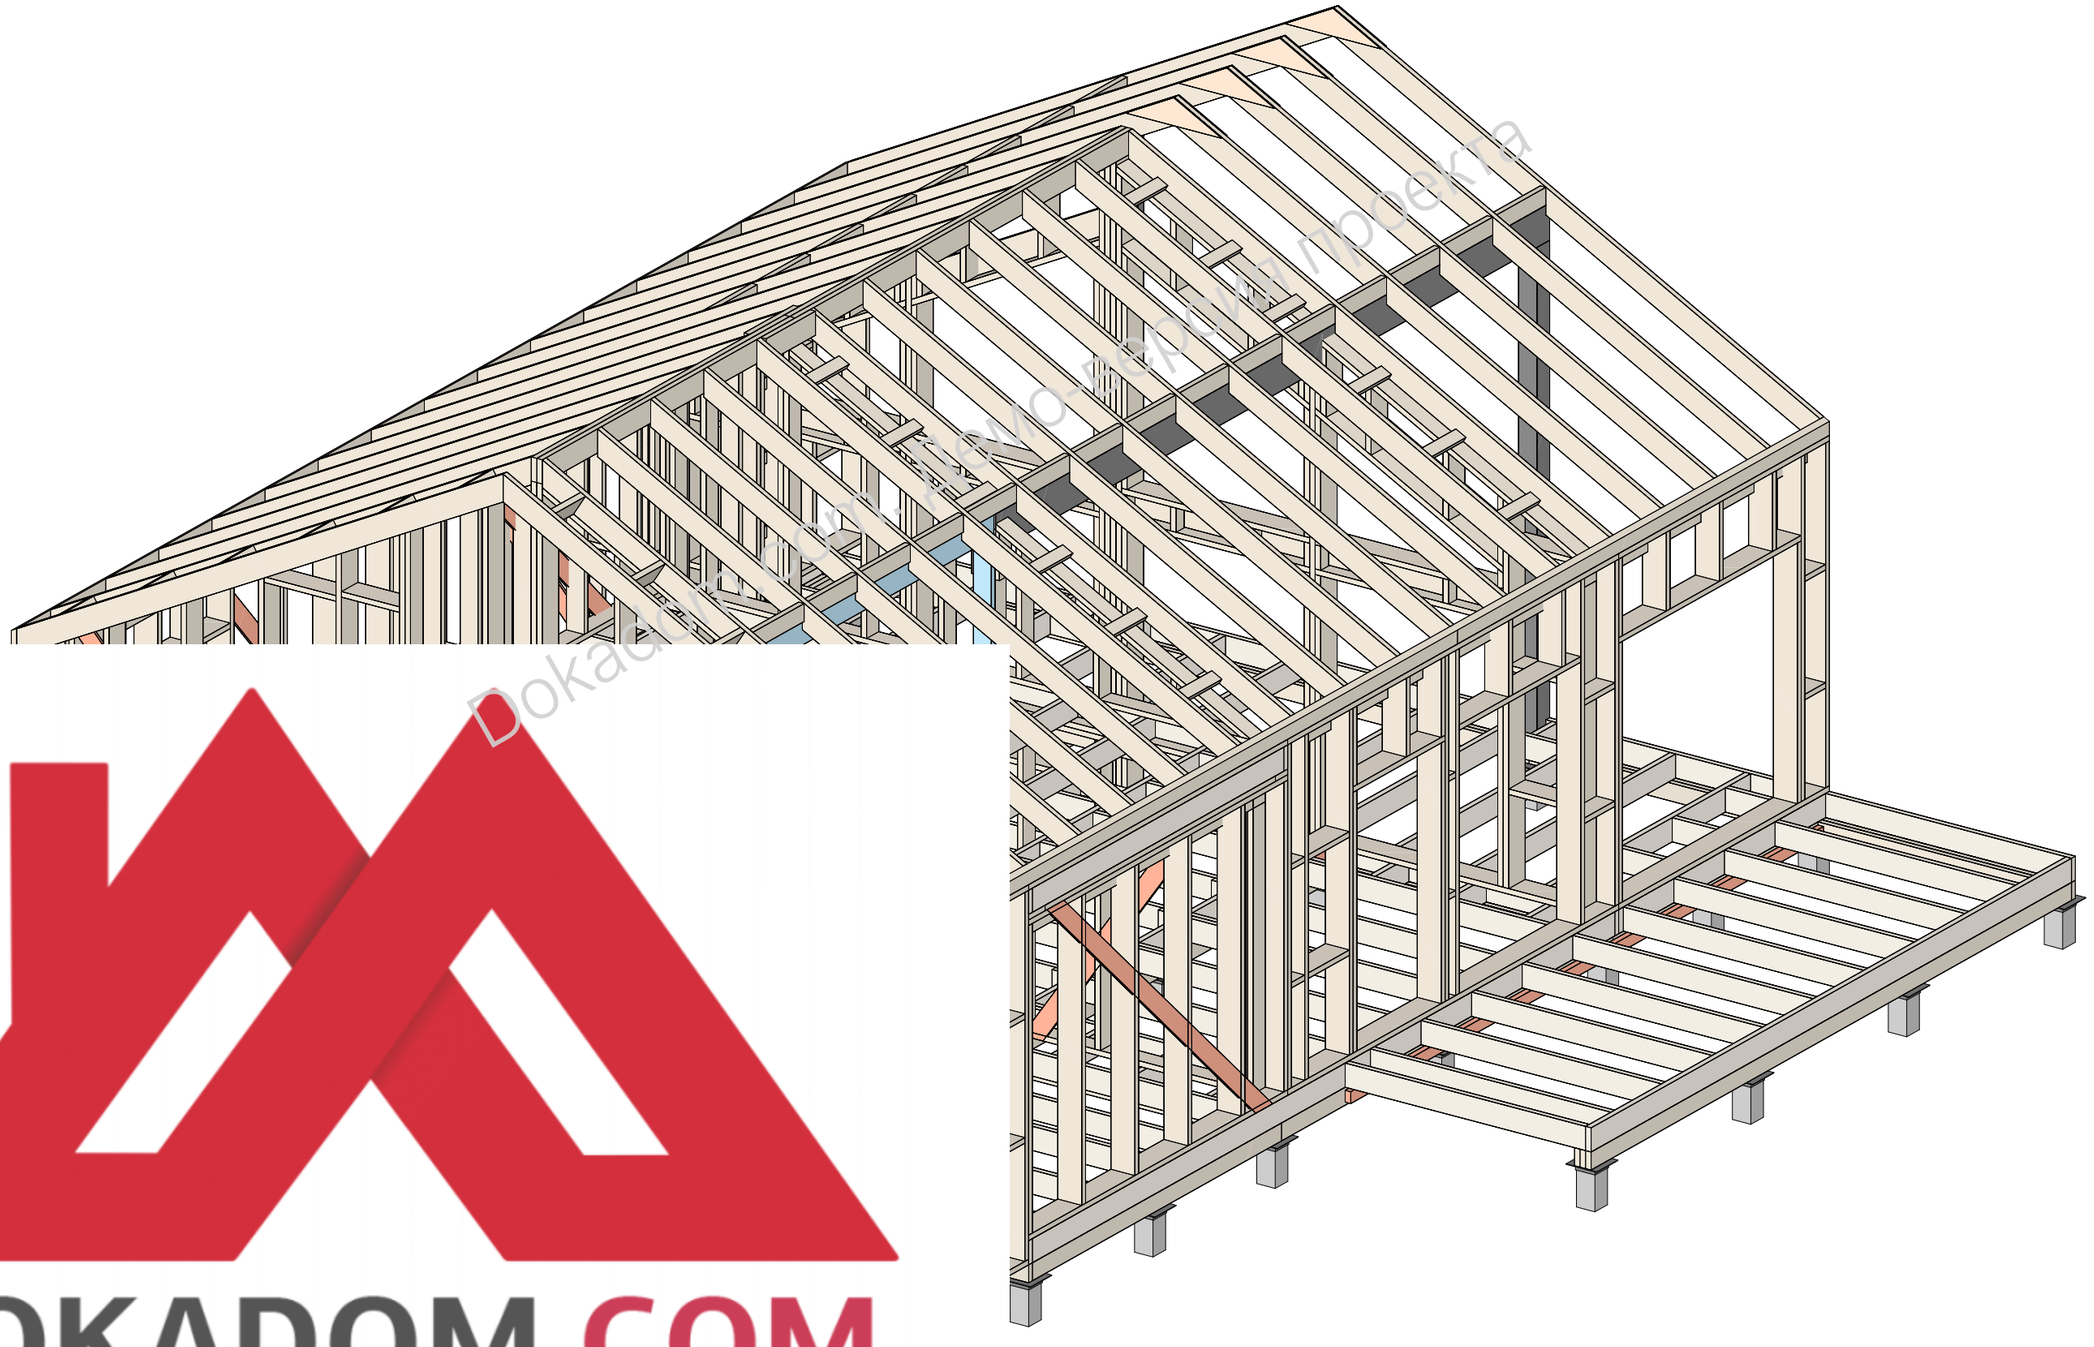

DOKADOM.COM
ДЕМО-ВЕРСИЯ ПРОЕКТА
Dokadom.com - демо-версия проекта


DOKADOM.COM	Разработал	Мокеев Н.С.		"Марго" Раздел КР	Модель каркаса, вид 2	Лист 3
	Проверил	Маркович П.В.				
	Заказчик					

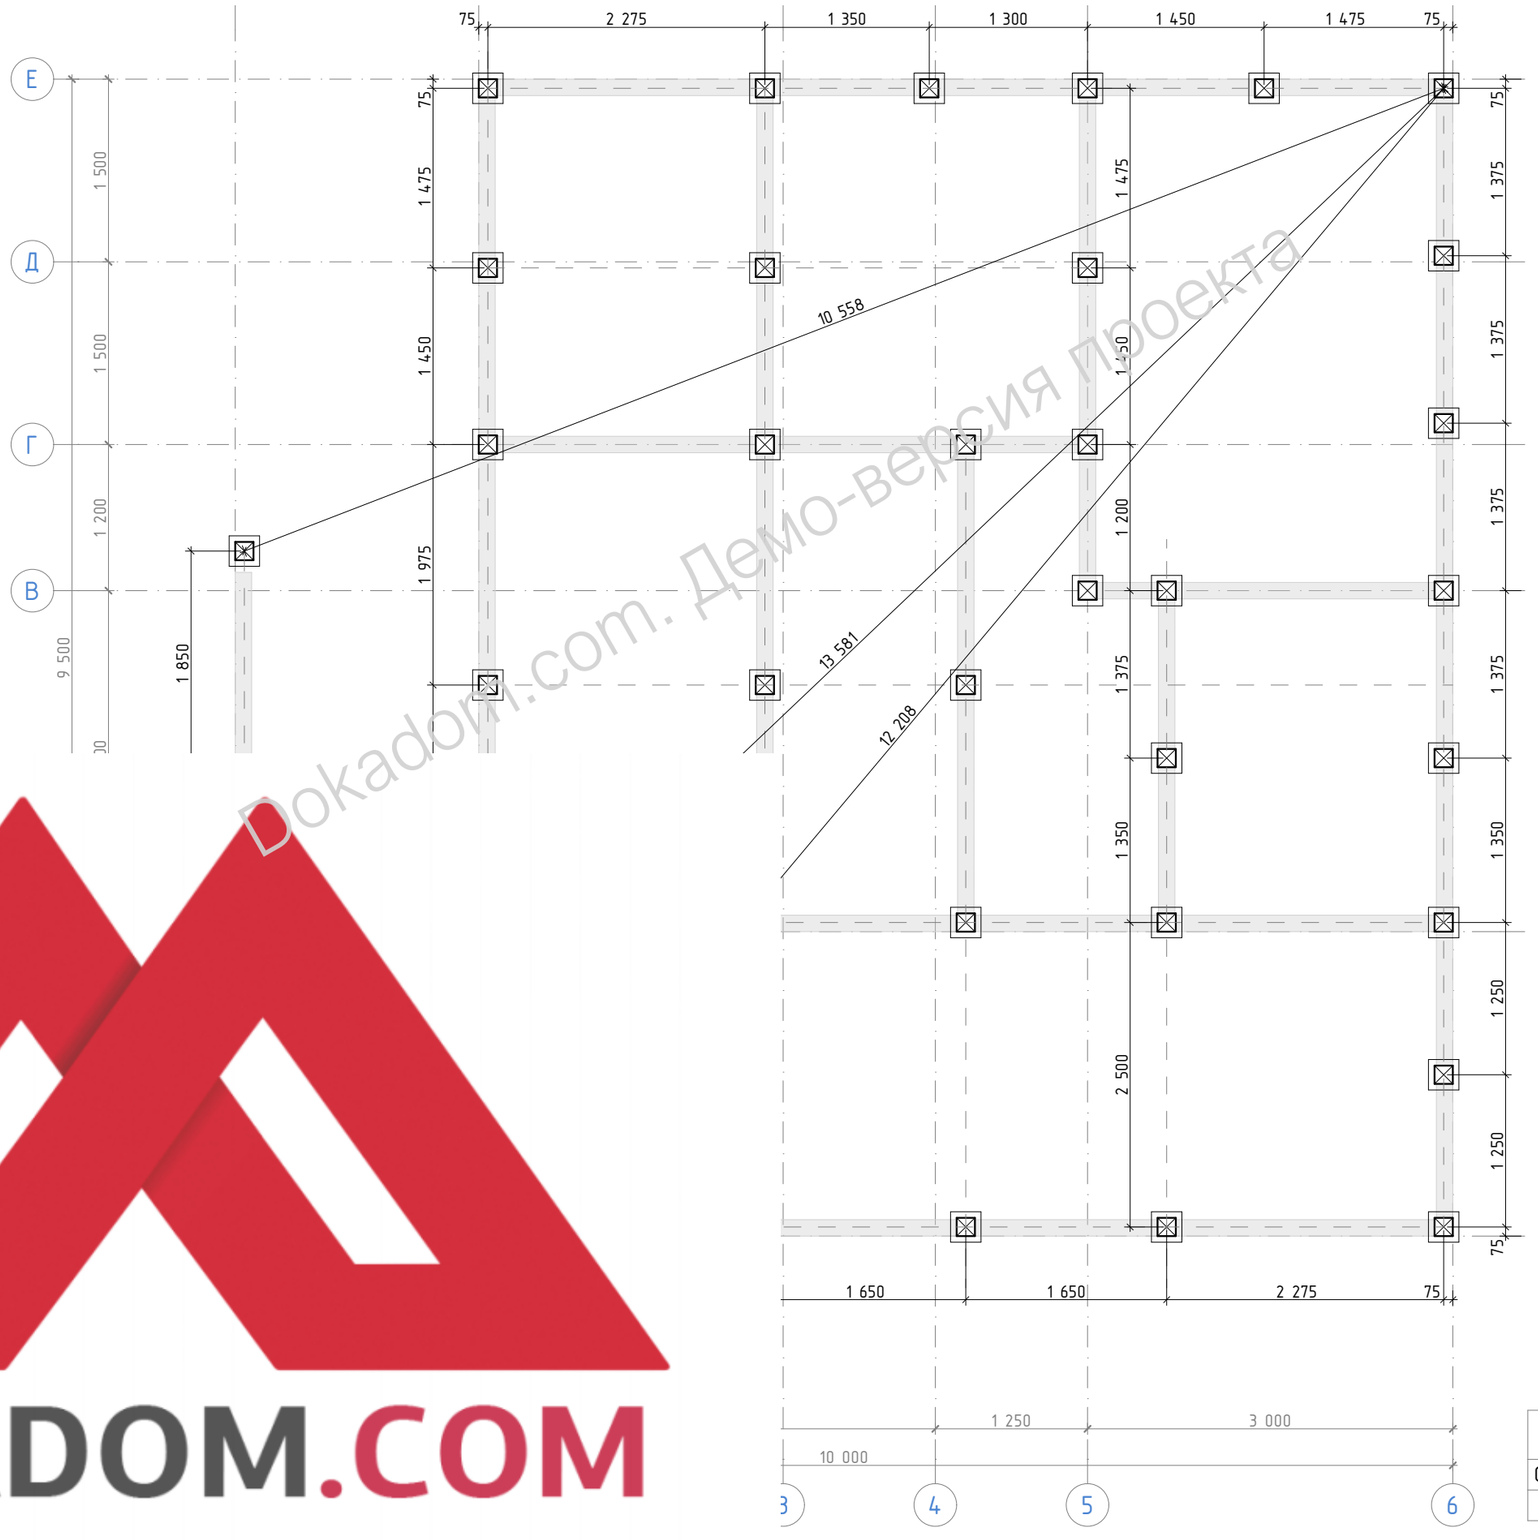

Наименование	Кол-во
Свая ж/б с оголовком	39
	39

DOKADOM.COM	Разработал	Мокеев Н.С.		"Марго" Раздел КР	План фундамента	Лист 3
	Проверил	Маркович П.В.				
	Заказчик					


Dokadom.com. Демо-версия Проекта
DOKADOM.COM
ДЕМО-ВЕРСИЯ ПРОЕКТА

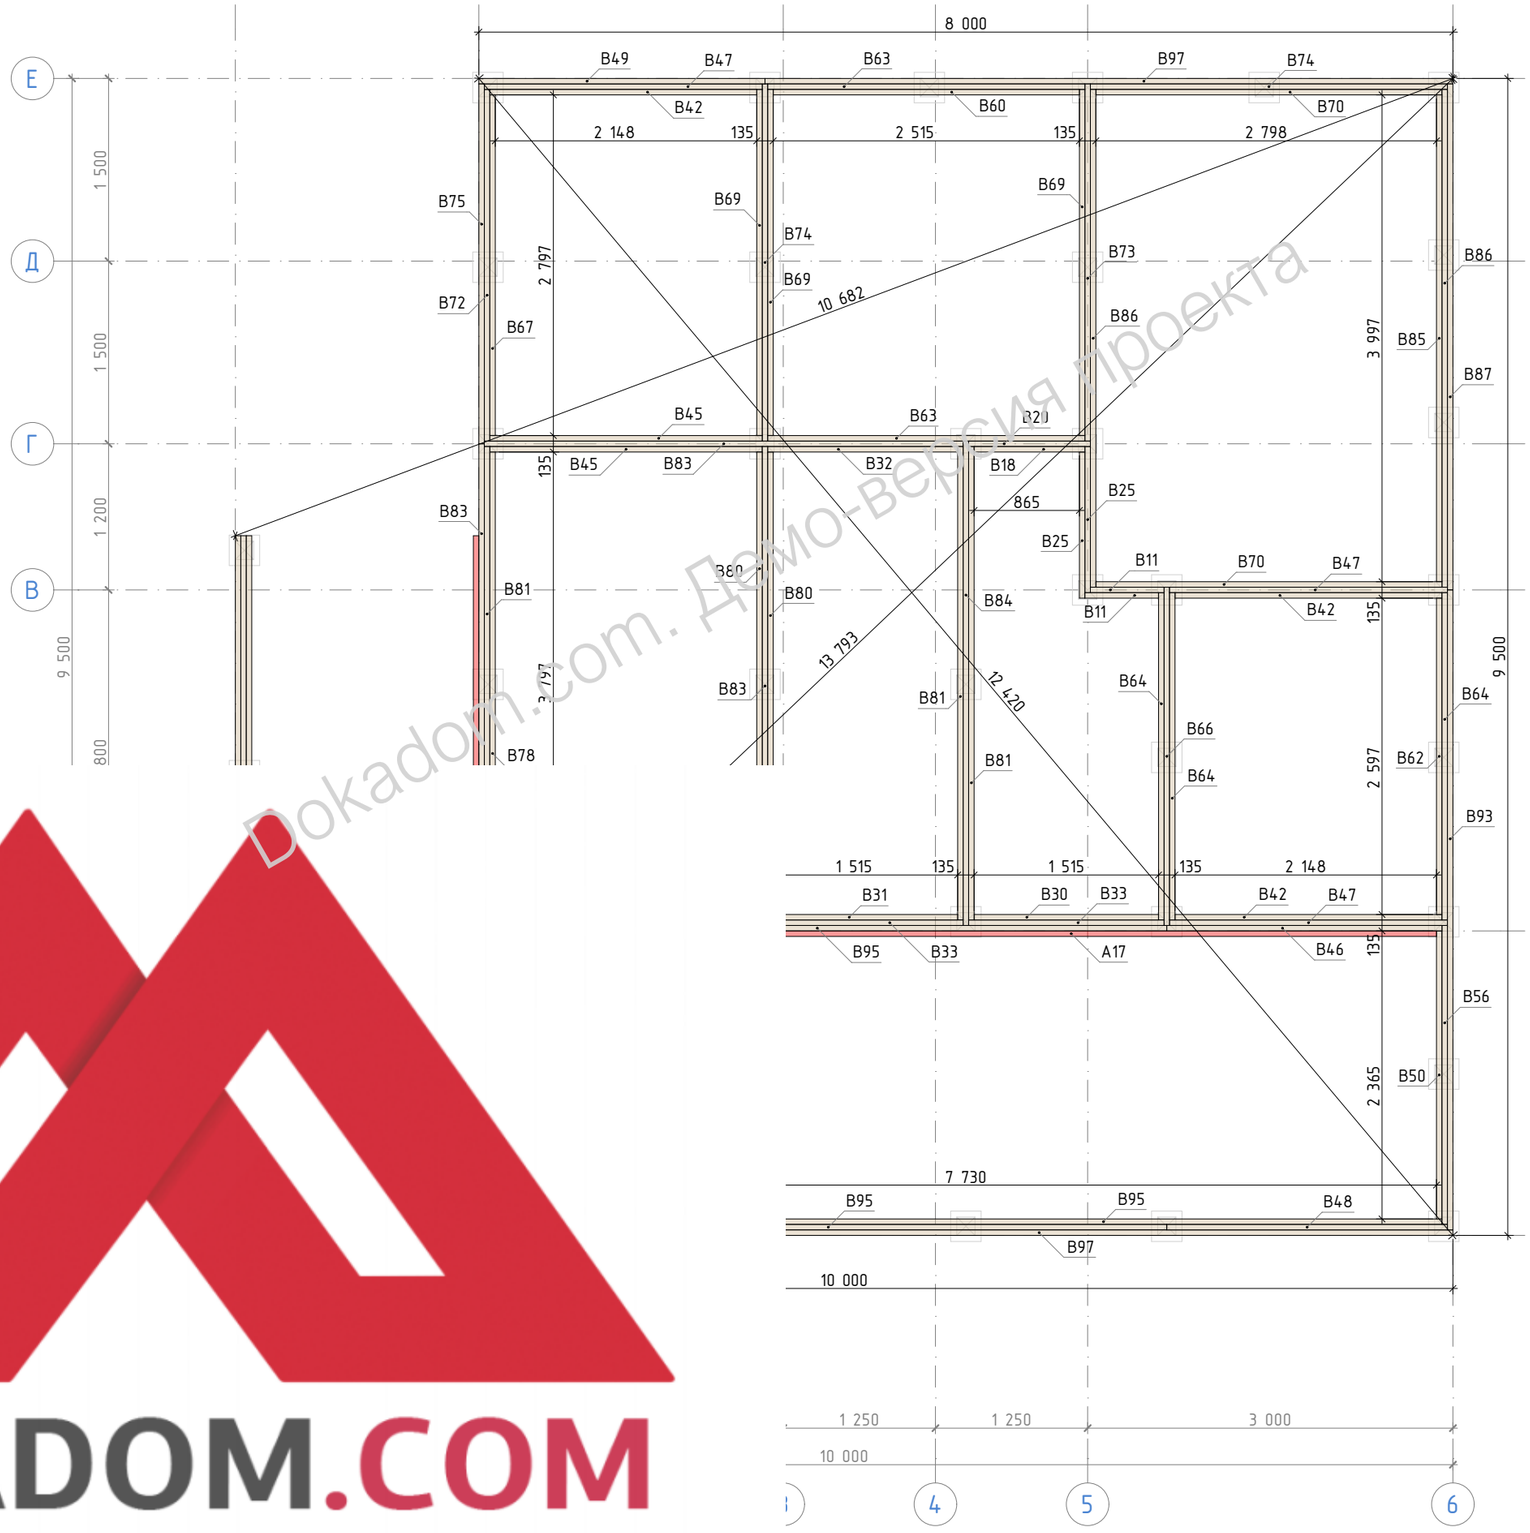

	Марка	Длина	Кол-во
Доска 45х145			
	B11	605	2
	B18	910	1
	B20	1 000	1
	B25	1 200	2
	B30	1 515	1
	B31	1 515	1
	B32	1 560	1
	B33	1 605	2
	B38	1 910	1
	B39	2 000	1
	B42	2 193	4
	B44	2 215	1
	B45	2 238	2
	B46	2 260	1
	B47	2 283	4
	B48	2 305	1
	B49	2 350	1
	B50	2 365	1
	B52	2 410	1
	B56	2 455	1
	B57	2 477	1
	B58	2 500	1
	B60	2 515	1
	B62	2 597	1
	B63	2 605	2
	B64	2 687	3
	B66	2 777	1
	B67	2 797	1
	B69	2 842	3
	B70	2 843	2
	B72	2 888	1
	B73	2 932	1
	B74	2 933	2
	B75	2 955	1
	B78	3 797	1
	B80	3 842	2
	B81	3 887	3
	B83	3 933	3
	B84	3 977	1
	B85	3 997	1
	B86	4 088	2
	B87	4 155	1
	B88	4 350	1
	B93	5 255	1
	B95	5 560	3
	B96	5 610	1
	B97	5 650	2
	B98	5 655	1
	B99	5 700	1
Доска 45х95			
	A11	1 730	1
	A16	5 610	1
	A17	6 000	1

OKADOM.COM	Разработал	Мокеев Н.С.		"Марго" Раздел КР	Схема монтажа обвязки свай
	Проверил	Маркович П.В.			Лист 5
	Заказчик				

Dokadom.com. Демо-версия проекта
DOKADOM.COM
ДЕМО-ВЕРСИЯ ПРОЕКТА

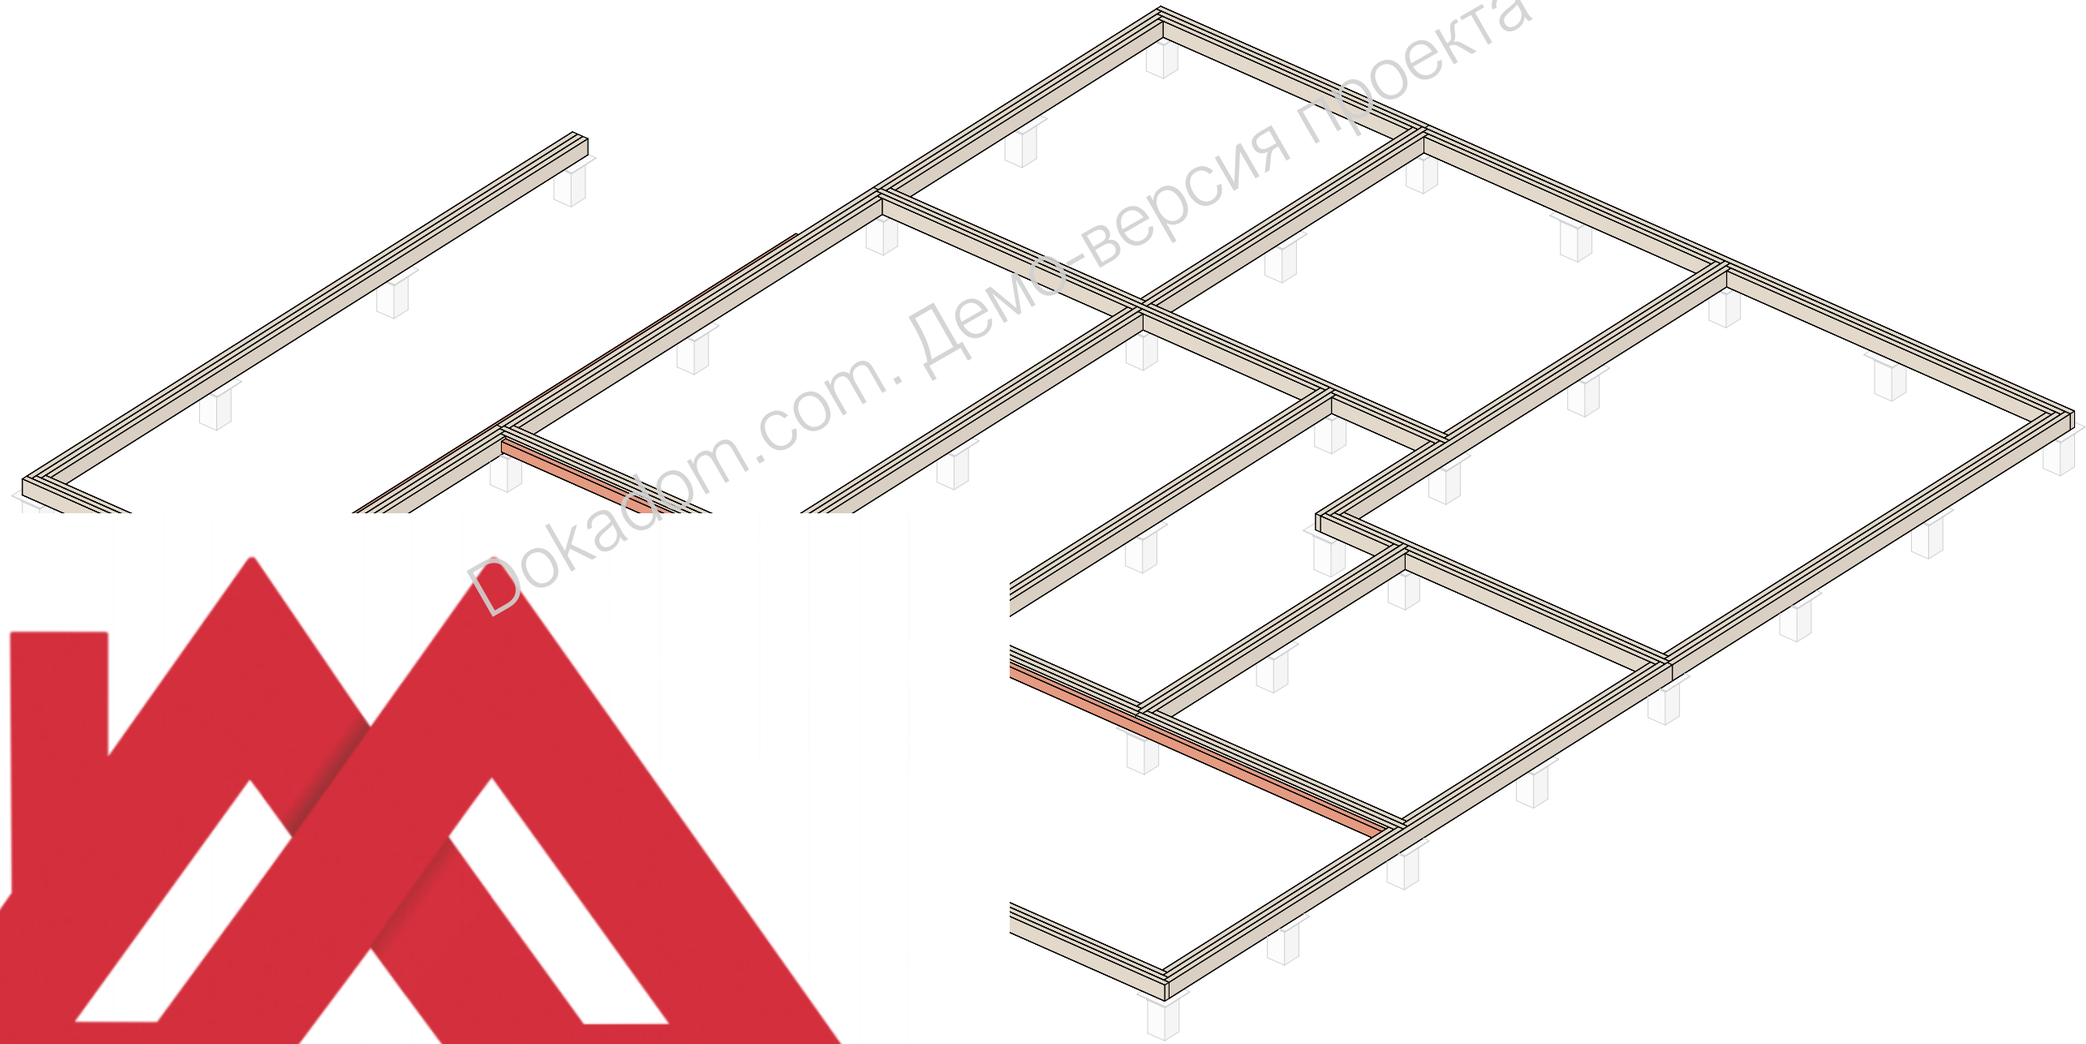


Dokadom.com. Демо-версия проекта

DOKADOM.COM
ДЕМО-ВЕРСИЯ ПРОЕКТА


OKADOM.COM	Разработал	Мокеев Н.С.		"Марго" Раздел КР	Модель обвязки свай и подкладочной доски	Лист 6
	Проверил	Маркович П.В.				
	Заказчик					

Ф3.01 **Угловое соединение**

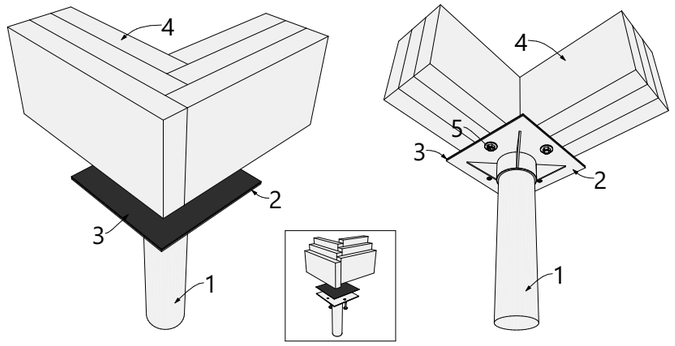


1-свая винтовая; 2-оголовок сваи; 3-рубероид ГОСТ 10923-93; 4-доска;
5-болт сантехнический 10x140 DIN 571 с шайбой DIN 9021.

Ф3.02 **Продольное соединение**

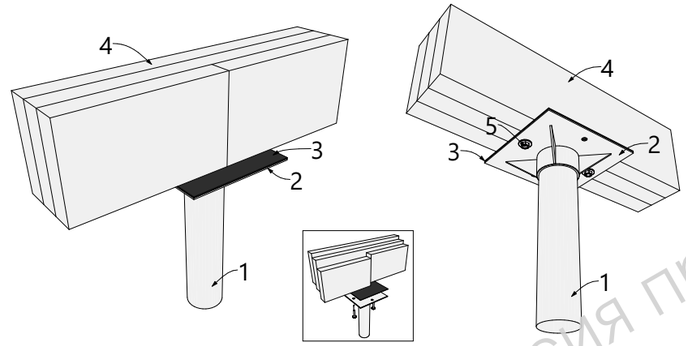


1-свая винтовая; 2-оголовок сваи; 3-рубероид ГОСТ 10923-93; 4-доска;
5-болт сантехнический 10x140 DIN 571 с шайбой DIN 9021.

Ф3.03 **Т-образное соединение 1**

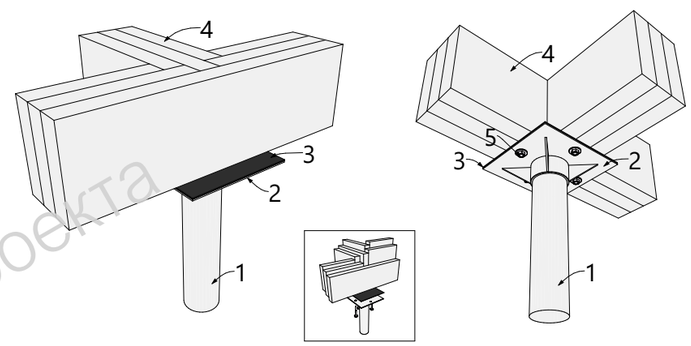


1-свая винтовая; 2-оголовок сваи; 3-рубероид ГОСТ 10923-93; 4-доска;
5-болт сантехнический 10x140 DIN 571 с шайбой DIN 9021.

Ф3.04 **Т-образное соединение 2**

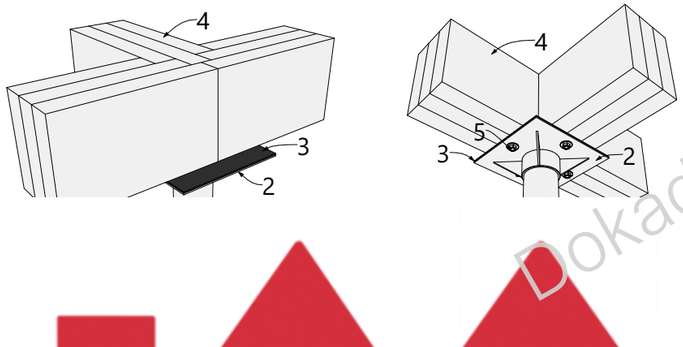


3-рубероид ГОСТ 10923-93; 4-доска;
10 DIN 571 с шайбой DIN 9021.

Ф3.05 **Х-образное соединение 1**

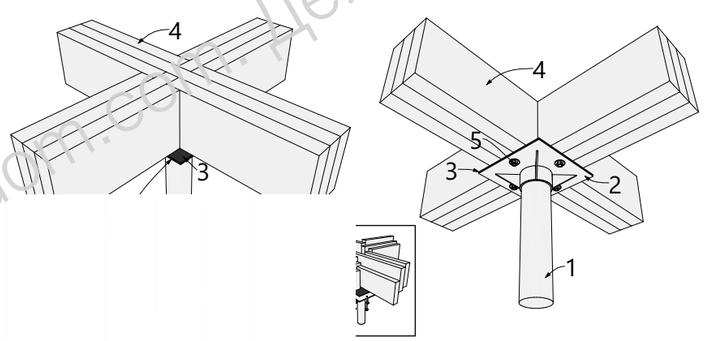


Ф3.06 **Х-образное соединение 2**

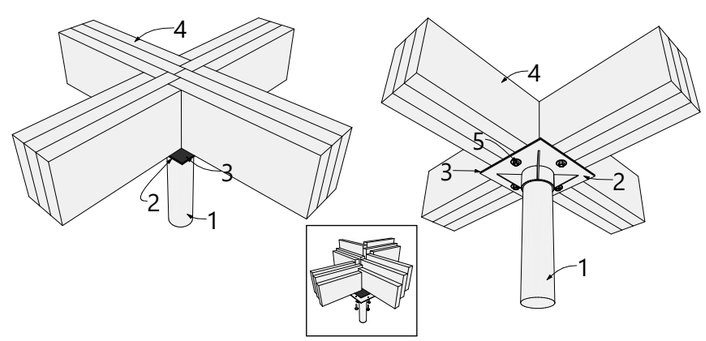

1-свая винтовая; 2-оголовок сваи; 3-рубероид ГОСТ 10923-93; 4-доска;
5-болт сантехнический 10x140 DIN 571 с шайбой DIN 9021.

Dokadom.com. Демо-версия проекта
DOKADOM.COM
ДЕМО-ВЕРСИЯ ПРОЕКТА


OKADOM.COM	Разработал	Мокеев Н.С.		"Марго" Раздел КР	Узлы обвязки свай	Лист 7
	Проверил	Маркович П.В.				
	Заказчик					

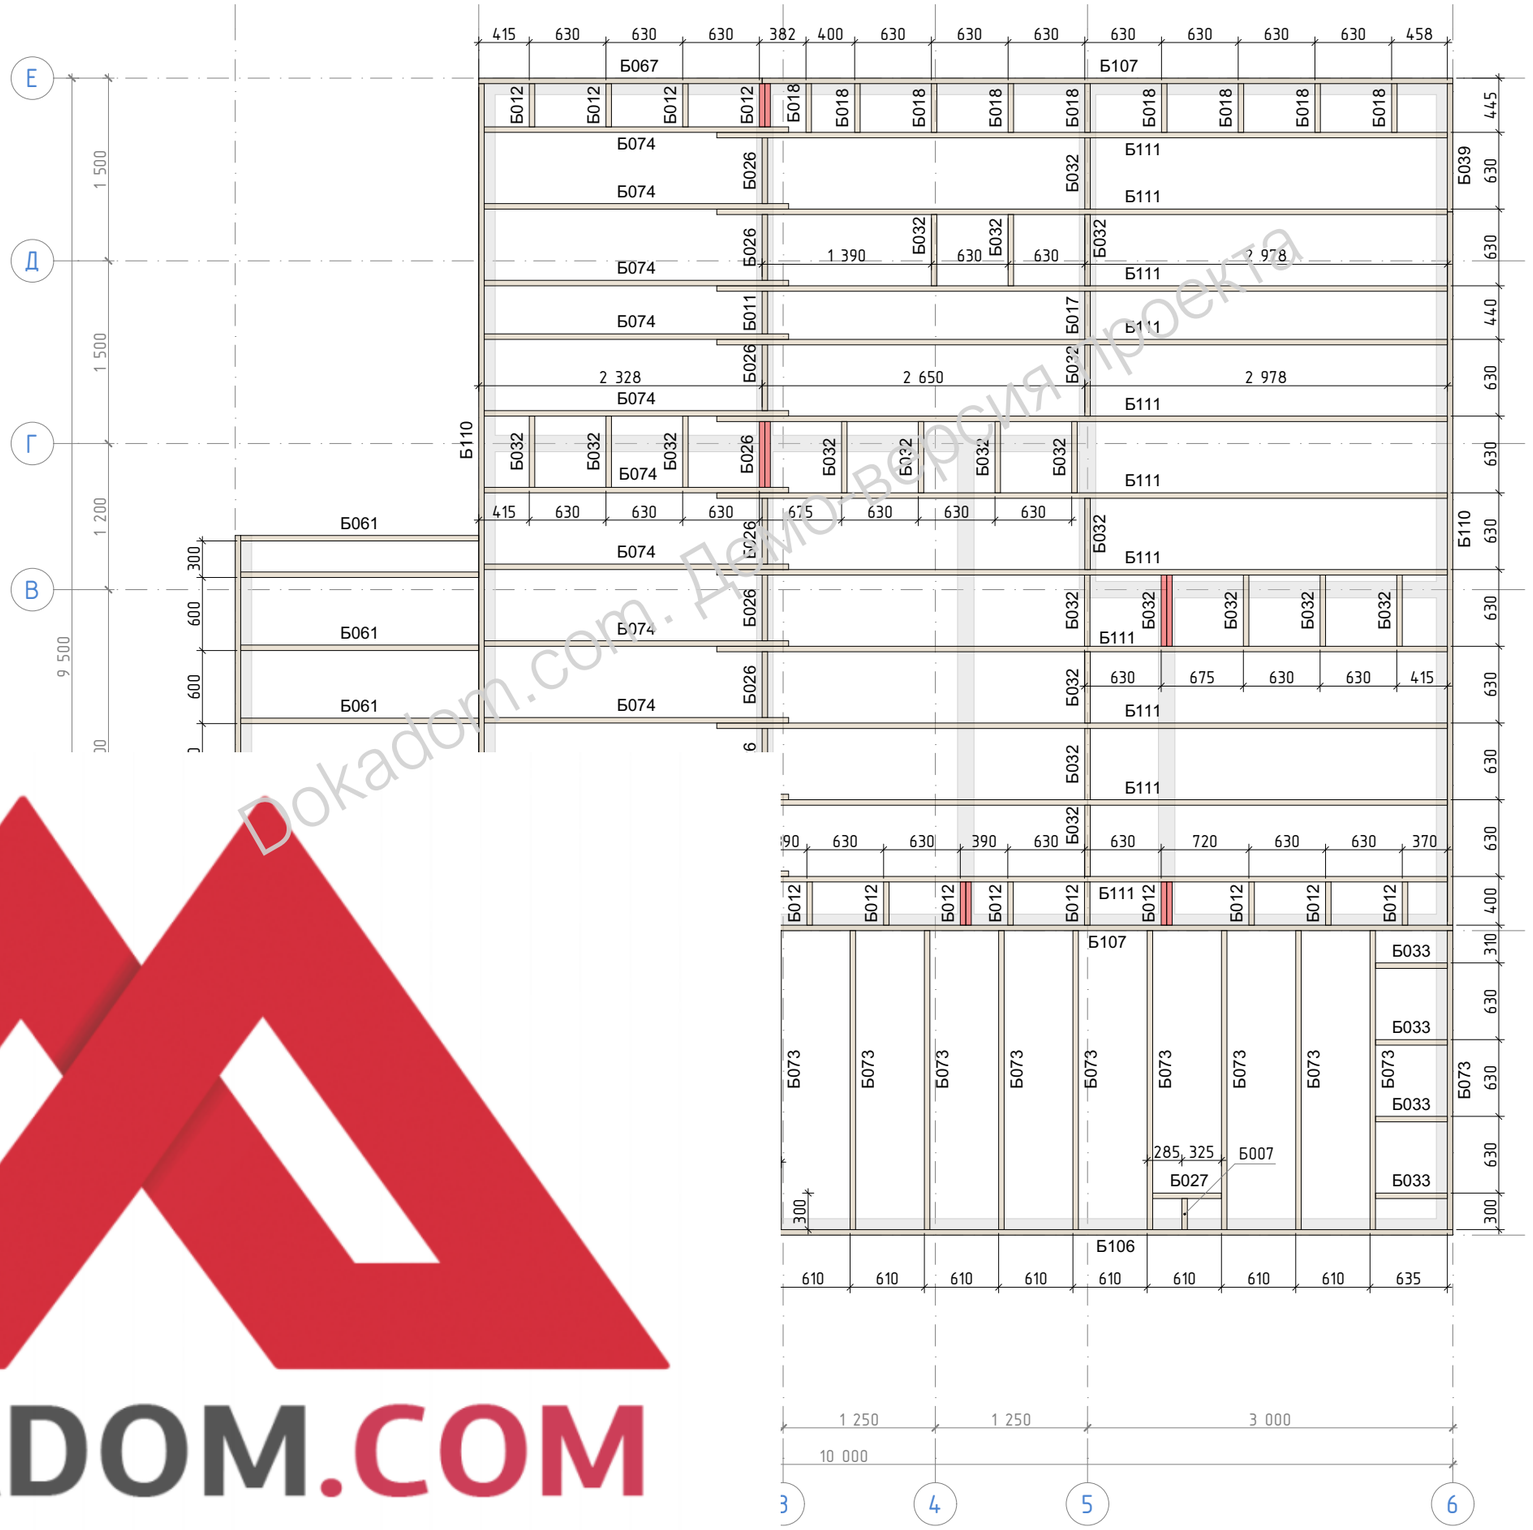

	Марка	Длина	Кол-во
Доска 45х195			
	Б007	255	2
	Б011	350	1
	Б012	355	18
	Б017	395	1
	Б018	400	12
	Б026	540	10
	Б027	565	6
	Б032	585	22
	Б033	590	4
	Б039	1 053	2
	Б061	1 955	10
	Б067	2 328	2
	Б073	2 455	14
	Б074	2 500	11
	Б099	4 463	1
	Б106	5 538	1
	Б107	5 672	2
	Б108	5 700	1
	Б110	5 858	2
	Б111	6 000	11

DOKADOM.COM	Разработал	Мокеев Н.С.		"Марго" Раздел КР	Схема сборки цокольного перекрытия
	Проверил	Маркович П.В.			Лист 8
	Заказчик				

Dokadom.com. Демо-версия проекта
DOKADOM.COM
ДЕМО-ВЕРСИЯ ПРОЕКТА

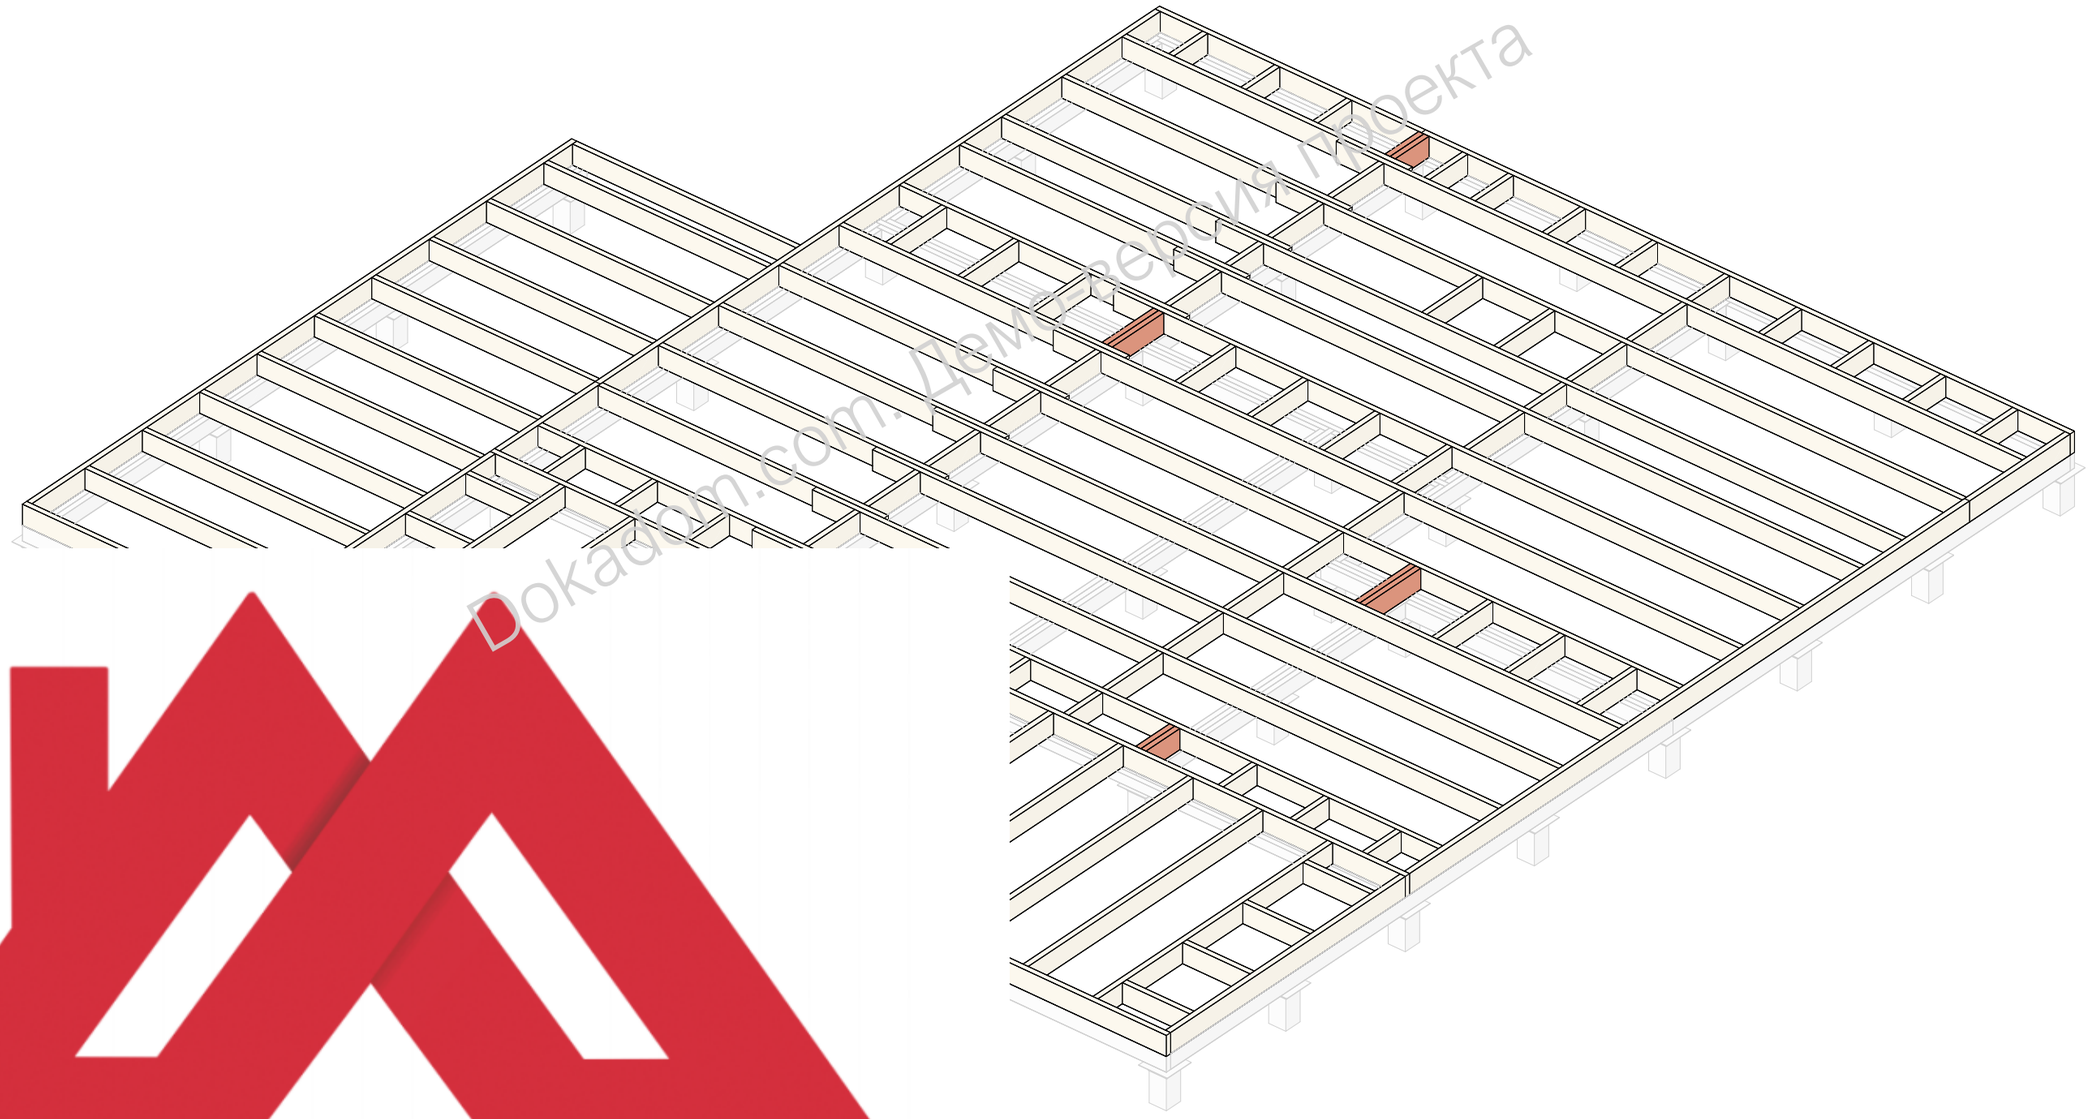


Dokadom.com. Демо-версия проекта

DOKADOM.COM
ДЕМО-ВЕРСИЯ ПРОЕКТА


OKADOM.COM	Разработал	Мокеев Н.С.		"Марго" Раздел КР	Модель цокольного перекрытия	Лист 9
	Проверил	Маркович П.В.				
	Заказчик					

П1.01 Крепление обвязочной доски перекрытия

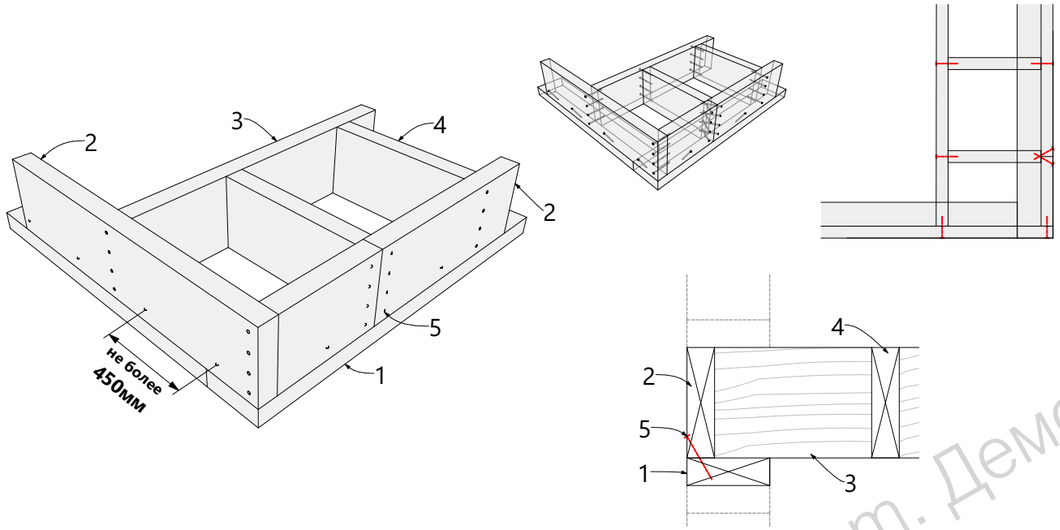


1-опорная доска/вторая верхняя обвязка стены; 2-обвязочная доска перекрытия; 3-балка перекрытия;
4-блок балка (перемычка); 5-гвоздь.

П1.08 Продольное соединение балок перекрытия на опоре

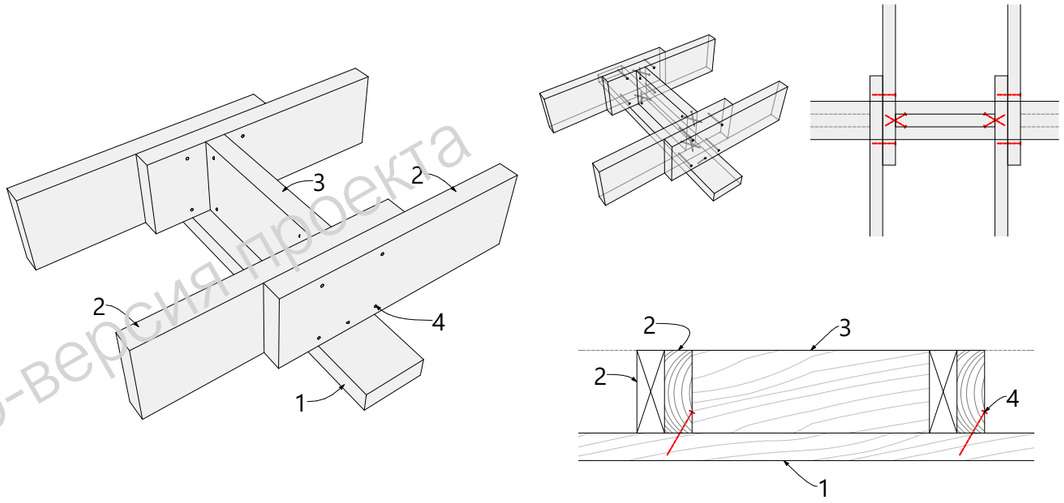

1-опорная доска/вторая верхняя обвязка стены; 2-балка перекрытия;
3-блок балка (перемычка); 4-гвоздь.

П1.06 Крепление распорок под стеной между балками перекрытия

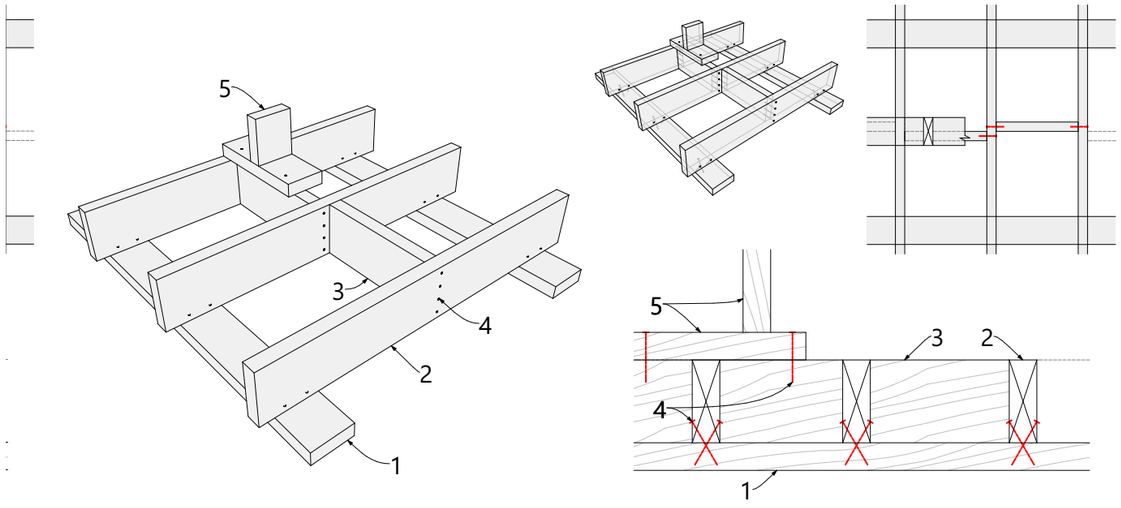


1-опорная доска/вторая верхняя обвязка стены; 2-балка перекрытия;
3-блок балка (перемычка/распорка); 4-гвоздь; 5-каркас стены.

Dokadom.com. Демо-версия проекта
DOKADOM.COM
ДЕМО-ВЕРСИЯ ПРОЕКТА

DOKADOM.COM	Разработал	Мокеев Н.С.		"Марго" Раздел КР	Узлы перекрытий 1	Лист 10
	Проверил	Маркович П.В.				
	Заказчик					

П1.09 Гвоздевое соединение балок перекрытия

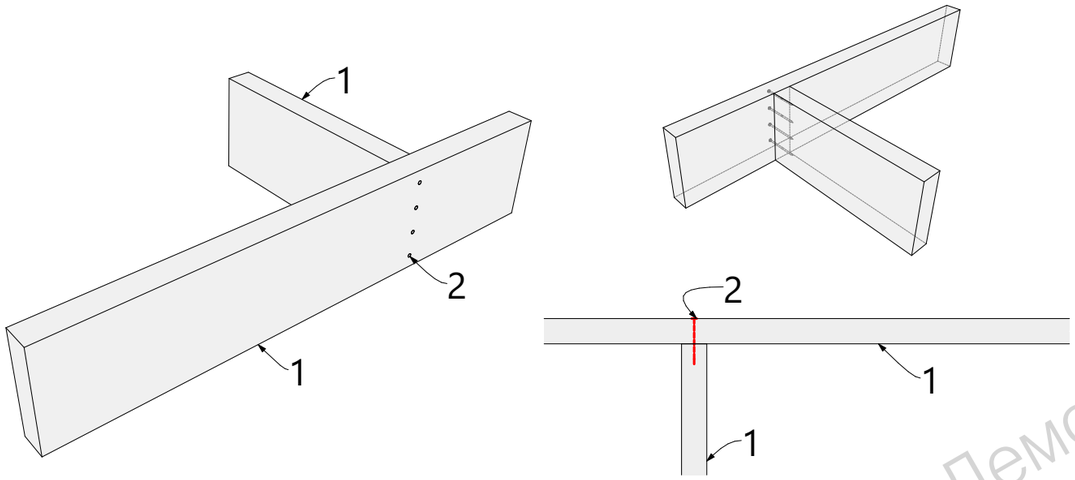


1-балка перекрытия; 2-гвоздь.

А1.01 Кол-во гвоздей по сечению пиломатериала

h - до 100мм
не менее двух гвоздей в торец


h - до 150мм
не менее трех гвоздей в торец

h - до 200мм
не менее четырех гвоздей в торец

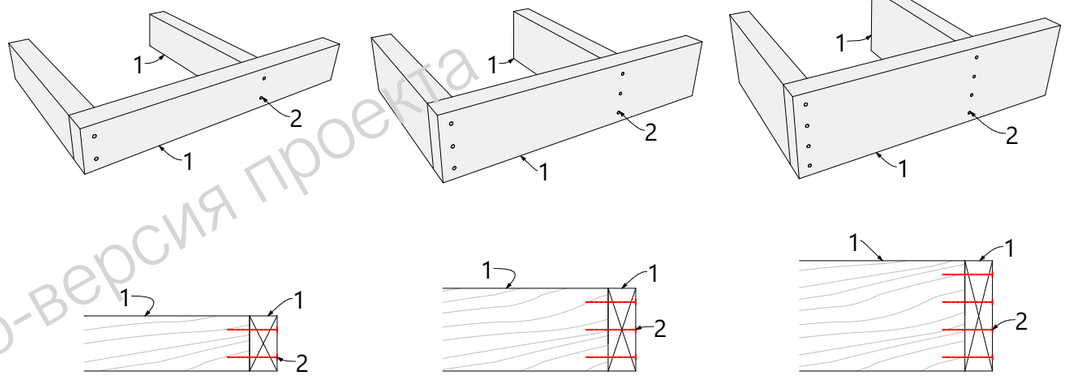

1-доска; 2-гвоздь.
h - высота сечения доски.


П1.03 Крепление блок балок под стеной

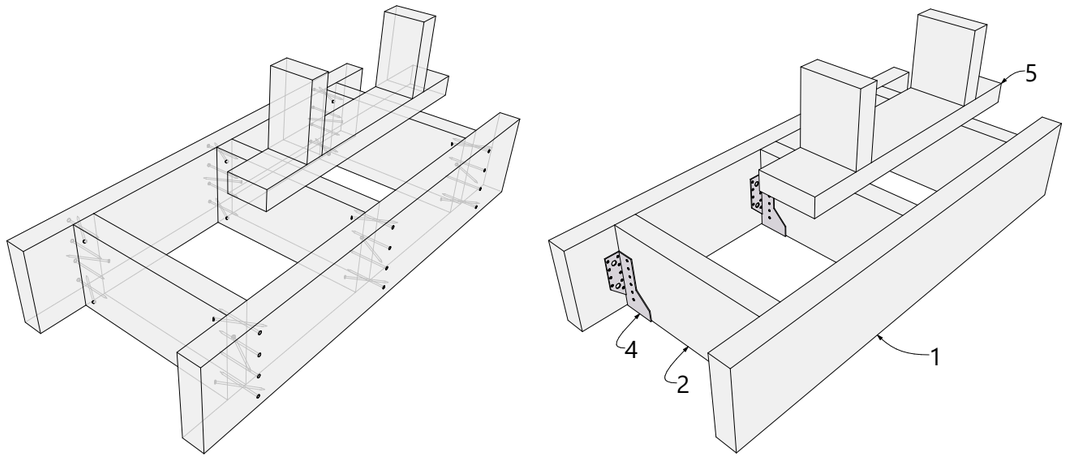

1-балка перекрытия; 2-блок балка (перемычка); 3-гвоздь;
4-металлическая опора бруса; 5-каркас стены.


Dokadom.com. Демо-версия проекта
DOKADOM.COM
ДЕМО-ВЕРСИЯ ПРОЕКТА

DOKADOM.COM	Разработал	Мокеев Н.С.		"Марго" Раздел КР	Узлы перекрытий 2	Лист 11
	Проверил	Маркович П.В.				
	Заказчик					

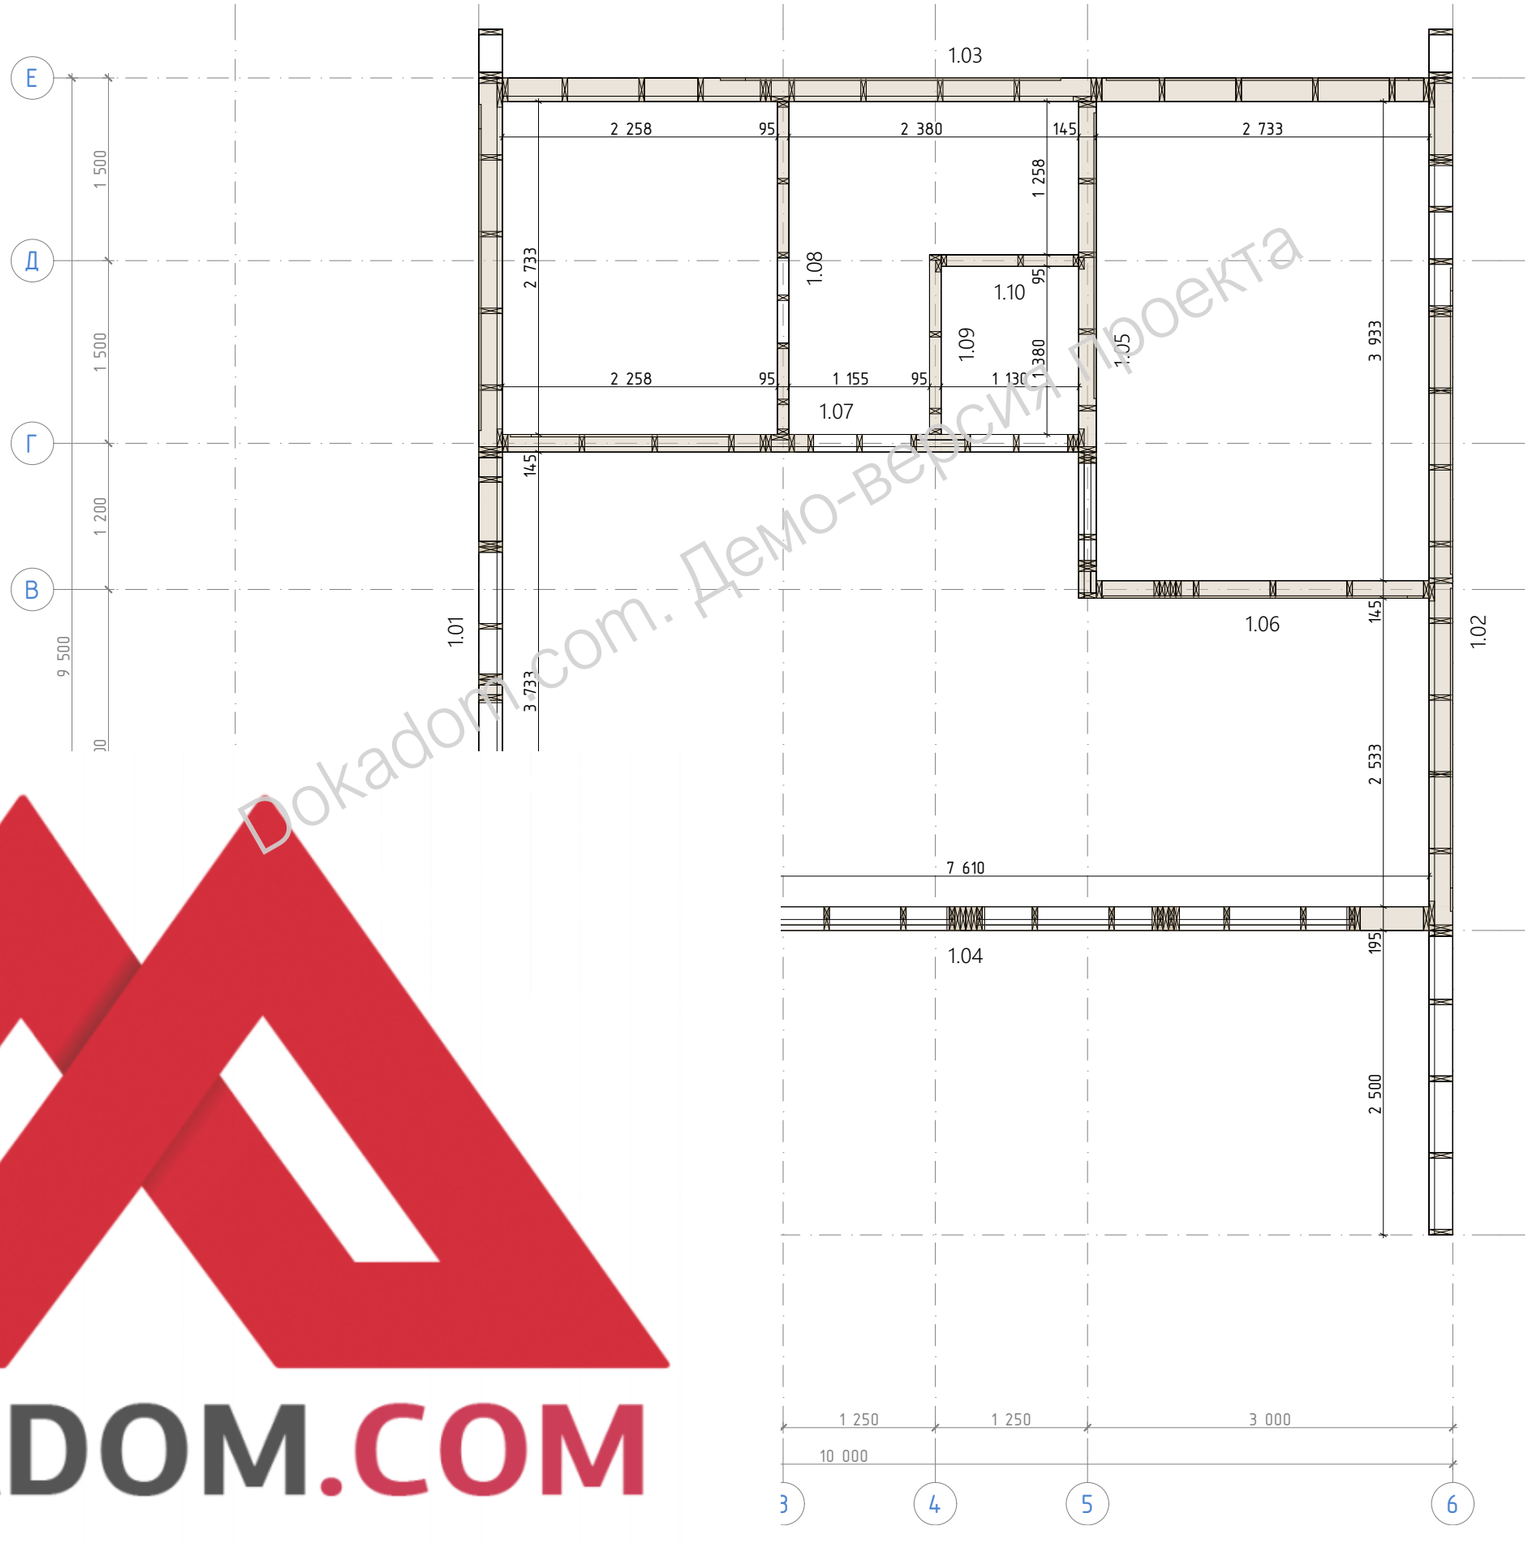

Dokadom.com. Демо-версия проекта
DOKADOM.COM
ДЕМО-ВЕРСИЯ ПРОЕКТА

DOKADOM.COM	Разработал	Мокеев Н.С.		"Марго" Раздел КР	Схема монтажа стен 1-го этажа	Лист 12
	Проверил	Маркович П.В.				
	Заказчик					

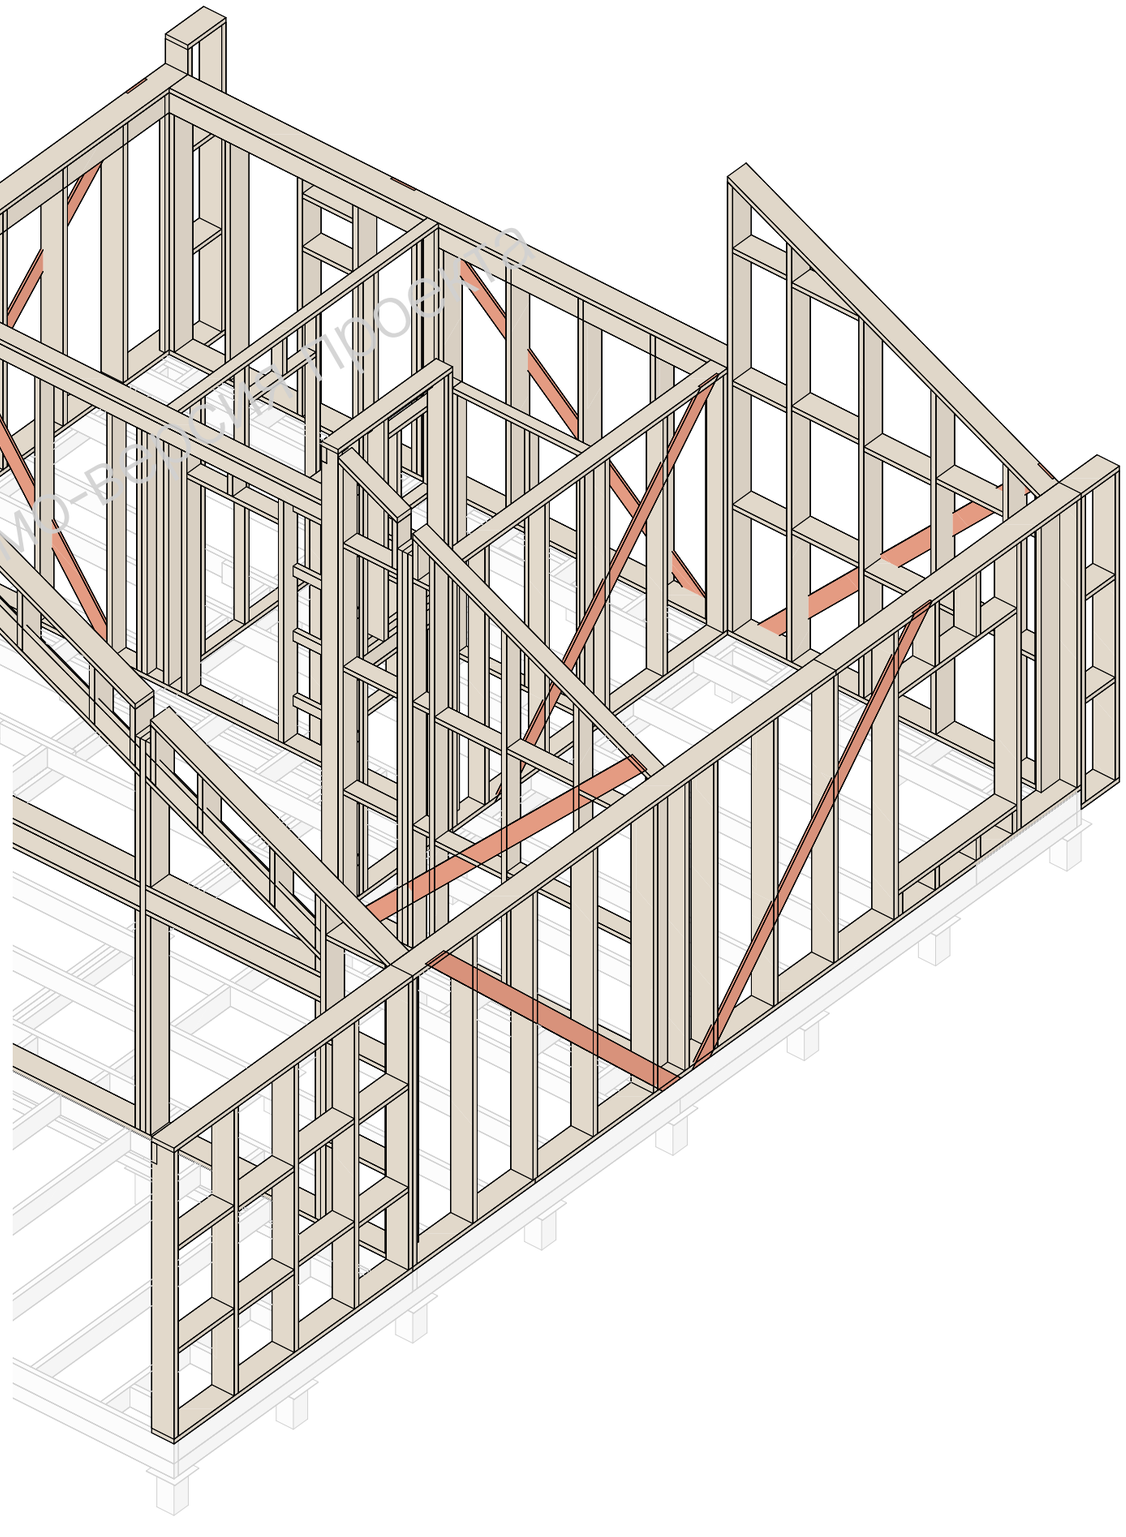


DOKADOM.COM
ДЕМО-ВЕРСИЯ ПРОЕКТА

DOKADOM.COM	Разработал	Мокеев Н.С.		"Марго" Раздел КР	Модель стен 1-го этажа	Лист 13
	Проверил	Маркович П.В.				
	Заказчик					



DOKADOM.COM
ДЕМО-ВЕРСИЯ ПРОЕКТА

DOKADOM.COM	Разработал	Мокеев Н.С.		"Марго" Раздел КР	Модель стен 1-го этажа	Лист 14
	Проверил	Маркович П.В.				
	Заказчик					

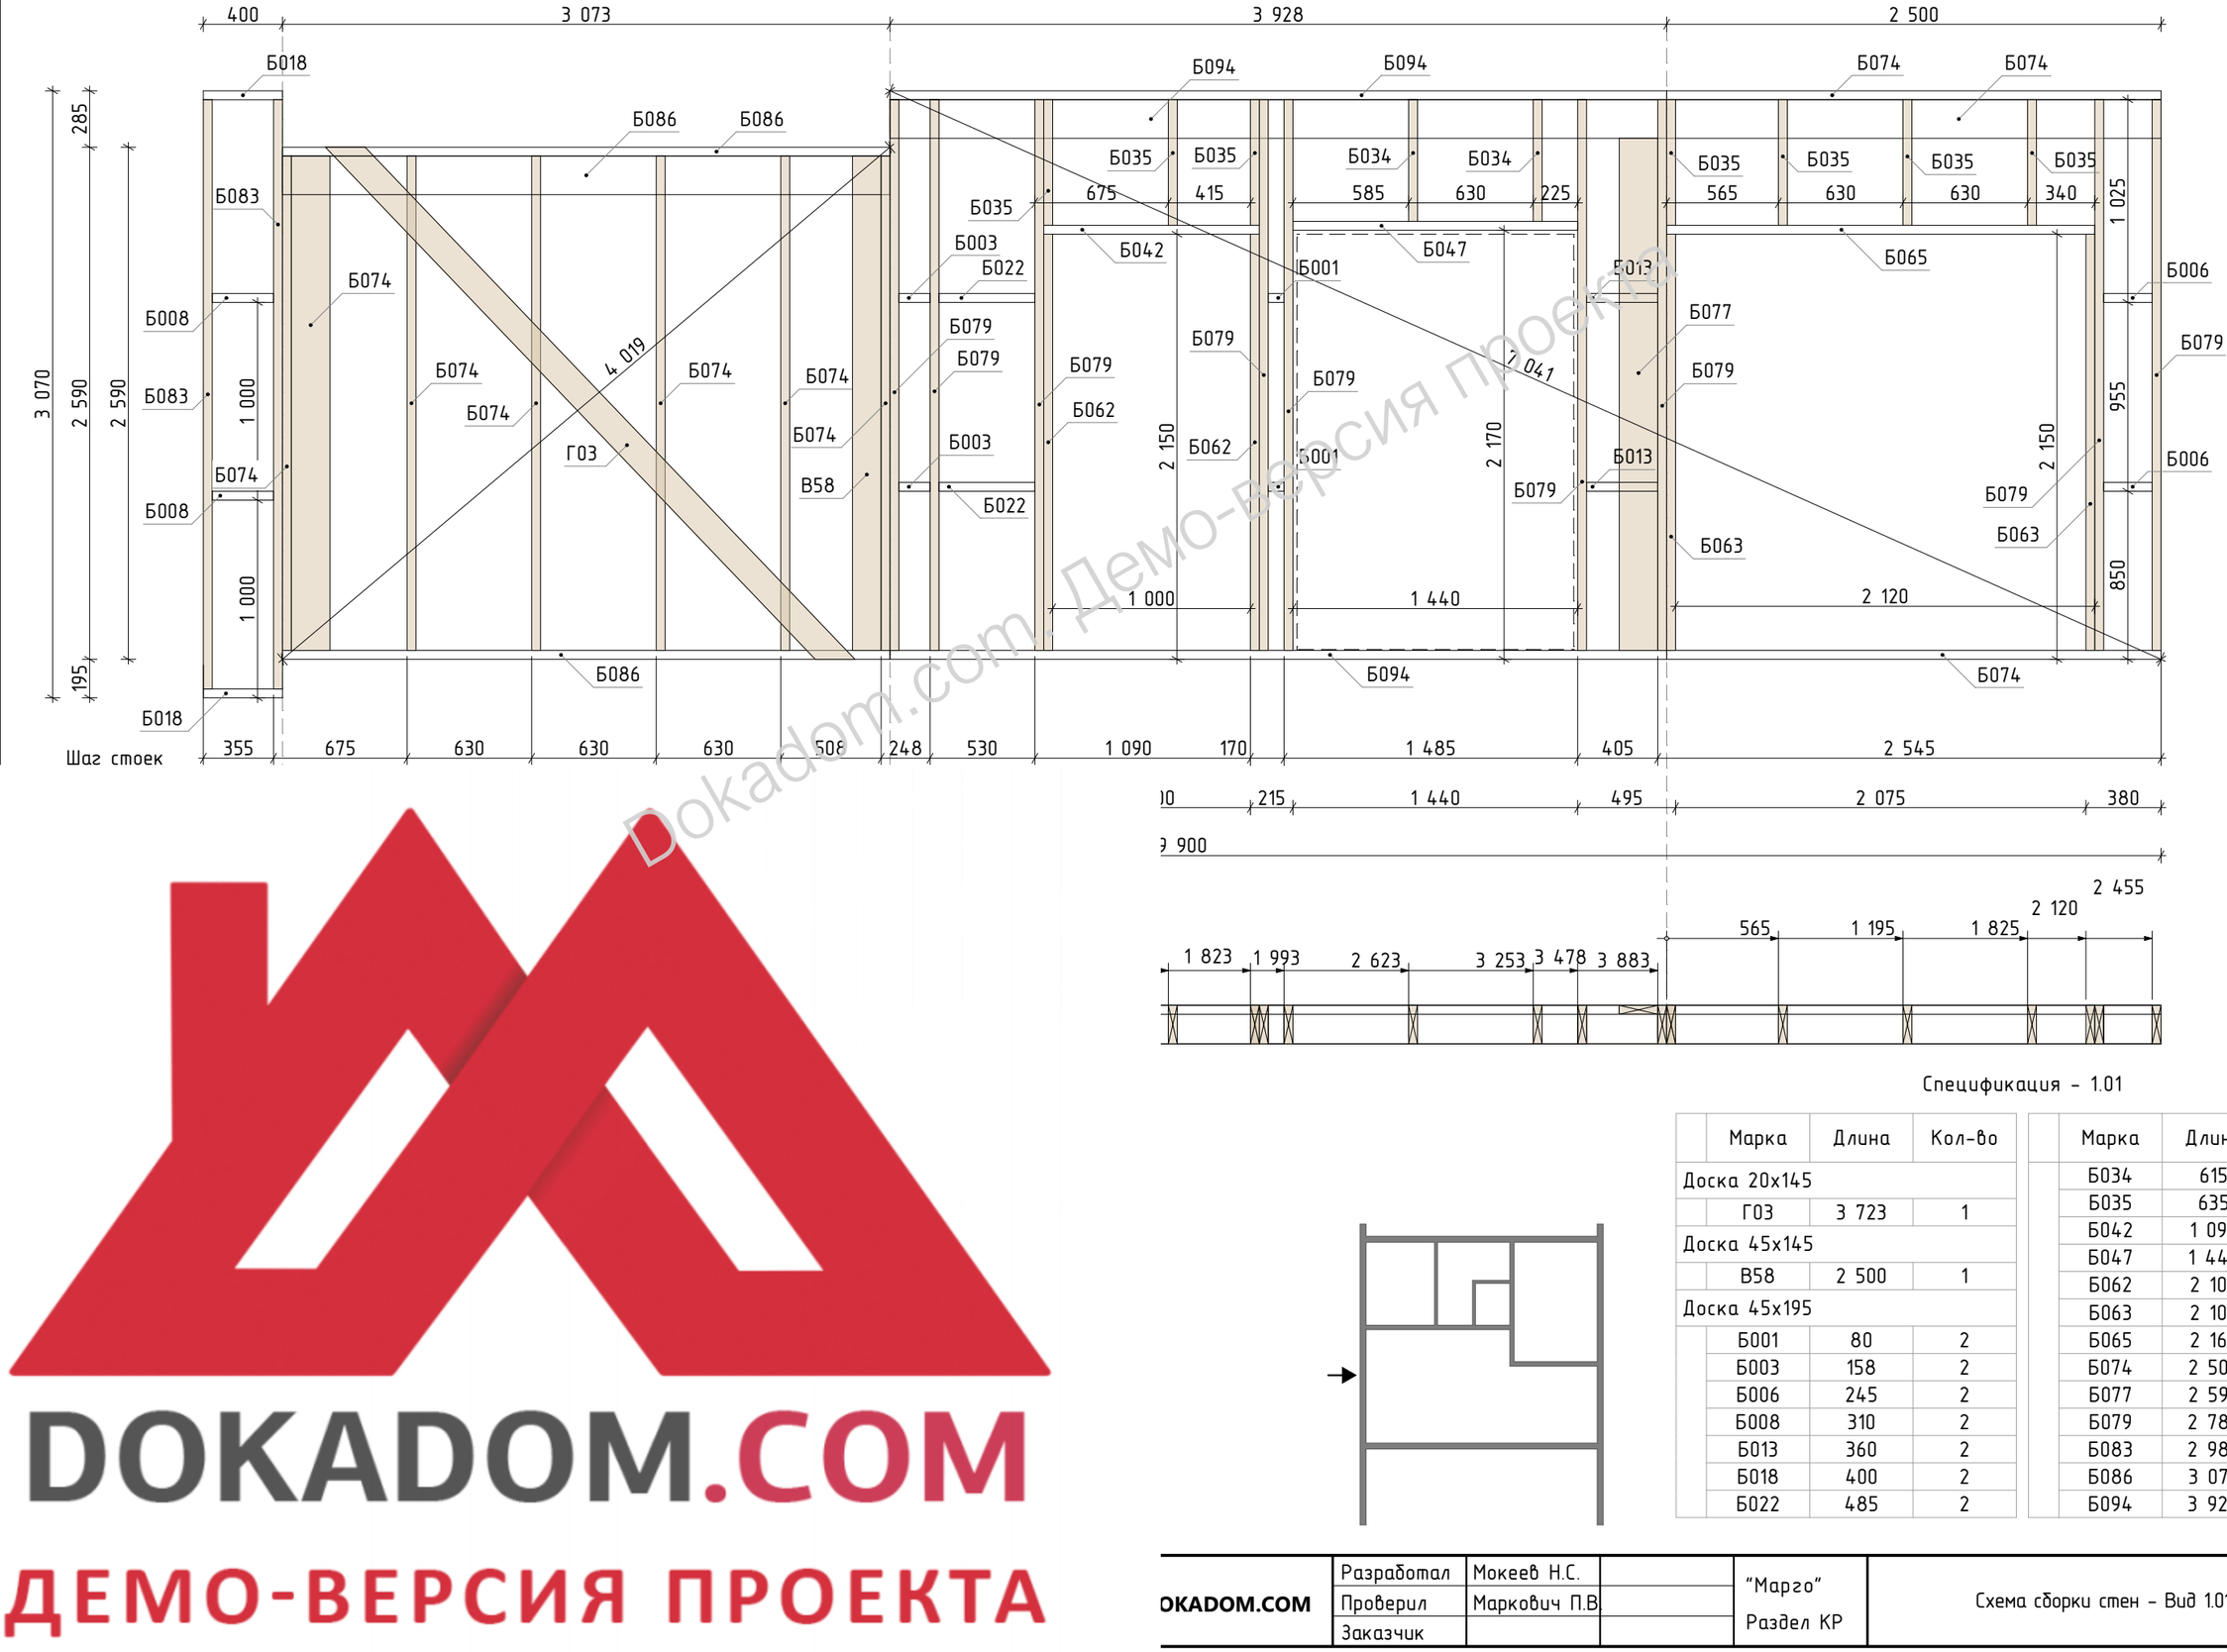

Dokadom.com. Демо-версия проекта


DOKADOM.COM
ДЕМО-ВЕРСИЯ ПРОЕКТА

Спецификация - 1.01


Марка	Длина	Кол-во
Доска 20х145		
ГО3	3 723	1
Доска 45х145		
В58	2 500	1
Доска 45х195		
Б001	80	2
Б003	158	2
Б006	245	2
Б008	310	2
Б013	360	2
Б018	400	2
Б022	485	2

Марка	Длина	Кол-во
Б034	615	2
Б035	635	7
Б042	1 090	1
Б047	1 440	1
Б062	2 105	2
Б063	2 105	2
Б065	2 165	1
Б074	2 500	10
Б077	2 590	1
Б079	2 785	9
Б083	2 980	2
Б086	3 073	3
Б094	3 928	3

DOKADOM.COM	Разработал	Мокеев Н.С.		"Марго" Раздел КР	Схема сборки стен - Вид 1.01	Лист 15
	Проверил	Маркович П.В.				
	Заказчик					

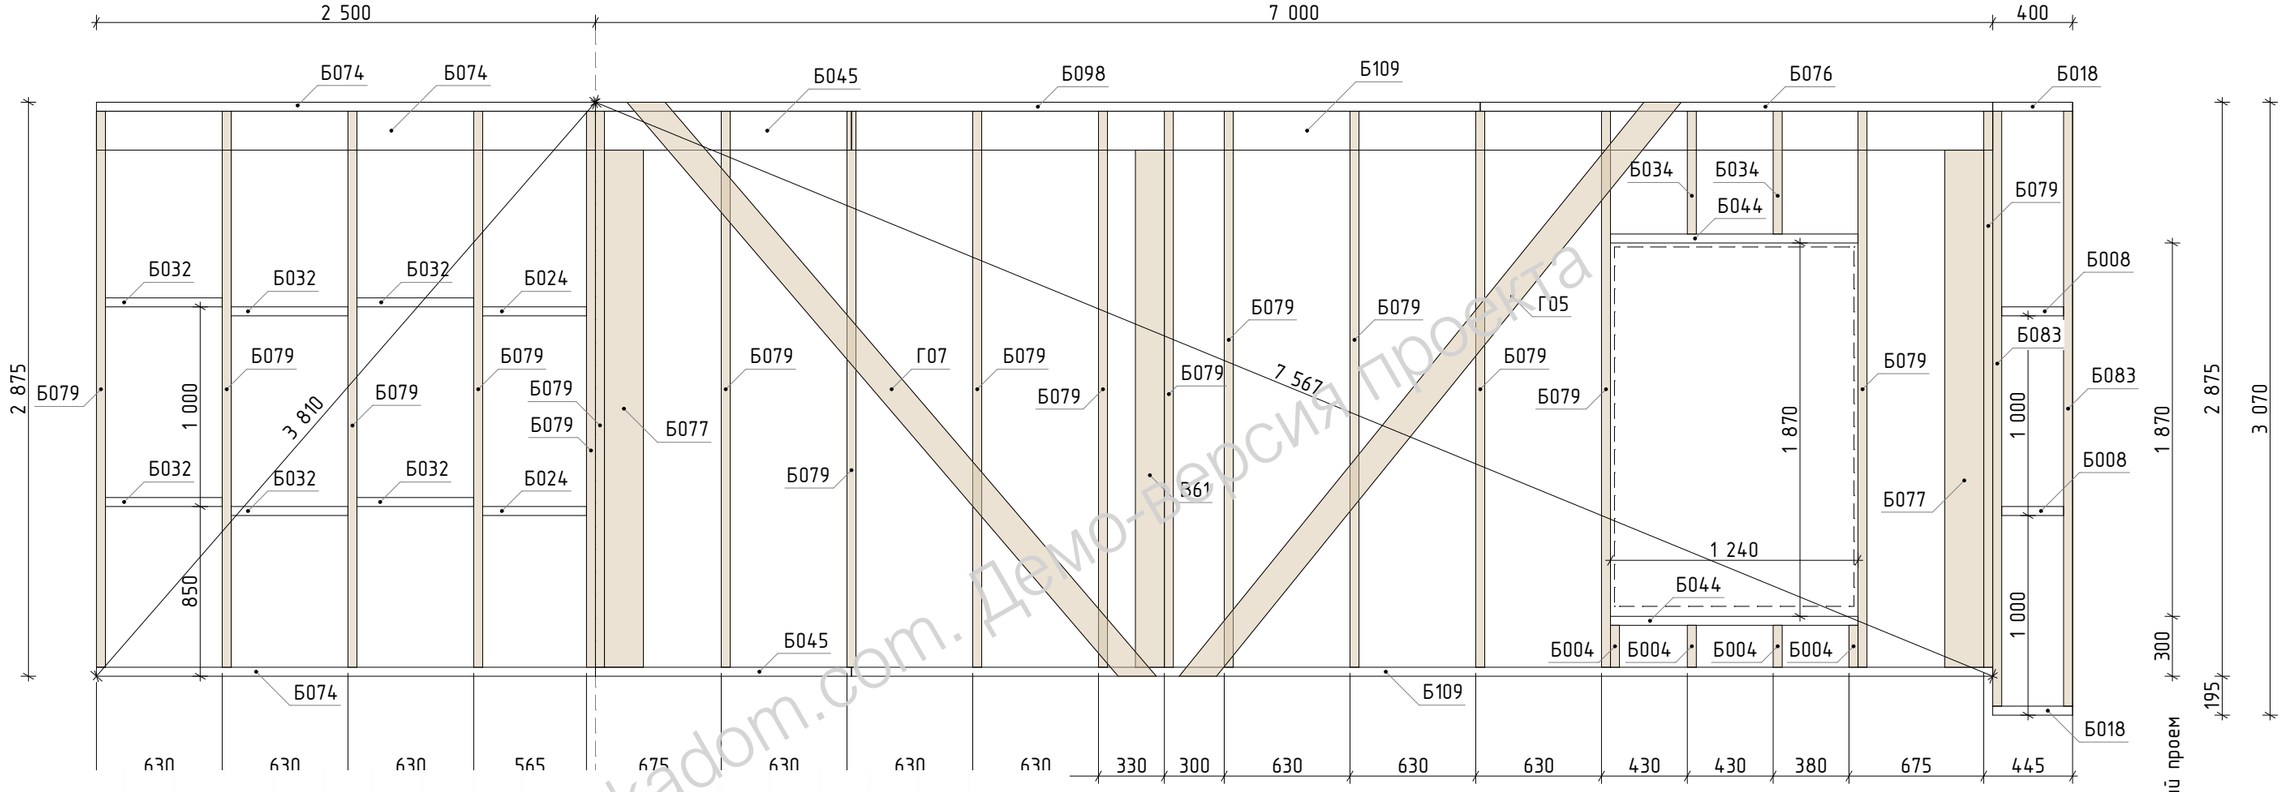

DOKADOM.COM
ДЕМО-ВЕРСИЯ ПРОЕКТА
Dokadom.com. Демо-версия проекта

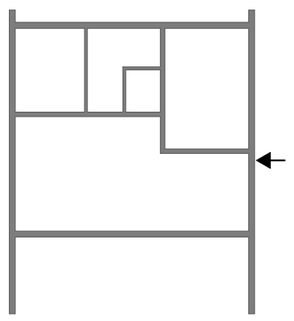



Спецификация - 1.02


Марка	Длина	Кол-во
Доска 20х145		
Г05	3 817	1
Г07	3 909	1
Доска 45х145		
В61	2 590	1
Доска 45х195		
Б004	210	4
Б008	310	2
Б018	400	2
Б024	520	2


Марка	Длина	Кол-во
Б032	585	6
Б034	615	2
Б044	1 240	2
Б045	1 283	2
Б074	2 500	3
Б076	2 568	1
Б077	2 590	2
Б079	2 785	17
Б083	2 980	2
Б098	4 433	1
Б109	5 718	2

DOKADOM.COM	Разработал	Мокеев Н.С.		"Марго" Раздел КР	Схема сборки стен - Вид 1.02	Лист 16
	Проверил	Маркович П.В.				
	Заказчик					

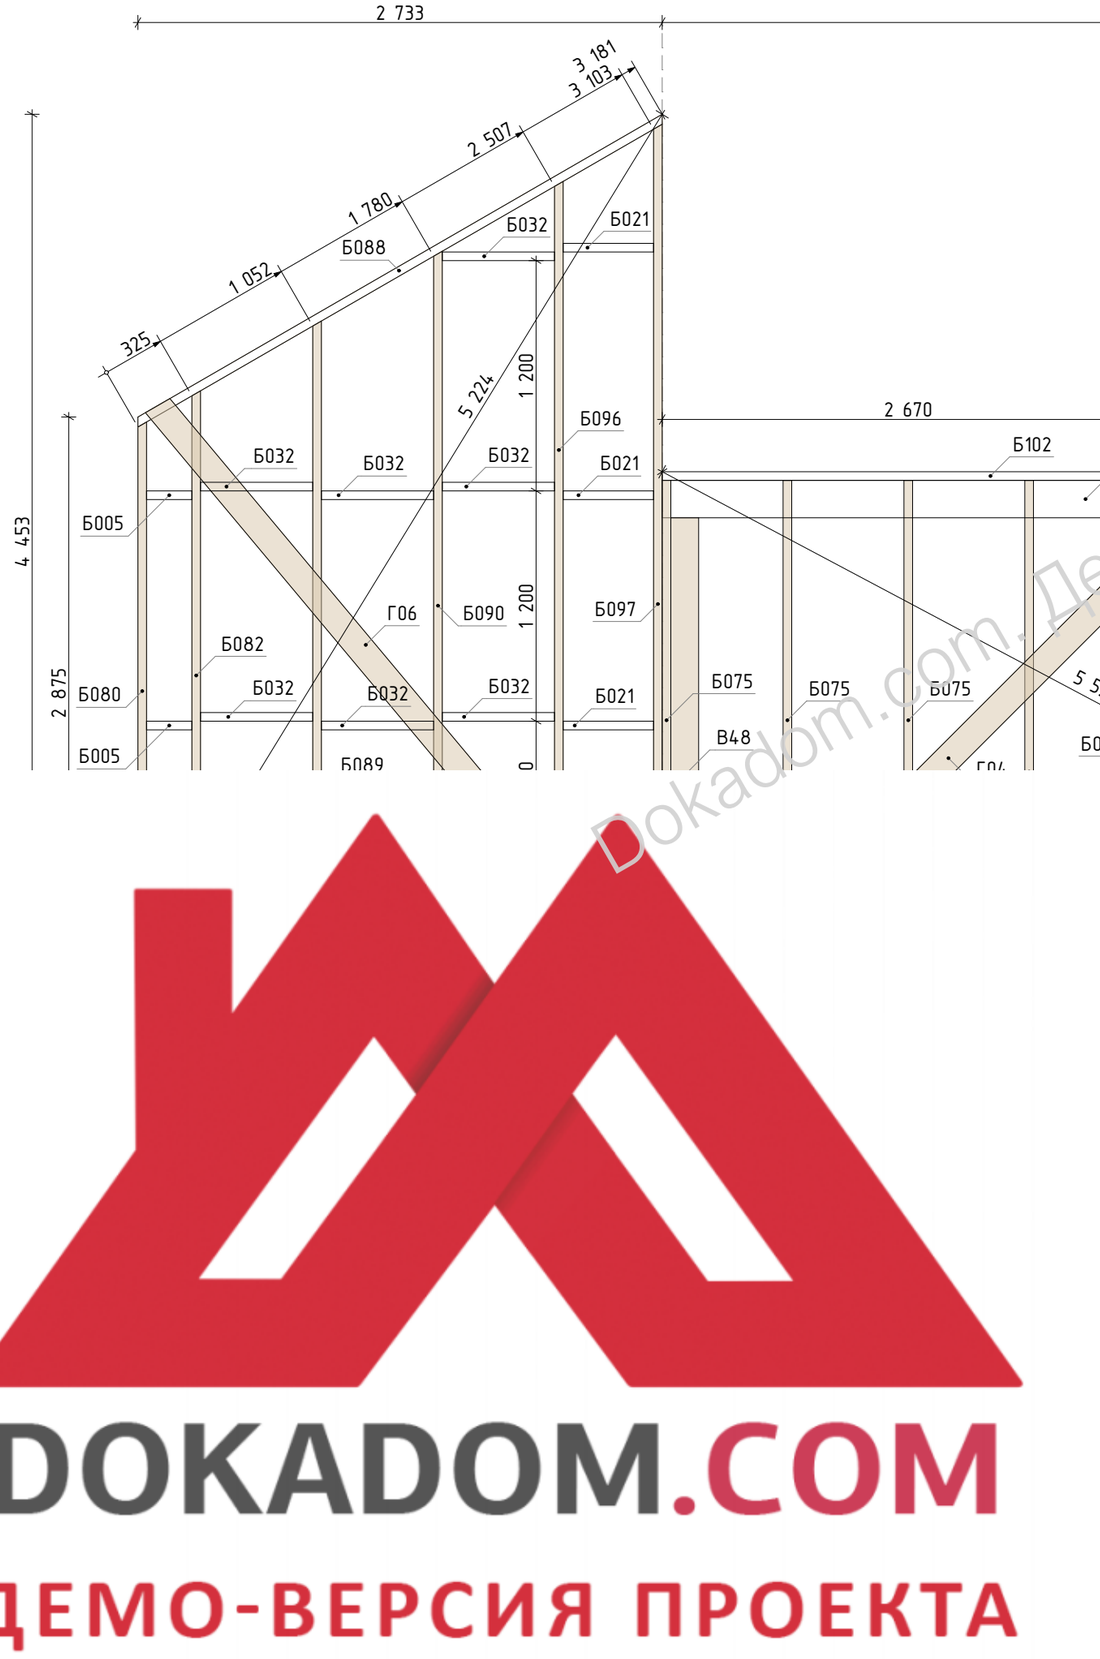

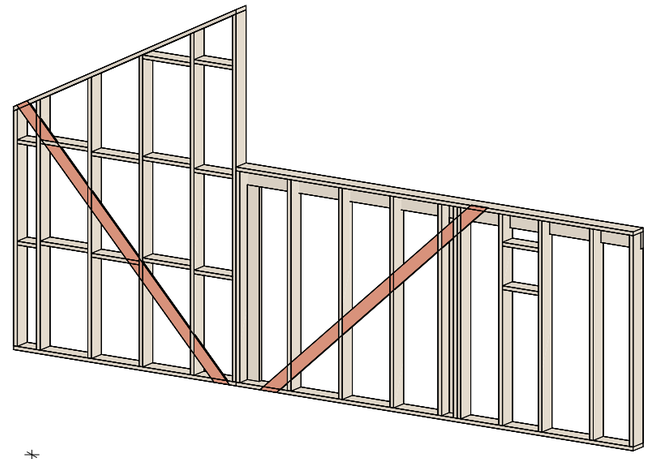

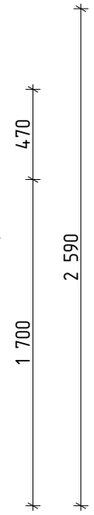

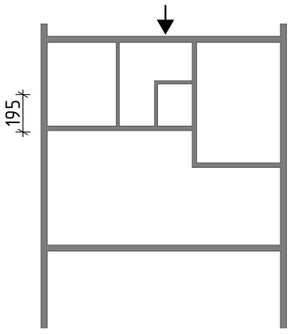


Спецификация - 1.03

	Марка	Длина	Кол-во
Доска 20х145			
	Г04	3 808	1
	Г06	3 899	1
Доска 45х145			
	В48	2 305	2
Доска 45х195			
	Б005	236	2
	Б020	440	2
	Б021	471	3
	Б032	585	7
	Б075	2 500	11
	Б078	2 733	1
	Б080	2 804	1
	Б082	2 966	1
	Б088	3 181	1
	Б089	3 330	1
	Б090	3 694	1
	Б096	4 058	1
	Б097	4 356	1
	Б102	4 877	3

DOKADOM.COM	Разработал	Мокеев Н.С.		"Марго"	Схема сборки стен - Вид 1.03	Лист
	Проверил	Маркович П.В.		Раздел КР		17
	Заказчик					

Dokadom.com. Демо-версия проекта
DOKADOM.COM
ДЕМО-ВЕРСИЯ ПРОЕКТА

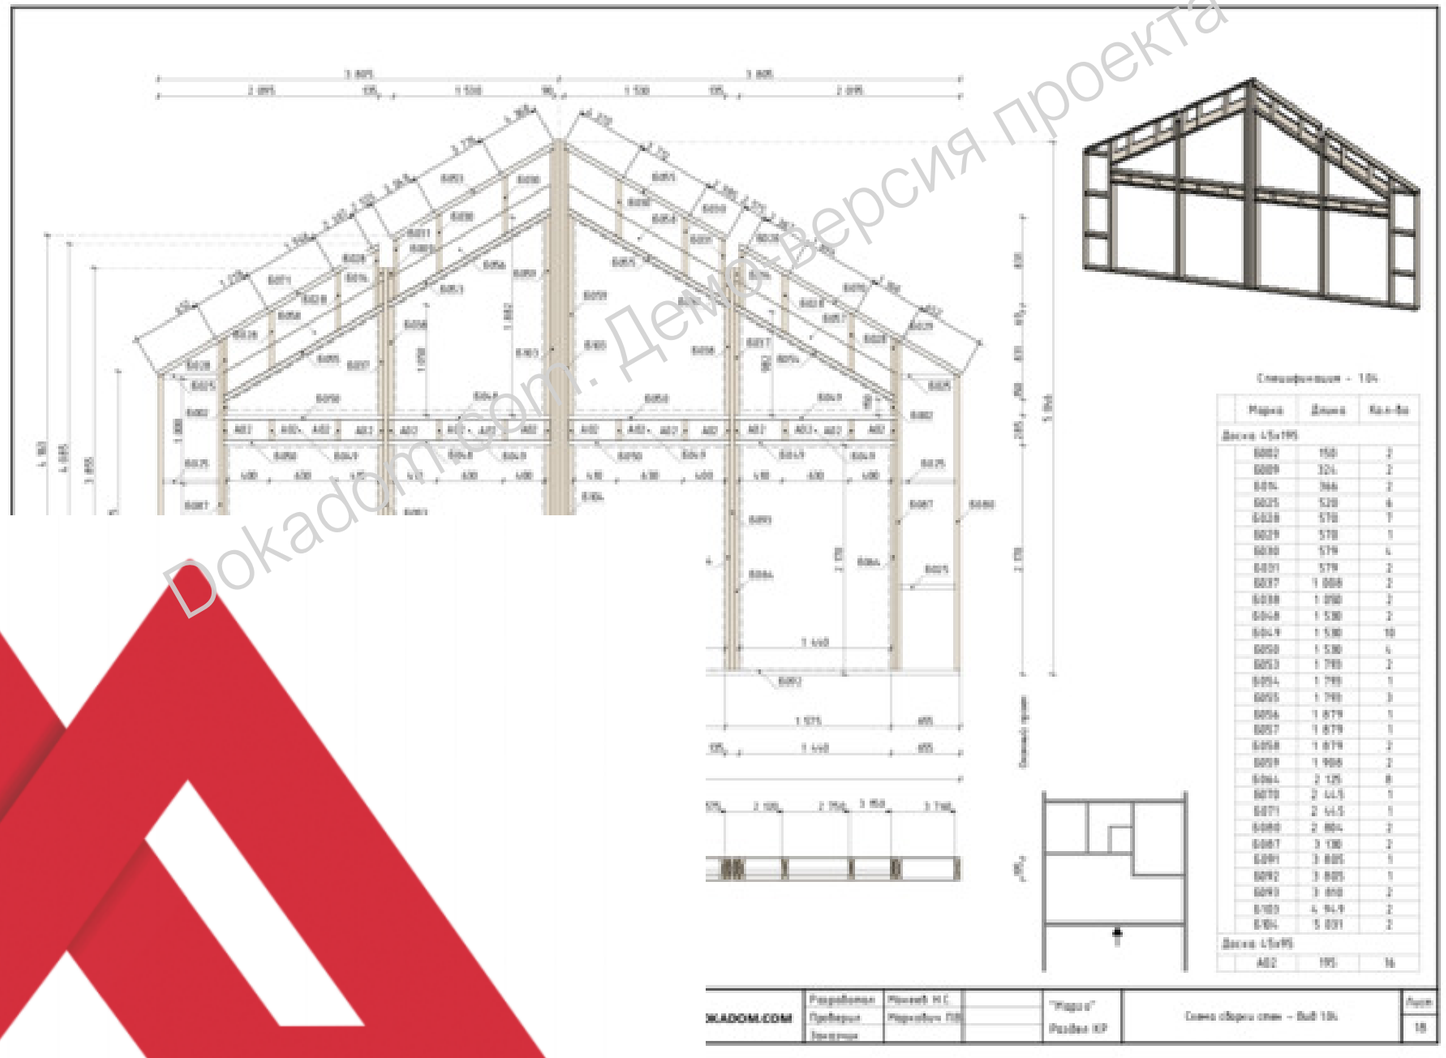


Спецификация - 1Ск

Марка	Длина	Кол-во
Доска 45х199		
6002	150	2
6009	324	2
6014	366	2
6025	520	4
6028	570	7
6029	570	1
6030	579	4
6031	579	2
6037	1 008	2
6038	1 050	2
6048	1 530	2
6049	1 530	10
6050	1 530	4
6053	1 790	2
6054	1 790	1
6055	1 790	3
6056	1 879	1
6057	1 879	1
6058	1 879	2
6059	1 906	2
6064	2 125	8
6070	2 415	1
6071	2 415	1
6080	2 864	2
6087	3 130	2
6091	3 805	1
6092	3 805	1
6093	3 850	2
6103	4 949	2
6104	5 031	2
Доска 45х95		
A02	195	14


DOKADOM.COM	Разработал	Жилкин Н.С.		"Мария"	Схема сборки стен – Вид 1Ск	Лист 18
	Проверил	Жилкин П.В.		Разбил КР		
	Эрекция					

Dokadom.com. Демо-версия проекта


DOKADOM.COM
ДЕМО-ВЕРСИЯ ПРОЕКТА

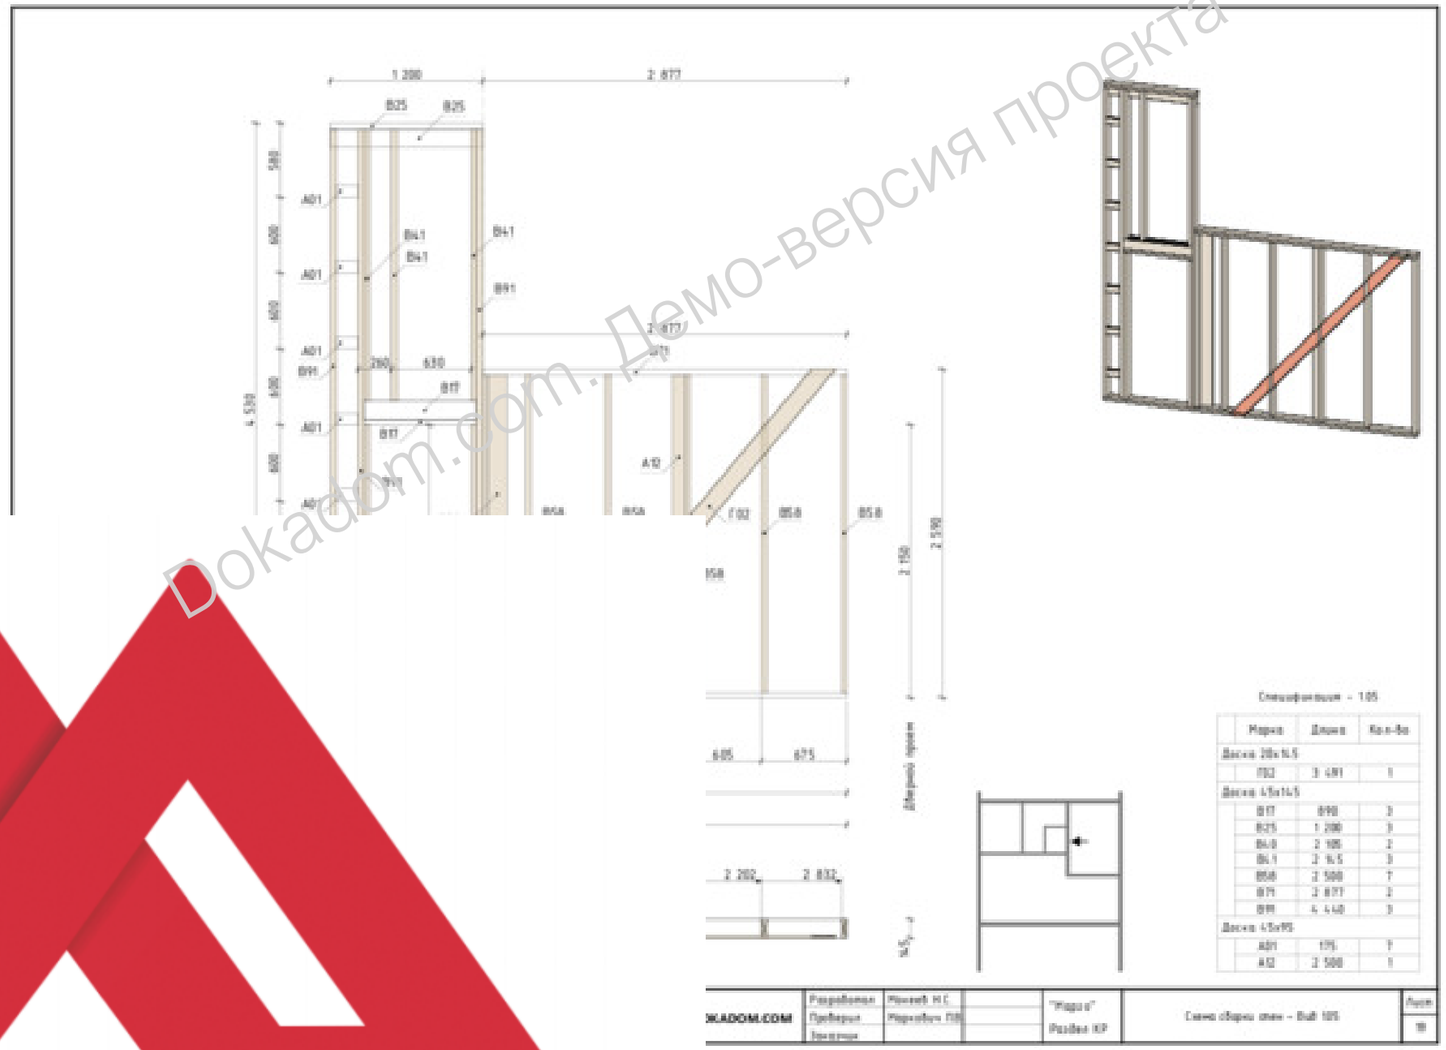

Dokadom.com. Демо-версия проекта
DOKADOM.COM
ДЕМО-ВЕРСИЯ ПРОЕКТА

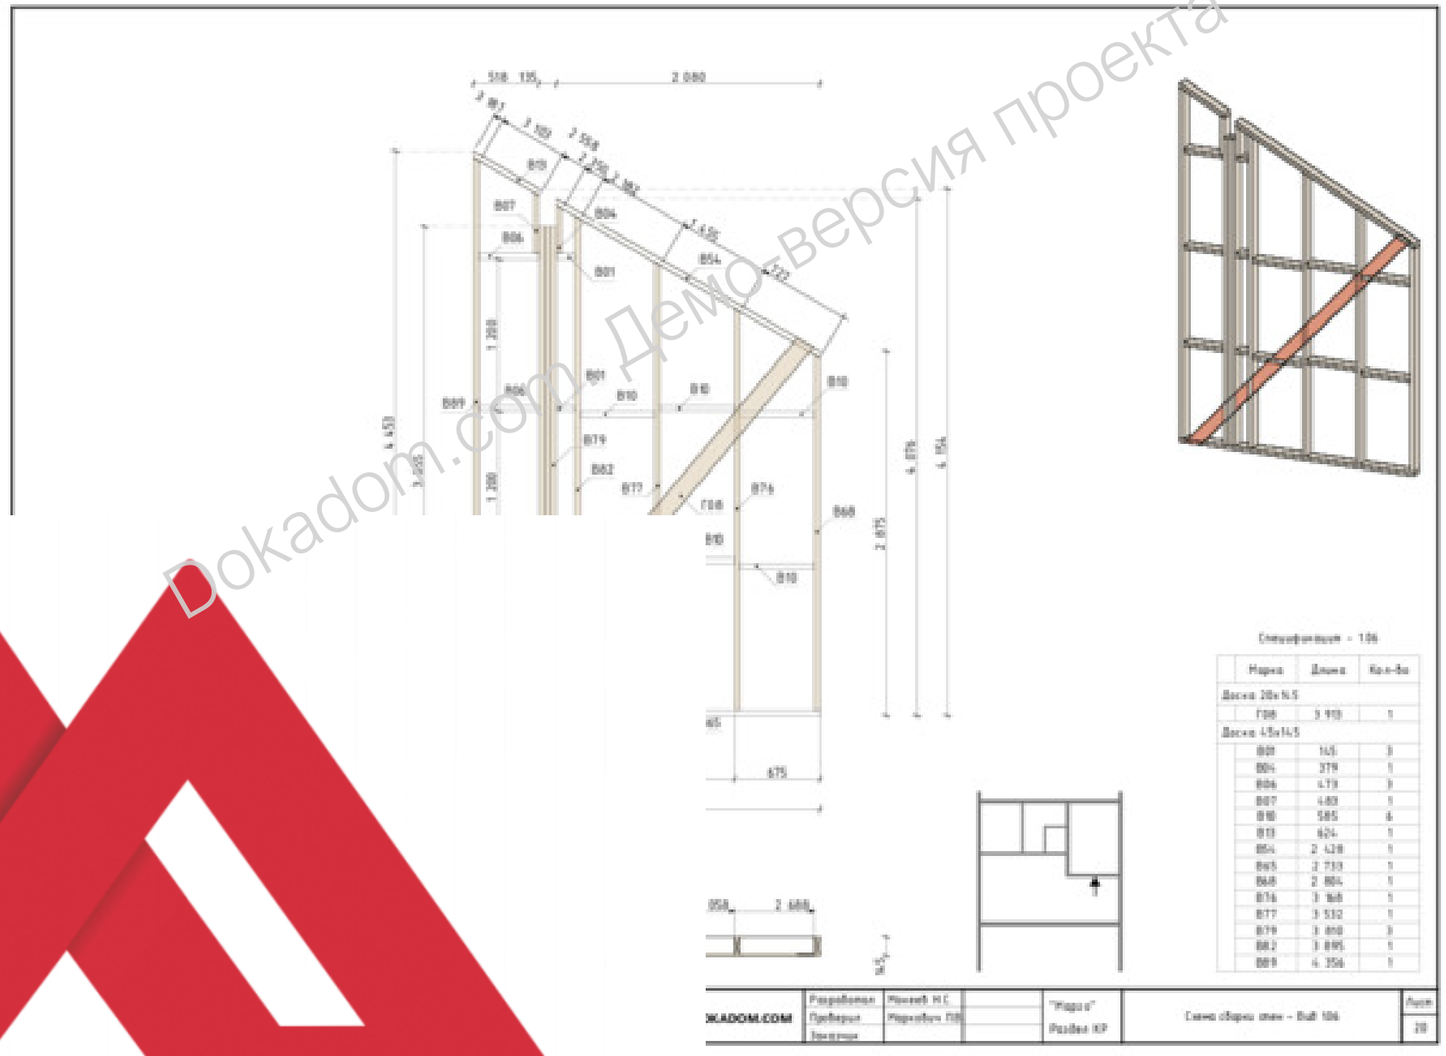


Dokadom.com - Демо-версия проекта
DOKADOM.COM
ДЕМО-ВЕРСИЯ ПРОЕКТА

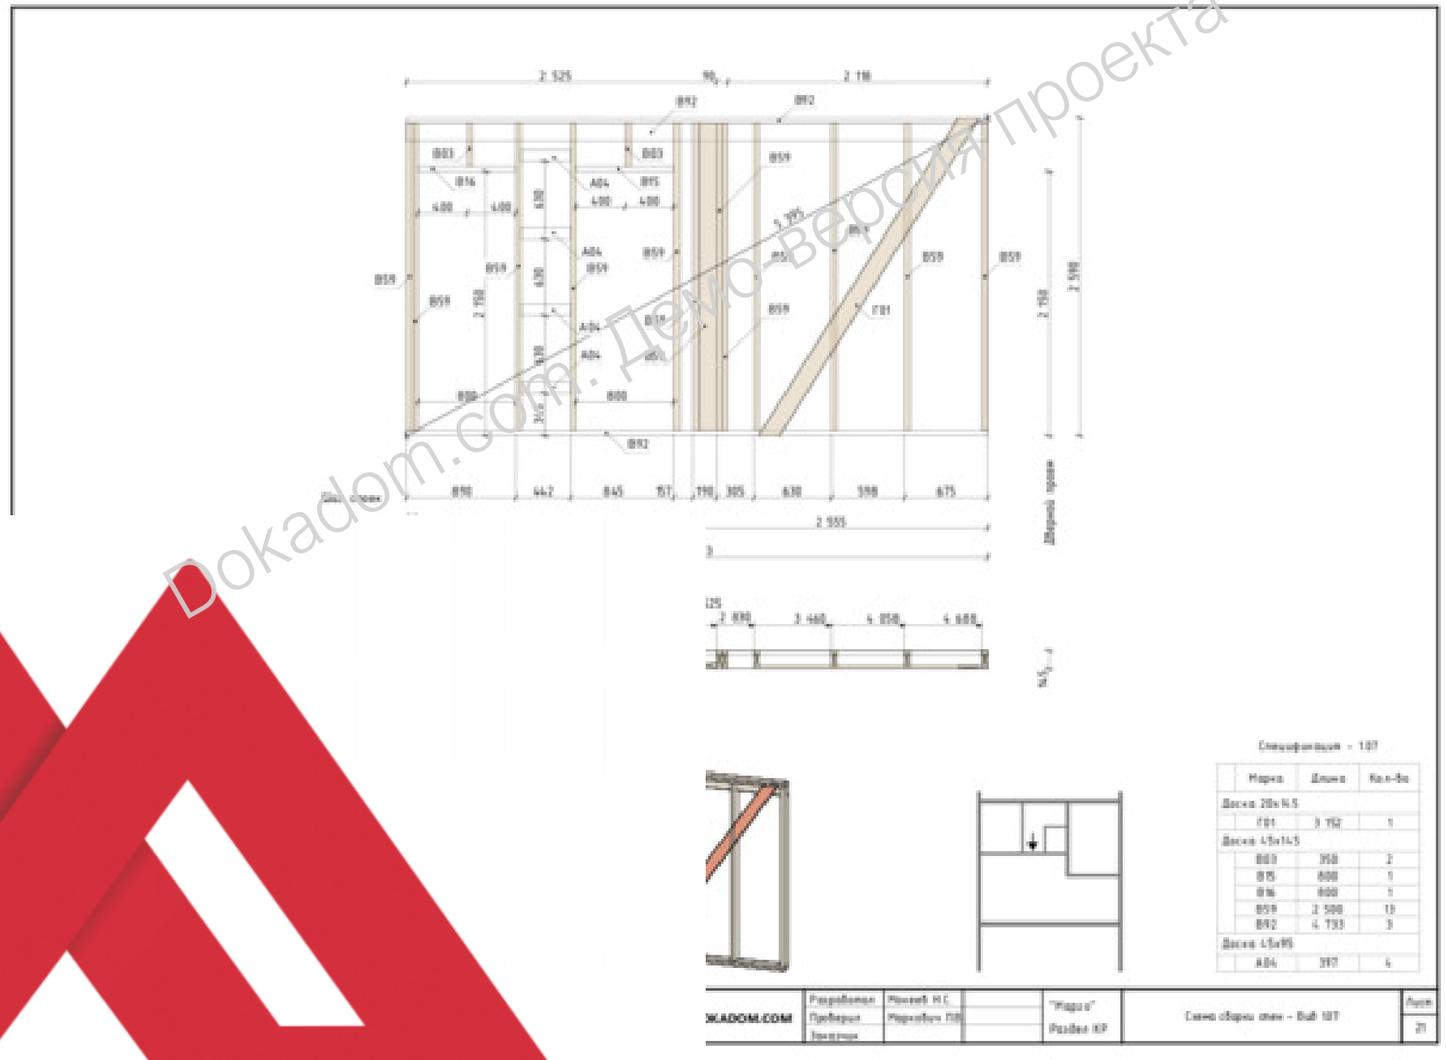


Dokadom.com. Демо-версия проекта


DOKADOM.COM
ДЕМО-ВЕРСИЯ ПРОЕКТА

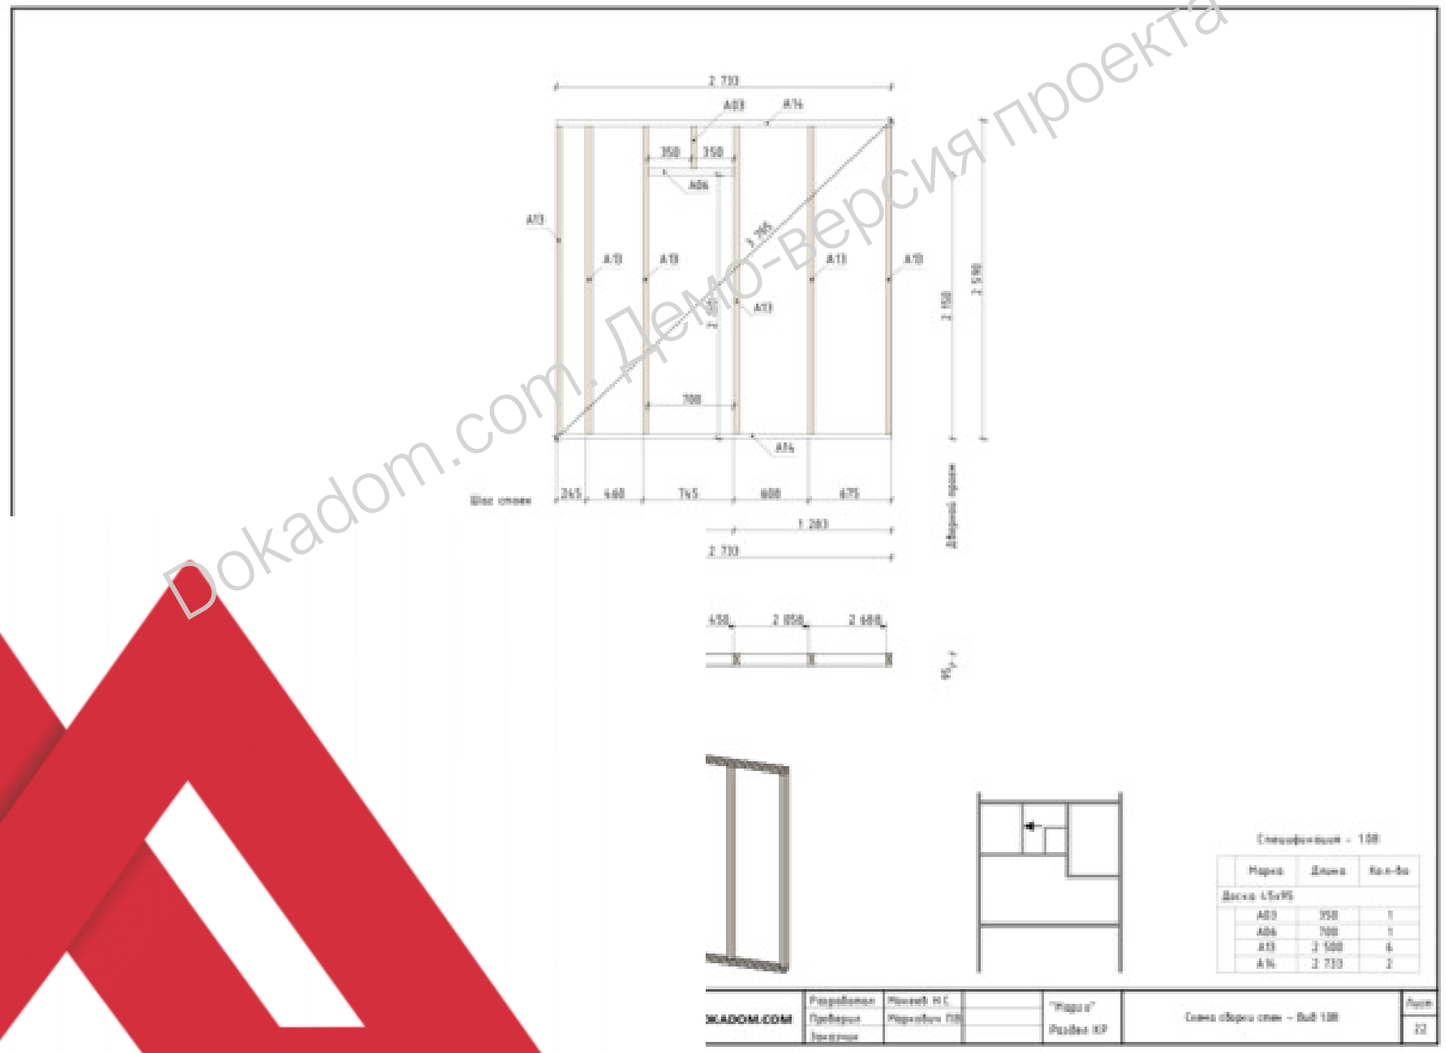

Dokadom.com. Демо-версия проекта
DOKADOM.COM
ДЕМО-ВЕРСИЯ ПРОЕКТА

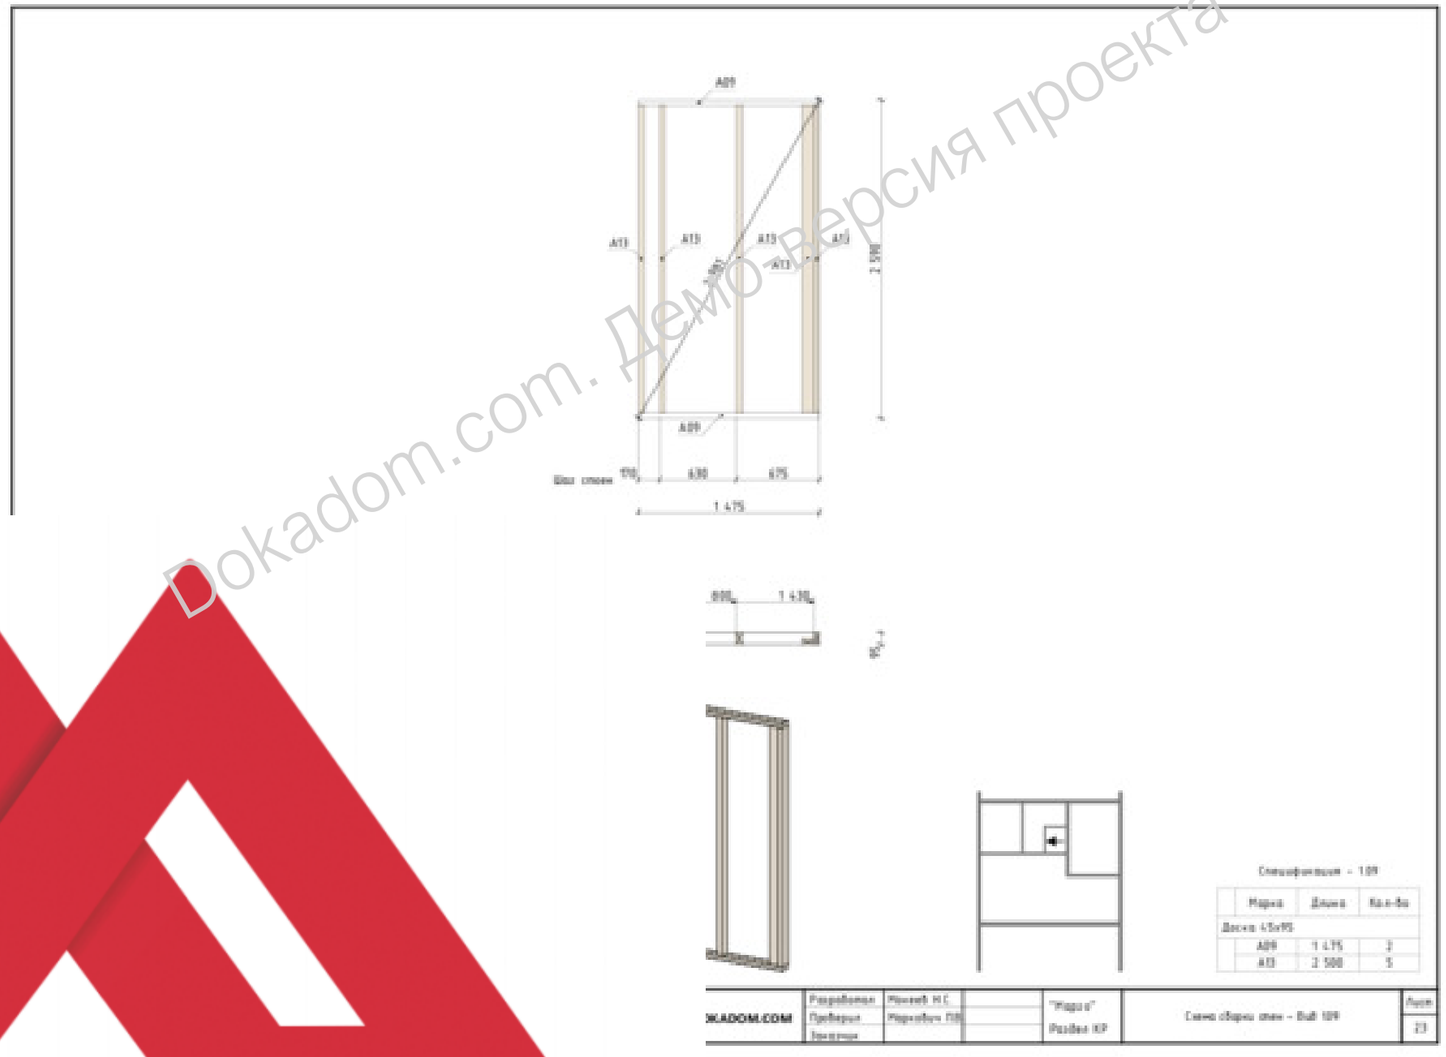

Dokadom.com. Демо-версия проекта
DOKADOM.COM
ДЕМО-ВЕРСИЯ ПРОЕКТА

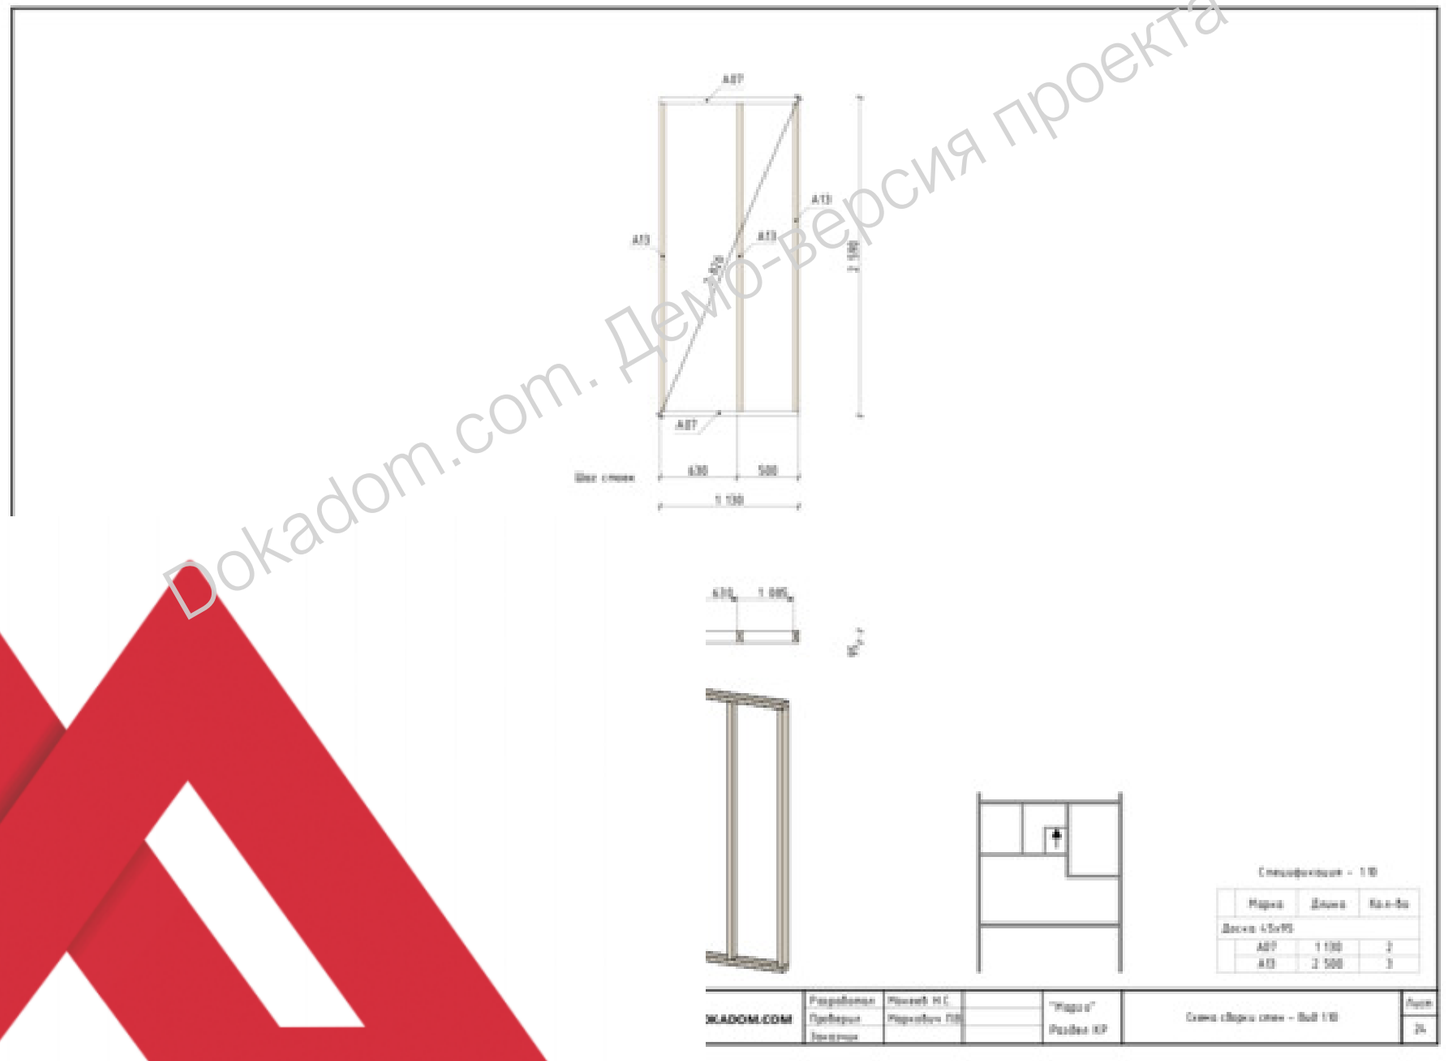


Dokadom.com. Демо-версия проекта

DOKADOM.COM
ДЕМО-ВЕРСИЯ ПРОЕКТА

С1.01

Соединения элементов каркасной стены с проемами

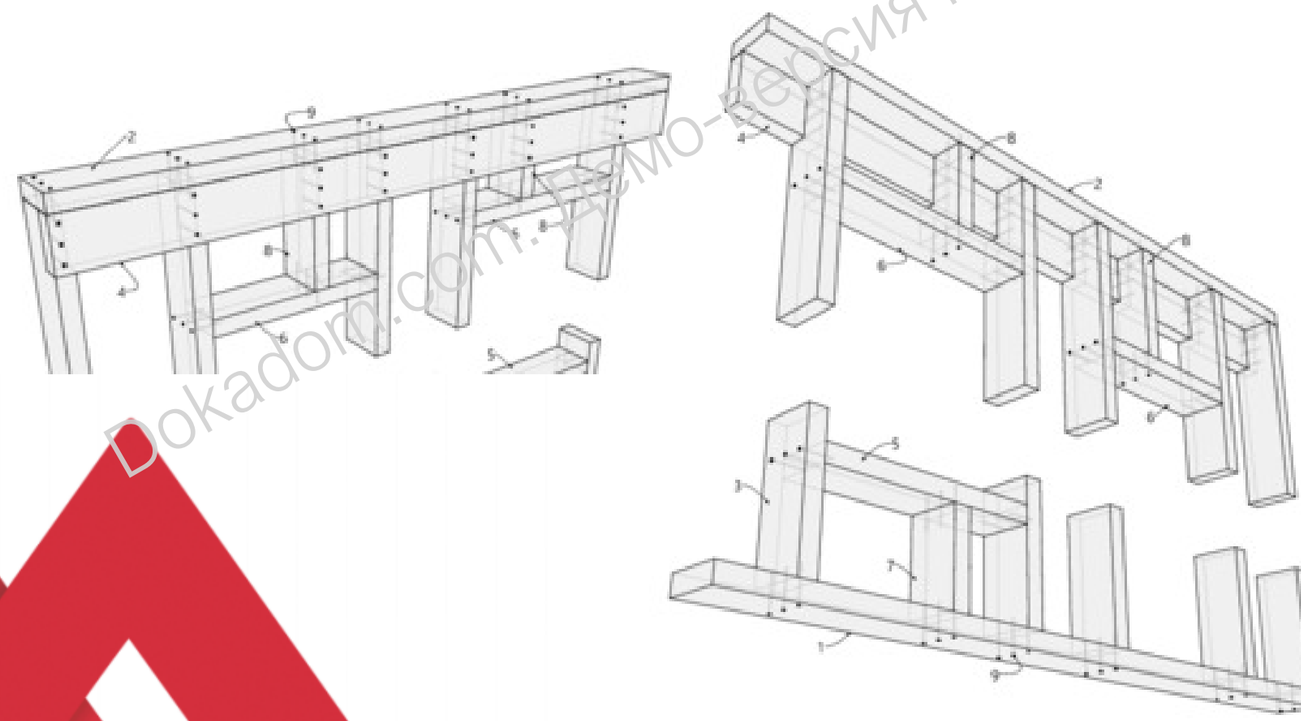


общий ригель каркасной стены; 5-нижняя перемычка проема; 6-верхняя перемычка проема; 7-нижняя стойка; 8-стойка; 9-косяк.

DOKADOM.COM	Разработал	Иванов И.С.		"Ридго"	Узлы стен 1	Лист 23
	Проверил	Иванович П.В.		Razdel IOP		
	Заказчик					

Dokadom.com. Демо-версия проекта


DOKADOM.COM
ДЕМО-ВЕРСИЯ ПРОЕКТА

С2.02 **Соединения элементов каркасной стены**

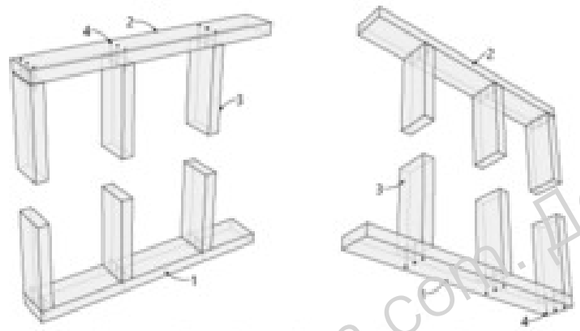


1-нижняя обвязка каркасной стены; 2-верхняя обвязка каркасной стены; 3-стойка каркасной стены; 4-гвозди.

С2.05 **Соединения узлов стен каркасной стены**

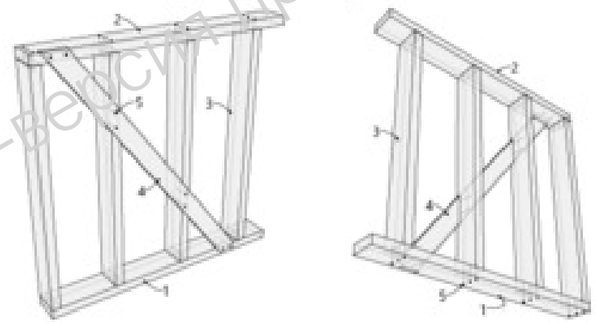

1-нижняя обвязка каркасной стены; 2-верхняя обвязка каркасной стены; 3-стойка каркасной стены; 4-раскосина; 5-подоконная доска.

С2.12 **Крепление каркасной стены снизу**

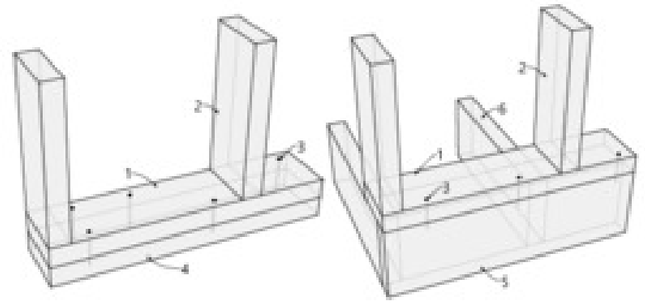

1-нижняя обвязка каркасной стены; 2-стойка каркасной стены; 3-гвозди; 4-опорная доска/ригель верхней обвязки; 5-обвязочная балка перекрытия; 6-балка перекрытия.

DOKADOM.COM	Разработал	Иванов И.С.		"Жара и"	Узлы стен 2	Лист 28
	Проверил	Иванов П.В.		Разбил КР		
	Эксперт					

Dokadom.com. Демо-версия проекта


DOKADOM.COM
ДЕМО-ВЕРСИЯ ПРОЕКТА

С1.07 Угловое соединение каркасных стен.




1-нижняя обвязка каркасной стены; 2-верхняя обвязка каркасной стены; 3-стойка каркасной стены;
4-общий ригель каркасной стены; 5-распор; 6-стойка для крепления отделки.

С1.09 Соединения каркасных стены. L-образное примыкание

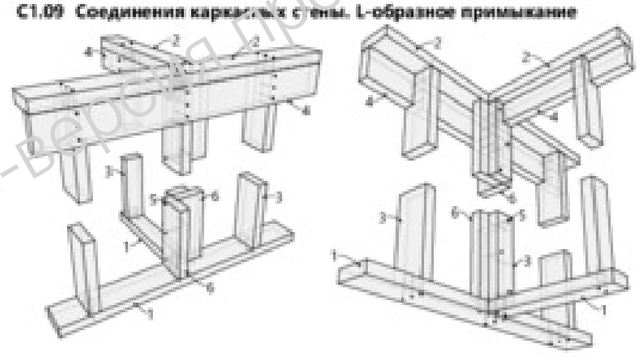

1-нижняя обвязка каркасной стены; 2-верхняя обвязка каркасной стены; 3-стойка каркасной стены;
4-общий ригель каркасной стены; 5-распор; 6-стойка для крепления отделки.

С1.15 Соединения каркасных стены. Перемычки

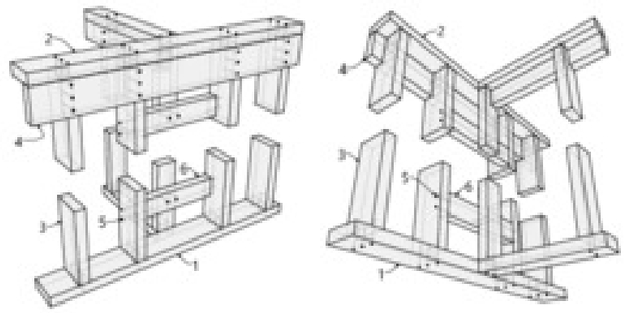


1-нижняя обвязка каркасной стены; 2-верхняя обвязка каркасной стены; 3-стойка каркасной стены;
4-общий ригель каркасной стены; 5-распор; 6-перемычка для соединения стен.

DOKADOM.COM	Разработал	Яковлев Н.С.		"Индустрия"	Узлы стен 3	Лист 27
	Проверил	Мирошкин П.В.		Раздел КР		
	Эскизный					


Dokadom.com. Демо-версия проекта

DOKADOM.COM
ДЕМО-ВЕРСИЯ ПРОЕКТА

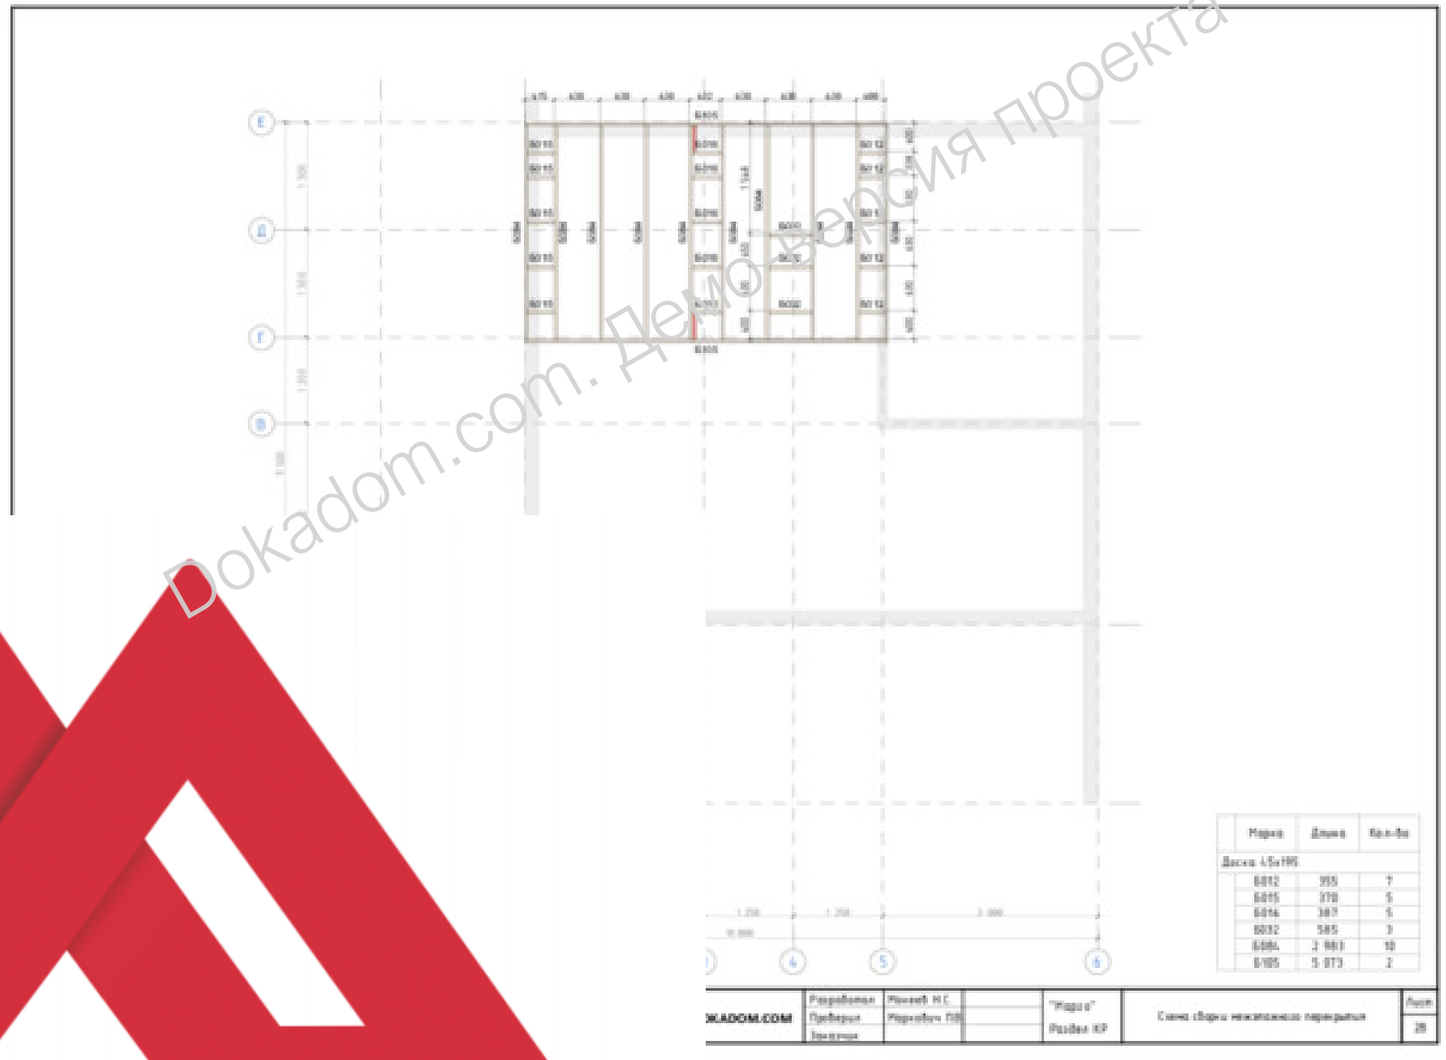


Марка	Длина	Кол-во
Доска 45х195		
6012	955	7
6015	370	5
6016	387	5
6032	585	3
6084	2 980	10
6105	5 073	2

Dokadom.com. Демо-версия проекта
DOKADOM.COM
ДЕМО-ВЕРСИЯ ПРОЕКТА

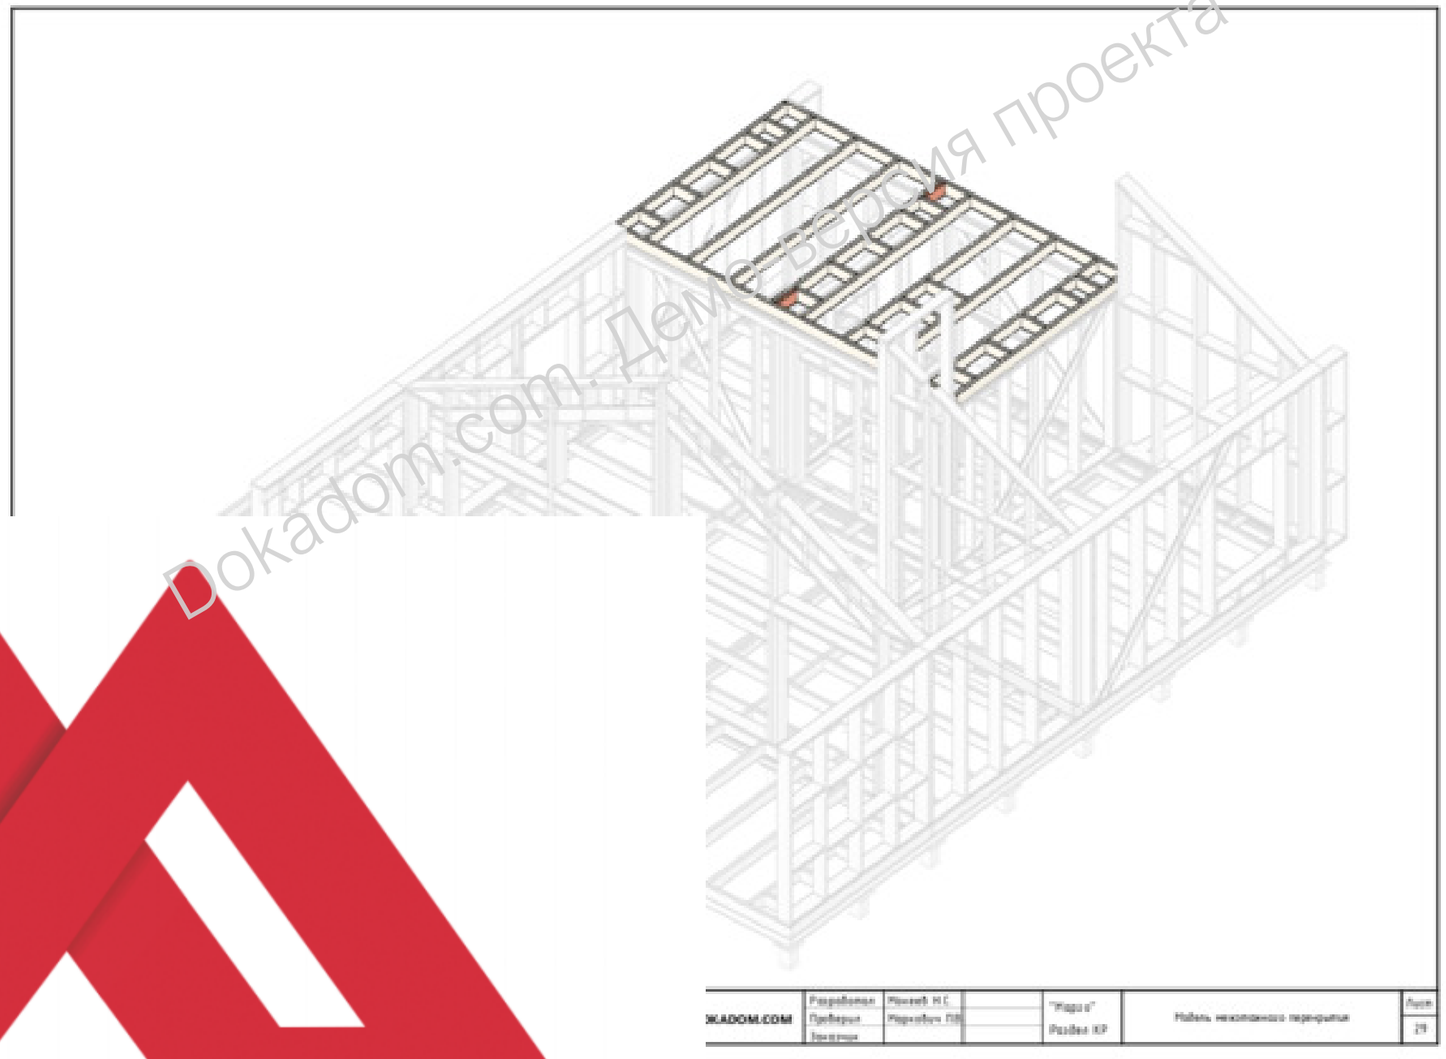


DOKADOM.COM
ДЕМО-ВЕРСИЯ ПРОЕКТА
Dokadom.com. Демо-версия проекта

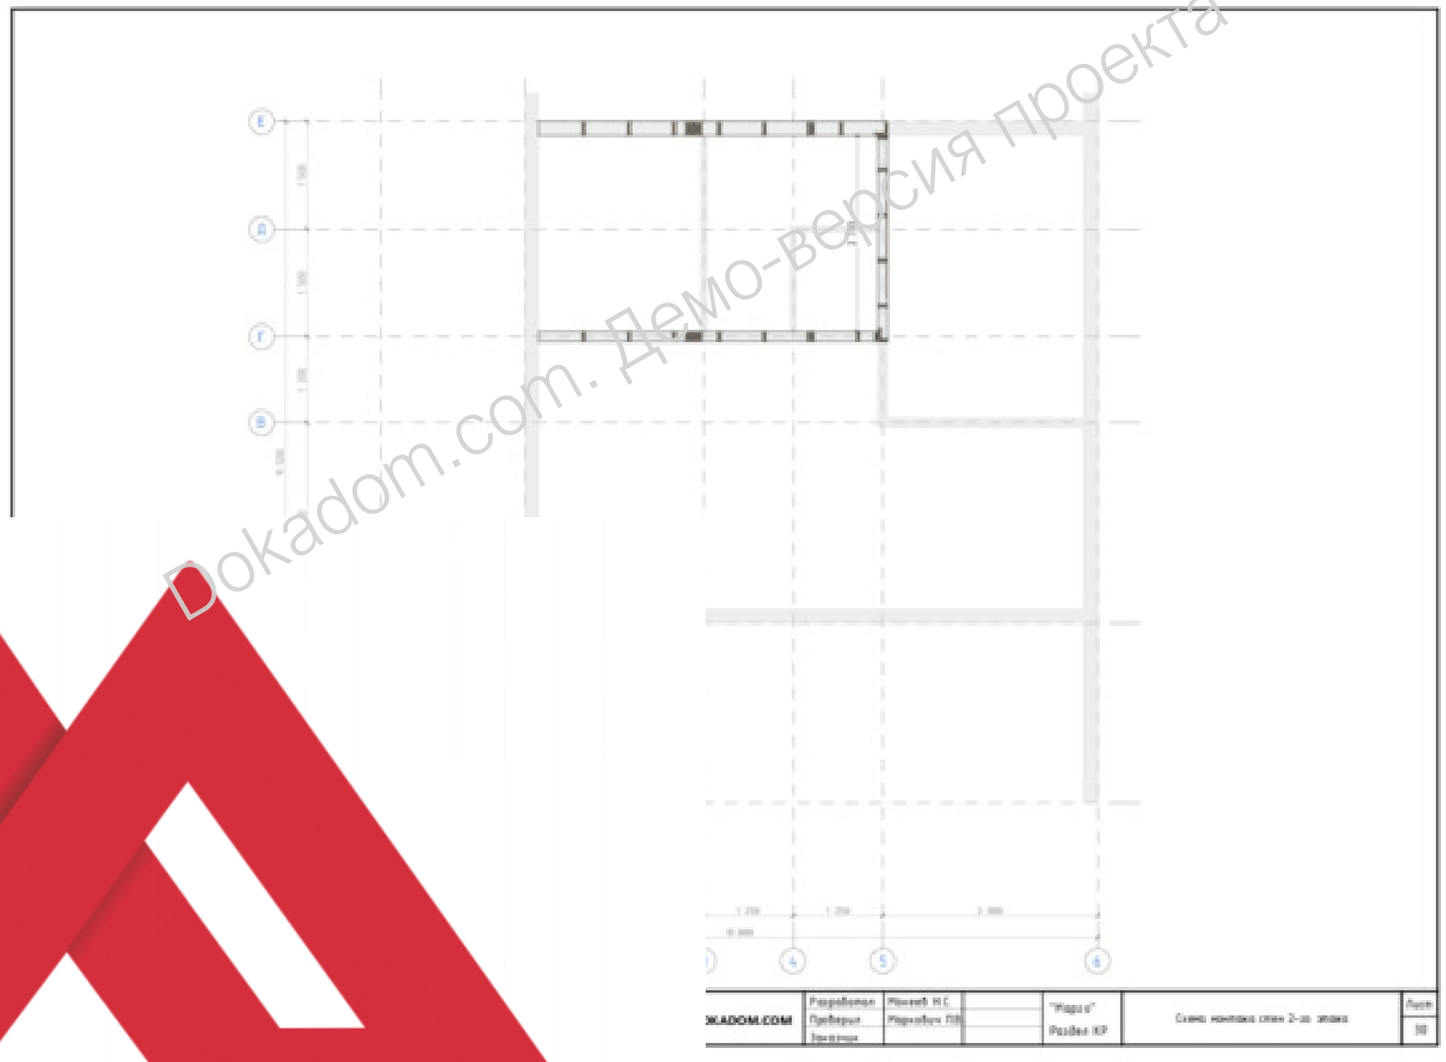


Dokadom.com. Демо-версия проекта

DOKADOM.COM


ДЕМО-ВЕРСИЯ ПРОЕКТА

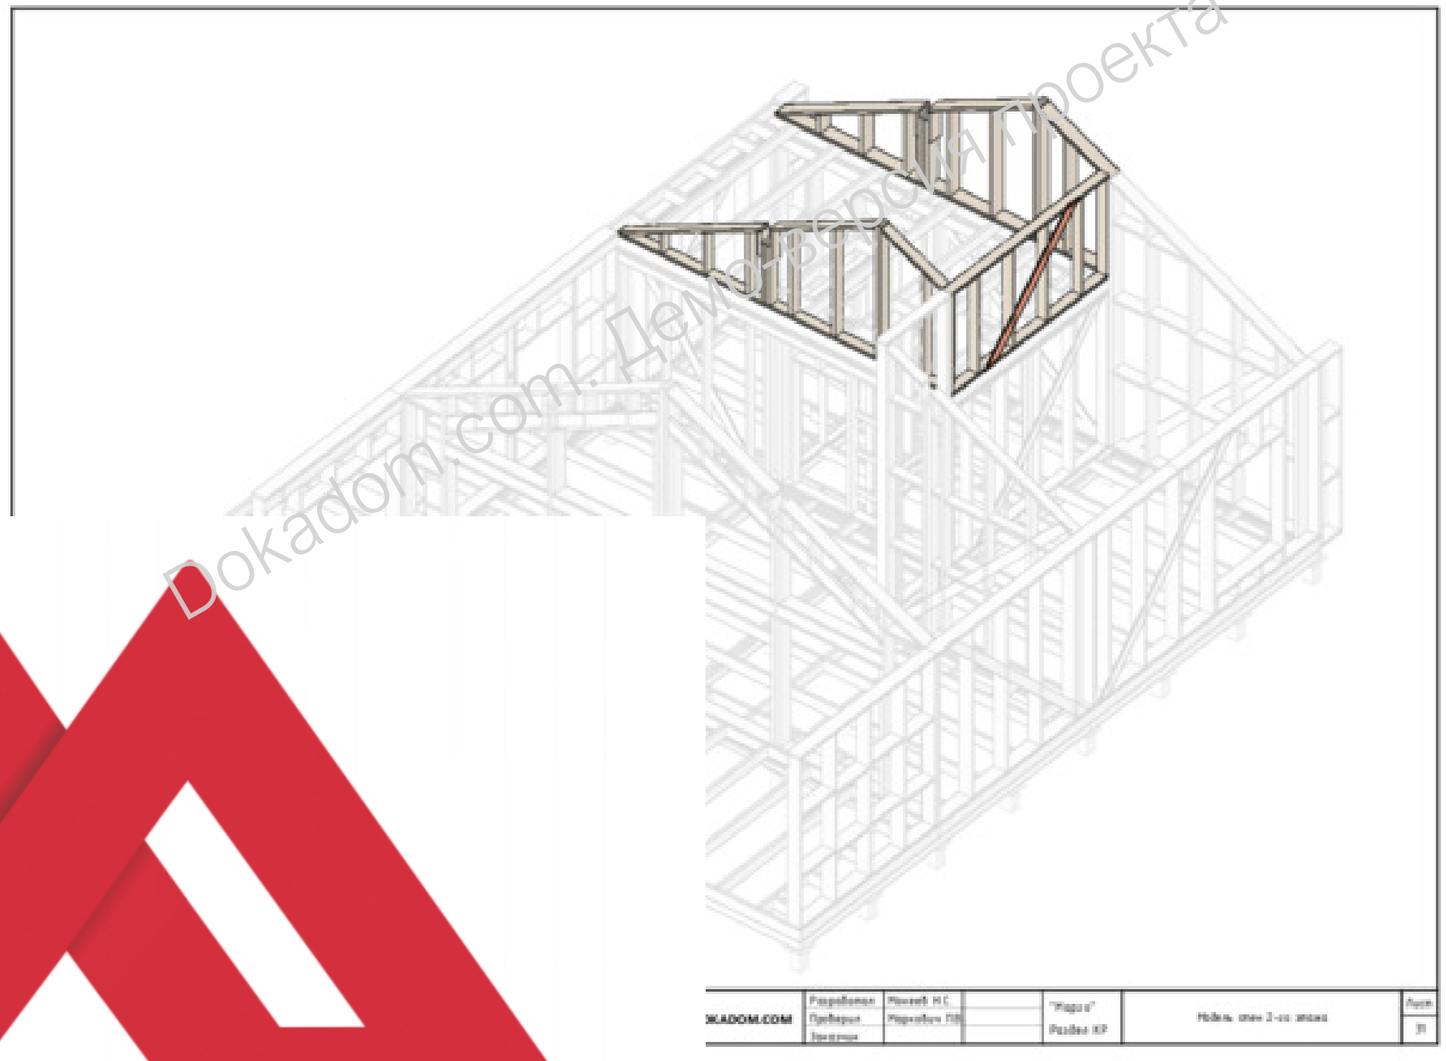


DOKADOM.COM
ДЕМО-ВЕРСИЯ ПРОЕКТА
Dokadom.com. Демо-версия проекта

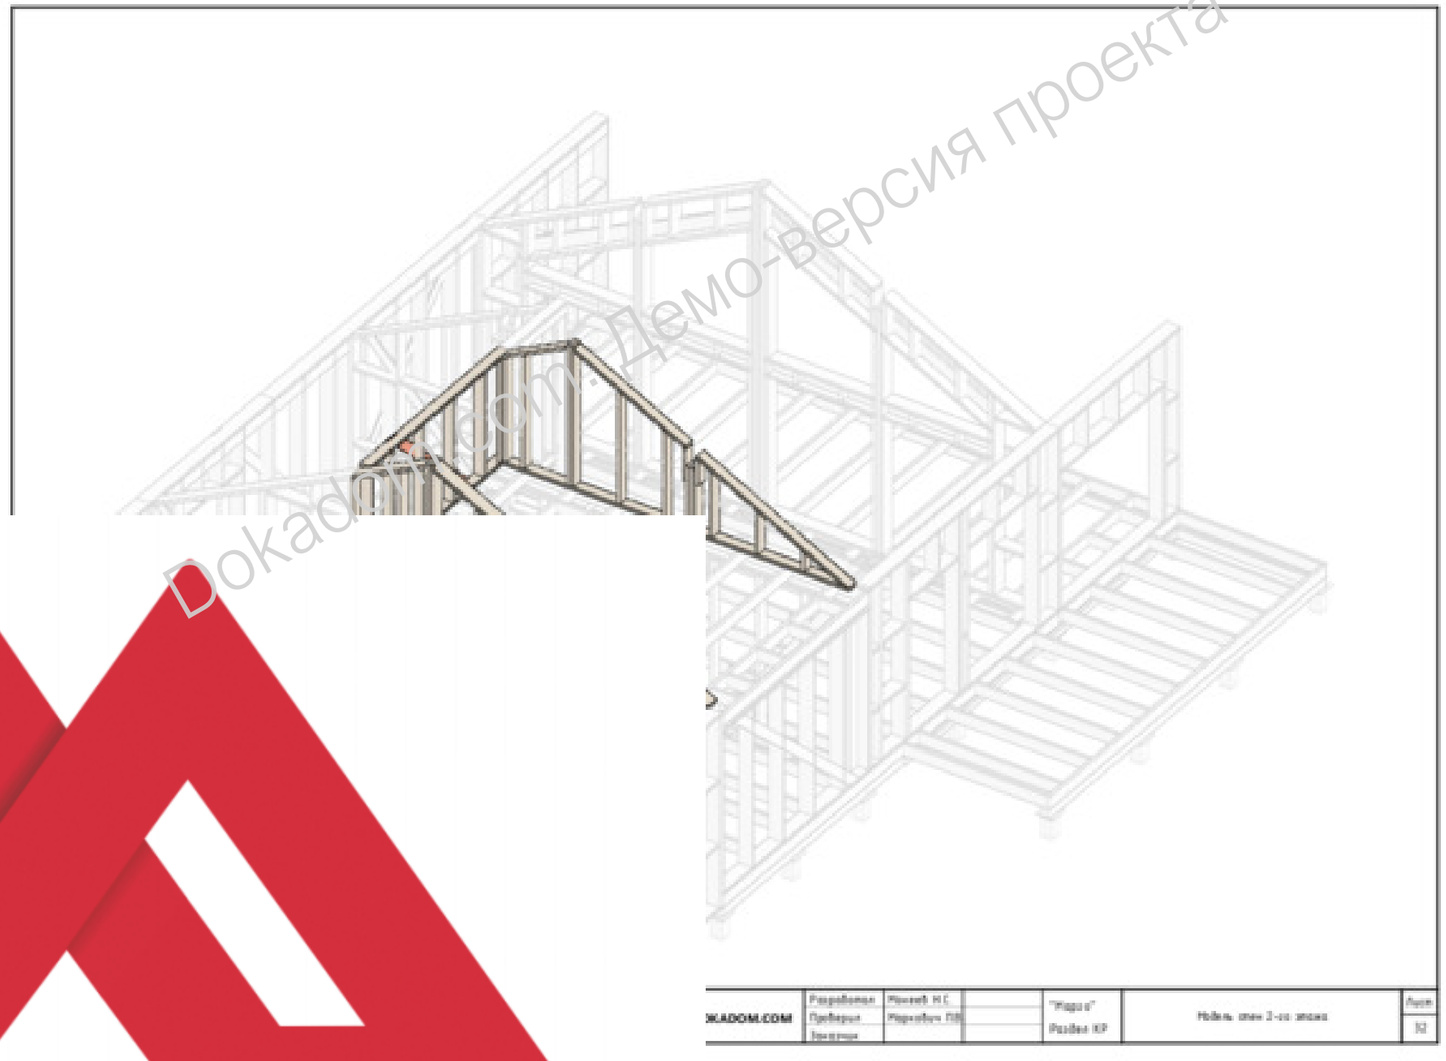


DOKADOM.COM
ДЕМО-ВЕРСИЯ ПРОЕКТА
Dokadom.com. Демо-версия проекта

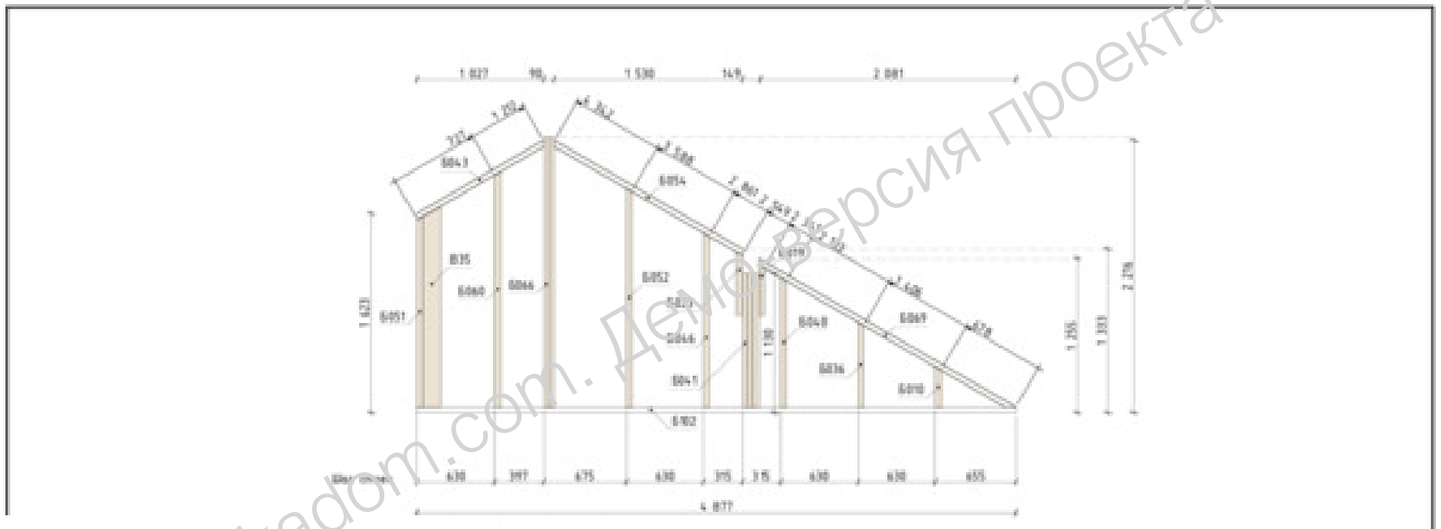

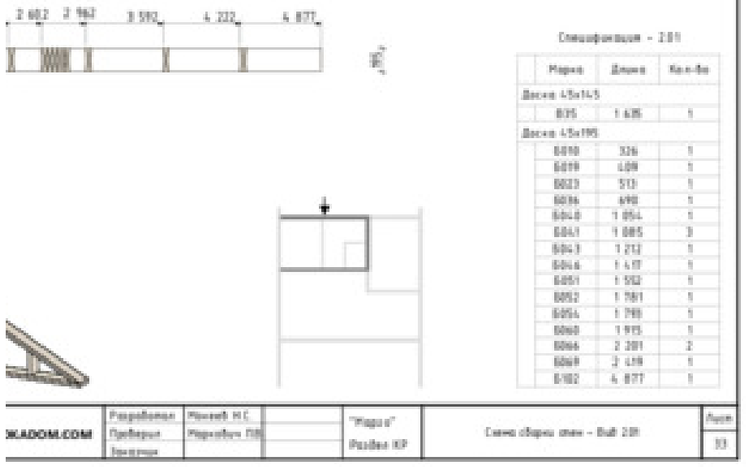


Dokadom.com. Демо-версия проекта
DOKADOM.COM
ДЕМО-ВЕРСИЯ ПРОЕКТА

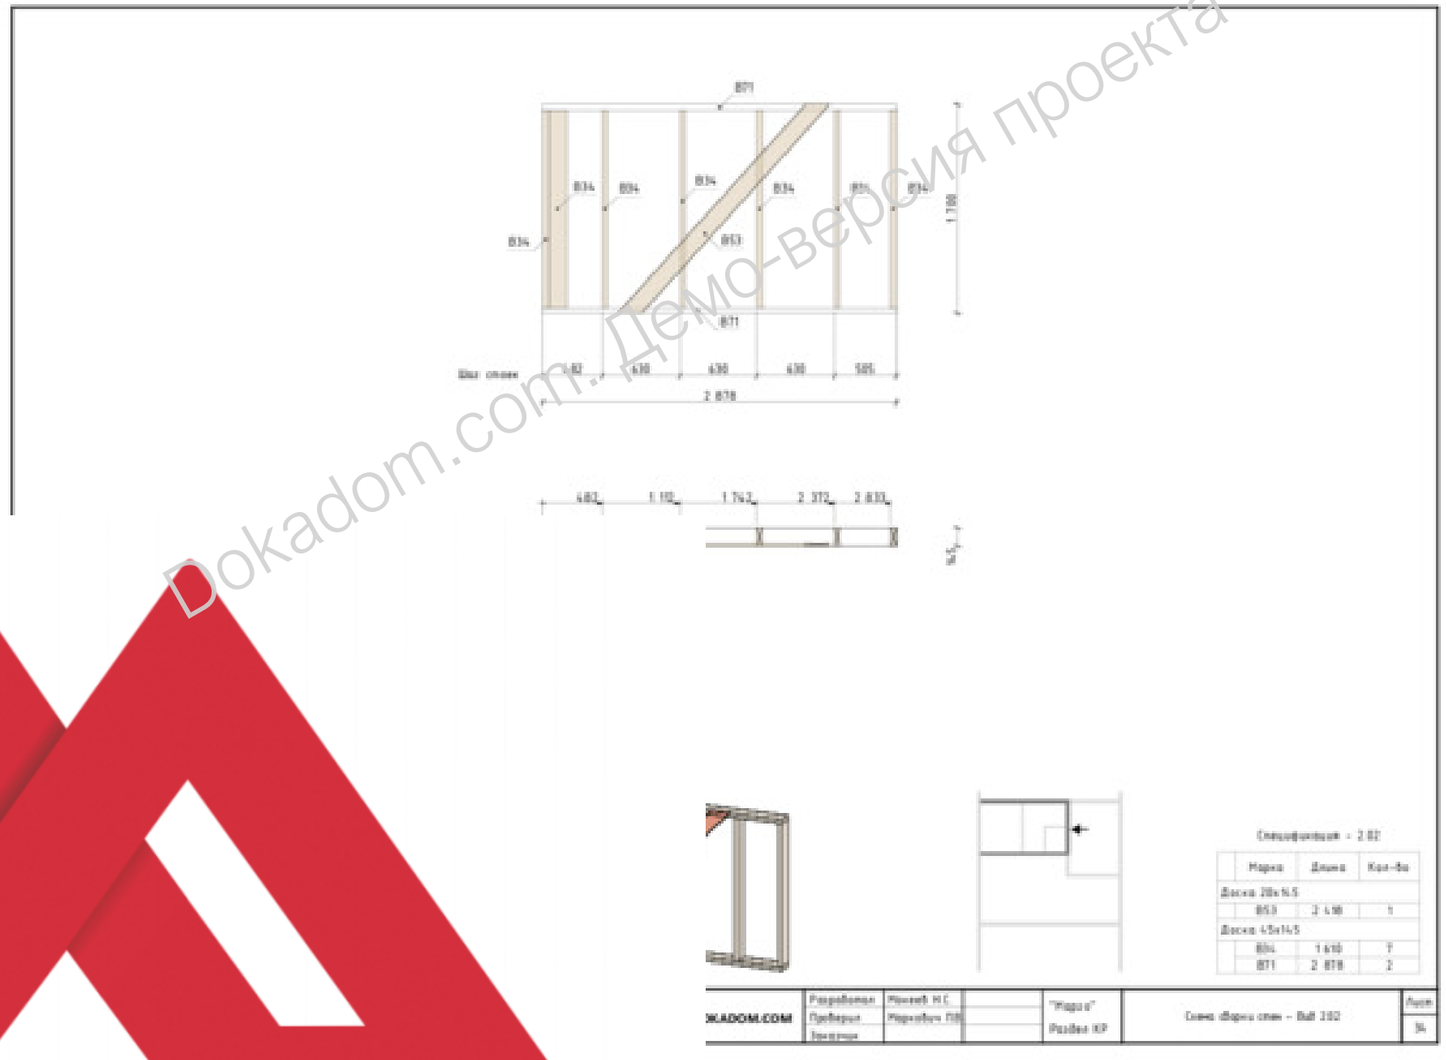


Dokadom.com. Демо-версия проекта


DOKADOM.COM
ДЕМО-ВЕРСИЯ ПРОЕКТА

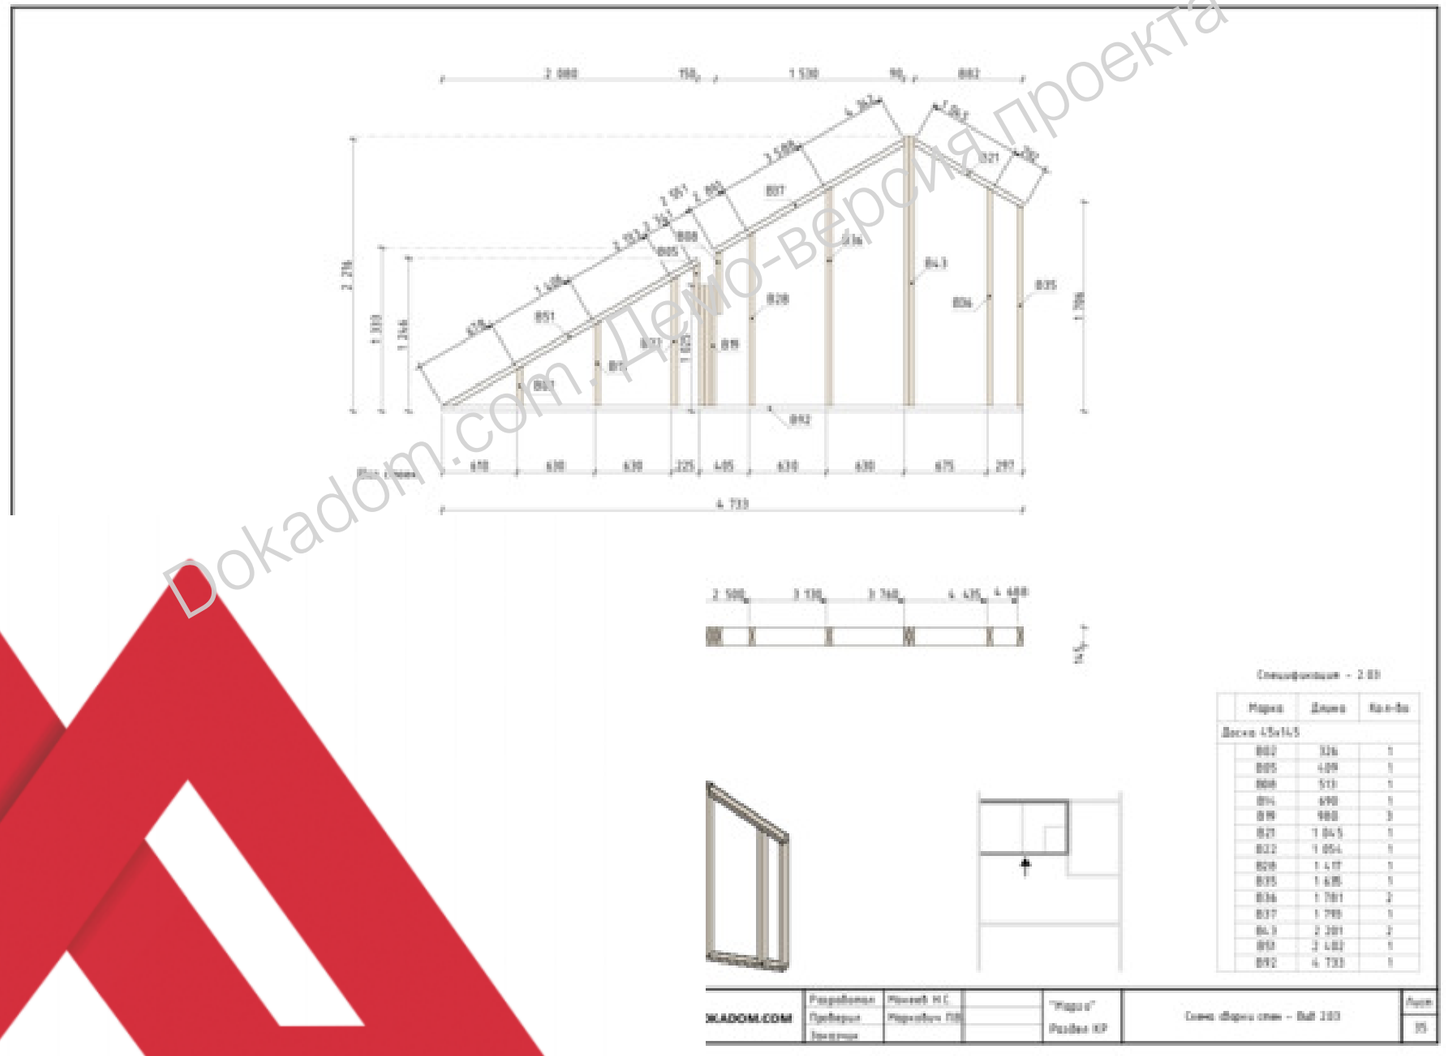

Dokadom.com. Демо-версия проекта
DOKADOM.COM
ДЕМО-ВЕРСИЯ ПРОЕКТА

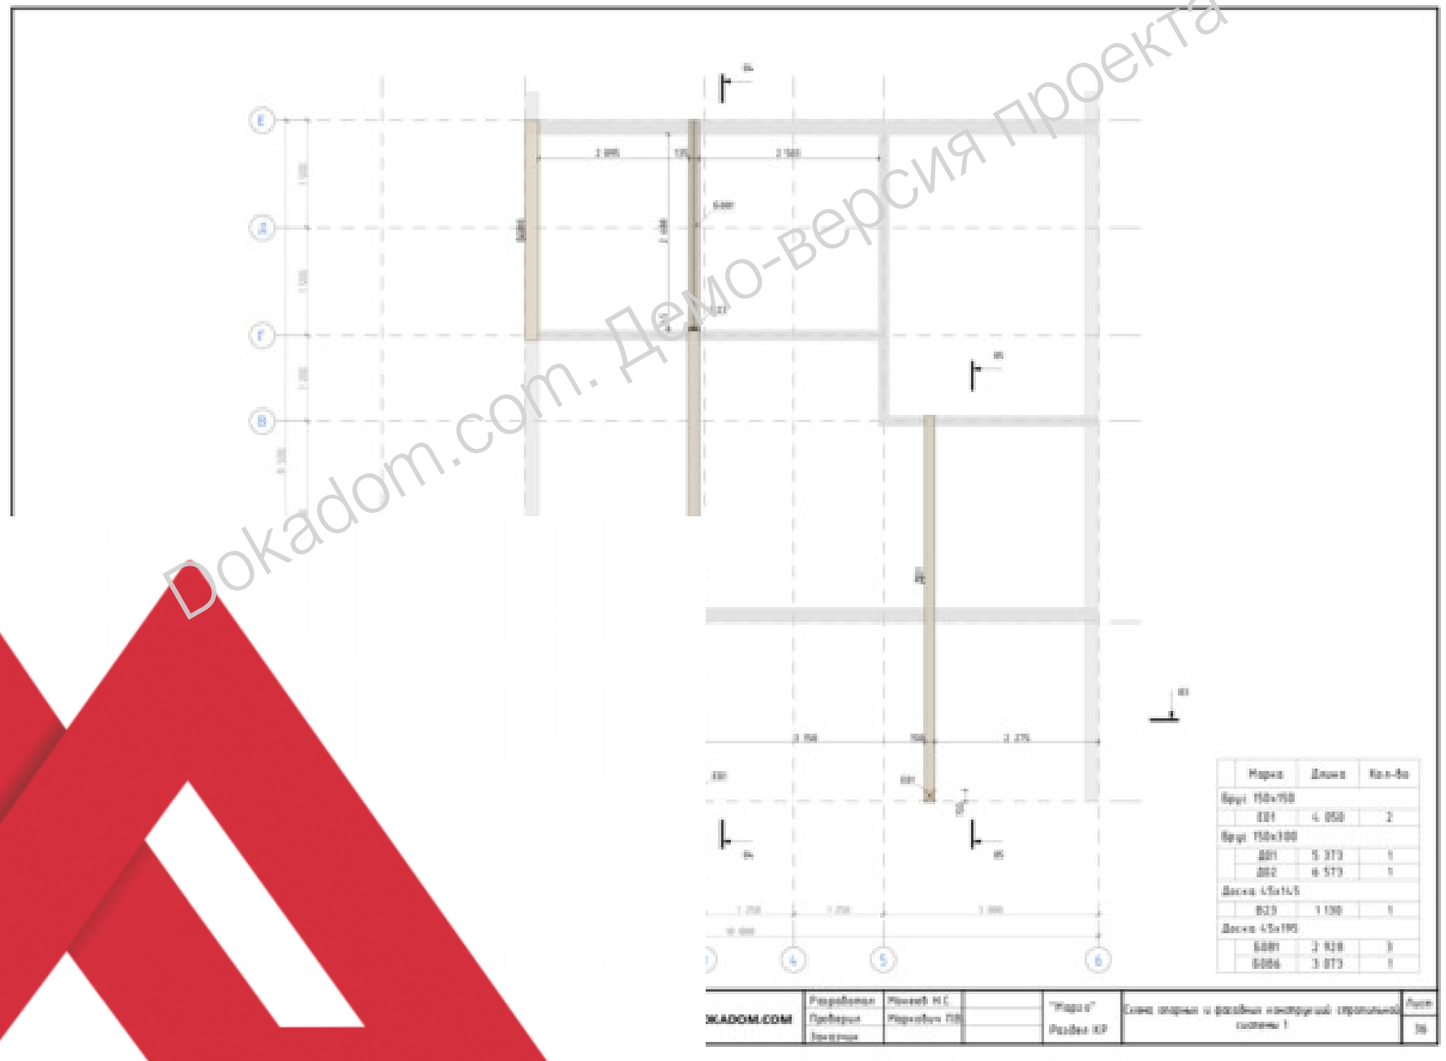

Dokadom.com. Демо-версия проекта
DOKADOM.COM
ДЕМО-ВЕРСИЯ ПРОЕКТА

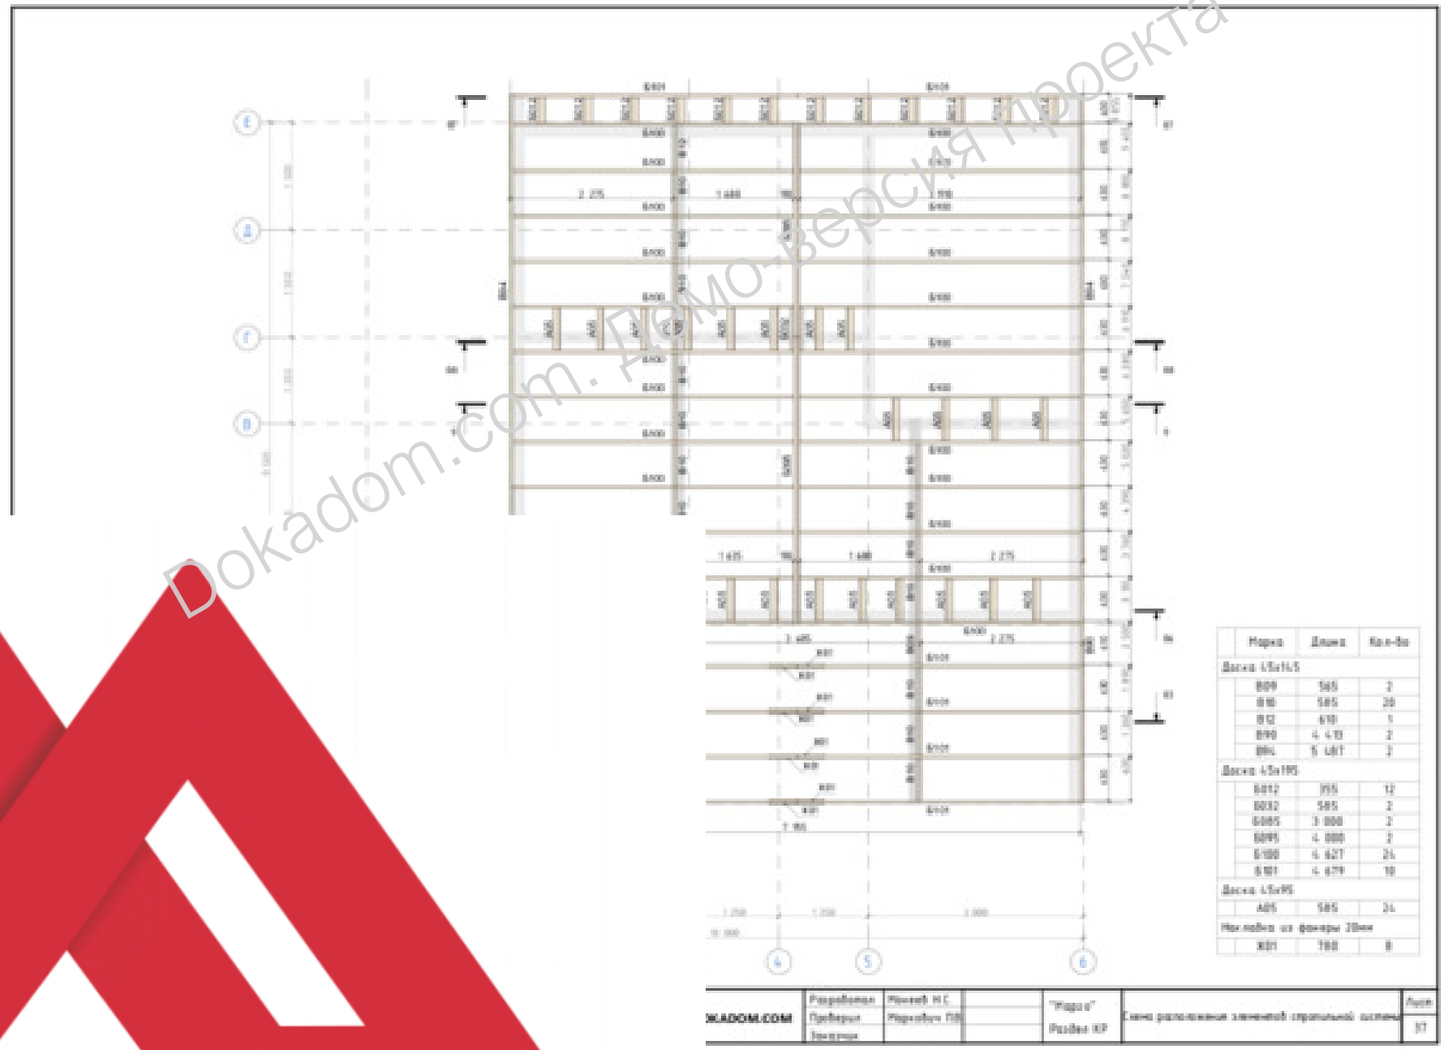

Марка	Длина	Кол-во
Доска 45х145		
В09	565	2
В10	585	20
В12	670	1
В90	4 470	2
В94	5 487	2
Доска 45х195		
Б012	355	12
Б032	585	2
Б085	3 000	2
Б095	4 000	2
Б100	4 627	24
Б101	4 679	10
Доска 45х95		
А05	585	24
Накладка из фанеры 20мм		
Х01	700	8


Разработал	Ишеев Н.С.		"Мадо и"	Схема расположения элементов стропильной системы	Лист 17
Проверил	Нарсеевич П.В.		Разбил КР		
Эпюрщик					

Dokadom.com. Демо-версия проекта

DOKADOM.COM

ДЕМО-ВЕРСИЯ ПРОЕКТА


Разрез 3-3

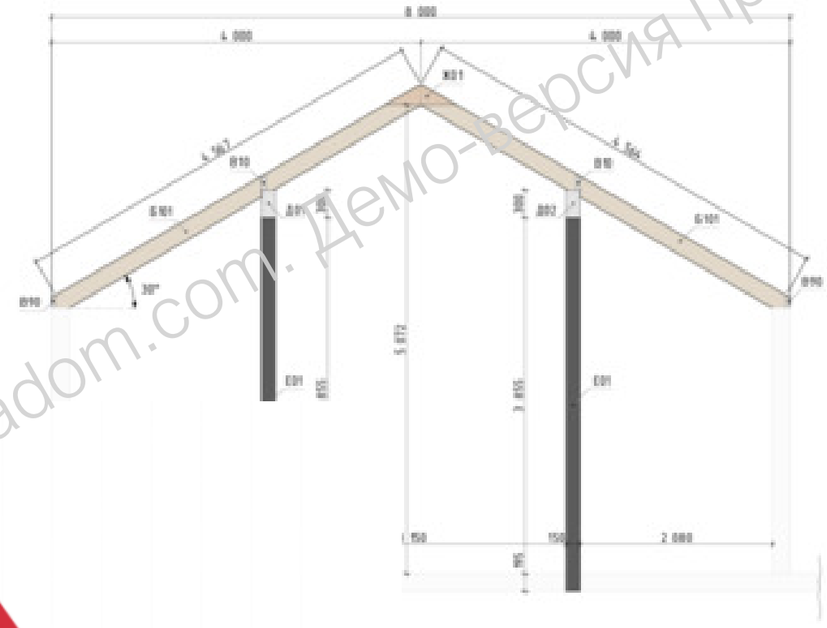


DOKADOM.COM	Разработал	Иванов И.С.		"Мадрид"	Разрез 3-3	Лист
	Проверил	Иванов И.С.		Разбивка КР		10
	Эксперт					

Dokadom.com. Демо-версия проекта
DOKADOM.COM
ДЕМО-ВЕРСИЯ ПРОЕКТА

Разрез 4–4

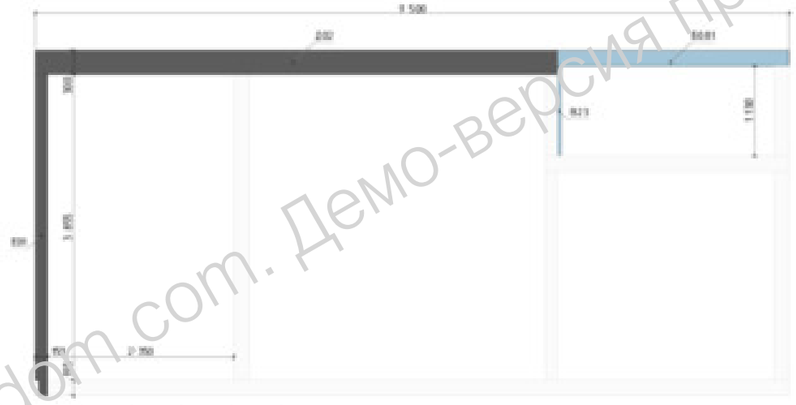

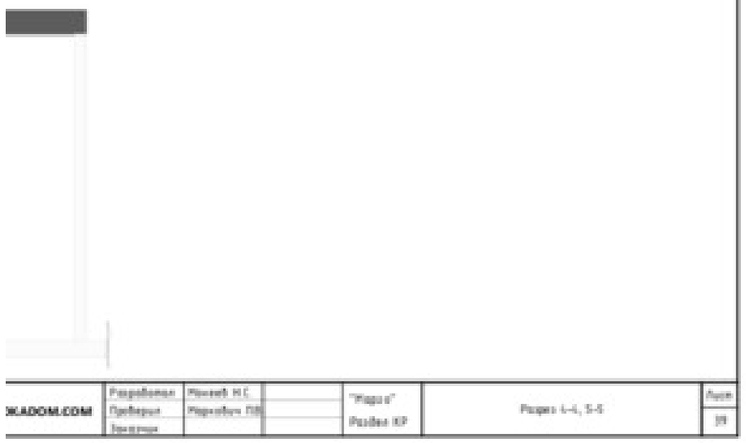


	Разработал	Иванов И.С.		"Мария"	Разрез 4-4, 5-5	Лист
	Проверил	Иванова П.В.		Разрез КР		19
	Эксперт					


Dokadom.com. Демо-версия Проекта

DOKADOM.COM
ДЕМО-ВЕРСИЯ ПРОЕКТА

Разрез 6-6

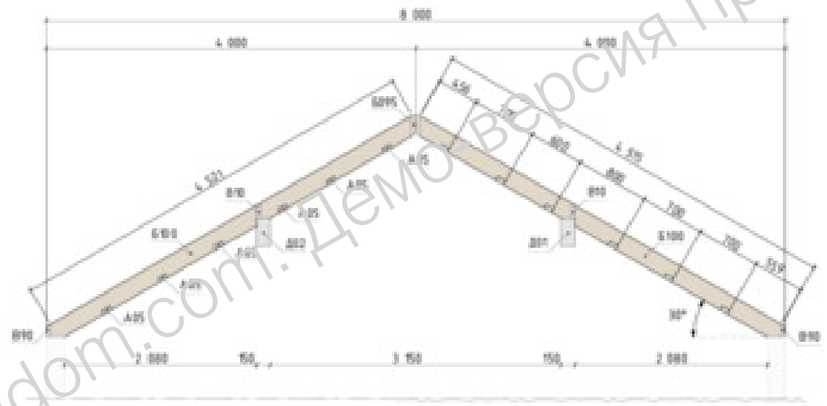

Разрез 7-7

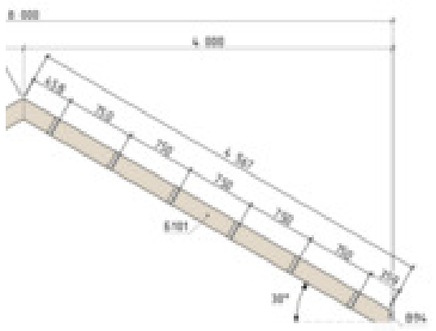


DOKADOM.COM	Разработал	Иванов И.С.		"Мария"	Разрезы 6-6, 7-7	Лист 48
	Проверил	Иванов П.В.		Разрез КР		
	Эксперт					


Dokadom.com. Демо-версия проекта

DOKADOM.COM
ДЕМО-ВЕРСИЯ ПРОЕКТА

Разрез 8-8

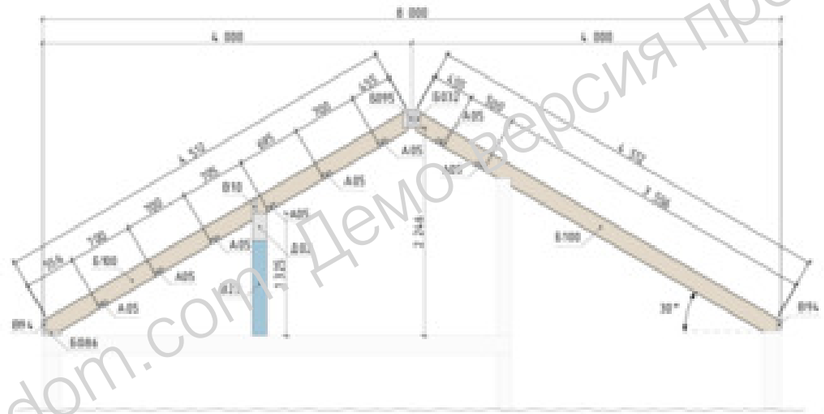


раз 9-9

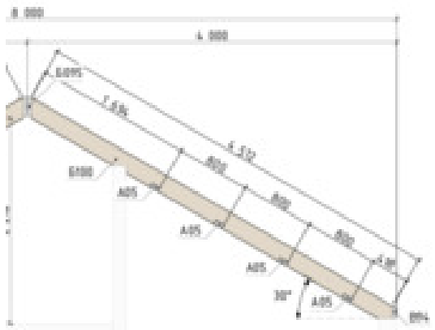


	Разработал	Ивлиев Н.С.		"Индиго"	Разрезы 8-8, 9-9	Лист
DOKADOM.COM	Проверил	Нормоконтр. ГИП		Разрезы КР		41
	Эксперт					

Dokadom.com Демо-версия проекта
DOKADOM.COM
ДЕМО-ВЕРСИЯ ПРОЕКТА

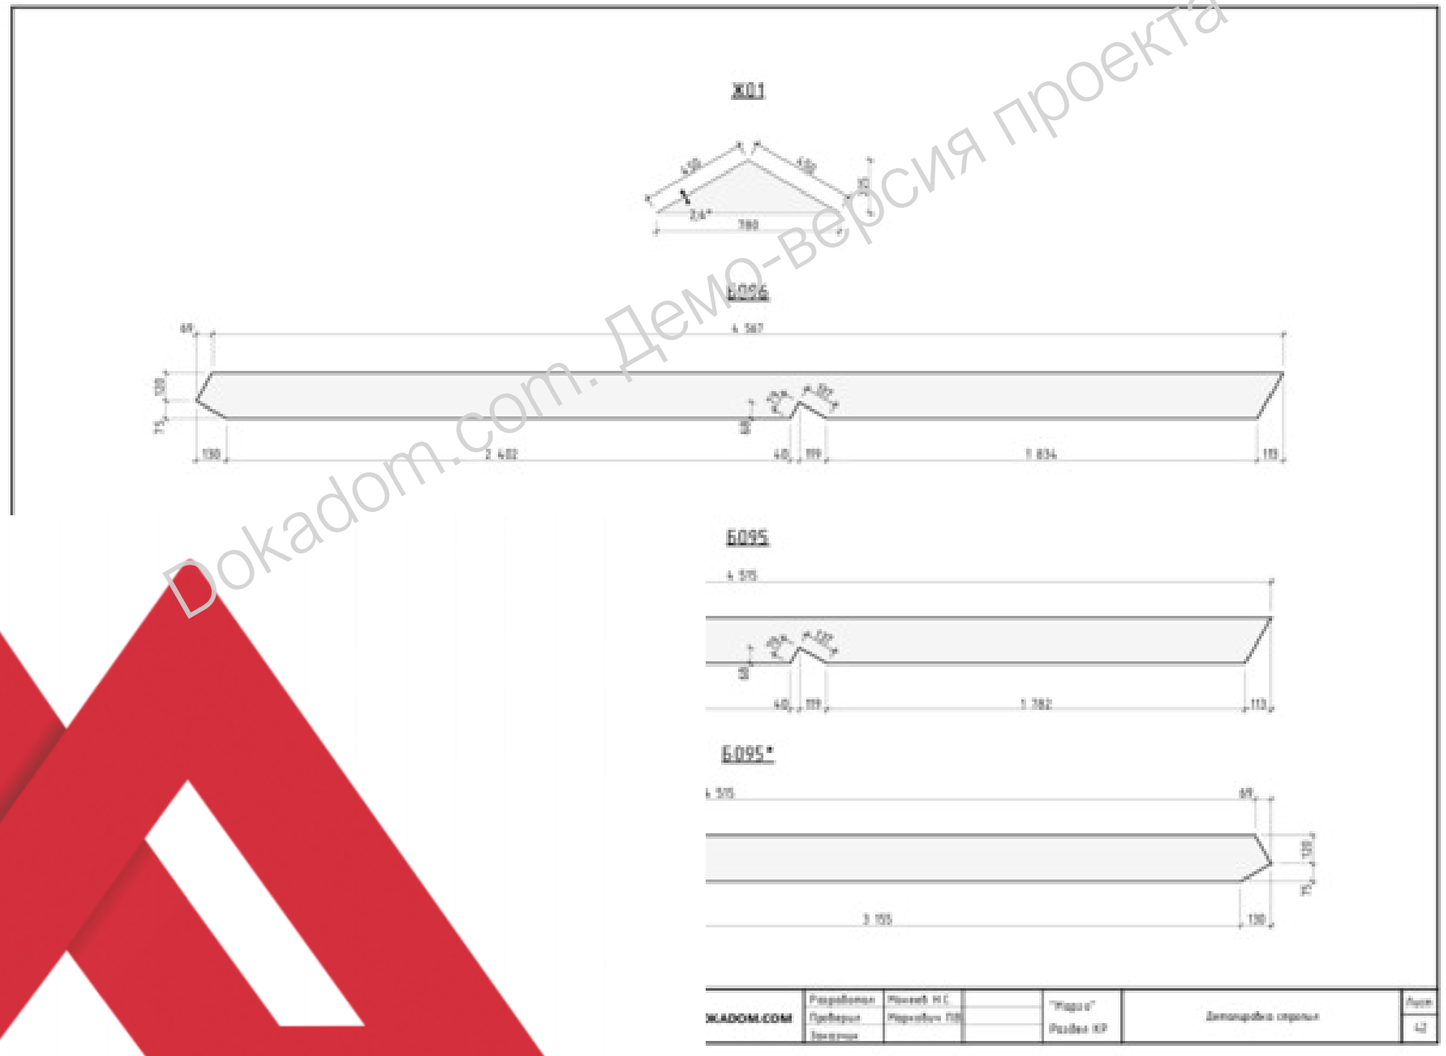


Dokadom.com. Демо-версия проекта
DOKADOM.COM
ДЕМО-ВЕРСИЯ ПРОЕКТА

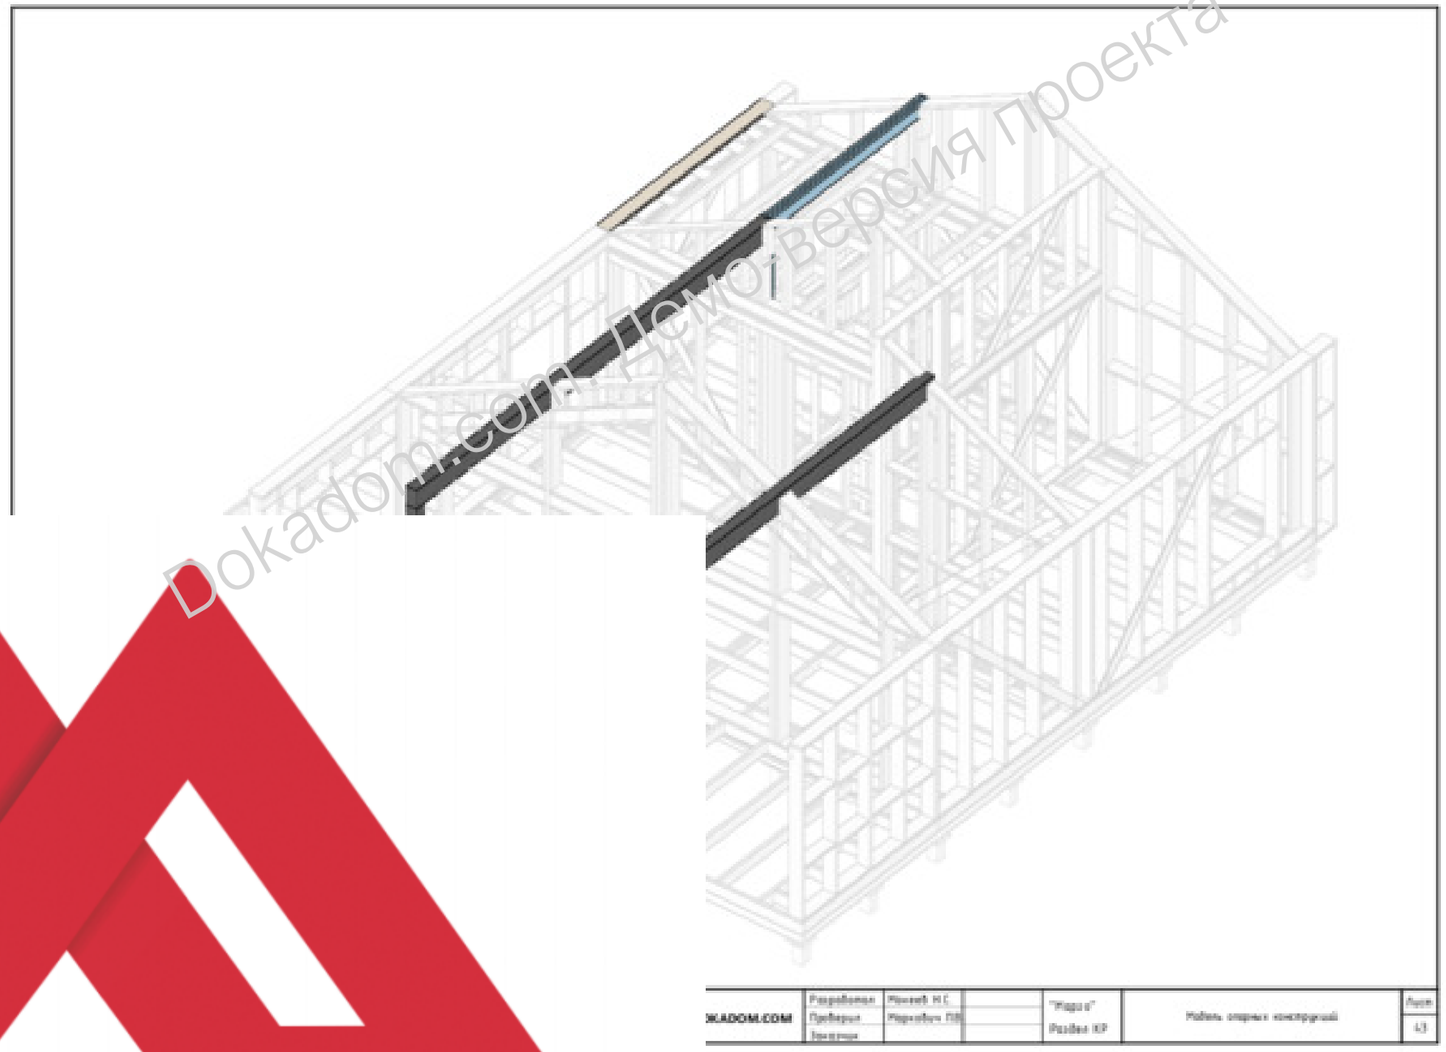


DOKADOM.COM	Разработал	Иванов И.С.		"Ридго"	Узел опорных конструкций	Лист
	Проверил	Нормоконт. ПТО		Razdva KP		43
	Утвердил					

DOKADOM.COM
ДЕМО-ВЕРСИЯ ПРОЕКТА
Dokadom.com - Демо-Версия Проекта

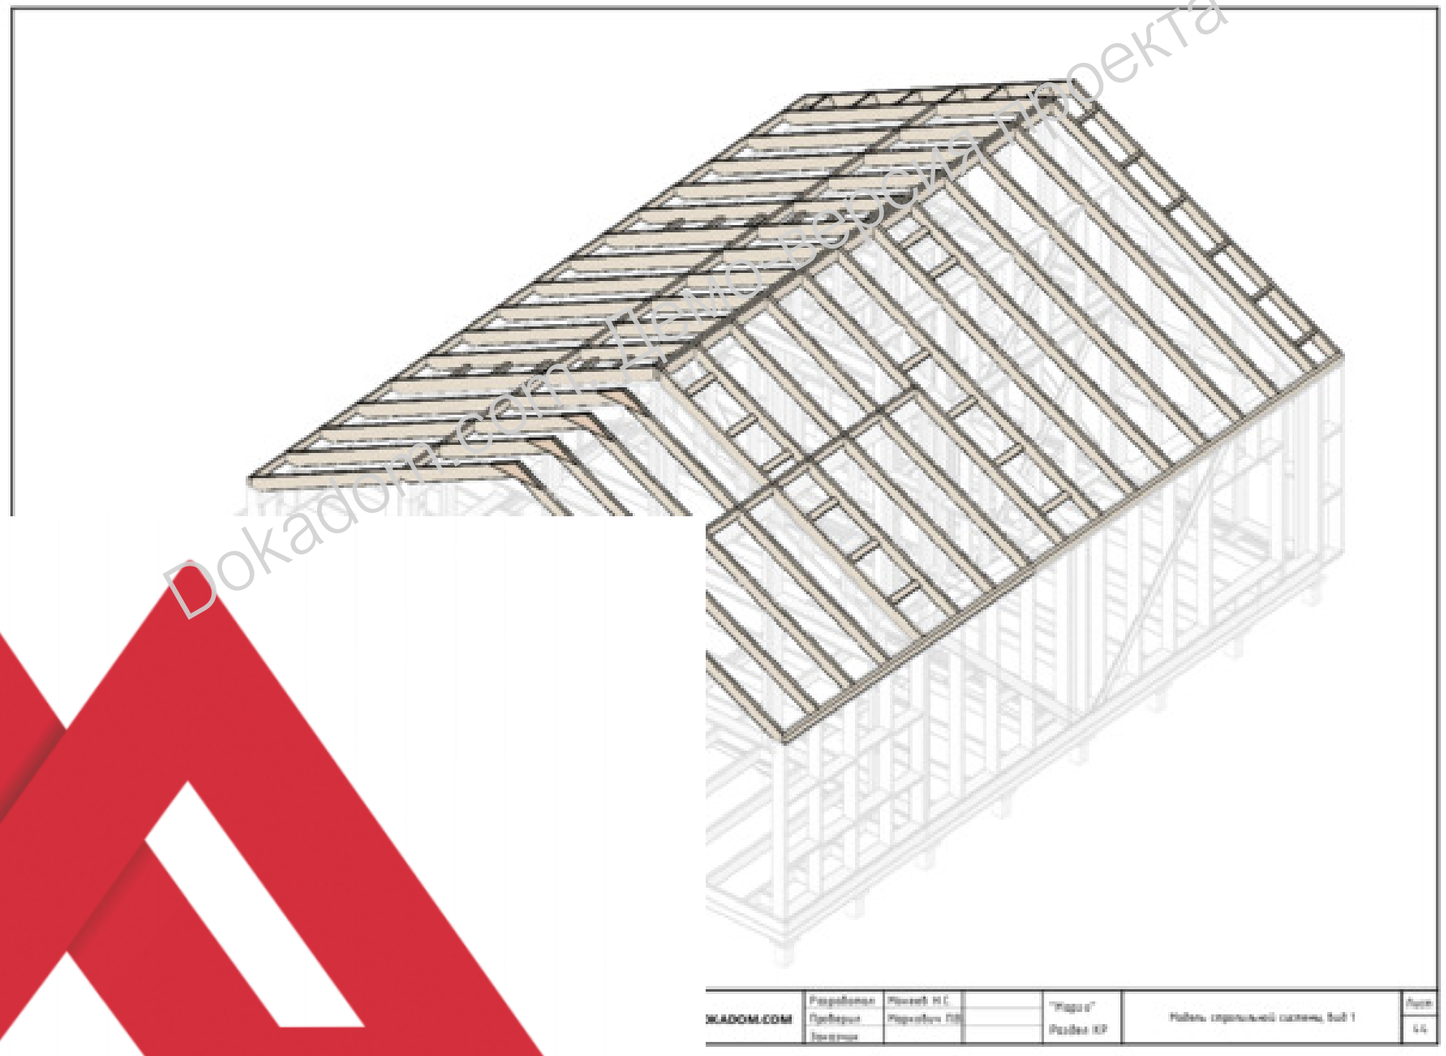

DOKADOM.COM	Разработал	Иванов И.С.		"Ундо и"	Навель стропильной системы, Вид 1	Лист
	Проверил	Иванов П.В.		Разбил ВР		44
	Заказчик					

Dokadom.com
DOKADOM.COM
ДЕМО-ВЕРСИЯ ПРОЕКТА

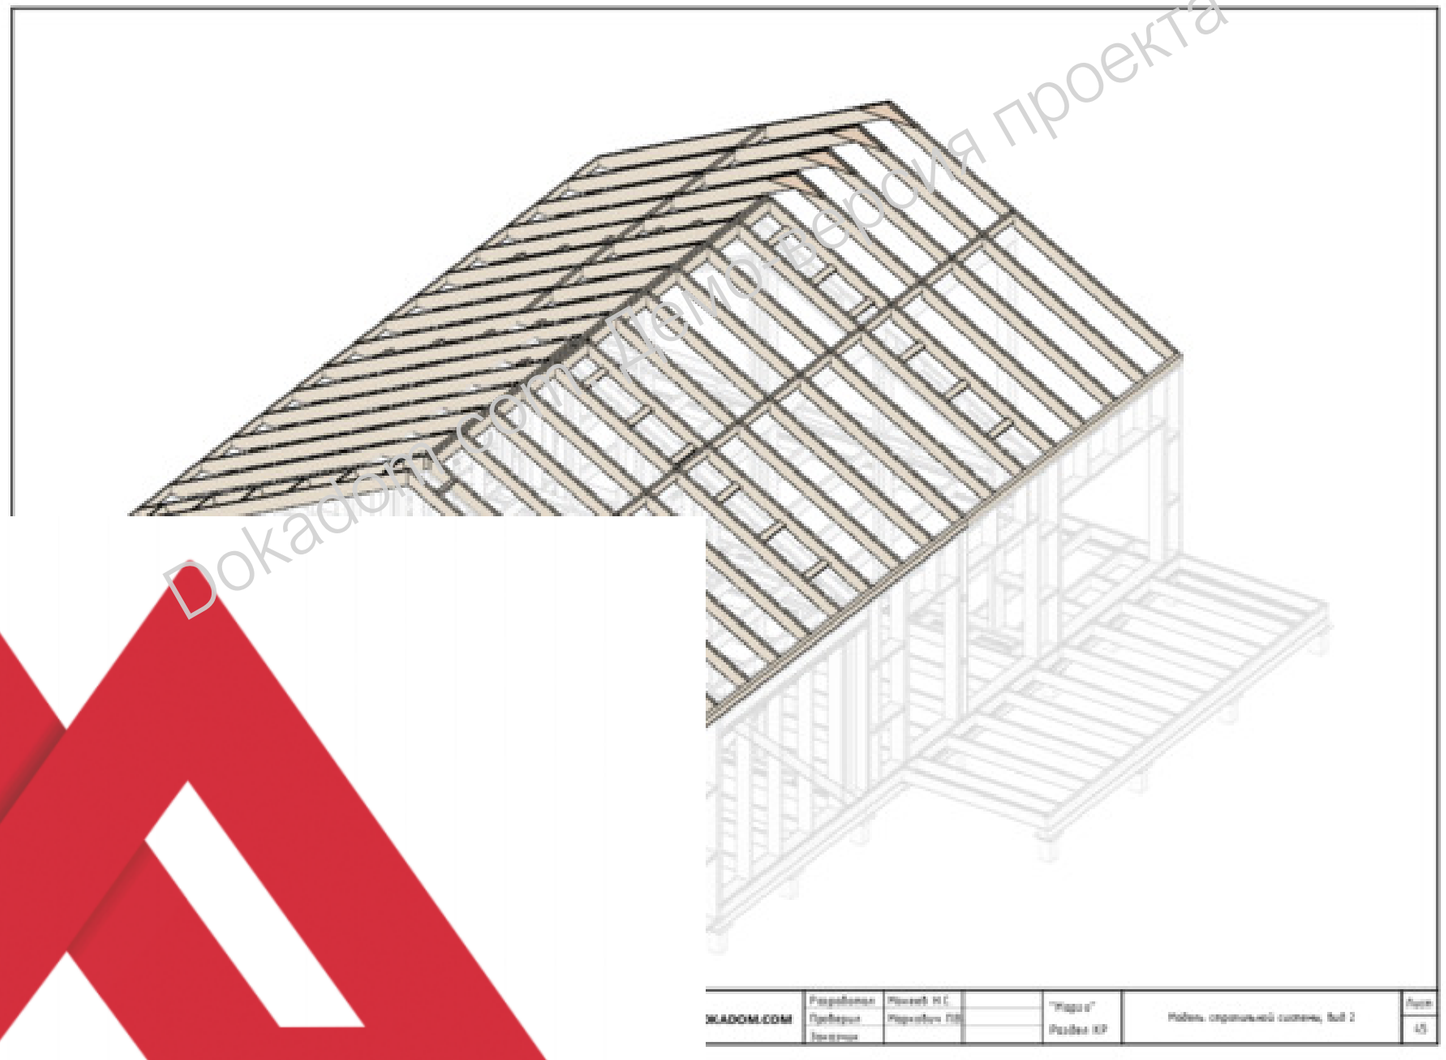

DOKADOM.COM	Разработал	Иванов И.С.		"Индиго"	Модель стропильной системы, Вид 2	Лист
	Проверил	Иванов П.В.		Разбивка КР		4/5
	Утвердил					

Dokadom.com
DOKADOM.COM
ДЕМО-ВЕРСИЯ ПРОЕКТА

Спецификация ПМ лестницы

Марка	Длина	Кол-во
Брус 150х150		
Л01	4 850	2
Брус 150х300		
Д01	5 373	1
Д02	4 573	1
Доска 30х145		
П53	2 418	1
П91	3 152	1
П92	3 491	1
П93	3 723	1
П94	3 808	1
П95	3 817	1
П96	3 899	1
П97	3 909	1
П98	3 913	1
Доска 45х145		
В01	143	3
В02	326	1
В03	350	2
В04	379	1
В05	439	1
В06	473	3
В07	483	1
В08	573	1
В09	583	1

Марка	Длина	Кол-во
В41	2 145	3
В42	2 193	4
В43	2 201	2
В44	2 215	1
В45	2 238	2
В46	2 268	1
В47	2 283	4
В48	2 305	3
В49	2 358	1
В50	2 365	1
В51	2 382	1
В52	2 418	1
В54	2 428	1
В55	2 453	1
В56	2 455	1
В57	2 477	1
В58	2 500	9
В59	2 509	13
В60	2 515	1
В61	2 590	1
В62	2 597	1
В63	2 605	2
В64	2 687	3
В65	2 733	1
В66	2 777	1
В67	2 797	1
В68	2 864	1

Марка	Длина	Кол-во
Доска 45х195		
В001	80	2
В002	150	2
В003	158	2
В004	218	4
В005	236	2
В006	243	2
В007	255	2
В008	330	2
В009	334	2
В010	424	1
В011	450	1
В012	455	37
В013	460	2
В014	566	2
В395	370	5
В396	387	5
В397	395	1
В398	400	16
В399	409	1
В400	440	2
В401	471	3
В402	485	2
В403	513	1
В404	520	3
В405	520	6
	540	10
	565	6
	570	7
	570	1
	579	4
	579	2
	585	48
	590	4
	615	4
	635	7
	690	1
1 000		2
1 050		2
1 053		2
1 054		1
1 085		3
1 090		1
1 212		1
1 240		2
1 280		2
1 417		1
1 448		1
1 500		2
1 580		10
1 580		4
1 552		1
1 781		1
1 795		2
1 795		2
1 795		3
1 879		1

Марка	Длина	Кол-во
В057	1 879	1
В058	1 917	2
В059	1 928	2
В060	1 973	1
[illegible]	1 955	10
В061	2 105	2
В062	2 105	2
[illegible]	2 125	8
В065	2 165	1
В066	2 201	2
В067	2 328	2
В068	2 380	1
В069	2 419	1
В070	2 445	1
В071	2 445	1
В072	2 453	1
В073	2 455	14
В074	2 500	24
В075	2 500	11
В076	2 568	1
В077	2 590	3
В078	2 733	2
В079	2 795	24
В080	2 864	3
В081	2 928	3
В082	2 966	1
В083	2 980	4
В084	2 980	10
В085	3 000	2
В086	3 073	4
В087	3 100	3
В088	3 181	1
В089	3 330	1
В090	3 494	1
В091	3 805	1
В092	3 905	1
В093	3 910	2
В094	3 928	3
В095	4 000	2
В096	4 058	1
В097	4 356	1
В098	4 433	1
В099	4 463	1
В100	4 627	24
В101	4 679	10
В102	4 877	4
В103	4 949	2
В104	5 031	2
В105	5 073	2
В106	5 538	1
В107	5 672	2
В108	5 700	1
В109	5 718	2
В110	5 858	2
В111	6 000	11
Доска 45х95		
А01	175	7

Марка	Длина	Кол-во
А02	195	16
А03	350	1
А04	397	4
А05	585	24
А06	700	1
А07	1 130	2
А08	1 370	1
А09	1 475	2
А10	1 525	1
А11	1 730	1
А12	2 500	1
А13	2 500	14
А14	2 738	2
А15	3 073	1
А16	5 610	1
А17	6 000	1
Накладка из фанеры 20мм		
К01	780	8

DOKADOM.COM	Разработал	Ивлиев Н.С.		"Индиго"	Спецификация металлического силового каркаса	Лист 48
	Проверил	Руководитель ПТО		Разбивка КР		
	Утвердил					

Dokadom.com. ДЕМО-ВЕРСИЯ ПРОЕКТА

DOKADOM.COM
ДЕМО-ВЕРСИЯ ПРОЕКТА

Объем пиломатериала каркаса (Без учета осколов)

Тип и сечение элемента каркаса	Объем
Брус 150х150	0,18
Брус 150х300	0,54
Доска 28х145	0,09
Доска 45х145	3,01
Доска 45х198	7,91
Доска 45х95	0,38
Наплавка из фанеры 20мм	0,01
	12,11 м³

Объем доп. пиломатериала (Без учета осколов)

Наименование	Объем, куб. м
Брус он 50х90	0,51
Брус он 50х50	1,53
Доска 28х100	0,76
Доска 25х100	1,66
	4,46 м³

Объем утеплителя каркаса

Наименование	Объем, куб. м
Доп. утепление наобиты	2,27

Общая площадь материалов

Тип	Наименование	Площадь, кв. м
Крыша		
	Внутр. отделка потолка	45,23
	Гидро-Ветрозащита	93,97
	Мембрана паропитка	94,08
	Нар. отделка потолка и софитов	25,55
	Пароизоляция	47,61
Перекрытие		
	Внутр. отделка потолка	11,68
	Гидро-Ветрозащита	146,00
	Пароизоляция	62,52
	Покрытие пола - Ламинат	48,70
	Покрытие пола - Керамогранит	29,17
	Фанера	58,09
Стены		
	Внутр. отделка стен	167,57
	Гидро-Ветрозащита	90,21
	Жалюзийная пленка	104,68
	Нар. отделка стен	106,10
	Пароизоляция	68,82

Площадь внутреннего напольного покрытия

№	Наименование	Площадь, кв. м
1.2	Кухня - гостиная	23,91
1.3	Спальня	10,16
1.4	Душевая	4,23
1.5	Сауна	5,72
1.6	Санузел	1,34
		45,34 м²

Площадь наружного напольного покрытия

№	Наименование	Площадь, кв. м
1.1	Терраса	29,94
		29,94 м²

DOKADOM.COM	Разработал	Иванов И.С.		"Мира и"	Свайная обвязка	Лист 47
	Проверил	Иванов П.В.		Разбивка КР		
	Архитект					

Dokadom.com Демо-версия проекта
DOKADOM.COM
ДЕМО-ВЕРСИЯ ПРОЕКТА